


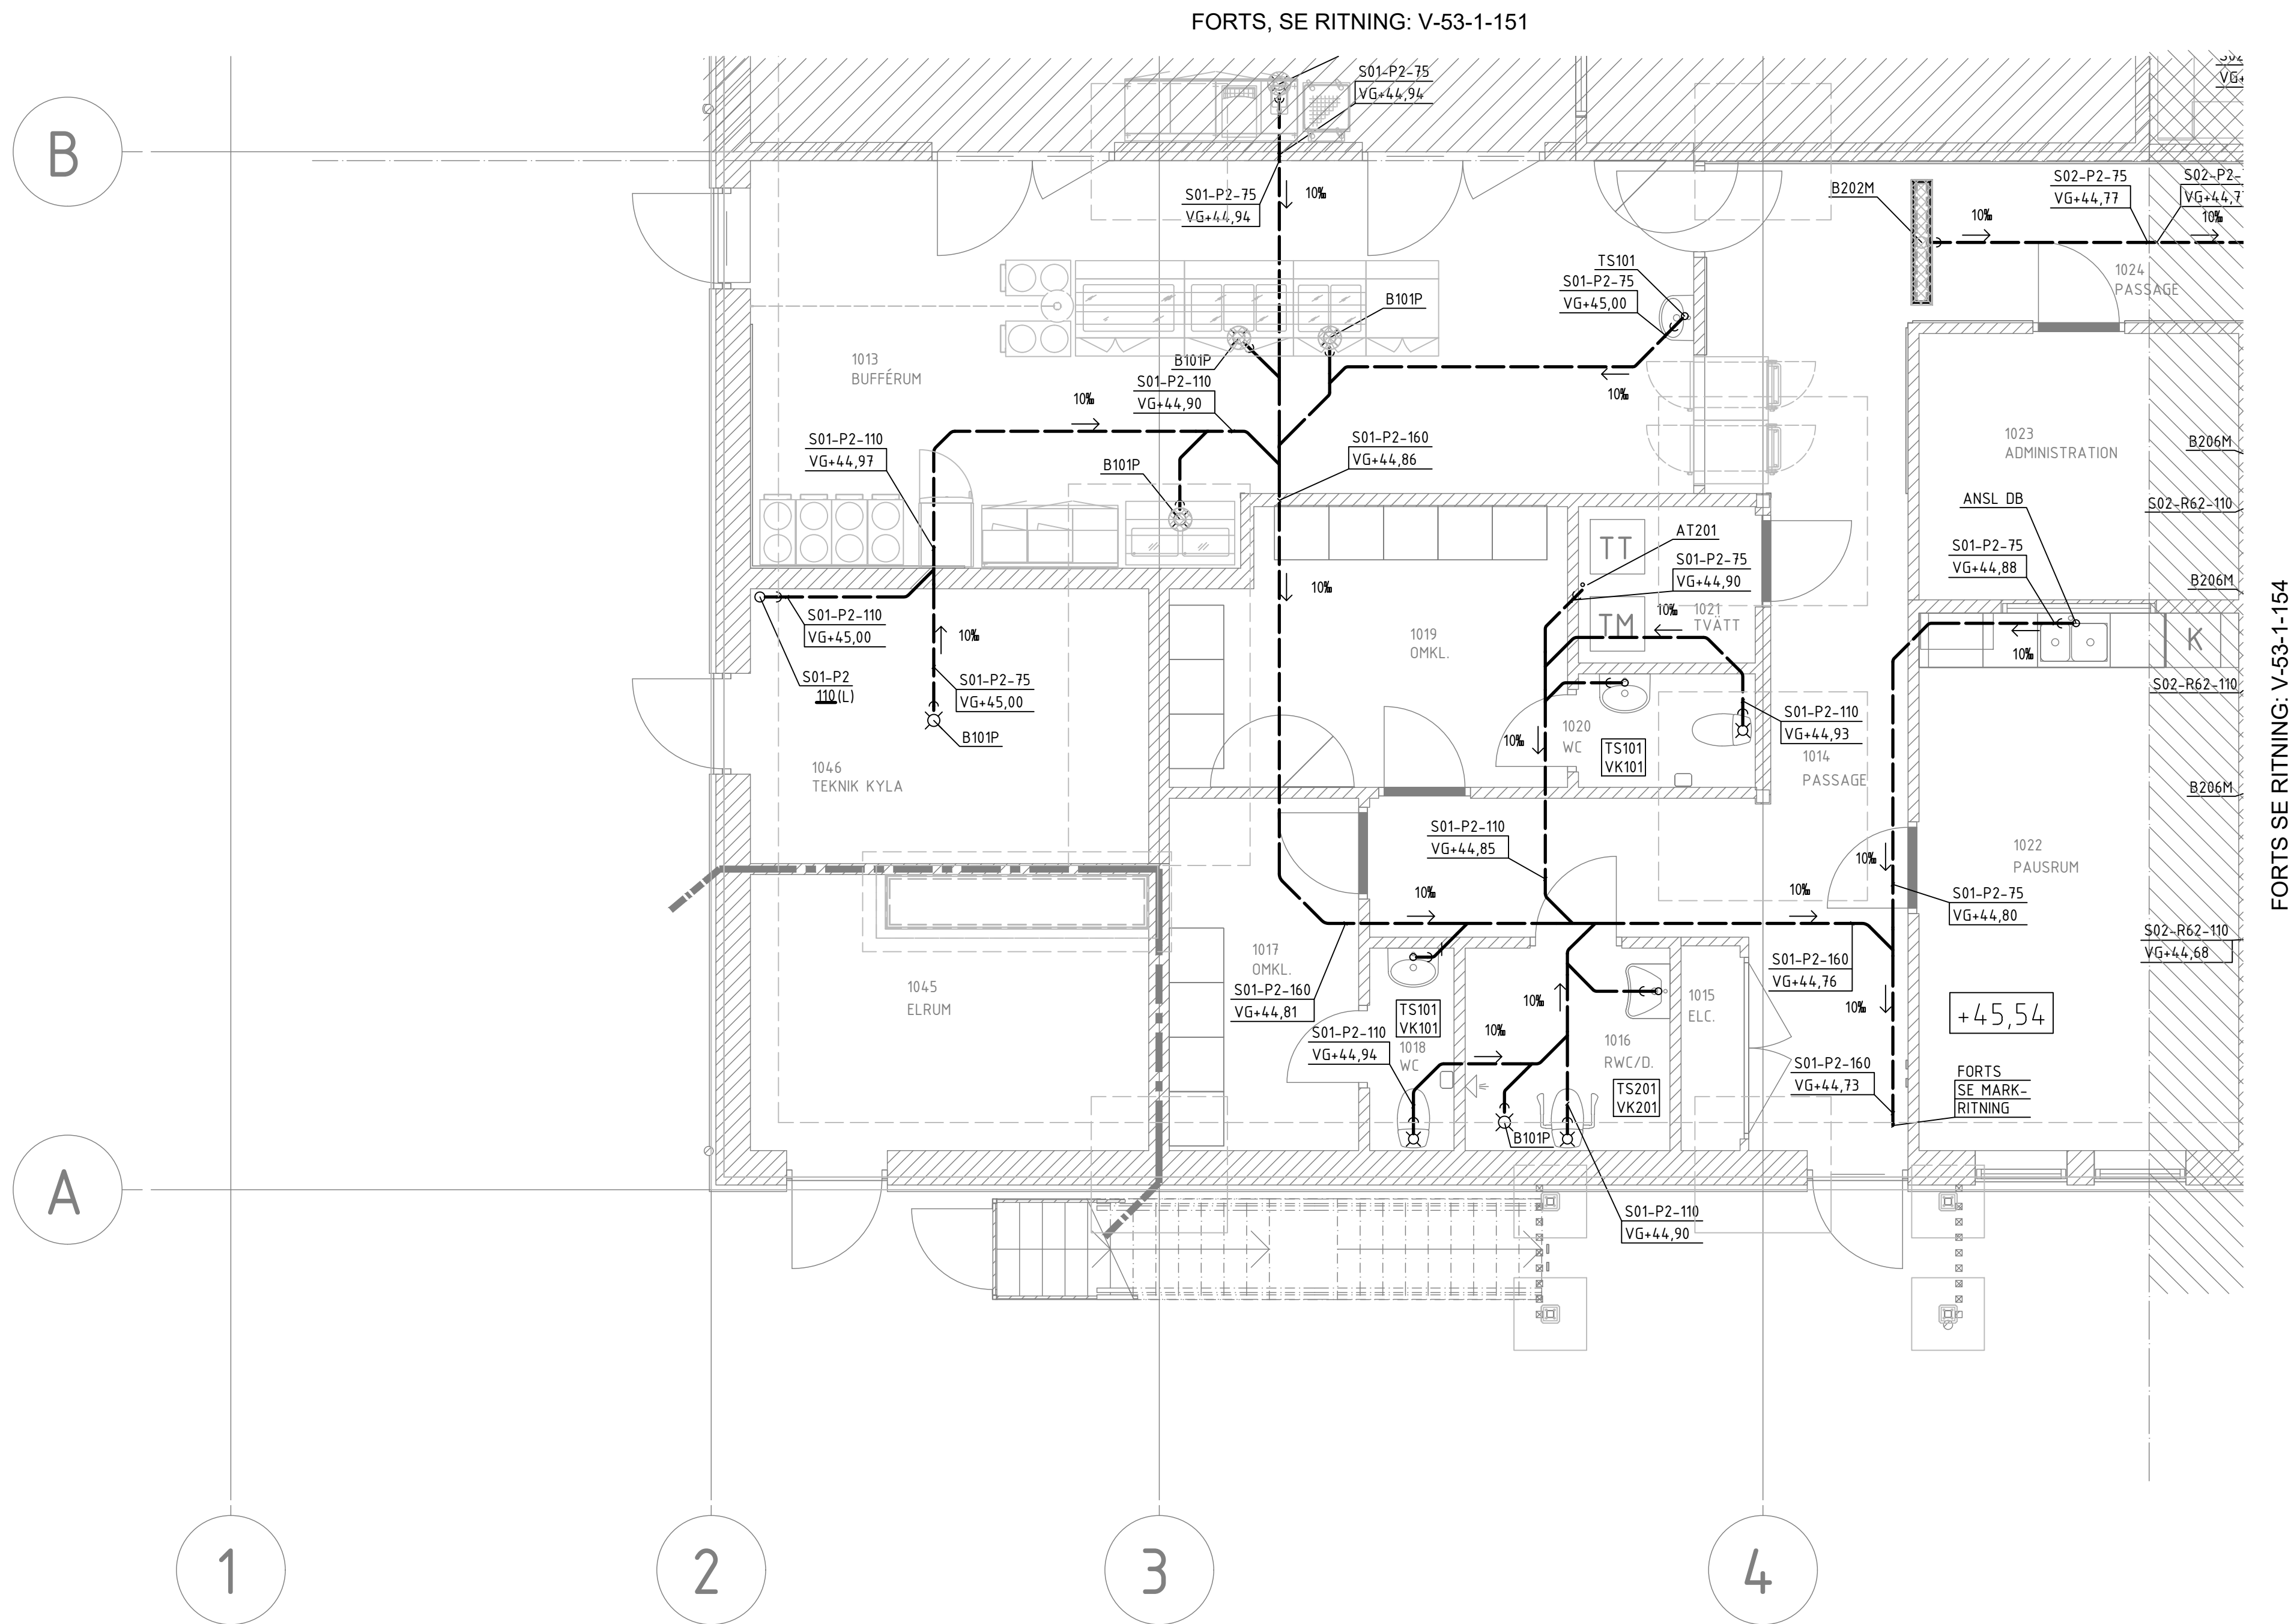

FORTS SE RITNING: V-53-1-154

SEKTION

ORIENTERINGSPÅR

STATUS

FÖRFRÅGNINGSUNDERLAG

HANDLING

BYGGHANDLING

DATUM

2024-12-20

ODKÄND AV

T.BERGSTRÖM

ANDRINGS PM

BESTÄLLARE

 **ROBERTSFORS**
KOMMUN

PROJEKTNAMN

CENTRALKÖK

OMRADE

ROBERTSFORS KOMMUN

PROJEKTNUMMER

FÖRRETS

YTRE RINGVÄGEN 4

DARIENUMMER

FASTIGHET

FORDONET 1

DISCIPLIN

VS

FÖRETAG

NORCONSULT SVERIGE AB

ÖPPNINGSNUMMER

108 83 71

SKAPAD AV

MAN

TELEFON

010 141 80 00

KONTAKTPERSON

JONAS JOHANSSON

BYGGNADSVÄRDE

(KLIMATKORRIGERT RVM 2009)

+45,54 (FG)

VÄNINGSPLAN

1

VÄNINGSDEL

DELOMRÅDE

DEL 5.3

SYSTEM

53 SPILLVATTENINSTALLATIONER

BESKRIVNING

PLAN 0 - DEL 5.3, UNDER PLATTA

RITNINGSKATEGORI

PLAN

SKALA

1:50

FORMAT

A1

ANDRING

DOKUMENTNUMMER

V-53-1-053

