


FORTS, SE RITNING: V-53-1-052

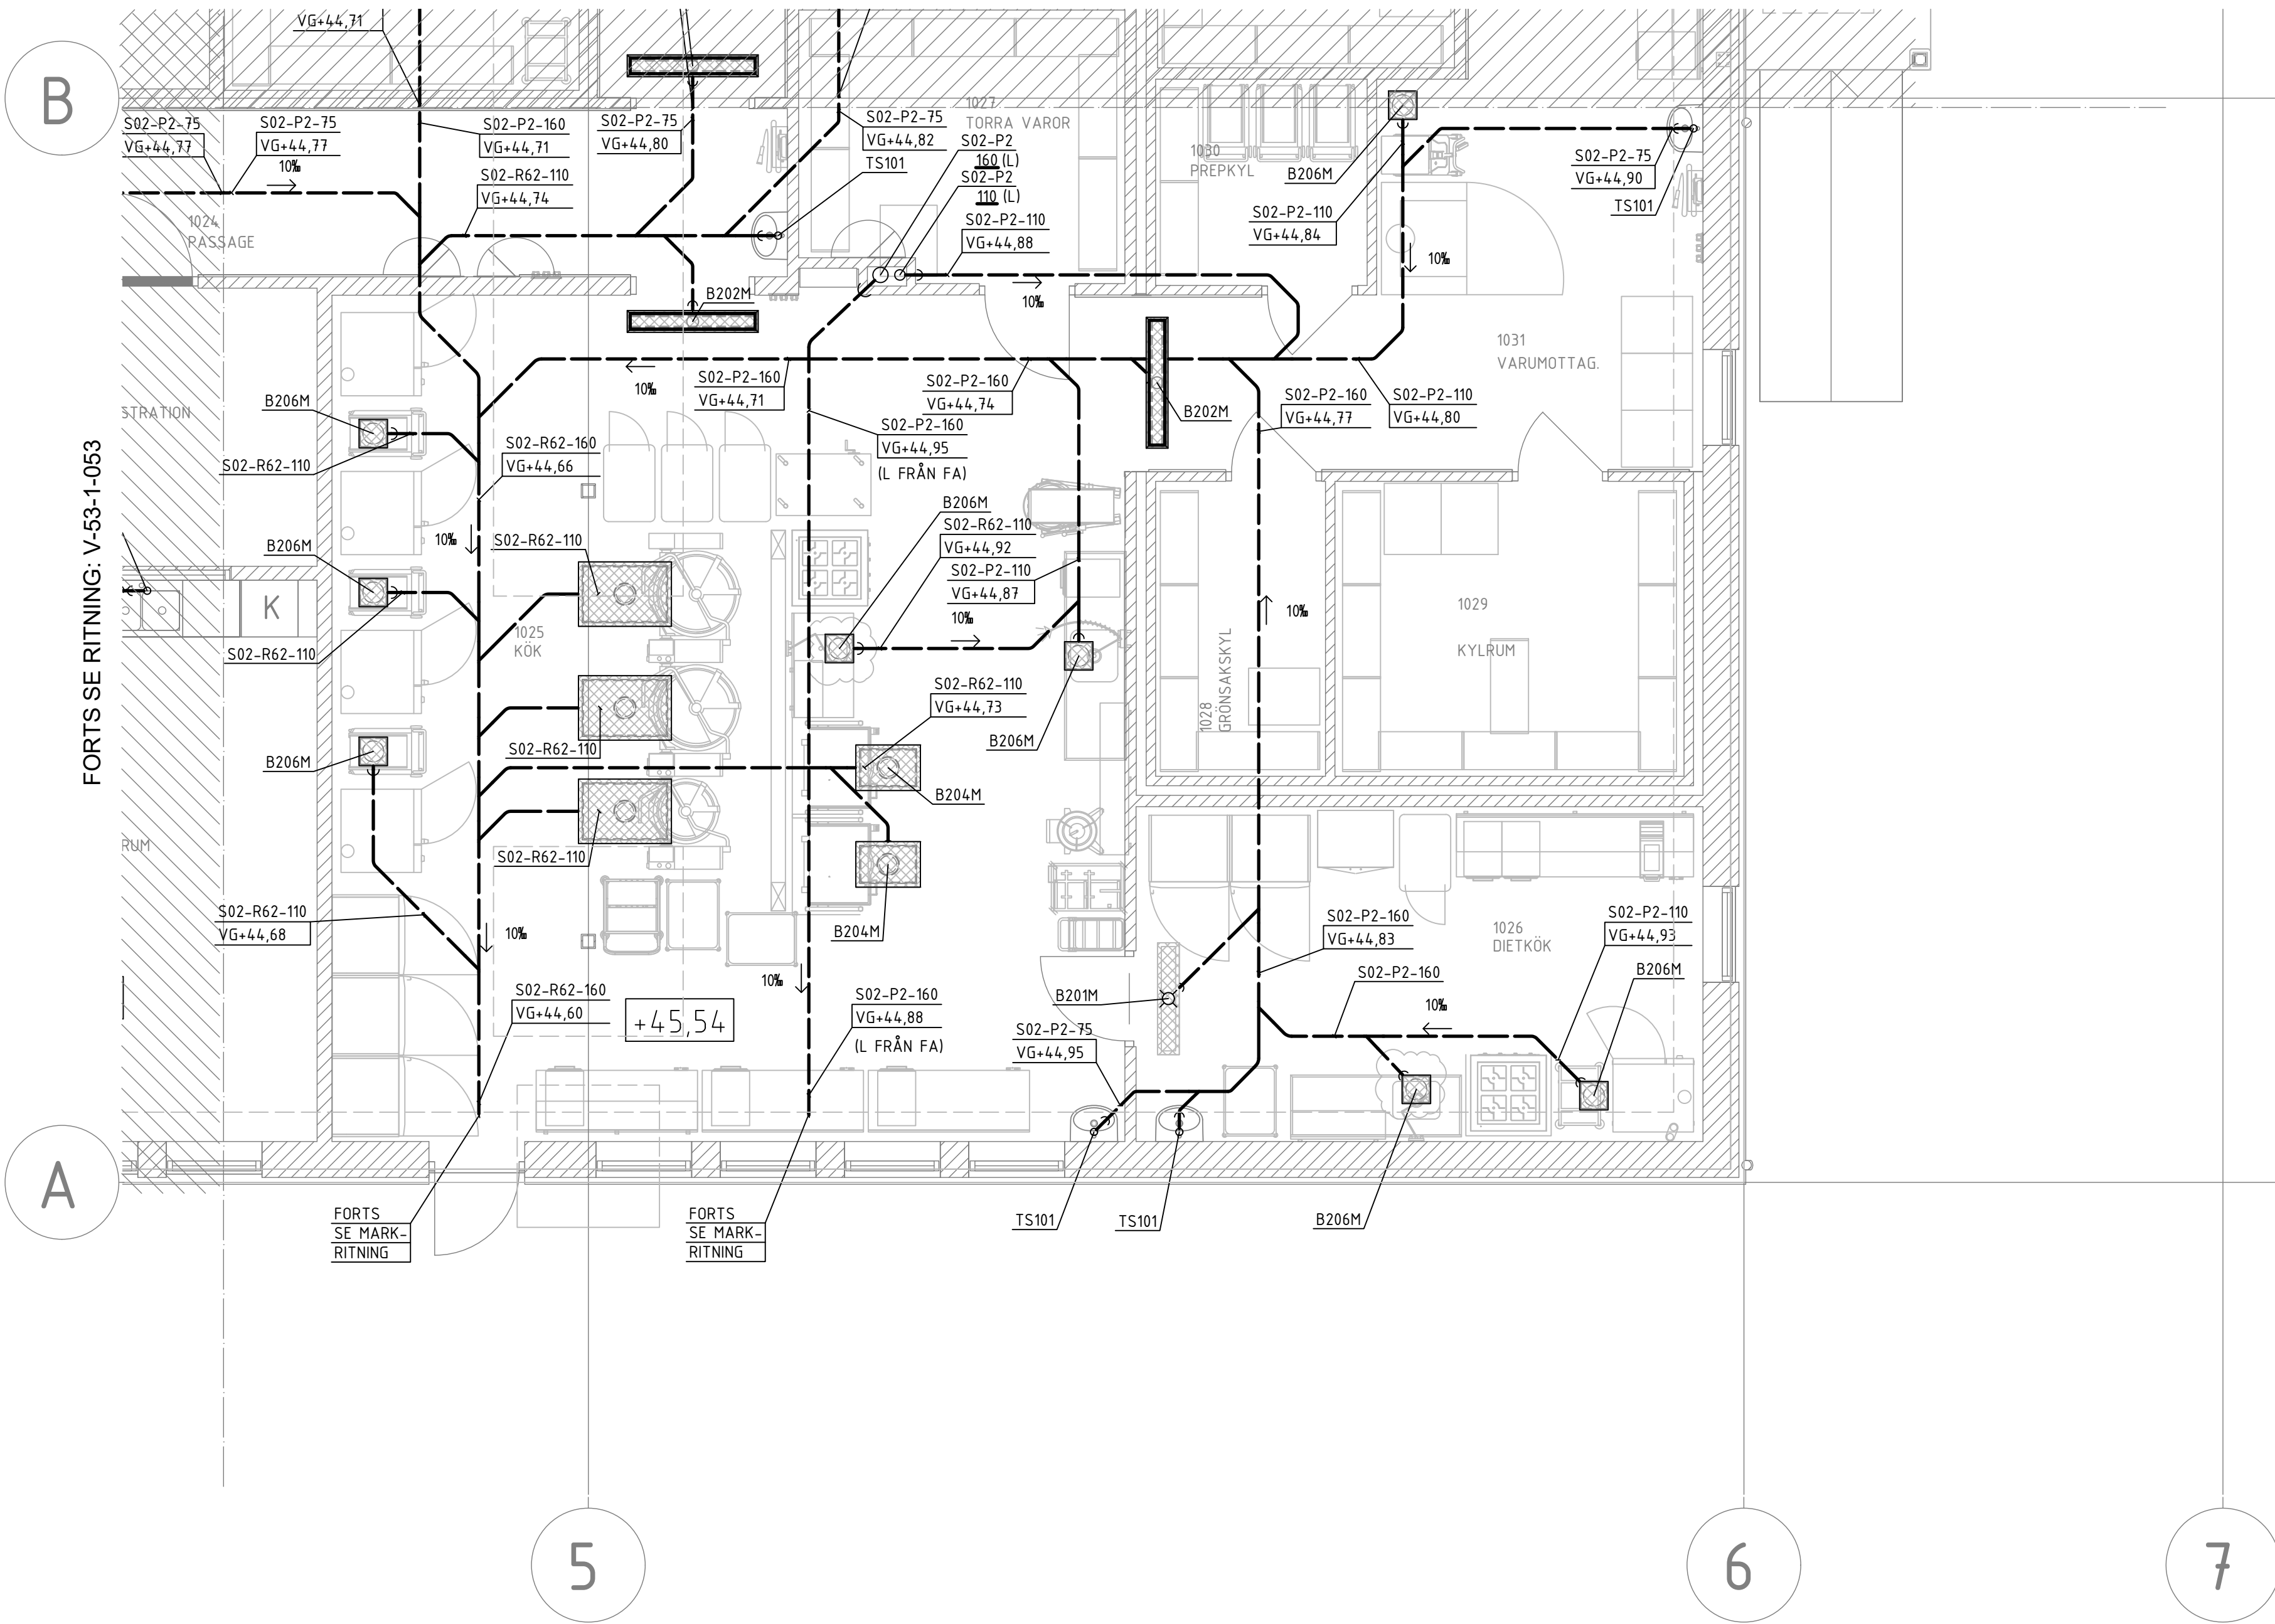

ORIENTERINGSSKISS

DEL 7

DEL 2

DEL 3

DEL 4

DEL 5

DEL 6

DEL 1

STATUS

FÖRFRÅGNINGSUNDERLAG

HANDLING

BYGGHANDLING

DATUM

2024-12-20

GODKÄND AV

T.BERGSTRÖM

ÄNDRINGS PM

BESTÄLLARE

ROBERTSFORS
KOMMUN

PROJEKTNAMN

CENTRALKÖK

OMRADE

ROBERTSFORS KOMMUN

PROJEKTNUMMER

FÖRRETT

YTTRE RINGVÄGEN 4

DARIENUMMER

FASTIGHET

FORDONET 1

DISCIPLIN

FÖRETAG

NORCONSULT SVERIGE AB

ÖPPNINGSNUMMER

SKAPAD AV

MAN

TELEFON

KONTAKTPERSON

JONAS JOHANSSON

BYGGNADSVÄRDE

(KLIMATKORRIGERT 2000)

+45,54 (FG)

VÄNINGSPLAN

VÄNINGSDEL

DELOMRÅDE

1

DEL 5.4

SYSTEM

53 SPILLVATTENINSTALLATIONER

BESKRIVNING

PLAN 0 - DEL 5.4, UNDER PLATTA

RITNINGSKATEGORI

PLAN

SKALA

1:50

FORMAT

A1

DOKUMENTNUMMER

ÄNDRING

V-53-1-054