



FÖRKLARINGSTEXT
SE RITNING V-50-0-001

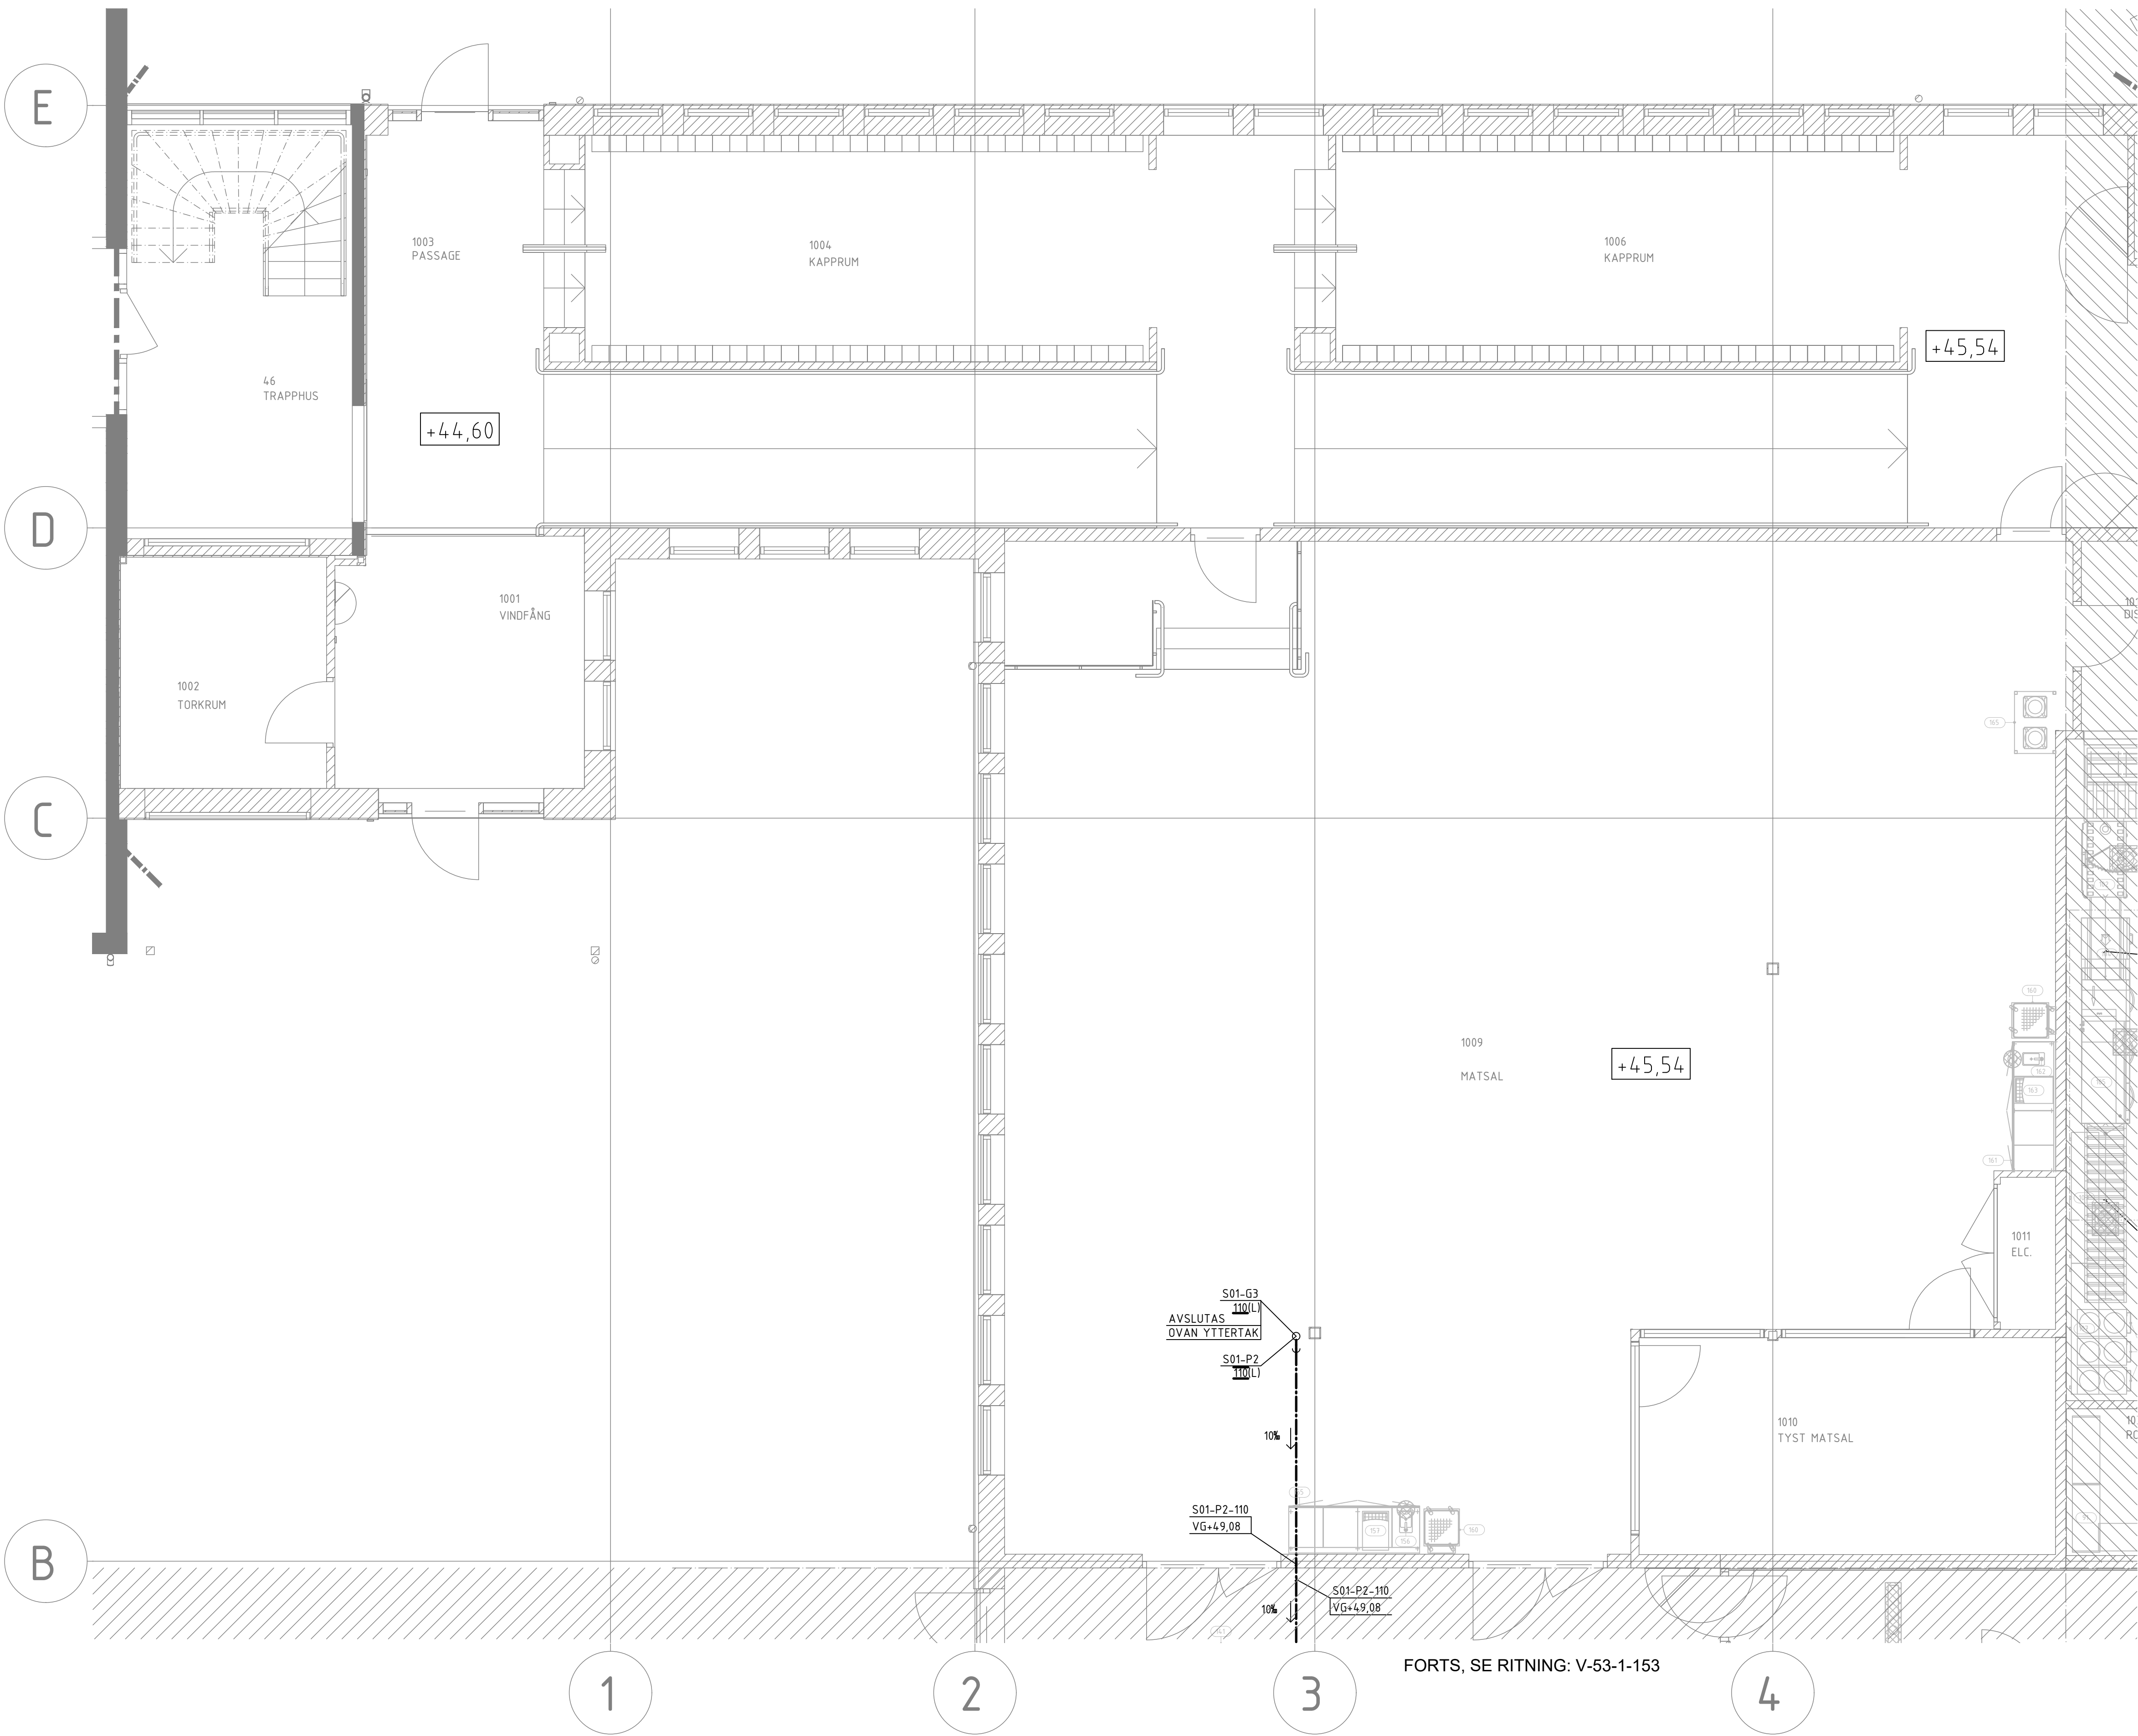

FORTS SE RITNING: V-53-1-152

SEKTION		
ORIENTERINGSPOL		
STATUS		
FÖRFRÅGNINGSUNDERLAG		
HANDLING		
BYGGHANDLING		
DATUM	2024-12-20	ODOKAND AV
DOKUMENT	T.BERGSTRÖM	ANDRINGS PM
BESTÄLLARE		
PROJEKTNAMN		
CENTRALKÖK		
OMRADE		
ROBERTSFORS KOMMUN		
PROJEKTNUMMER	FÖRRETT	YTTRE RINGVÄGEN 4
DARIENUMMER	FASTIGHET	FÖRÖNET 1
DISCIPLIN	FÖRETAG	NORCONSULT SVERIGE AB
OPPRÄGGSNUMMER	SKAPAD AV	MAN
TELEFON	KONTAKTPERSON	JONAS JOHANSSON
BYGGNADSVÄR	(KLUBBID RPH 2001)	+45,54 (FG)
VÄNINGSPLAN	VÄNINGSDEL	DELOMRÅDE
1		DEL 4.1, 5.1
SYSTEM		
53 SPILLVATTENINSTALLATIONER		
PLAN 1 - DEL 4.1, 5.1		
RITNINGSKATEGORI	SKALA	FORMAT
PLAN	1:50	A1
DOKUMENTNUMMER	ANDRNING	
V-53-1-151		

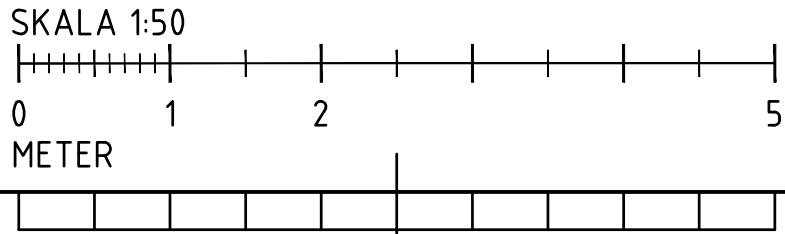

FILNAMN: