
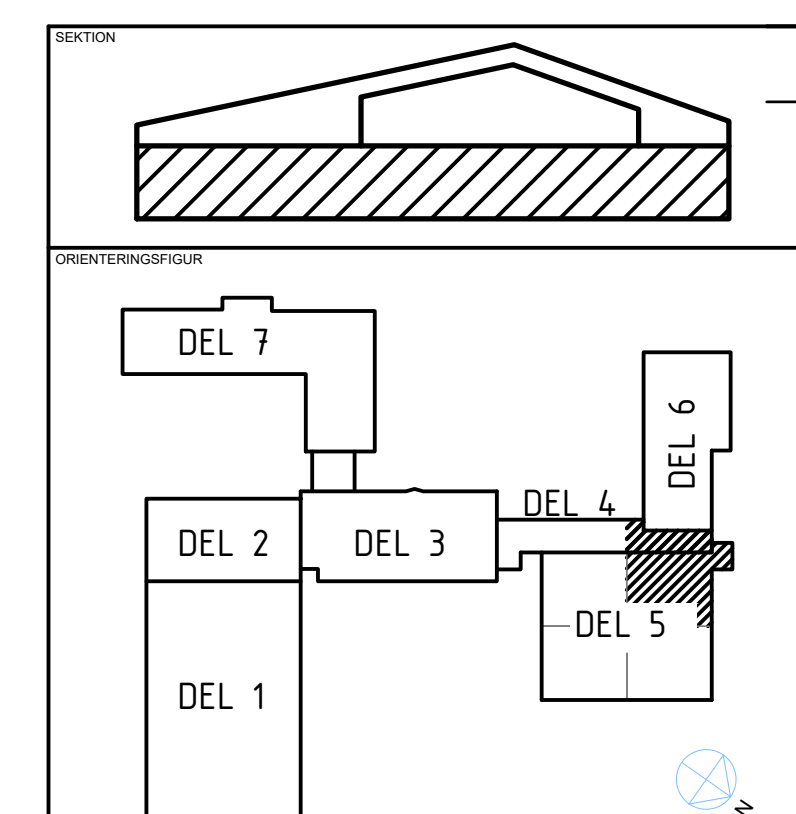


FÖRKLARINGSTEXT
SE RITNING V-50-0-001

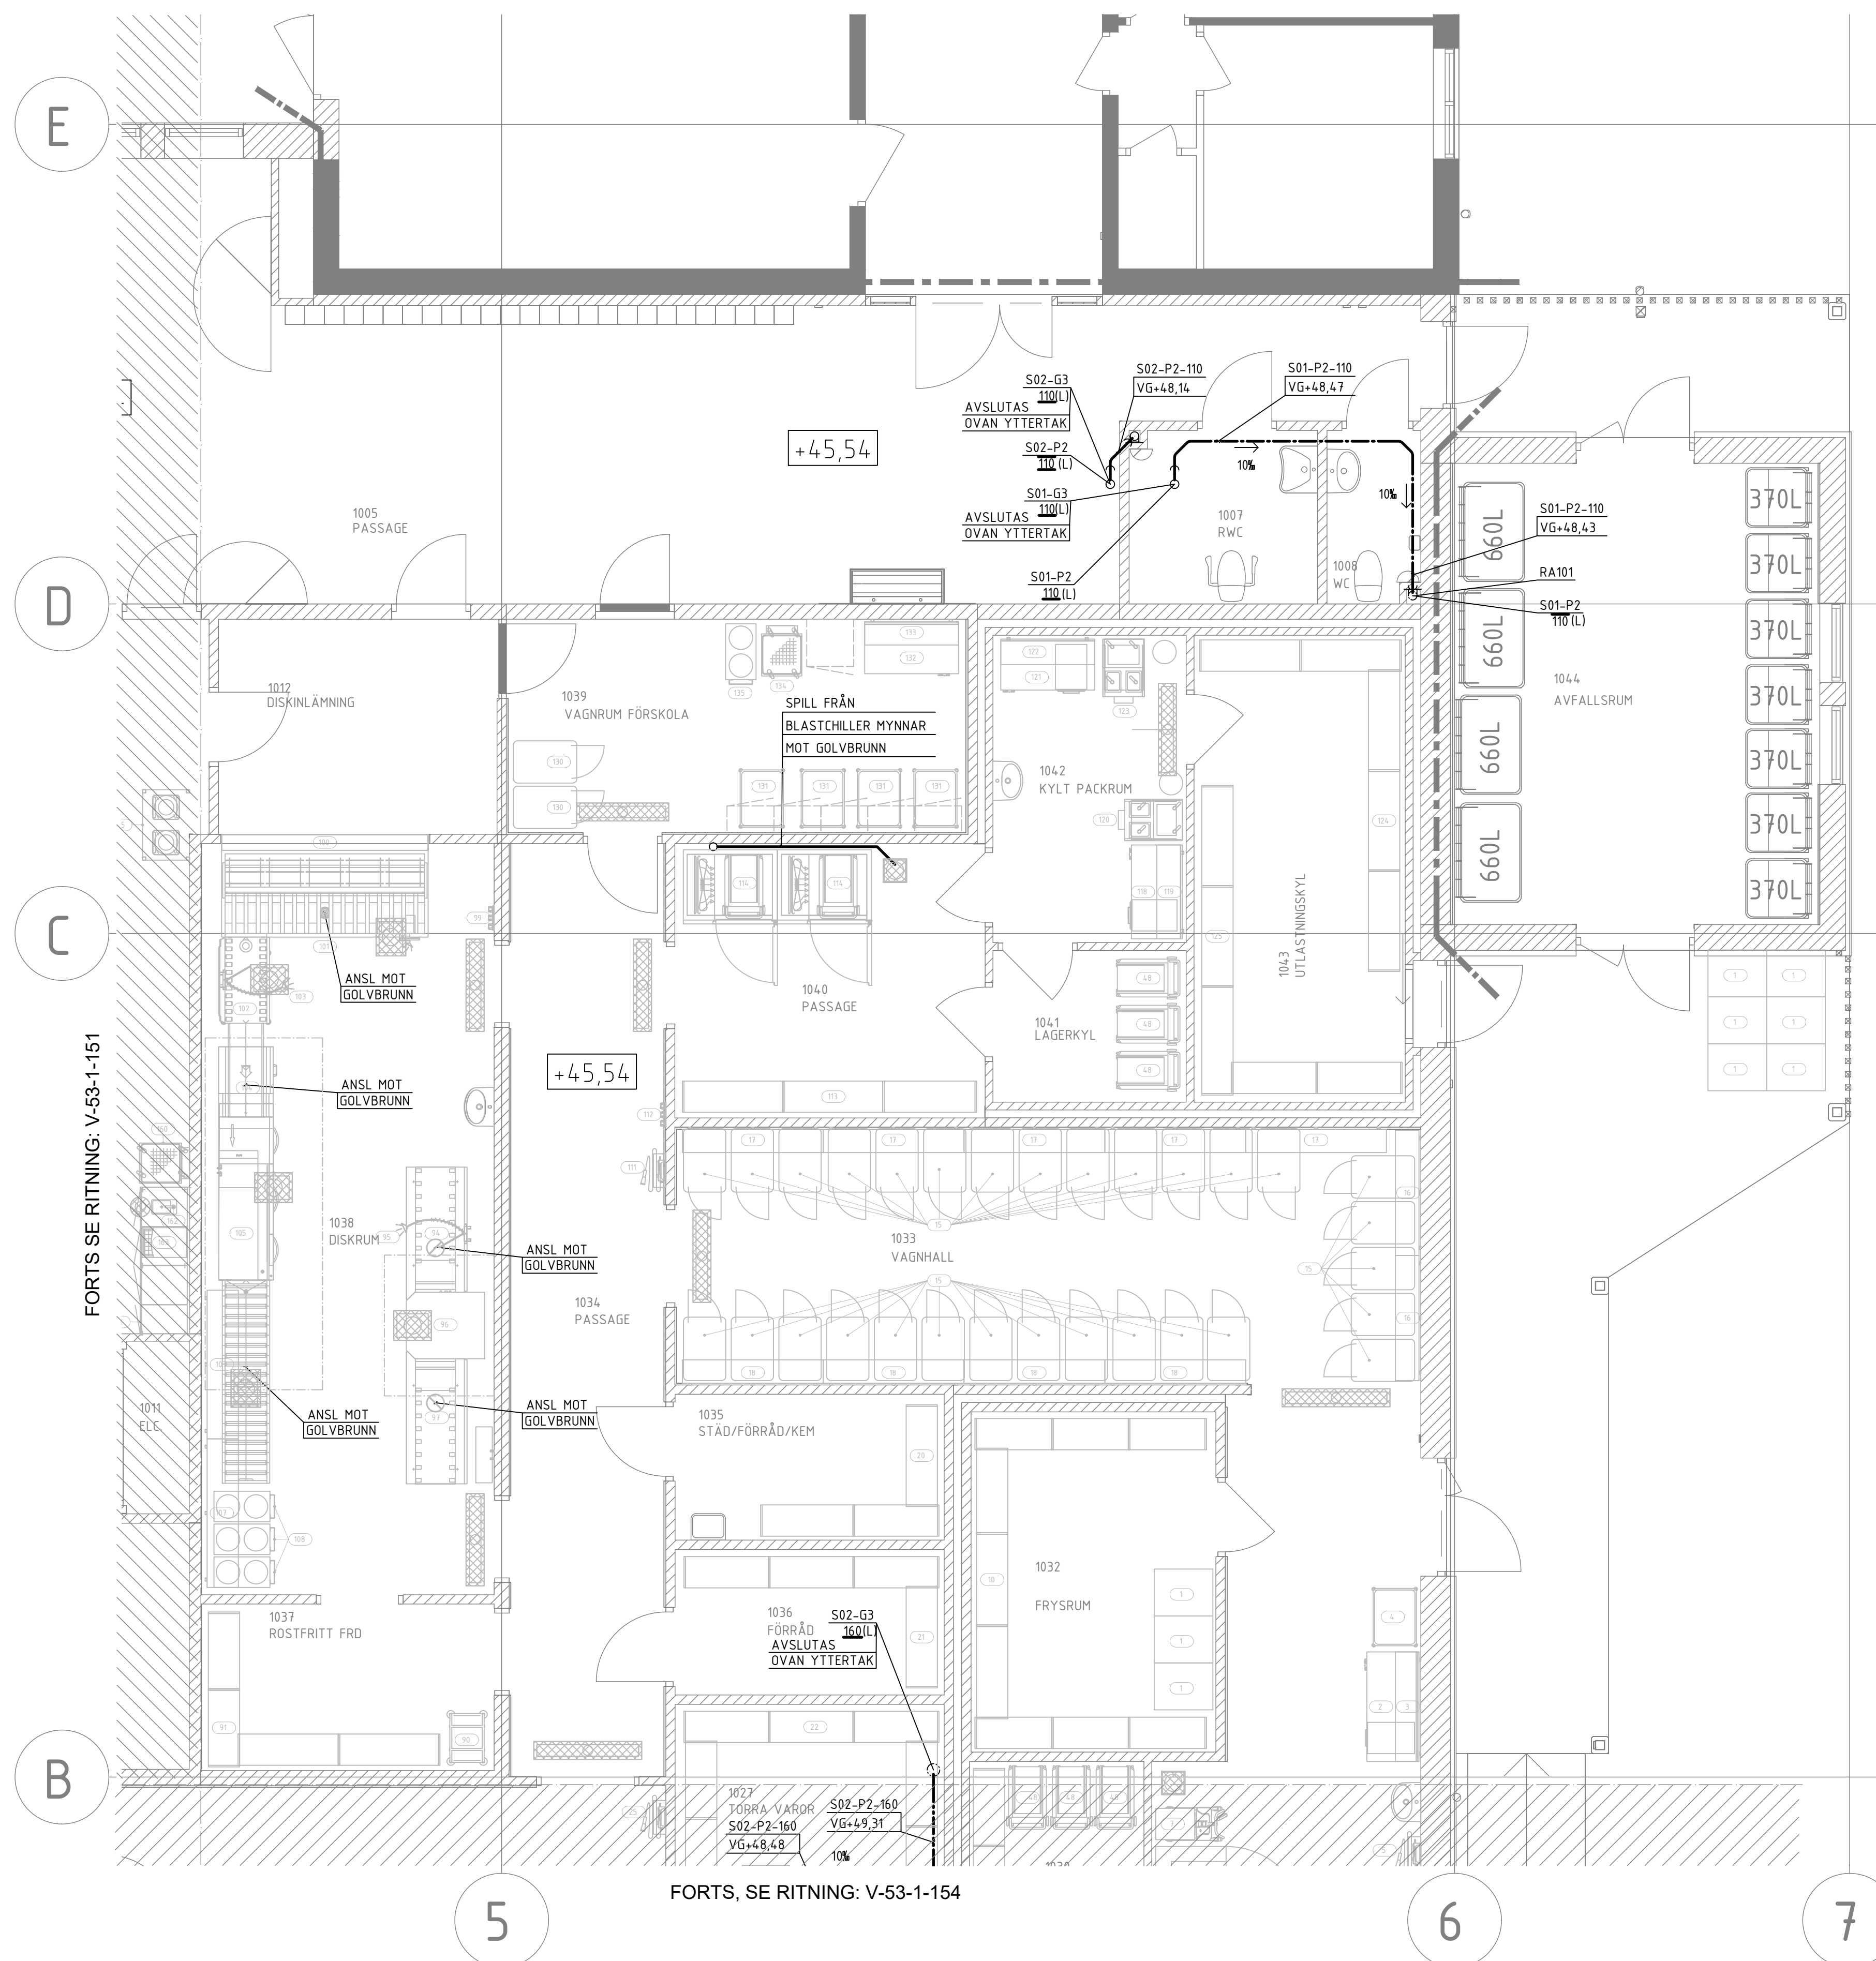

STATUS FÖRFRÅGNINGSUNDERLAG

BYGGHANDLING

DATUM	GODKÄND AV	ÄNDRINGS PM
2024-12-20	T.BERGSTRÖM	

2024-12-20	T.BERGSTRÖM	
BESTÄLLARE		



PROJEKTNAMN

CENTRAALKÖK

OMRADE ROBERTSFORS KOMMUN

PROJEKTNUMMER	ADRESS
	YTTRE RINGVÄGEN 4

DIARIENUMMER	FASTIGHET FORDONET 1
--------------	-------------------------

DISCIPLIN	FÖRETAG
	NORCONSULT SVERIGE AB

UPPDRAGSNUMMER	SKAPAD AV
108 83 71	MAN

108 85 71	MAN
TELEFON	KONTAKTPERSON
010 141 80 00	TOMAS BERGSTRÖM

010 141 80 00	TOMAS BERGSTRÖM
BYGGNADSVÄRK	FLUSHÖJD (RH 2000)
	+45 54 (EFG)

		+45,54 (FG)
VÄNINGSPLAN	VÄNINGSDEL	DELOMRÅDE
1		DEL 4.2.5.2

1		DEL 4.2, 5.2
SYSTEM		
53 SPILL VATTENINSTALLATIONER		

53 SPILLVATTENINSTÄLLNING	
SPECIFIKATION	
PLAN 1	DEL 4, 2, 5, 2

RITNINGSKATEGORI	SKALA	FORM
PLAN	1:50	A4

PLAN	1:50	A1
DOKUMENTNUMMER		ANDR

V-53-1-152

	1	2	
--	---	---	---	---	---	---	---	---	---	----	----	-----

SKALA 1:50

0 1 2 5

METER

[illegible]