
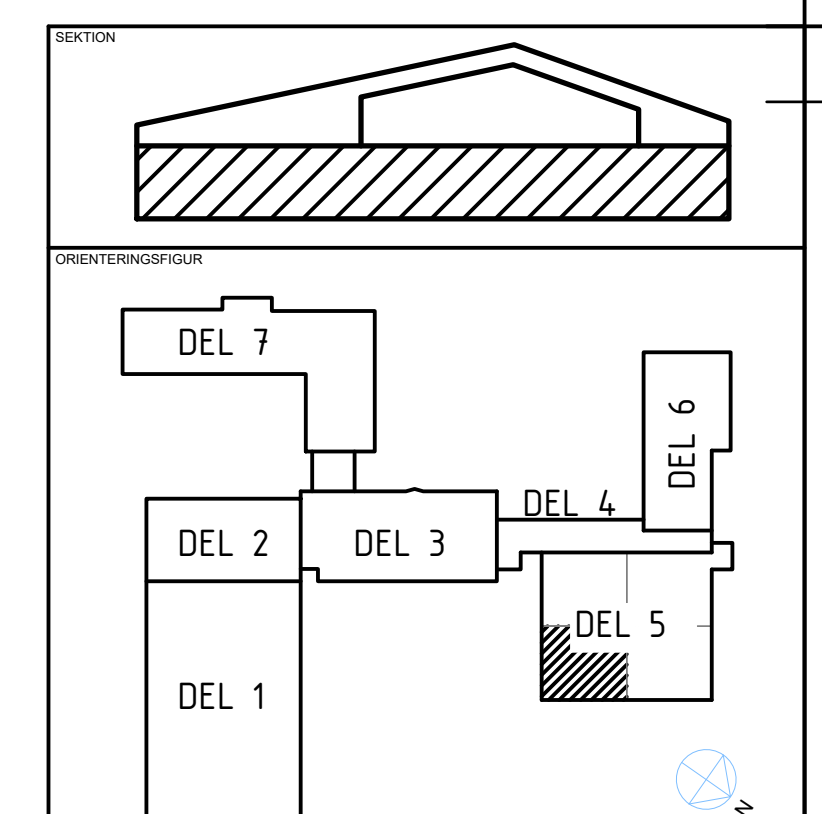


FÖRKLARINGSTEXT
SE RITNING V-50-0-001

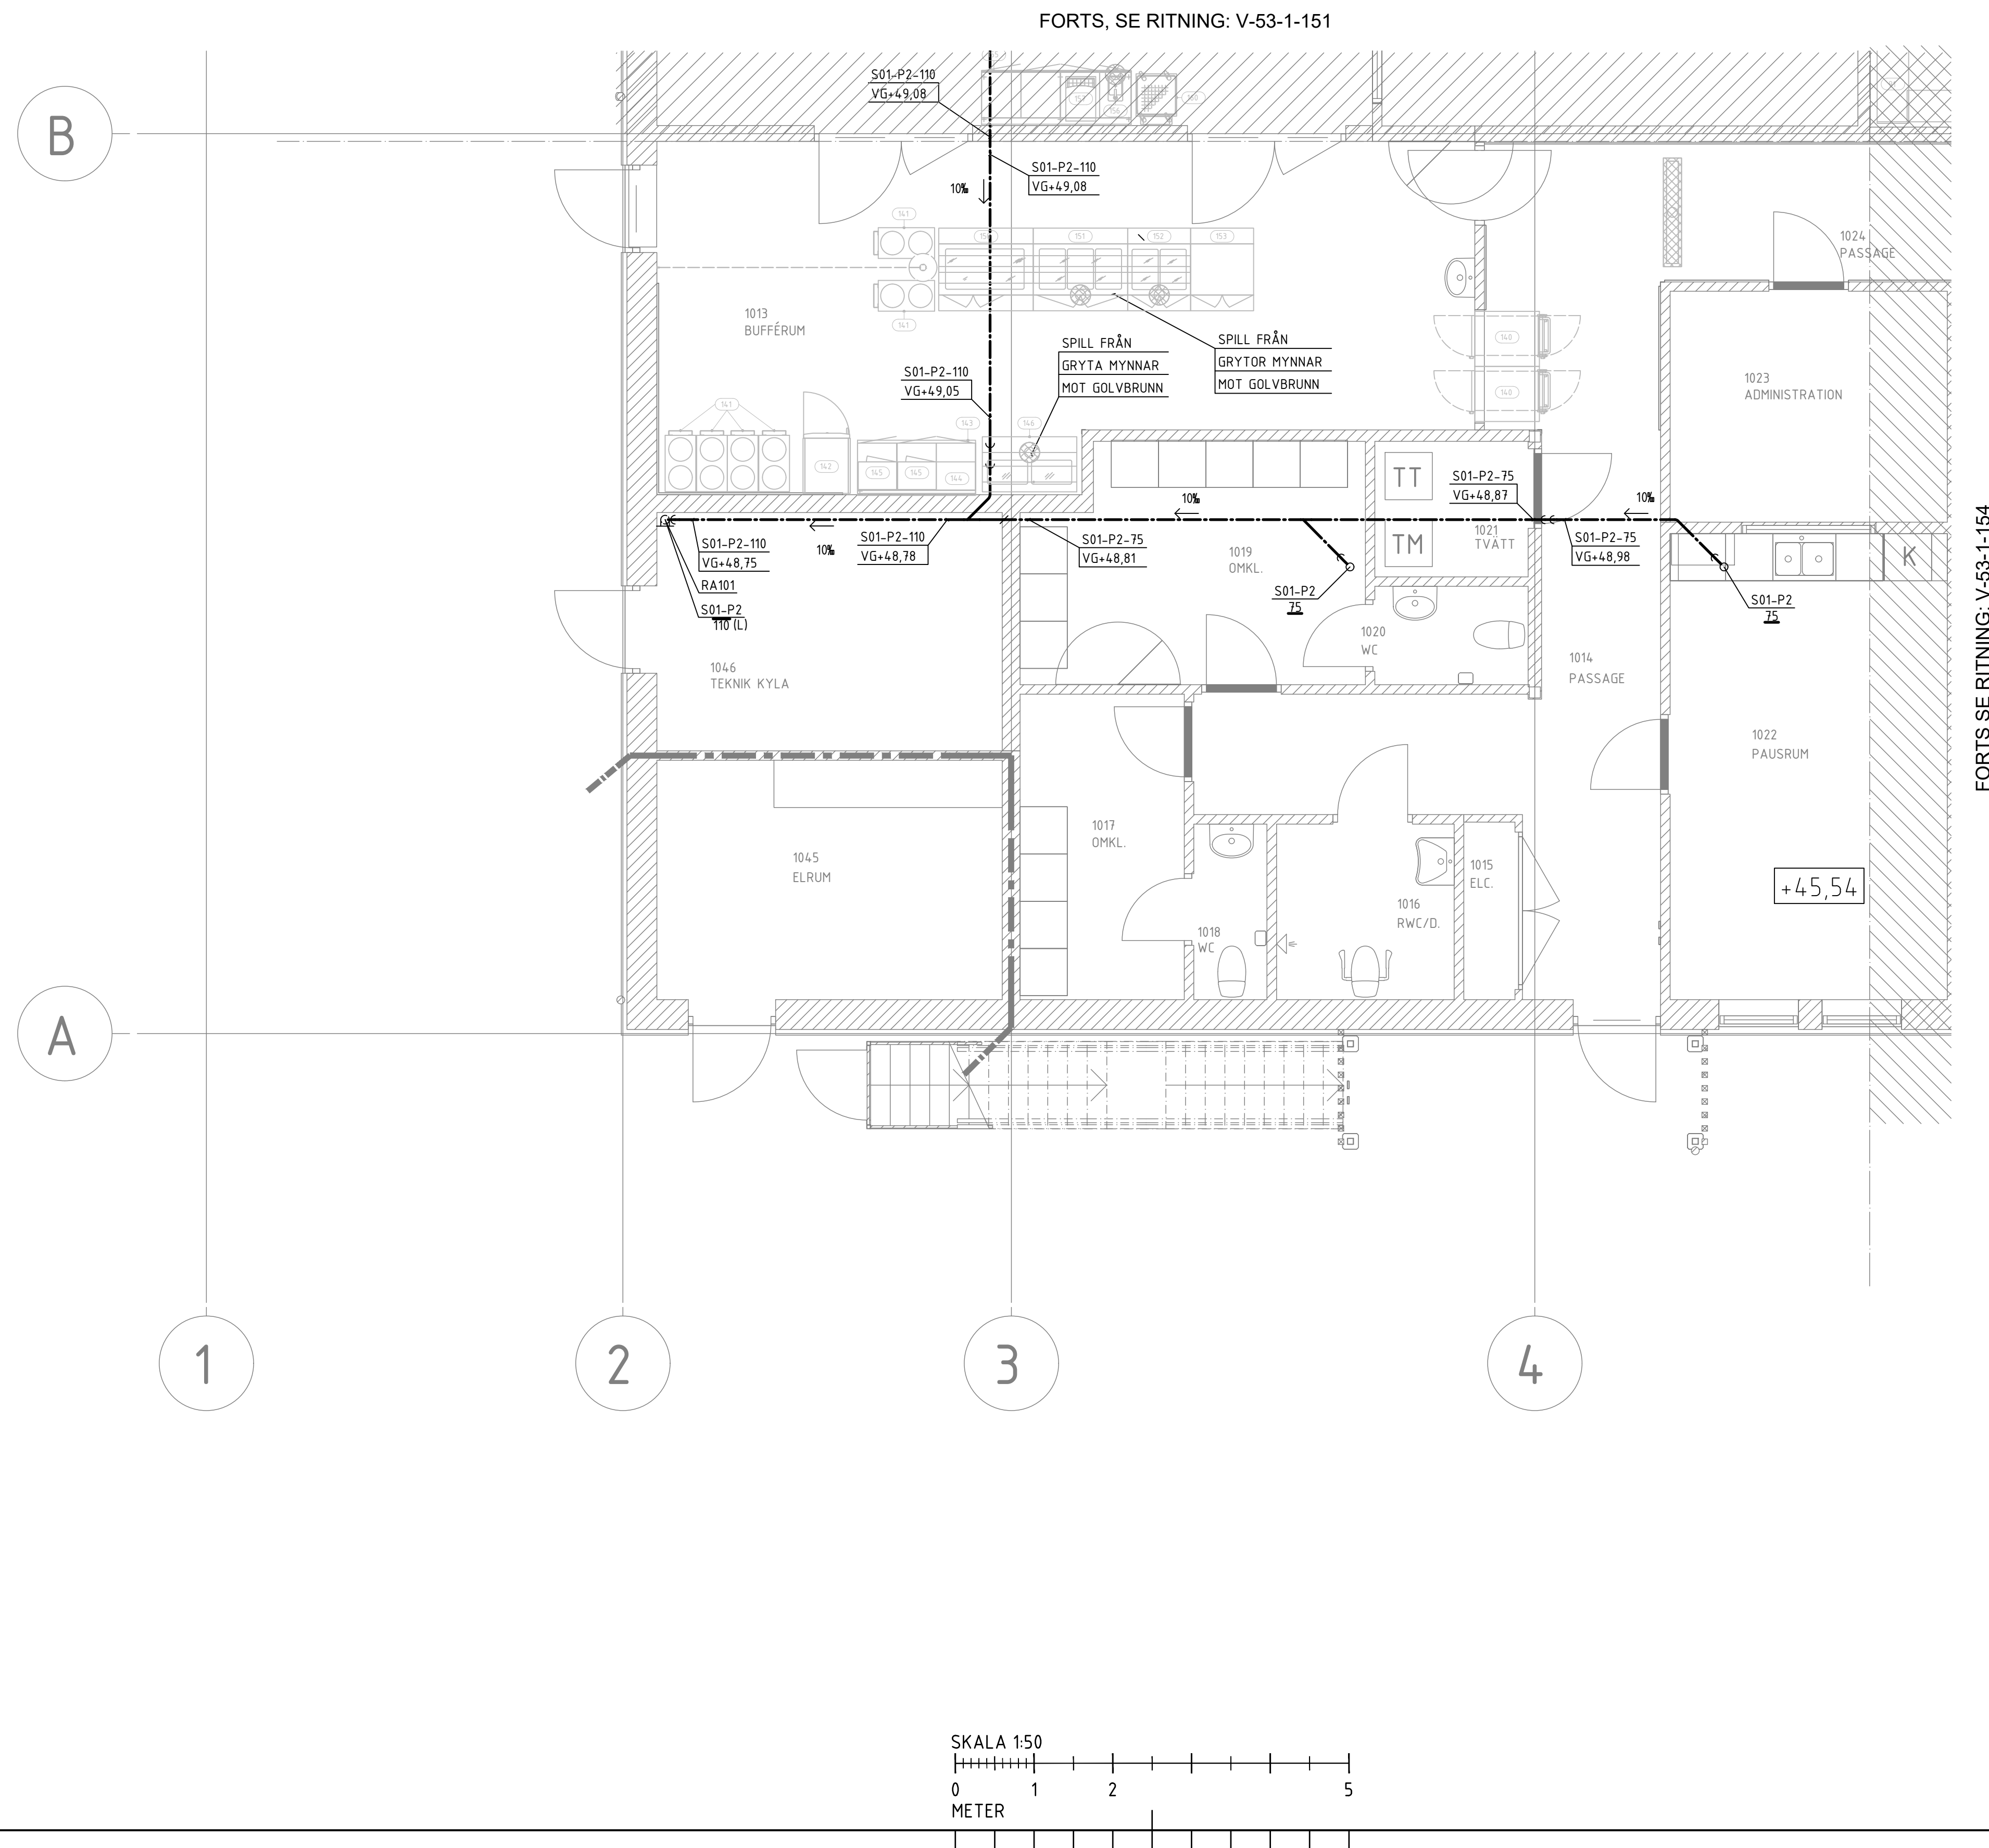

STATUS			
FÖRFRÅGNINGSUNDERLAG			
HANDLING			
DATUM 2023-12-20		GÖRKÄND AV T.BERGSTRÖM	
BESTÄLLARE		ÄNDRINGS FM	
			
ROBERTSFORS KOMMUN			
PROJEKTNÄMN			
CENTRALKÖK			
OMRÅDE			
ROBERTSFORS KOMMUN			
PROJEKTNUMMER		ADRESS	
		YTTRE RINGVÄGEN 4	
CHARAKTERNUMMER		FÖRORDNET 1	
BESÖKSVIN VS		FÖRSTÄ NORCONSULT SVERIGE AB	
UTFÖRARNUMMER 108 83 71		SKAVAD AV MAN	
TELEFON 010 141 80 00		KONTAKTPERSON JONAS JOHANSSON	
BYGGNÄMNSVERK		PULSKOD (RM 2000) +45 54 (FG) DELKOMRÅDE	
VÄNINGSPLAN 1		VÄNINGSDEL DEL 5.3	
SYSTEM			
53 SPILLVATTENINSTALLATIONER			
SPECIFICATION			
PLAN 1 - DEL 5.3			
RITNINGSGRUPP PLAN		SKALA 1:50	FORMAT A1
DOKUMENTNUMMER V-53-1-153			ÄNDRING