
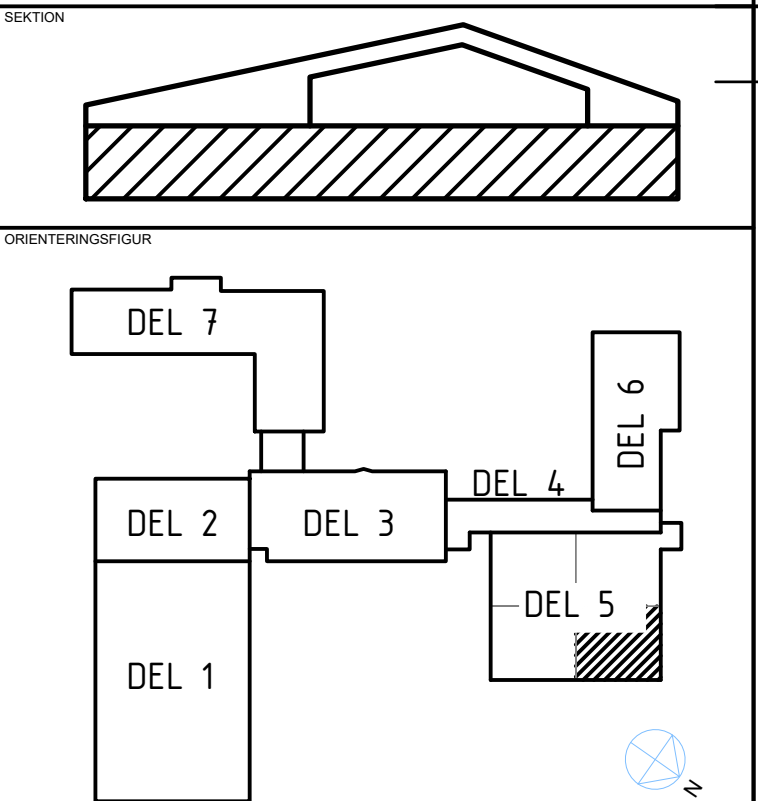
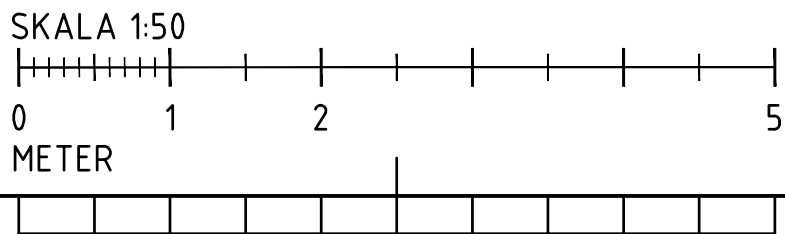


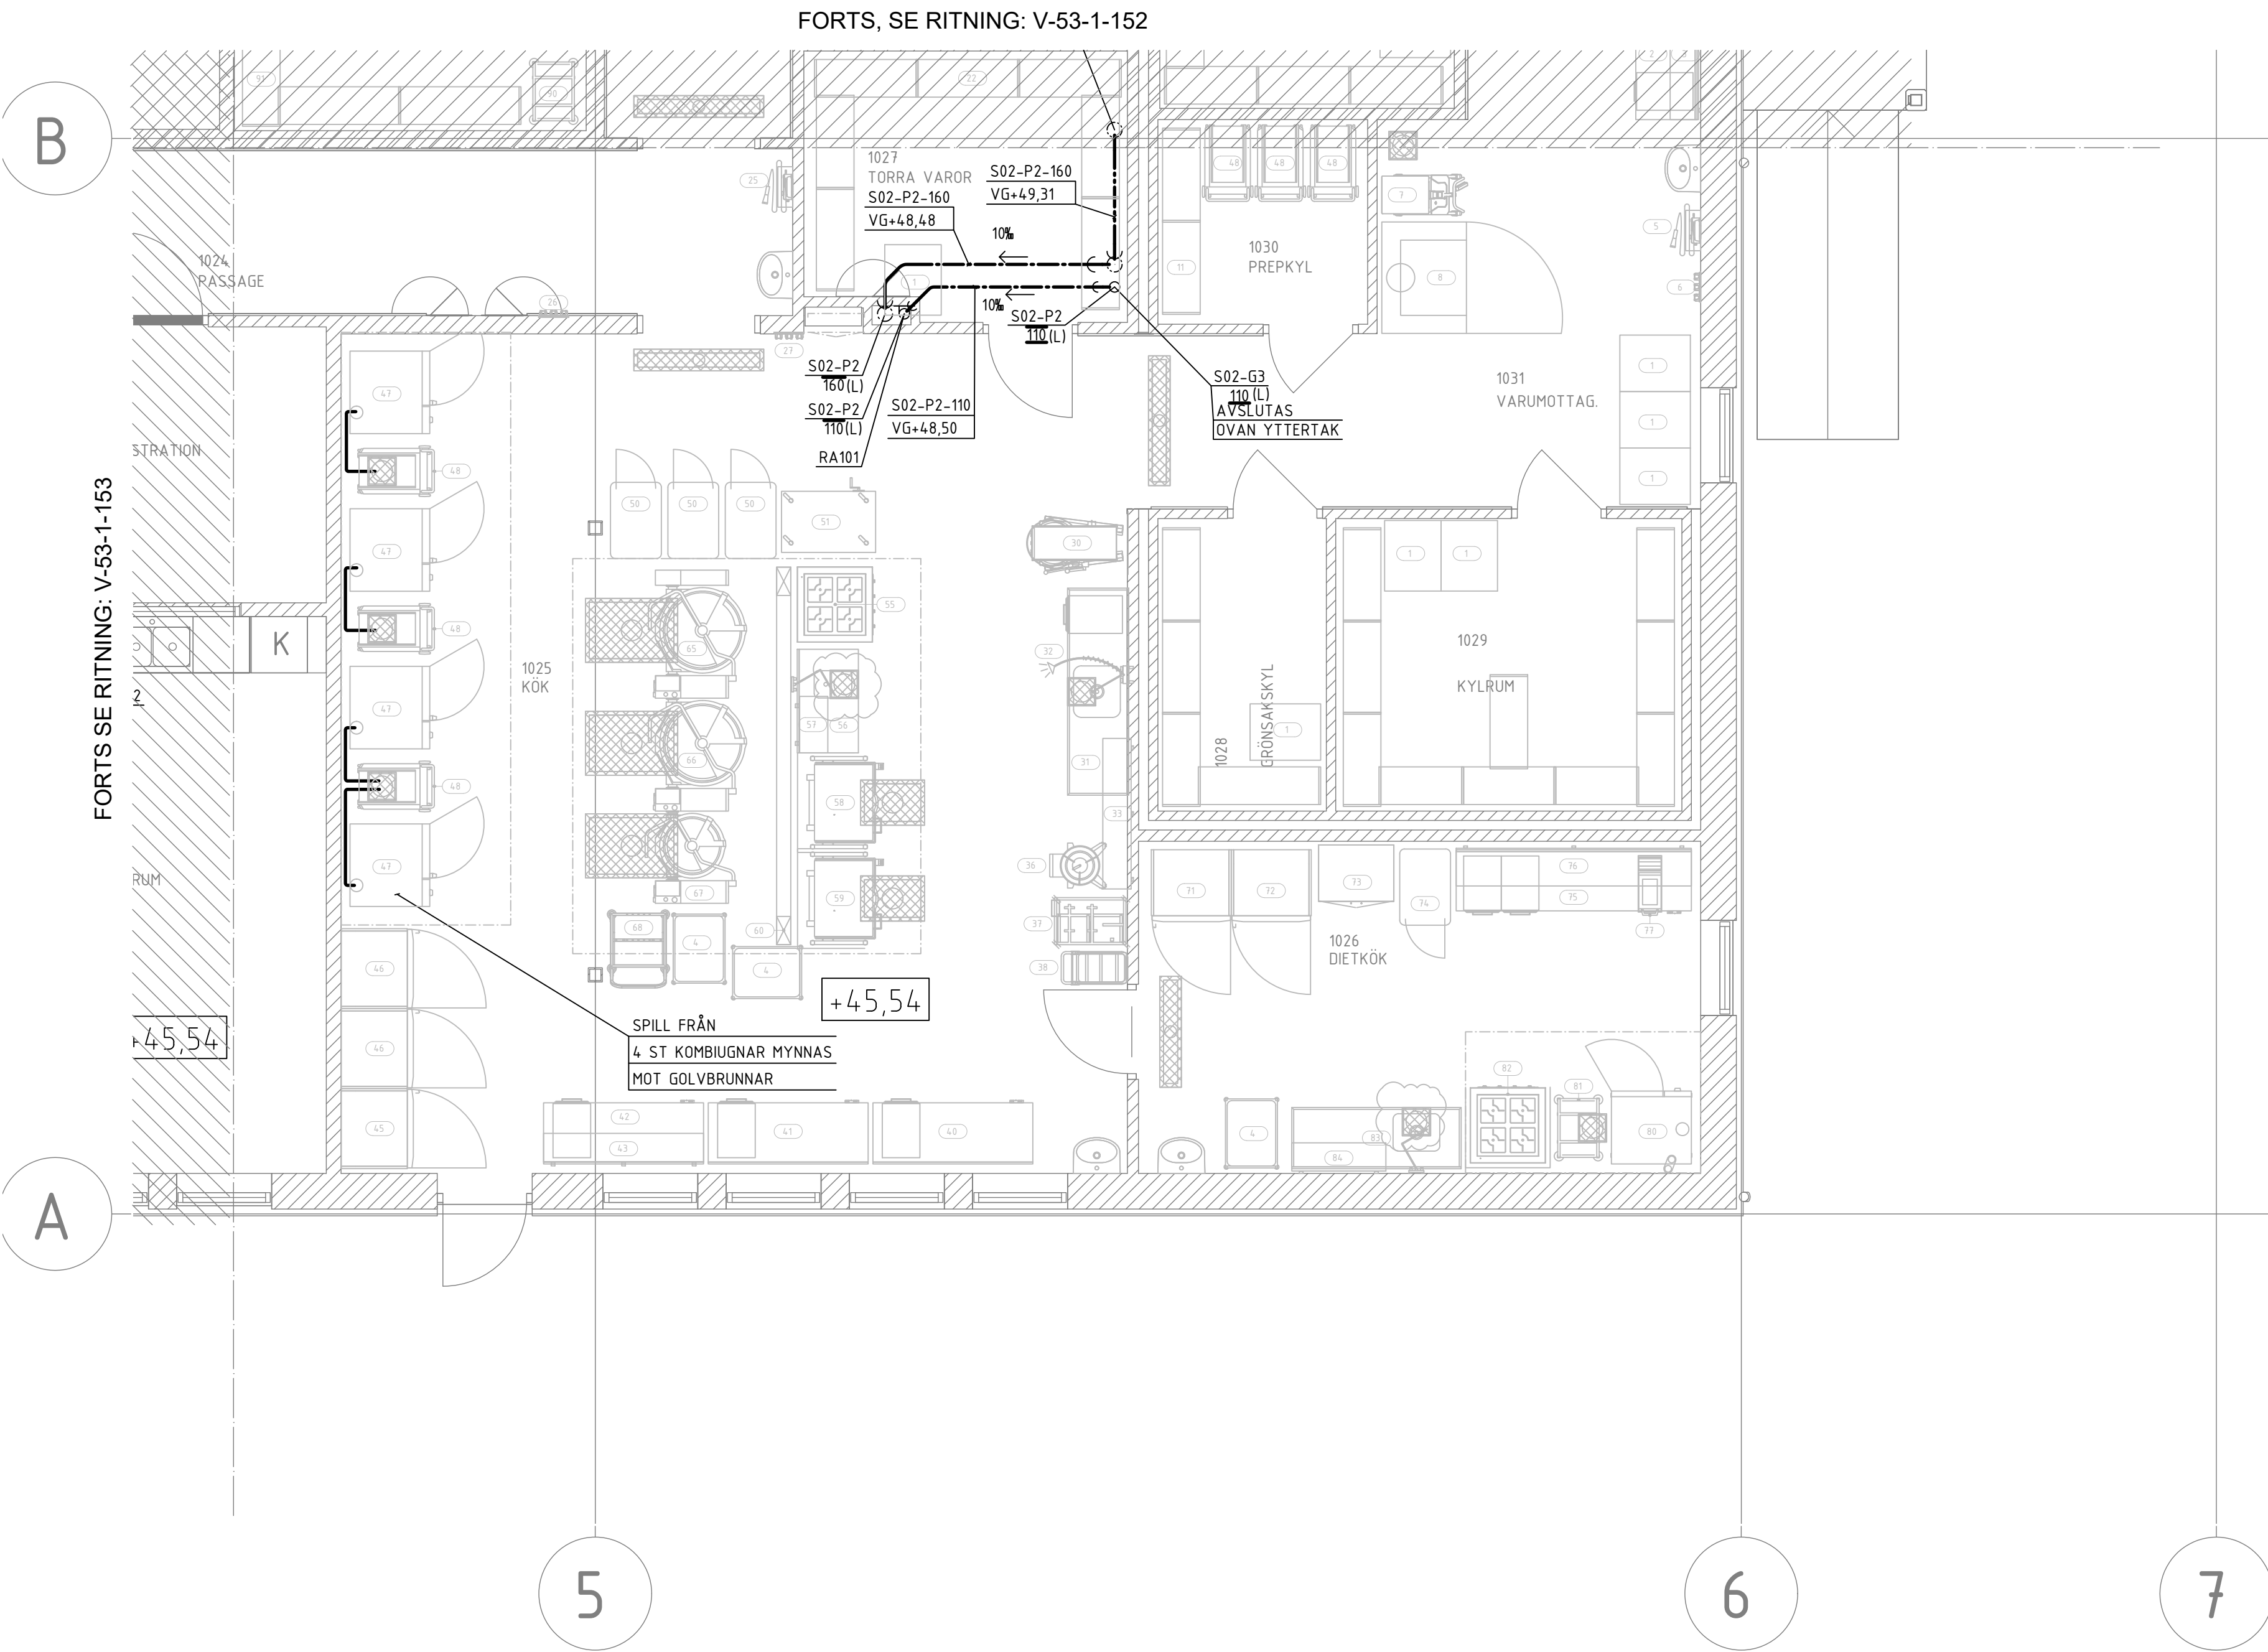

STATUS		FÖRFRÅGNINGSUNDERLAG			
HANDLING		BYGGHANDLING			
DATUM	2024-12-20	GODKÄND AV	T.BERGSTRÖM	ÄNDRINGS PM	
BESTÄLLARE					
		ROBERTSFORS KOMMUN			
PROJEKTNAMN					
CENTRALKÖK					
OMRÅDE					
ROBERTSFORS KOMMUN					
PROJEKTNUMMER	ADRESS				
	YTIRE RINGVÄGEN 4				
DARIENUMMER	FASTIGHET				
	FÖRDET 1				
DISCIPLIN	FÖRETAG				
VS	NORCONSULT SVERIGE AB				
OPPFÖRINGSNUMMER	SKAPAD AV				
108 83 71	MAN				
TELEFON	KONTAKTPERSON				
010 141 80 00	JONAS JOHANSSON				
BYGGNADSVÄRDE	(KLIMATKOD RPH 2009)				
	+45 54 (FG)				
VÄNINGSPLAN	VÄNINGSDEL				
1	DEL 5.4				
SYSTEM					
53 SPILLVATTENINSTALLATIONER					
BESKRIVNING					
PLAN 1 - DEL 5.4					
RITNINGSKATEGORI	SKALA			FORMAT	
PLAN	1:50			A1	
DOKUMENTNUMMER	ÄNDRING				
V-53-1-154					