
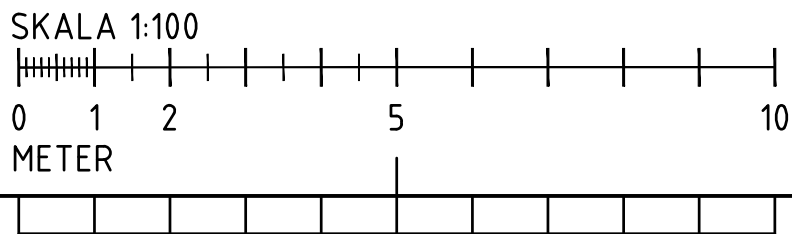


FÖRKLARINGSTEXT
SE RITNING V-50-0-001

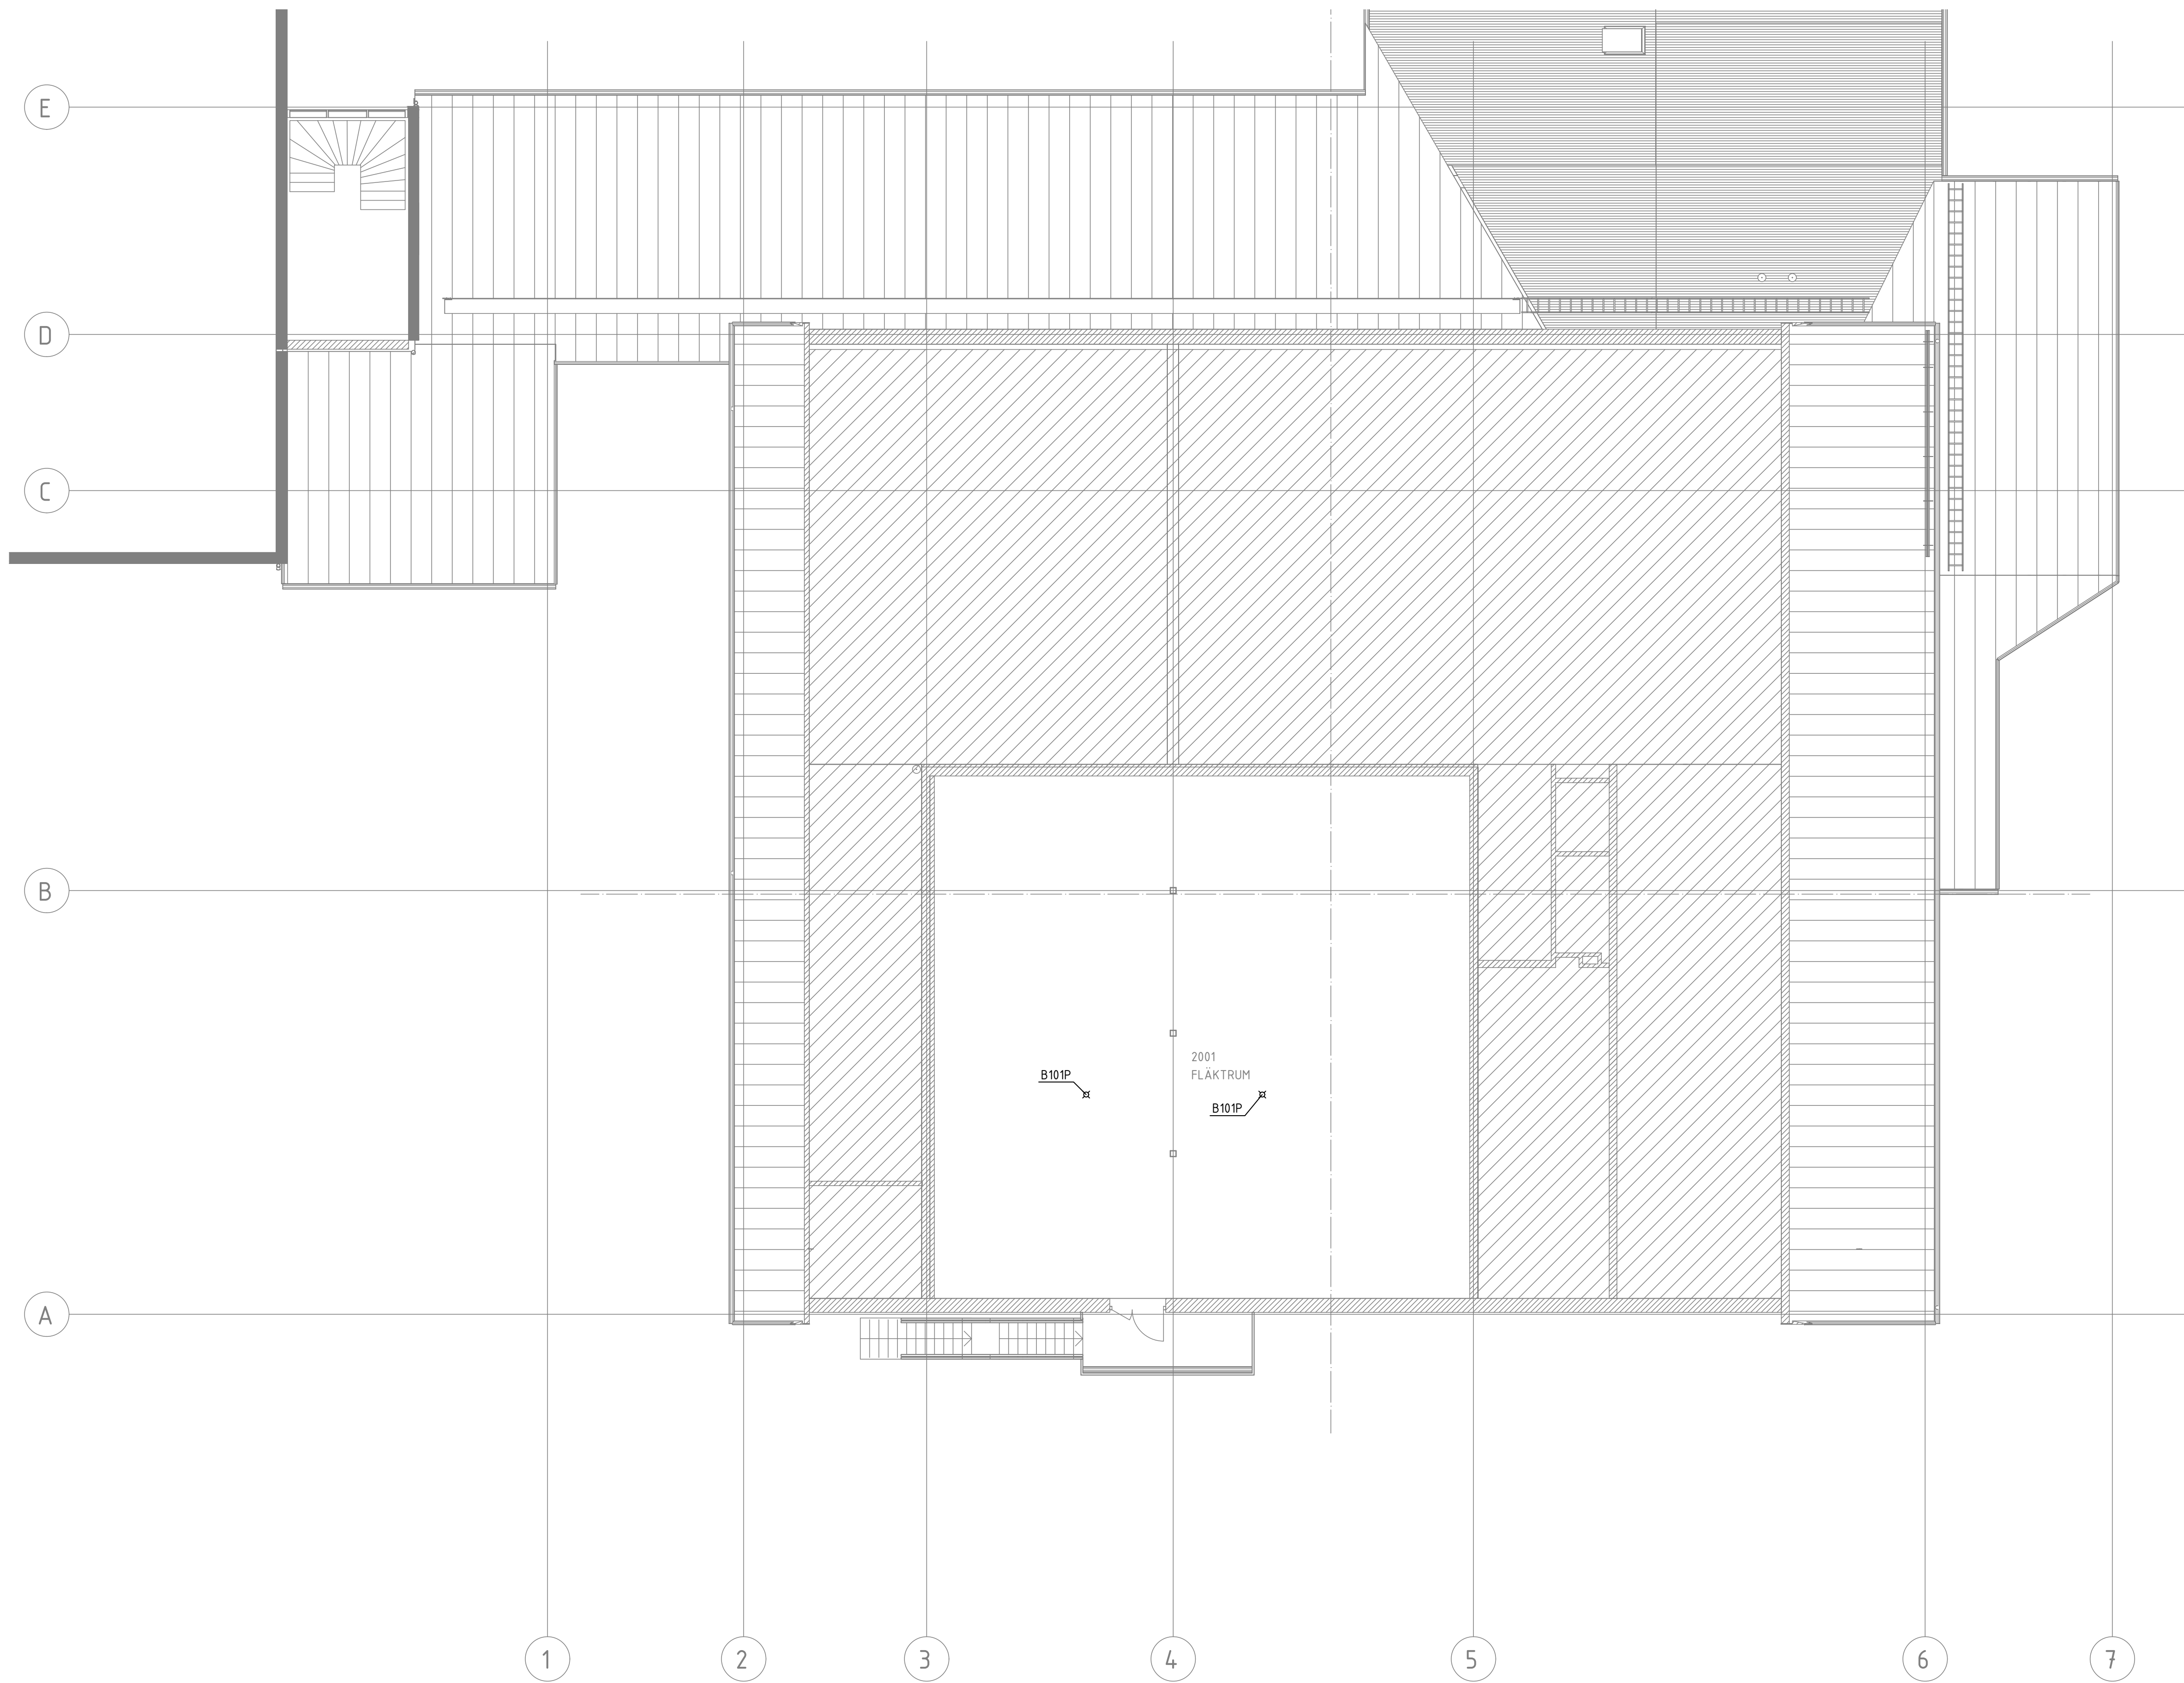

SEKTION

ORIENTERINGSPOL

DEL 1 DEL 2 DEL 3 DEL 4 DEL 5 DEL 6 DEL 7

STATUS

FÖRFRÅGNINGSUNDERLAG

HANDLING

BYGGHANDLING

DATUM

2024-12-20

GODKÄND AV

T.BERGSTRÖM

ANDRINGS PM

BESTÄLLARE

ROBERTSFORS KOMMUN

PROJEKTNAMN

CENTRALEKÖK

OMRADE

ROBERTSFORS KOMMUN

PROJEKTNUMMER

YTTRE RINGVÄGEN 4

DIARIENUMMER

FÖRORDNET 1

DISCIPLIN

NORCONSULT SVERIGE AB

OPPRÄGGSNUMMER

MAN

TELEFON

010 141 80 00

JONAS JOHANSSON

BYGGNADSVÄRDE

+49 54 (FG)

VÄNINGSPLAN

2

VÄNINGSDEL

DEL 4, 5

SYSTEM

53 SPILLVATTENINSTALLATIONER

PLAN 2 - ÖVERSIKT

SKALA

1:100

FORMAT

A1

DOKUMENTNUMMER

V-53-1-201