



FÖRKLARINGSTEXT
SE RITNING V-50-0-001

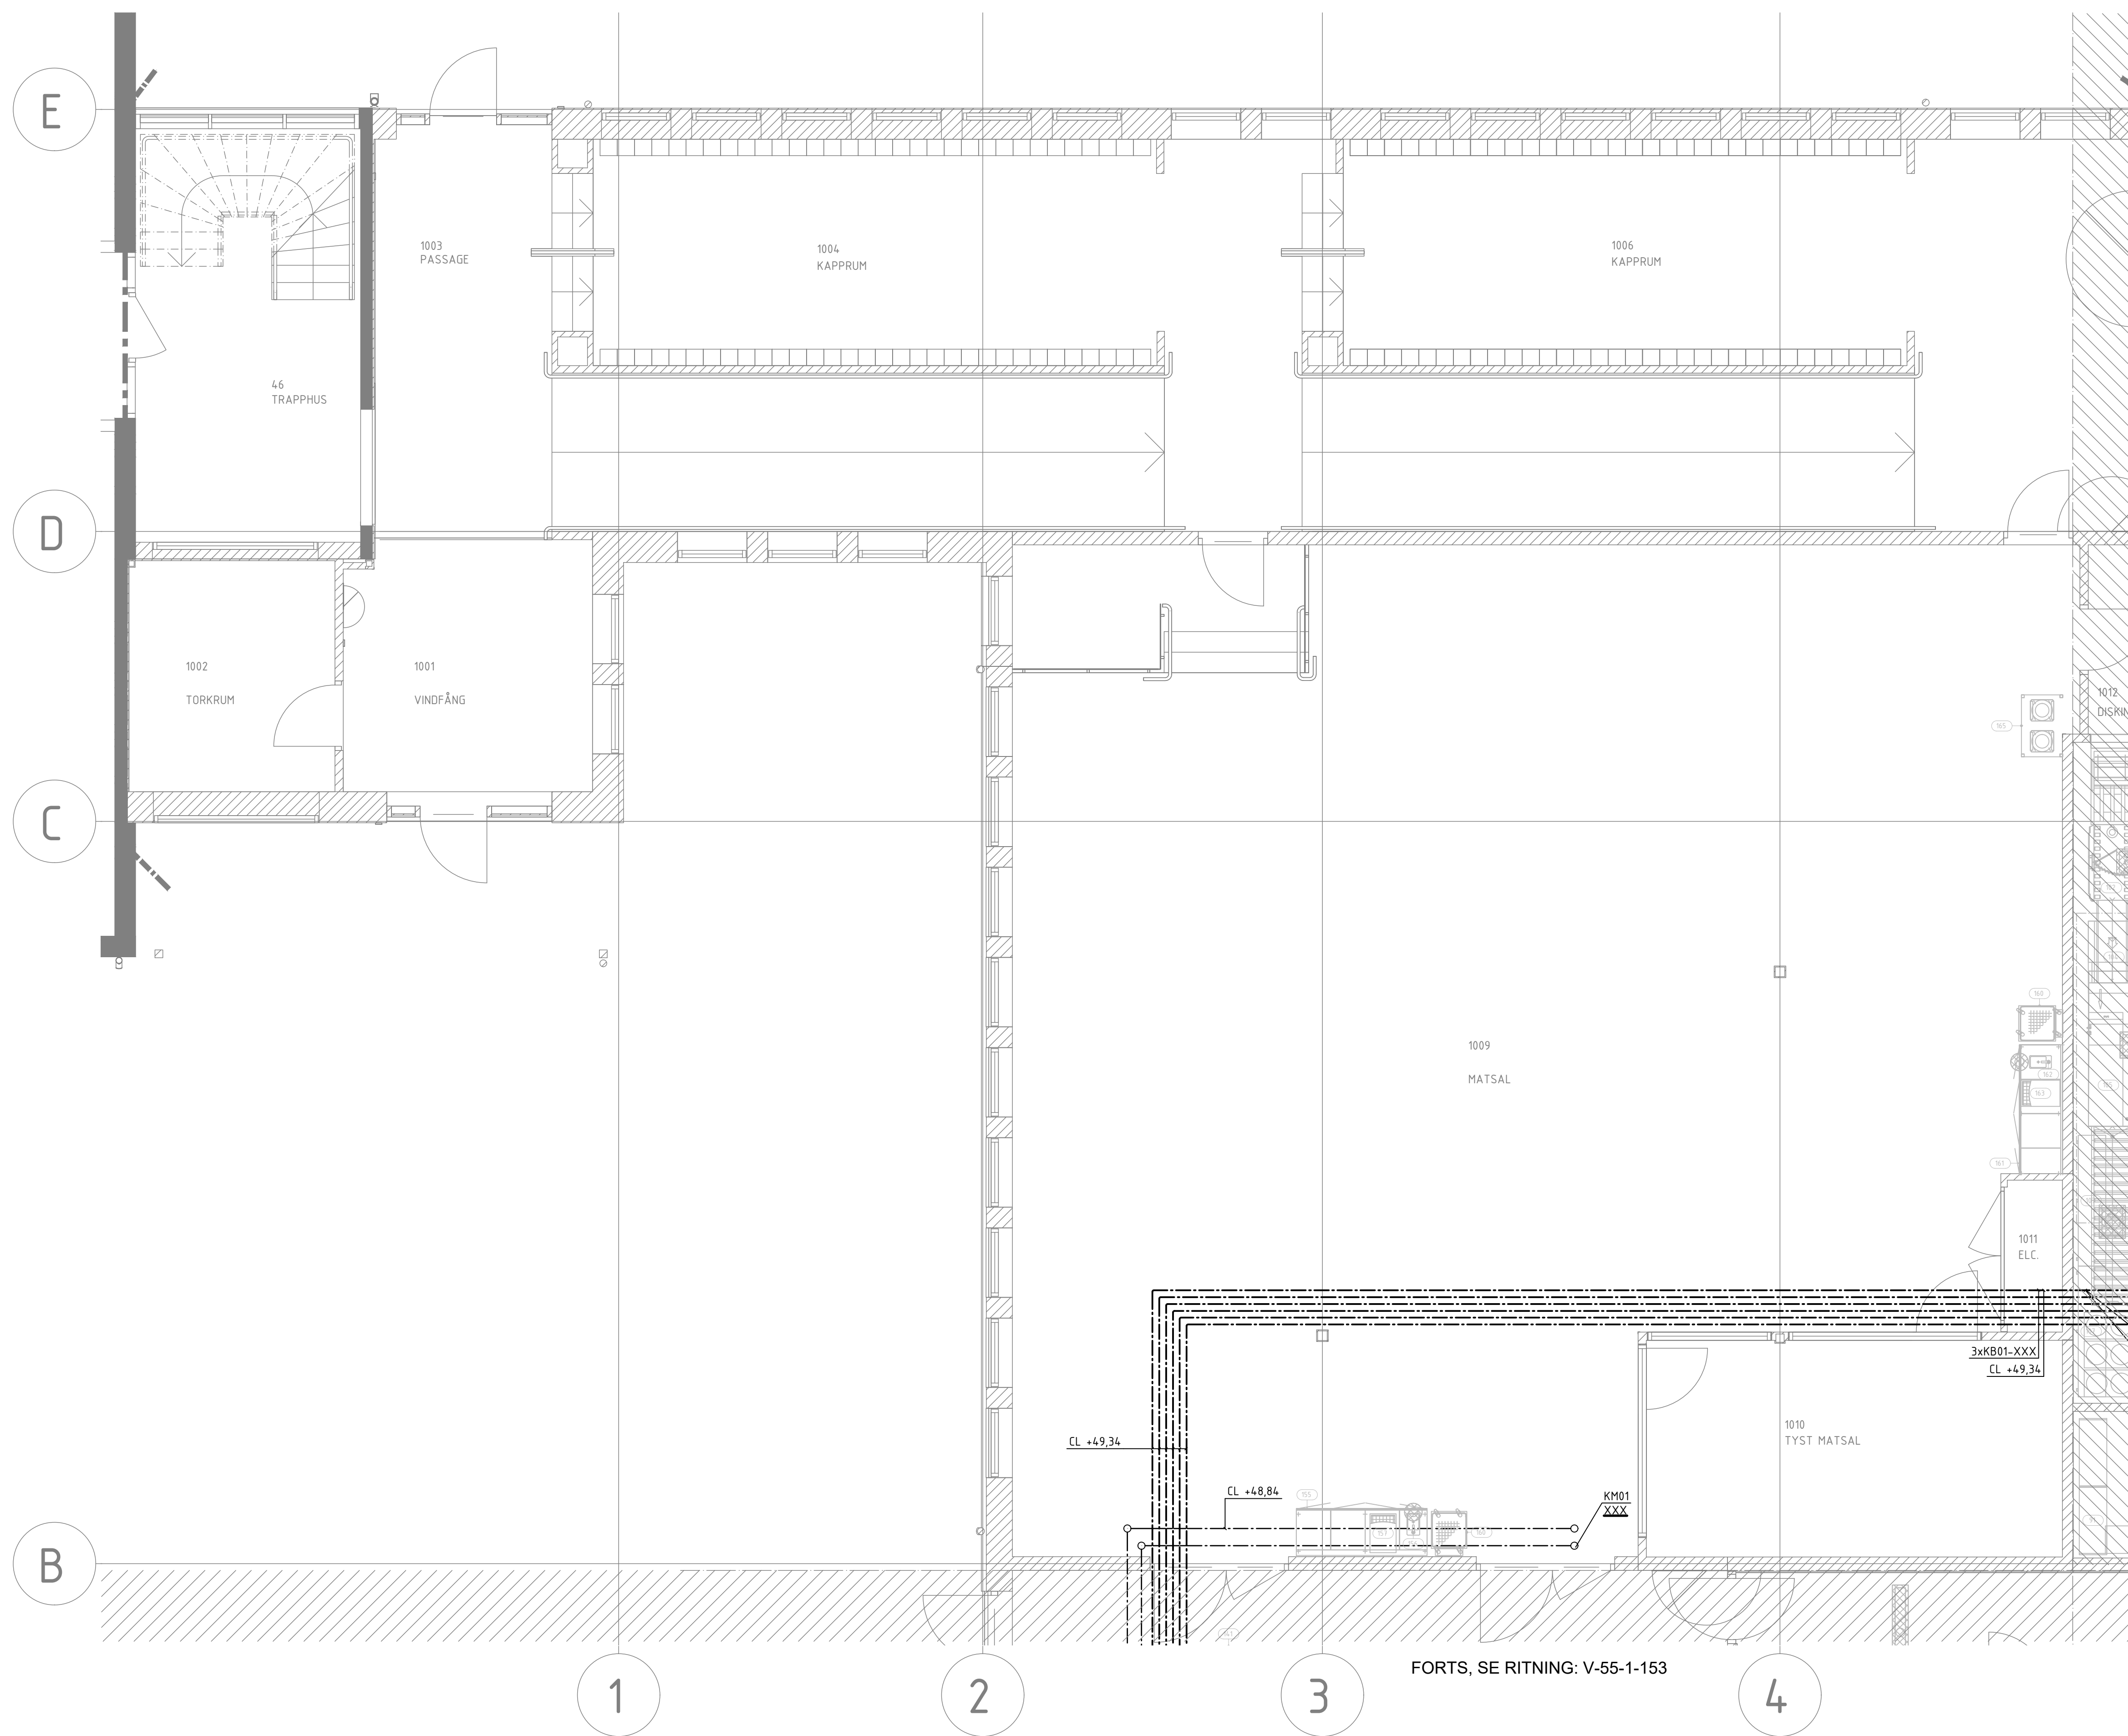

FORTS SE RITNING: V-55-1-152

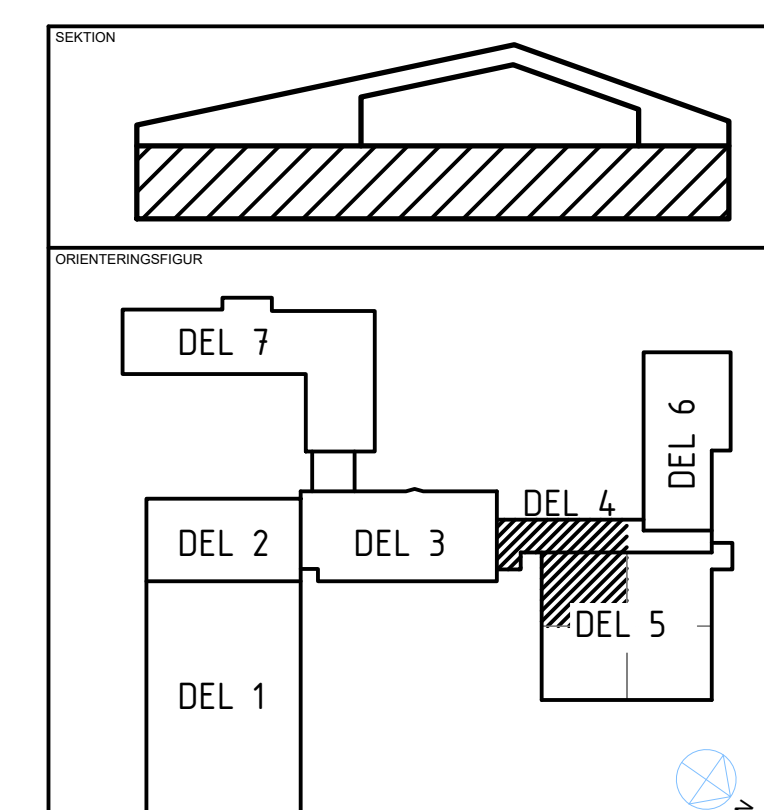

STATUS FÖRFRÅGNINGSUNDERLAG

PORT RÄGNINGSÖNDE	
HANDLING	BYGGHANDLING

DATUM	GODKÄND AV	ÄNDRINGS
2024-12-20	T.BERGSTRÖM	

2024-12-20	T. BERGSTRÖM	
BESTÄLLARE		



PROJEKTNAMN

CENTRAALKÖK

OMRADE ROBERTSFORS KOMMUN

PROJEKTNUMMER	ADRESS
	YTTRE RINGVÄGEN 4

DIARIENUMMER	FASTIGHET FORDONET 1
--------------	-------------------------

DISCIPLIN	FÖRETAG
VS	NORCONSULT SVERIGE AB

UPPDRAKSNUMMER	SKAPAD AV
108 83 71	MAN

TELEFON	KONTAKTPERSON
010 141 80 00	JONAS JOHANSSON

BYGGNADSVÄRDE	PLUSHÖJD (RH 2000) +45,54 (FG)
---------------	-----------------------------------

VÄNINGSPLAN	VÄNINGSDEL	DELOMRÅDE
1		DEL 4.1

55 KYLINSTALLATIONER

PLAN 1 - DEL 4.1, 5.1

PLAN 1 - DEL 4.1, 5.1
RITNINGSKATEGORI
PLAN

PLAN
DOKUMENTNUMMER
V-55-1-151

FILNAMN:

FORTS, SE RITNING: V-55-1-153