


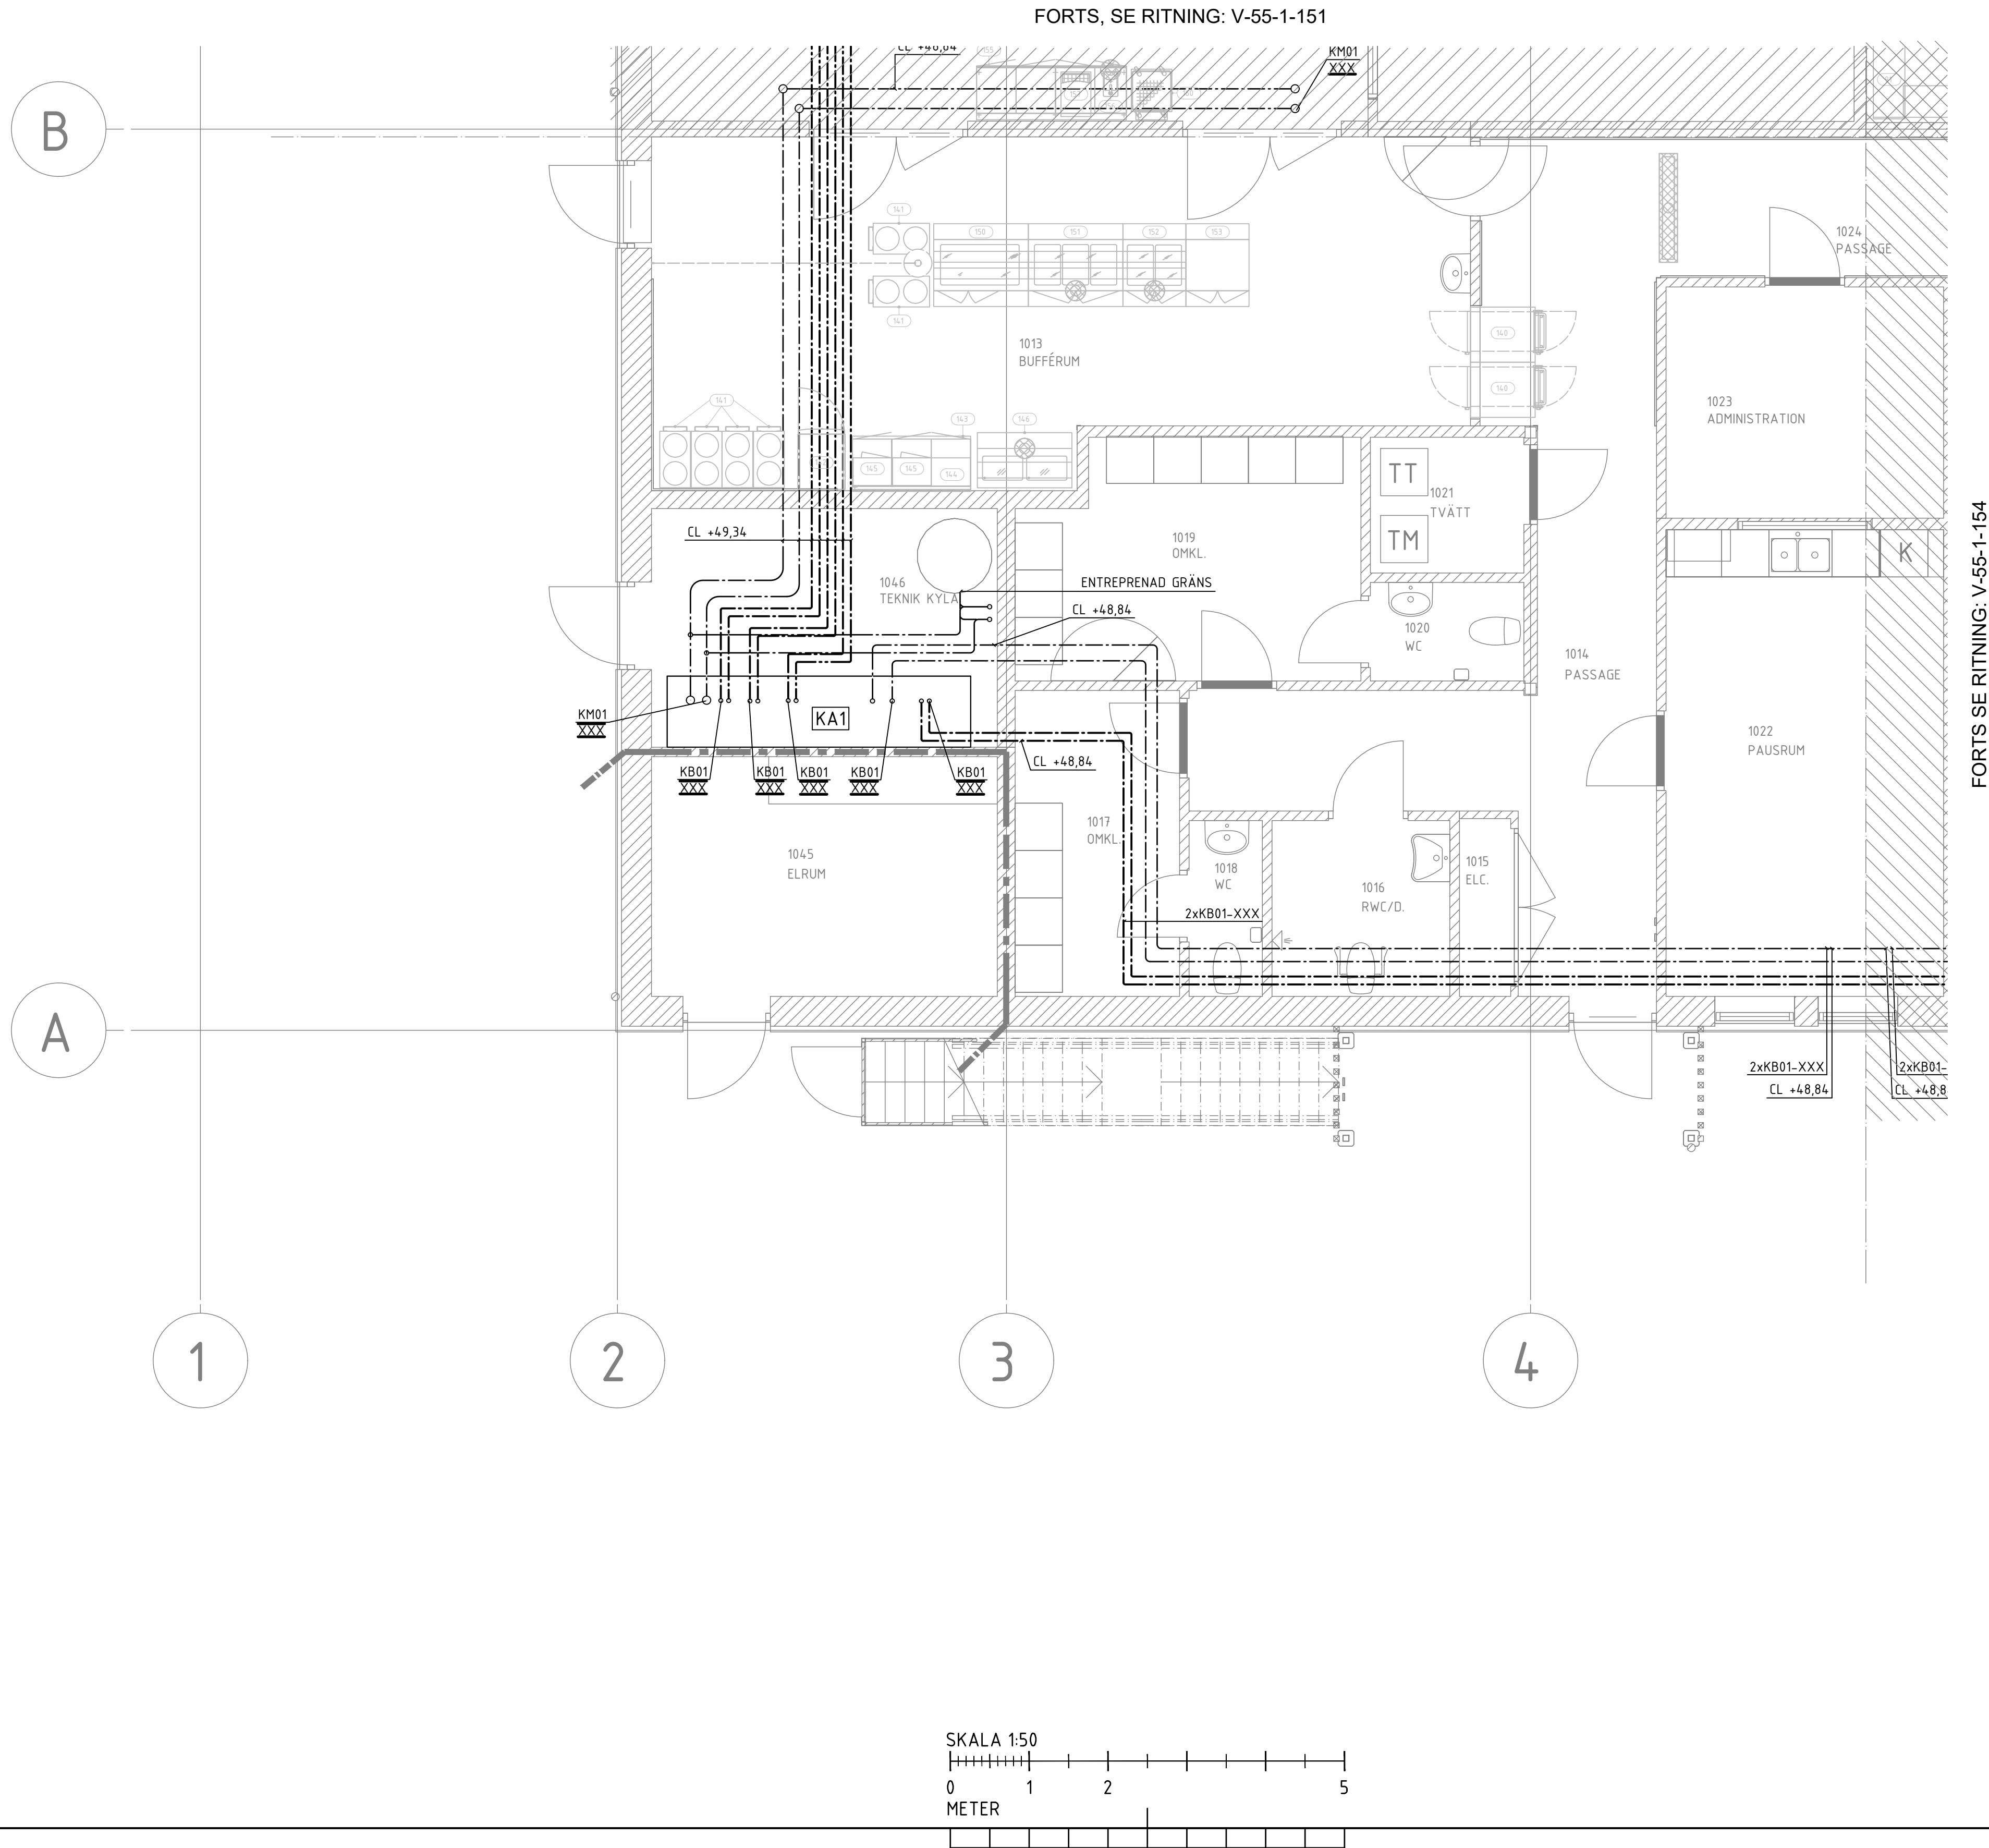

SEKTION

ORIENTERINGSPÅR

STATUS

FÖRFRÅGNINGSUNDERLAG

HANDLING

BYGGHANDLING

DATUM

2024-12-20

ODOKAND AV

T.BERGSTRÖM

ANDRINGS PM

BESTÄLLARE

ROBERTSFORS KOMMUN

PROJEKTNAMN

CENTRALKÖK

OMRADE

ROBERTSFORS KOMMUN

PROJEKTNUMMER

FÖRRETT

YTIRE RINGVÄGEN 4

DARIENUMMER

FASTIGHET

FORDONET 1

DISCIPLIN

VS

FÖRETAG

NORCONSULT SVERIGE AB

OPPFÖRINGSNUMMER

108 83 71

SKAPAD AV

MAN

TELEFON

010 141 80 00

KONTAKTPERSON

JONAS JOHANSSON

BYGGNADSVÄRDE

(KLIMATKORRIGERT 2006)

+45,54 (FG)

VÄNINGSPLAN

1

VÄNINGSDEL

DELOMRÅDE

DEL 5.3

SYSTEM

55 KYLINSTALLATIONER

BESKRIVNING

PLAN 1 - DEL 5.3

RITNINGSKATEGORI

PLAN

SKALA

1:50

FORMAT

A1

DOKUMENTNUMMER

V-55-1-153

ANDRNING