
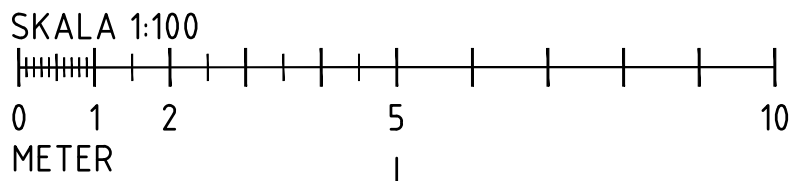


FÖRKLARINGSTEXT
SE RITNING V-50-0-001

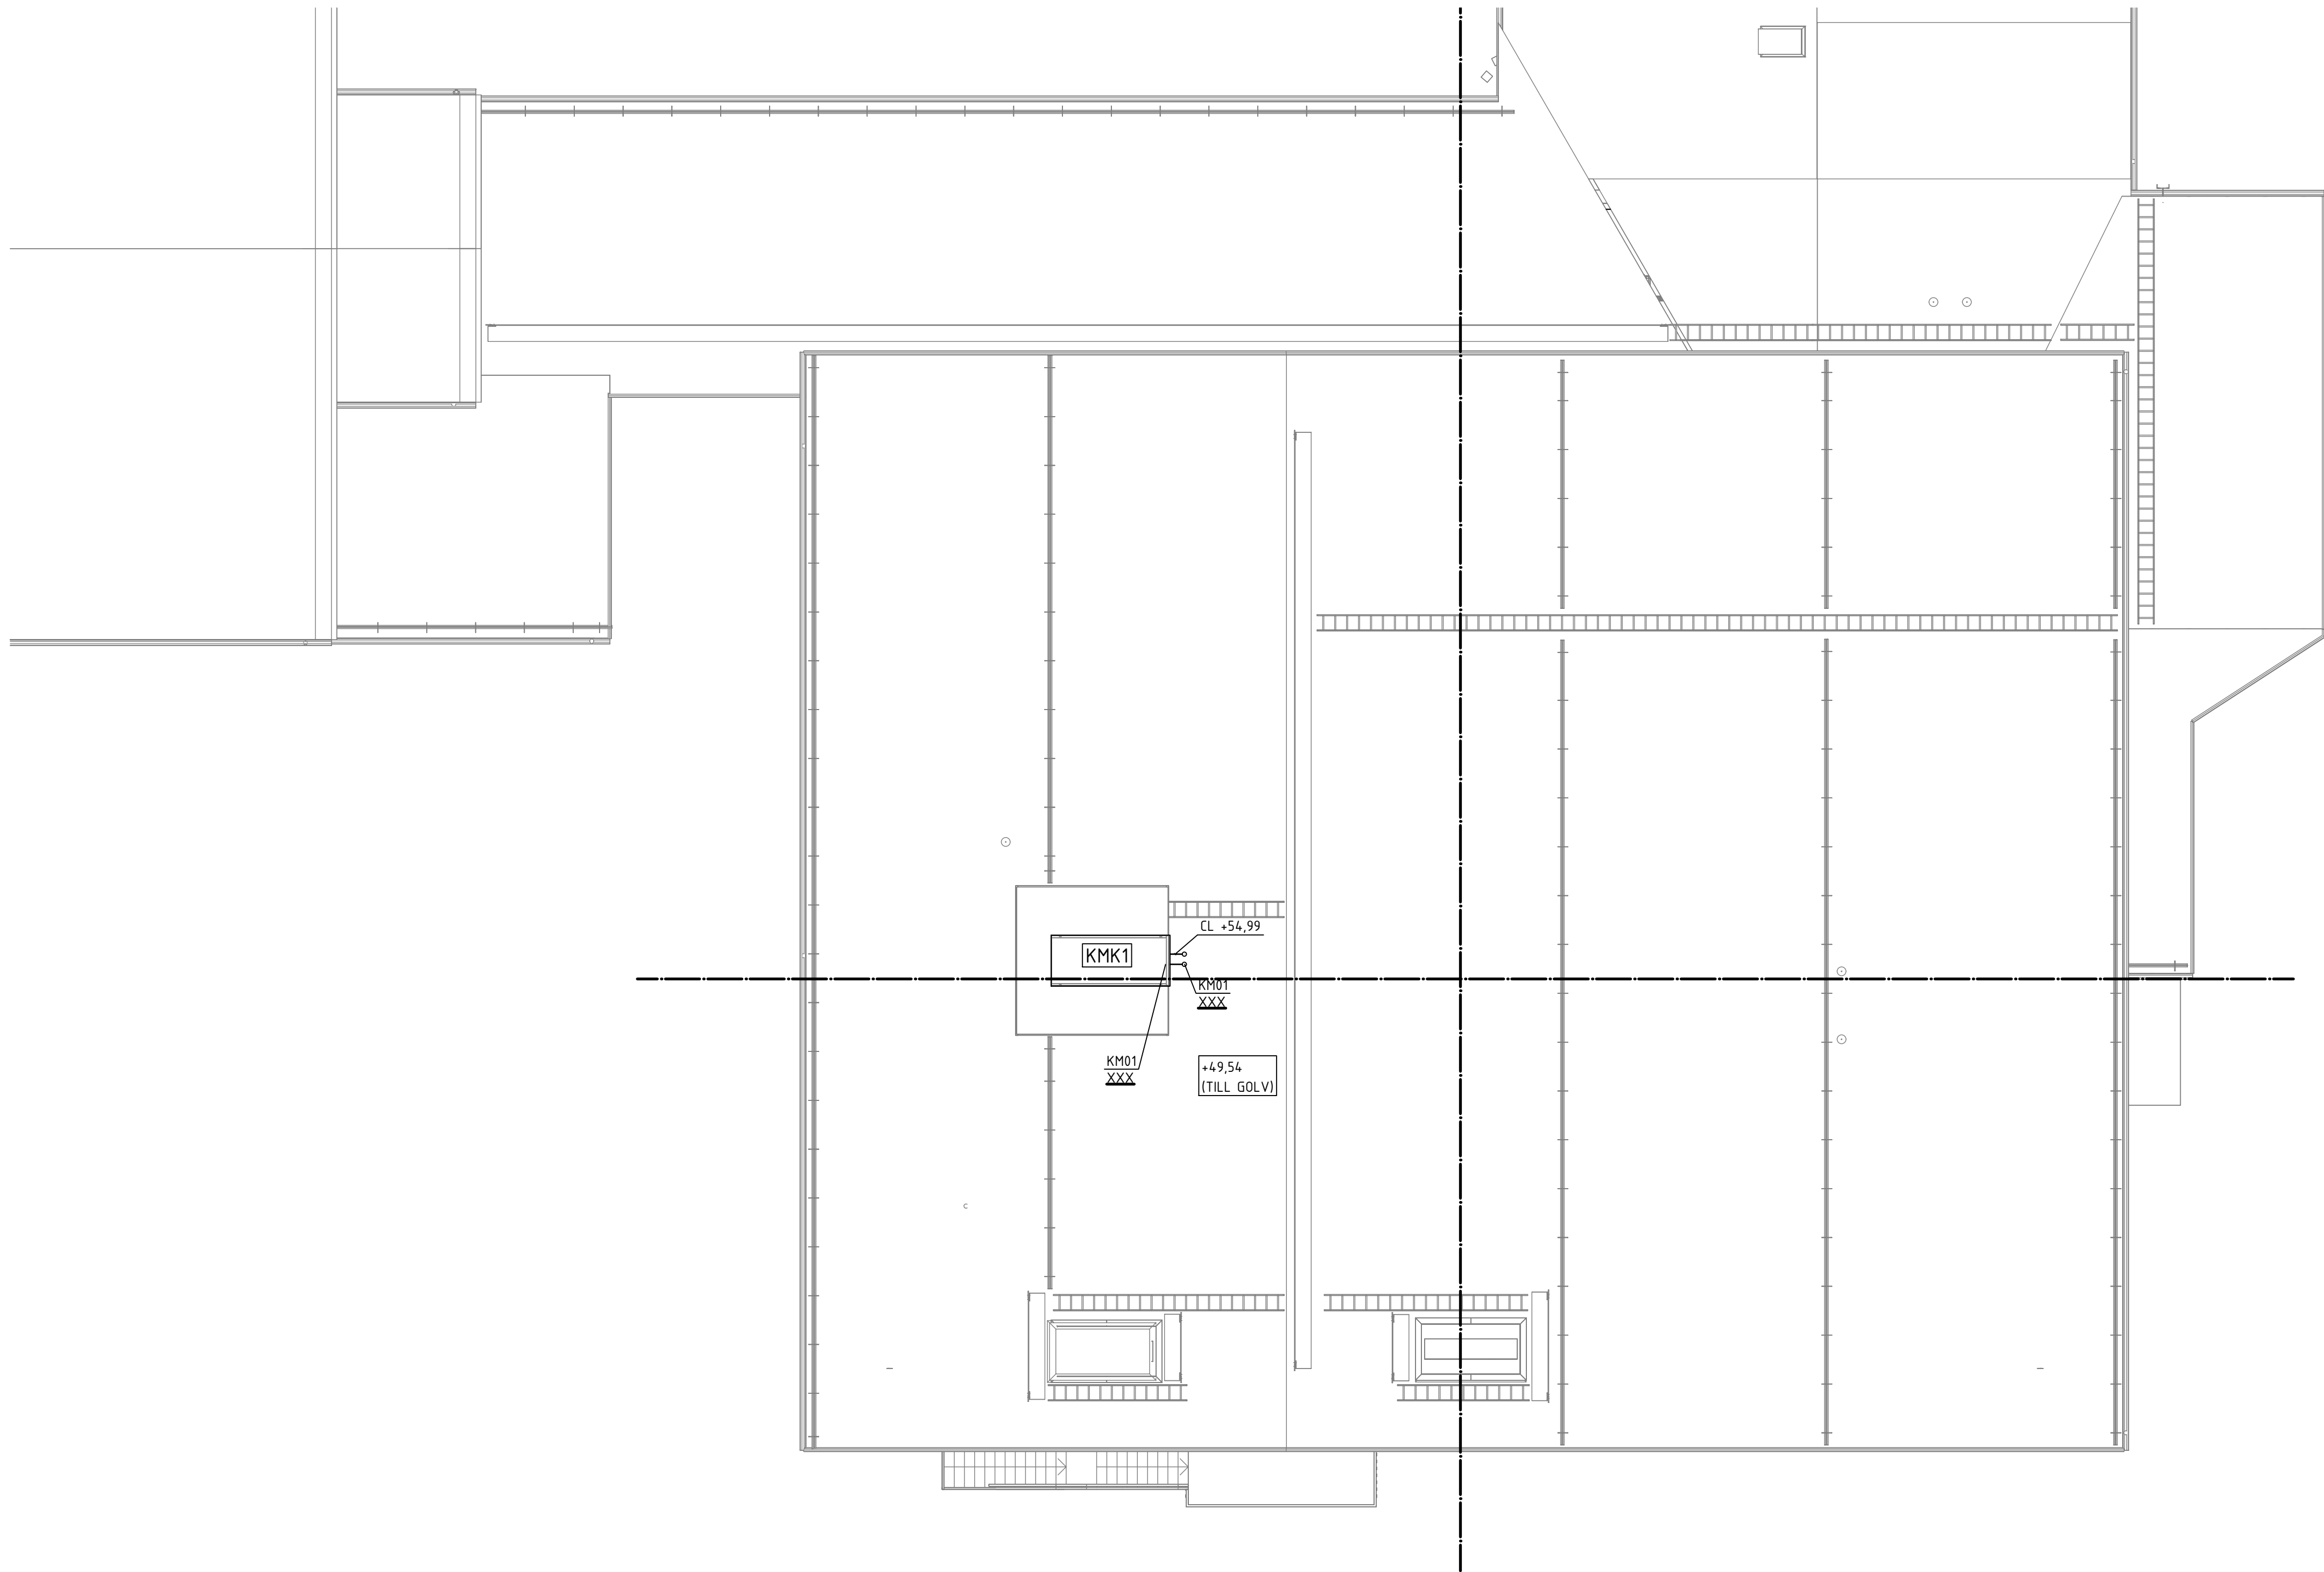

SEKTION

ORIENTERINGSPOL

STATUS

FÖRFRÅGNINGSUNDERLAG

HANDLING

BYGGHANDLING

DATUM

2024-12-20

GODKÄND AV

T.BERGSTRÖM

ANDRINGS PM

BESTÄLLARE

ROBERTSFORS KOMMUN

PROJEKTNAMN

CENTRALKÖK

OMRADE

ROBERTSFORS KOMMUN

PROJEKTNUMMER

108 83 71

DISCIPLIN

VS

DIARIENUMMER

YTTRE RINGVÄGEN 4

DISCIPLIN

NORCONSULT SVERIGE AB

OPPFÖRINGSNUMMER

MAN

TELEFON

010 141 80 00

JONAS JOHANSSON

BYGGNADSVÄRK

+49,54 (FG)

YANINGSPLAN

3

YANINGSDEL

DEL 4, 5

SYSTEM

55 KYLINSTALLATIONER

PLAN 3 - ÖVERSIKT

SKALA

1:100

FORMAT

A1

DOKUMENTNUMMER

V-55-1-301