
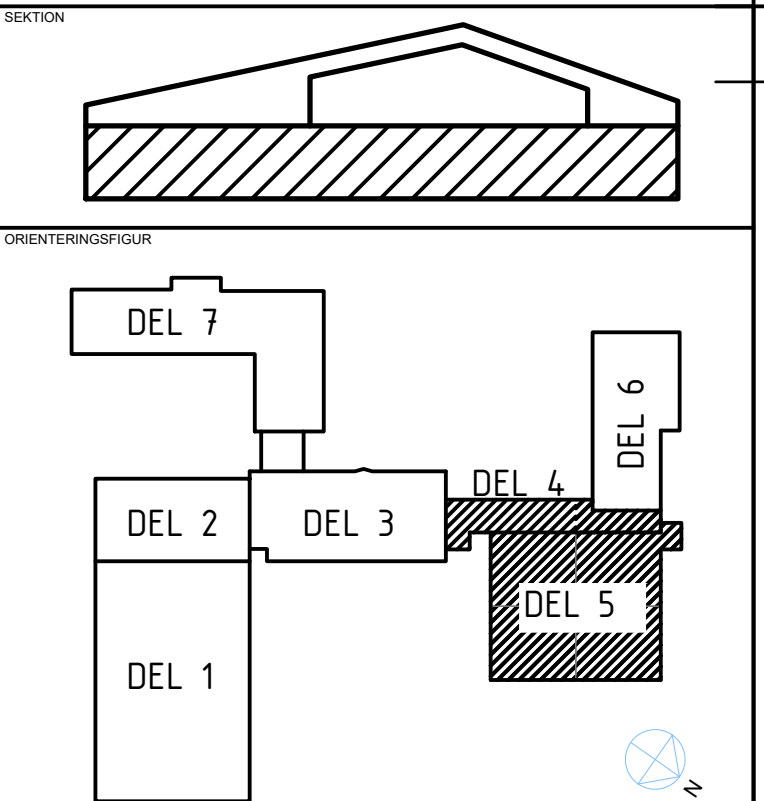


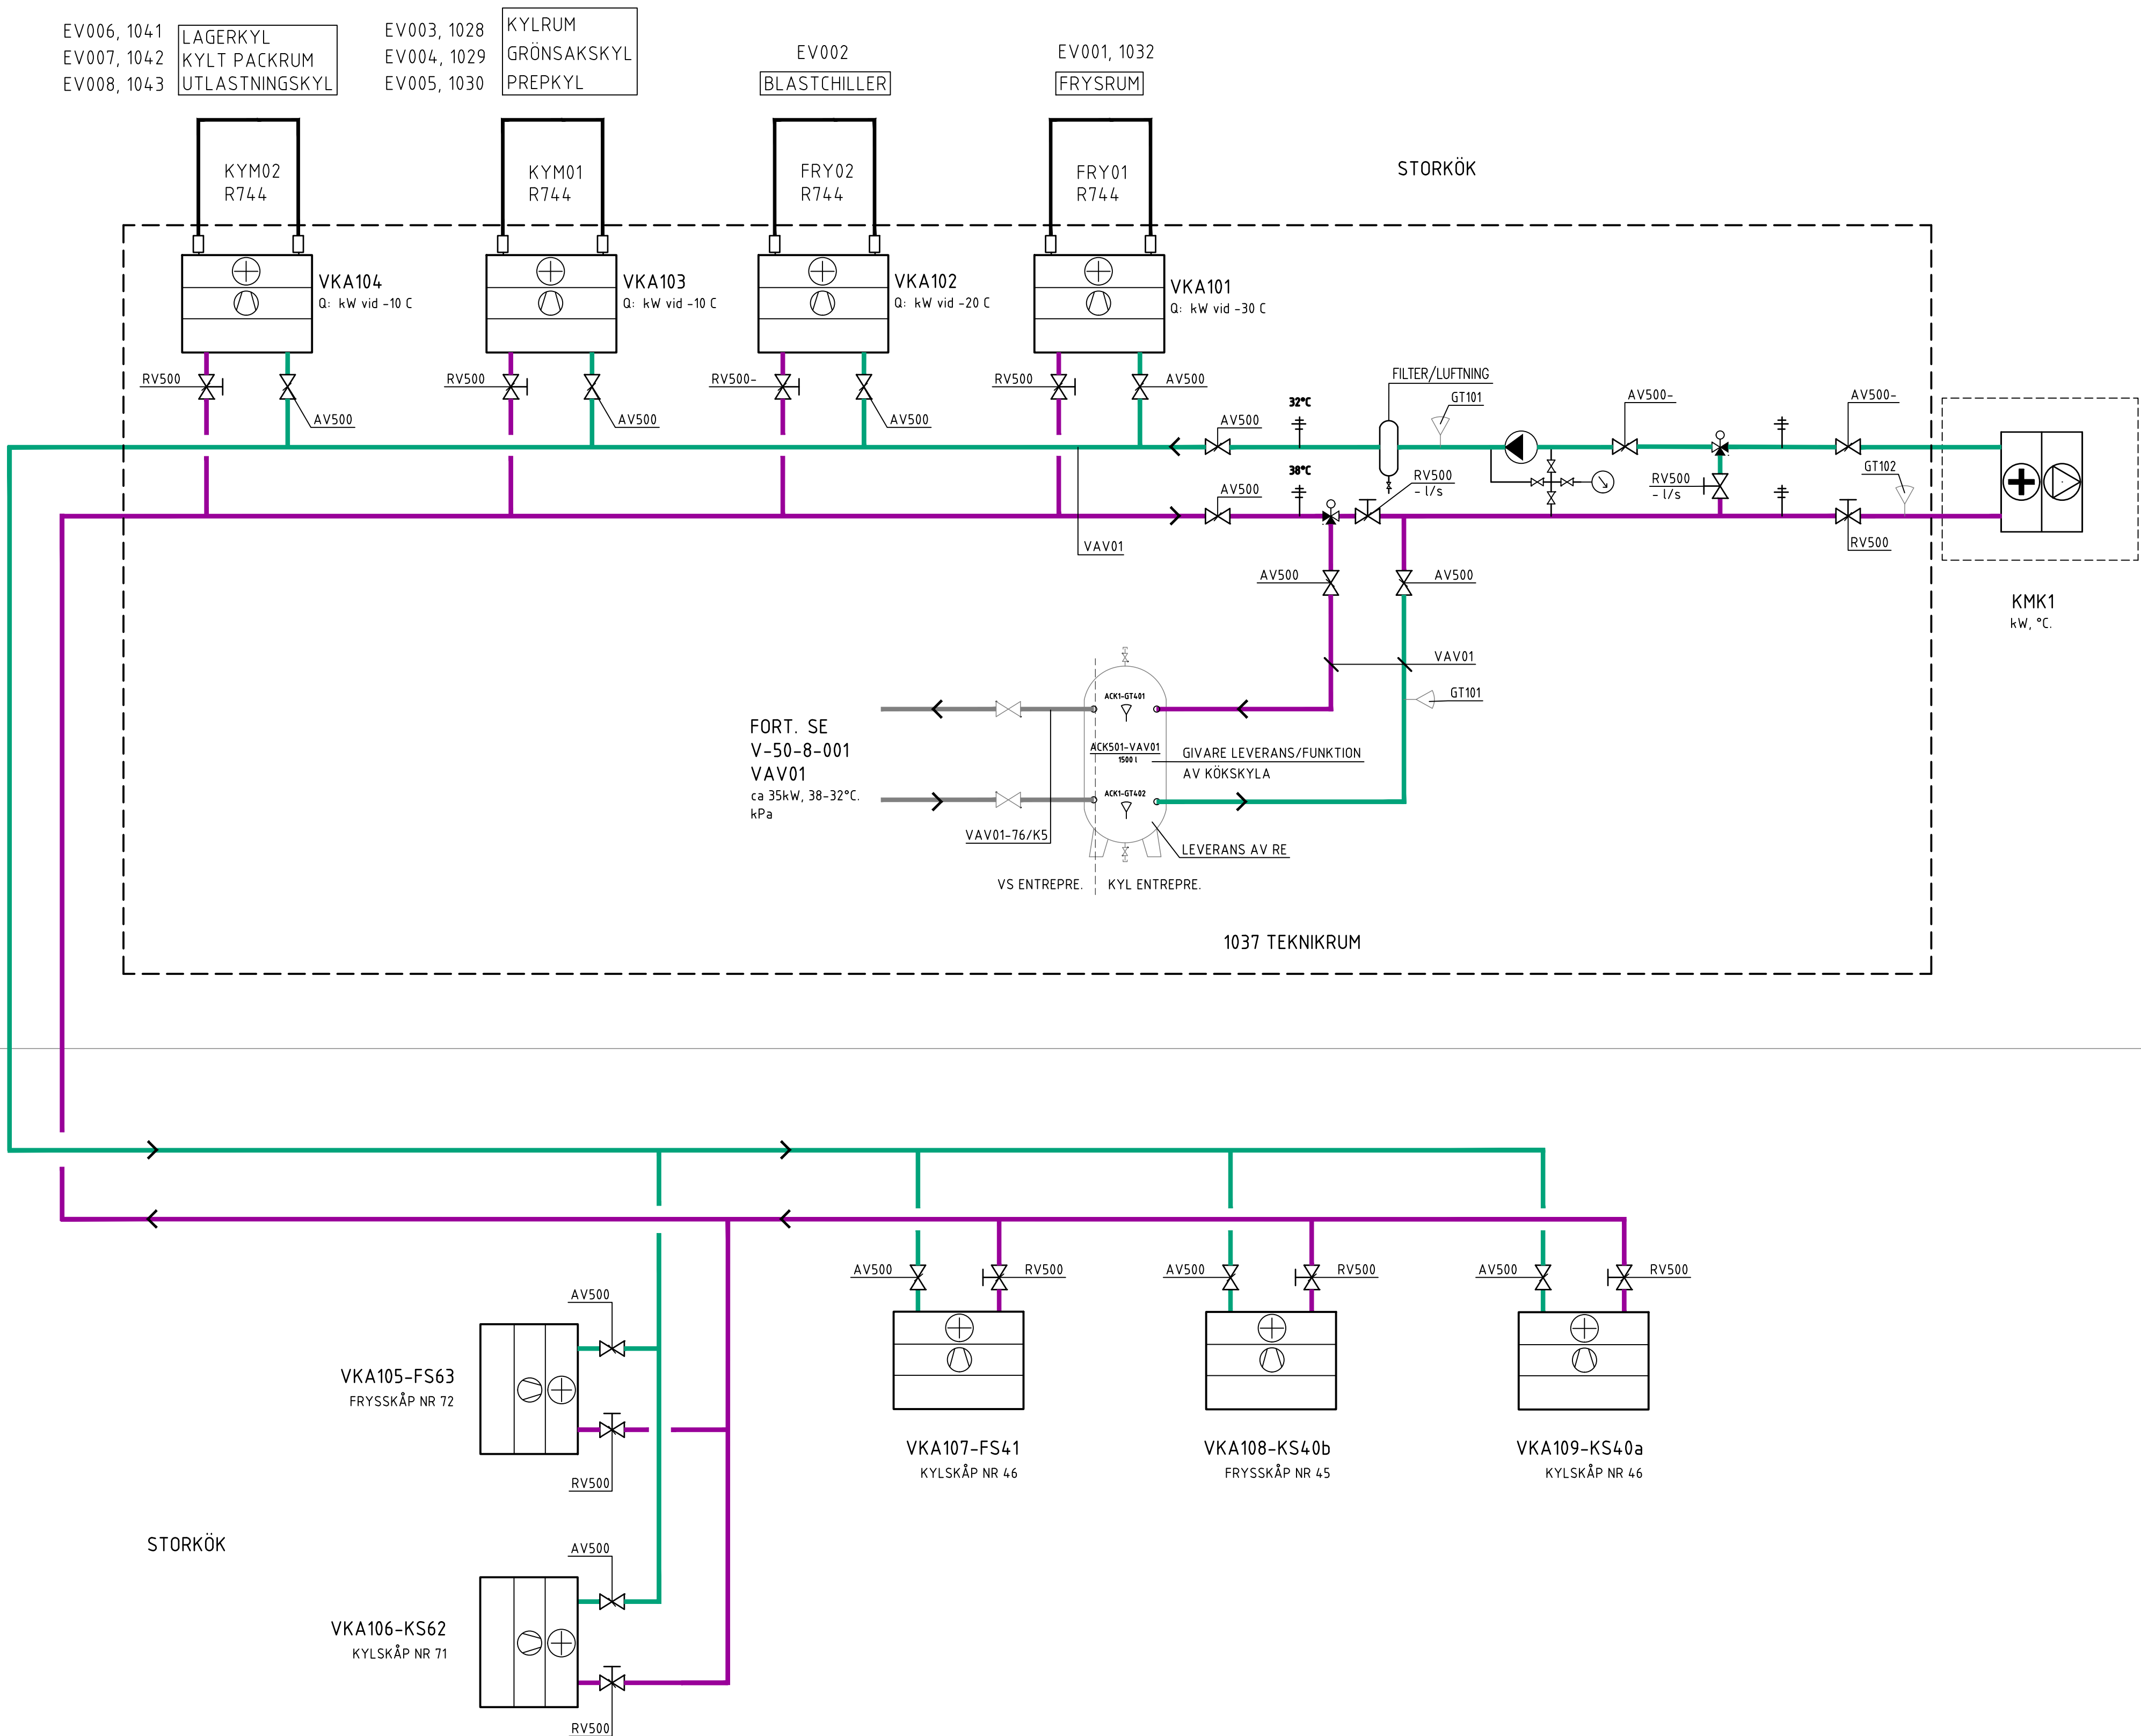

SEKTION		
ORIENTERINGSPÅR		
STATUS		
FÖRFRÅGNINGSUNDERLAG		
HANDLING		
BYGGHANDLING		
DATUM	GODKÄND AV	ÄNDRINGS PM
2024-12-20	T.BERGSTRÖM	
BESTÄLLARE		
ROBERTSFORS KOMMUN		
PROJEKTNAMN		
CENTRALKÖK		
OMRADE		
ROBERTSFORS KOMMUN		
PROJEKTNUMMER	FÖRRETT	
	YTIRE RINGVÄGEN 4	
DARIENUMMER	FASTIGHET	
	FORDONET 1	
DISCIPLIN	FÖRETAG	
VS	NORCONSULT SVERIGE AB	
ÖPPNINGSNUMMER	SKAPAD AV	
108 83 71	MAN	
TELEFON	KONTAKTPERSON	
010 141 80 00	JONAS JOHANSSON	
BYGGNADSVÄRDE	(KLIMATID 2000)	
	+49.54 (FG)	
VÄNINGSPLAN	VÄNINGSDEL	DELOMRÅDE
1		DEL 4, 5
SYSTEM		
55 KYLINSTALLATIONER		
BESKRIVNING		
FLÖDESSHEMA		
RITNINGSKATEGORI	SKALA	FORMAT
SCHEMA		A1
DOKUMENTNUMMER	ÄNDRING	
V-50-8-002		