


FÖRKLARINGSTEXT
SE RITNING V-50-0-001

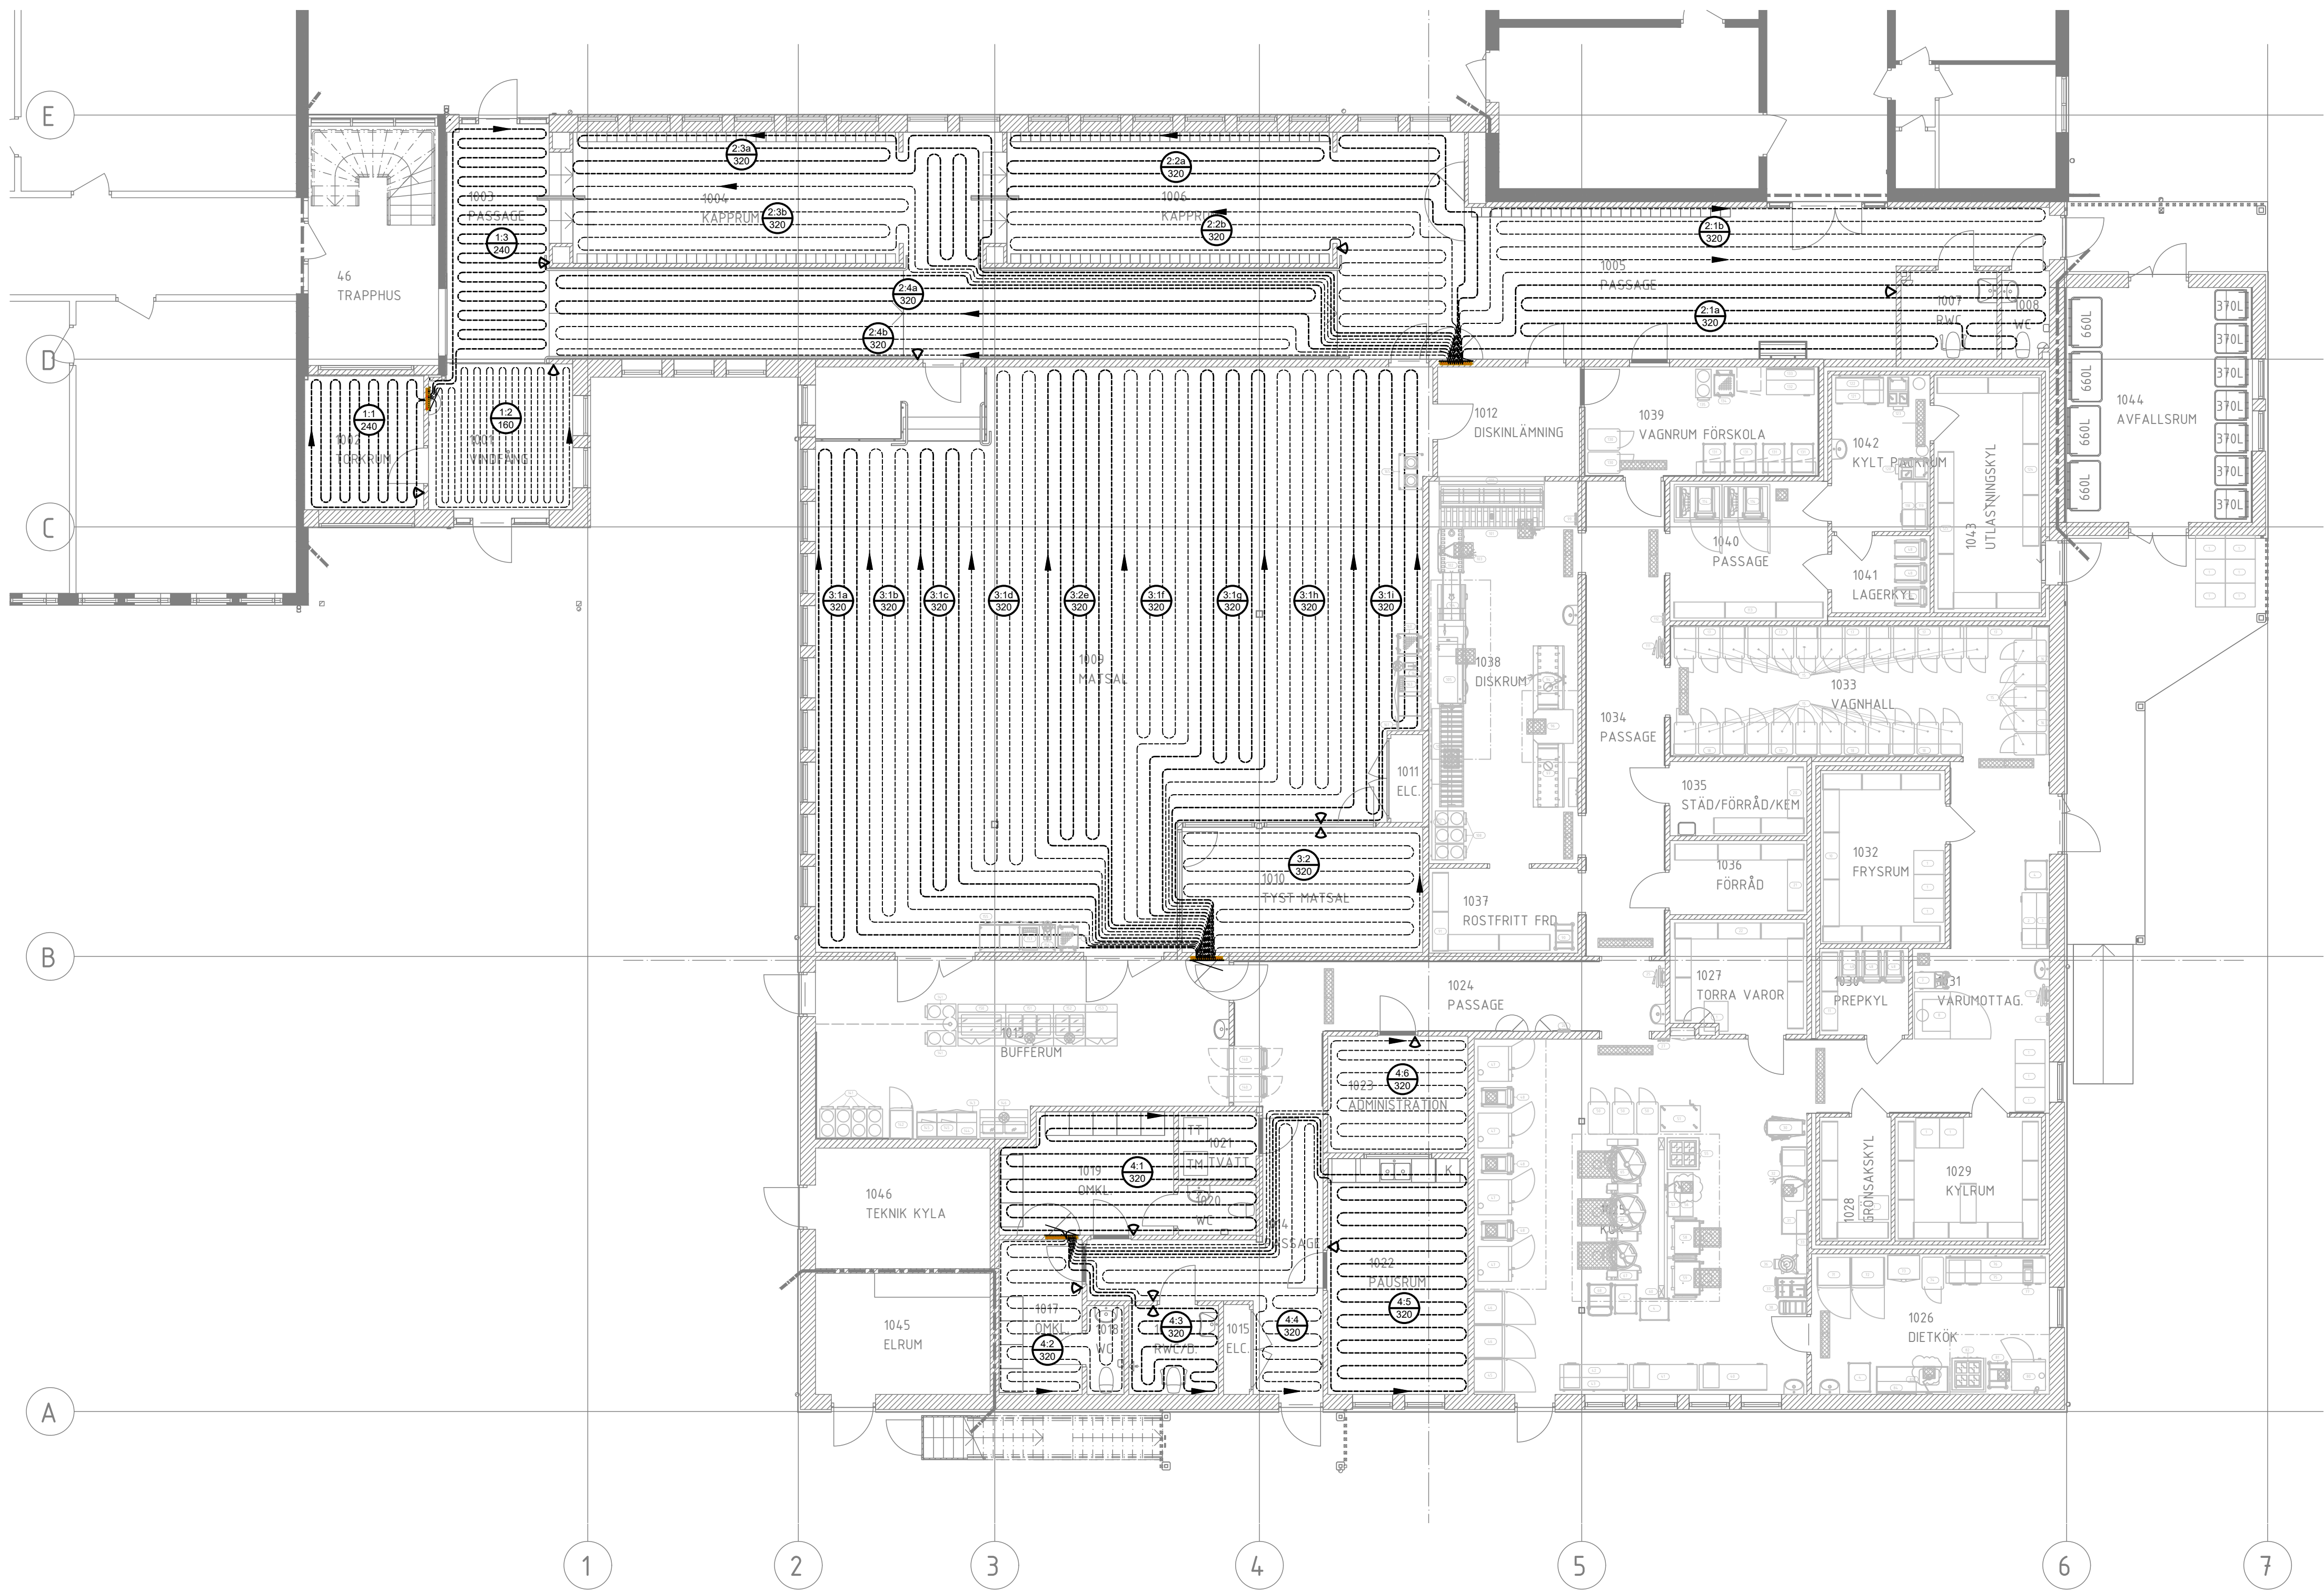

LK Projekt Nr:	LK044871			
Fördelare:	1			
Systemtemp.:	39,0/ 32,0 °C			
Flöde:	266 l/h / 4,4 l/min			
Max tryckfall:	13,3 kPa			
Krets	System	c/c	Längd(m)	Inj. värde VKF RF
1:1	L16	240	42,6	0,50
1:1	L16	240	66,0	0,75
1:3	L16	160	79,5	4,50

LK Projekt Nr:

LK044871

Fördelare:

2

Systemtemp.:

39,0/ 32,0 °C

Flöde:

694 l/h / 11,6 l/min

Max tryckfall:

11,7 kPa

Krets	System	c/c	Längd(m)	Inj.värde VKF RF
2.1a	L16	320	83,3	2,75
2.1b	L16	320	91,3	4,50
2.2a	L16	320	77,4	0,75
2.2b	L16	320	65,7	0,50
2.3a	L16	320	87,1	0,50
2.3b	L16	320	88,3	0,50
2.4a	L16	320	87,1	1,25
2.4b	L16	320	83,4	1,00

LK Projekt Nr:

LK044871

Fördelare:

3

Systemtemp.:

39,0/ 32,0 °C

Flöde:


817 l/h / 13,6 l/min

Max tryckfall:

9,0 kPa

Krets	System	c/c	Längd(m)	Inj. värde VKF RF
3.1	L16	320	60,5	0,50
3.1a	L16	320	68,5	0,75
3.1b	L16	320	65,1	0,50
3.1c	L16	320	61,4	0,50
3.1d	L16	320	85,8	4,50
3.1e	L16	320	84,5	4,00
3.1f	L16	320	72,3	1,00
3.1g	L16	320	76,0	1,50
3.1h	L16	320	82,0	2,25
3.1i	L16	320	83,3	3,00

LK Projekt Nr:	LK044871			
Fördelare:	4			
Systemtemp.:	39,0/ 32,0 °C			
Flöde:	240 l/h / 4,0 l/min			
Max tryckfall:	5,9 kPa			
Krets	System	c/c	Längd(m)	Inj. värde VKF RF
4.1	L16	320	66,9	0,50
4.2	L16	320	39,8	0,50
4.3	L16	320	26,6	0,50
4.4	L16	320	54,1	0,75
4.5	L16	320	90,3	4,50
4.6	L16	320	57,5	0,50

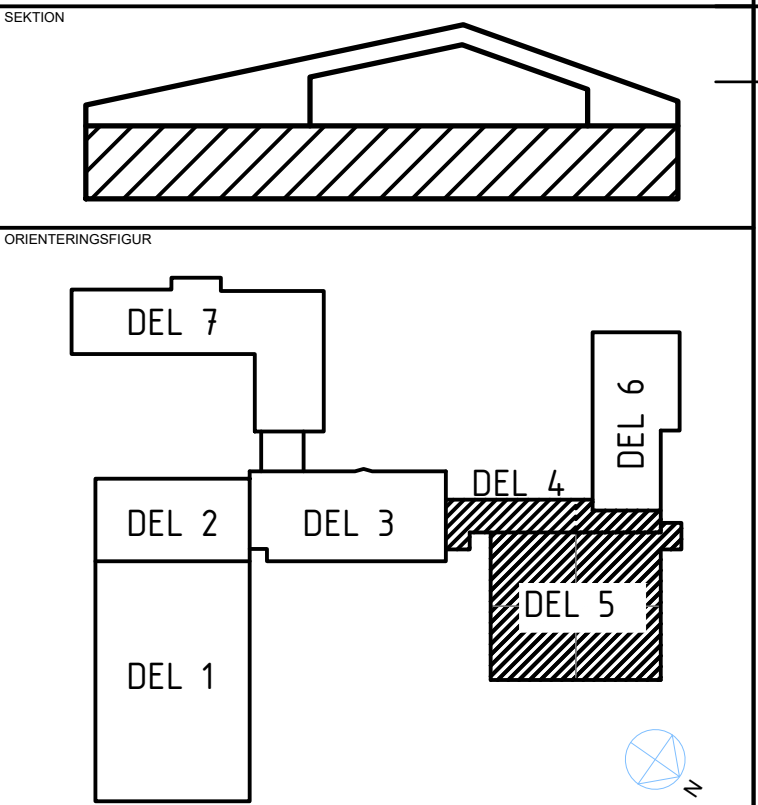

STATUS		
FÖRFRÅGNINGSUNDERLAG		
HANDLING		
BYGGHANDLING		
DATUM	GODKÄND AV	ÄNDRINGS PM
2024-12-20	T.BERGSTRÖM	
BESTÄLLARE		
 ROBERTSFORS KOMMUN		
PROJEKTNAMN		
CENTRAALKÖK		
OMRADE		
ROBERTSFORS KOMMUN		
PROJEKTNUMMER	FÖRETAG	
	YTTRE RINGVÄGEN 4	
DARIENUMMER	FASTIGHET	
	FÖRÖNET 1	
DISCIPLIN	FÖRETAG	
VS	NORCONSULT SVERIGE AB	
OPPRORINGSNUMMER	SKAPAD AV	
108 83 71	MAN	
TELEFON	KONTAKTPERSON	
010 141 80 00	JONAS JOHANSSON	
BYGGNADSVÄRDE	(KLUBBID RPH 2001)	
	+44,60, +45,07, +45,54 (FG)	
VÄNINGSPLAN	VÄNINGSDEL	DELOMRADE
1		DEL 4, 5
SYSTEM		
56 VÄRMEINSTALLATIONER		
RITNINGSKATEGORI		
PLAN 1 - ÖVERSIKT, UNDER PLATTA		
RITNINGSKATEGORI	SKALA	FORMAT
PLAN	1:100	A1
DOKUMENTNUMMER	ÄNDRING	
V-56-1-001		

