


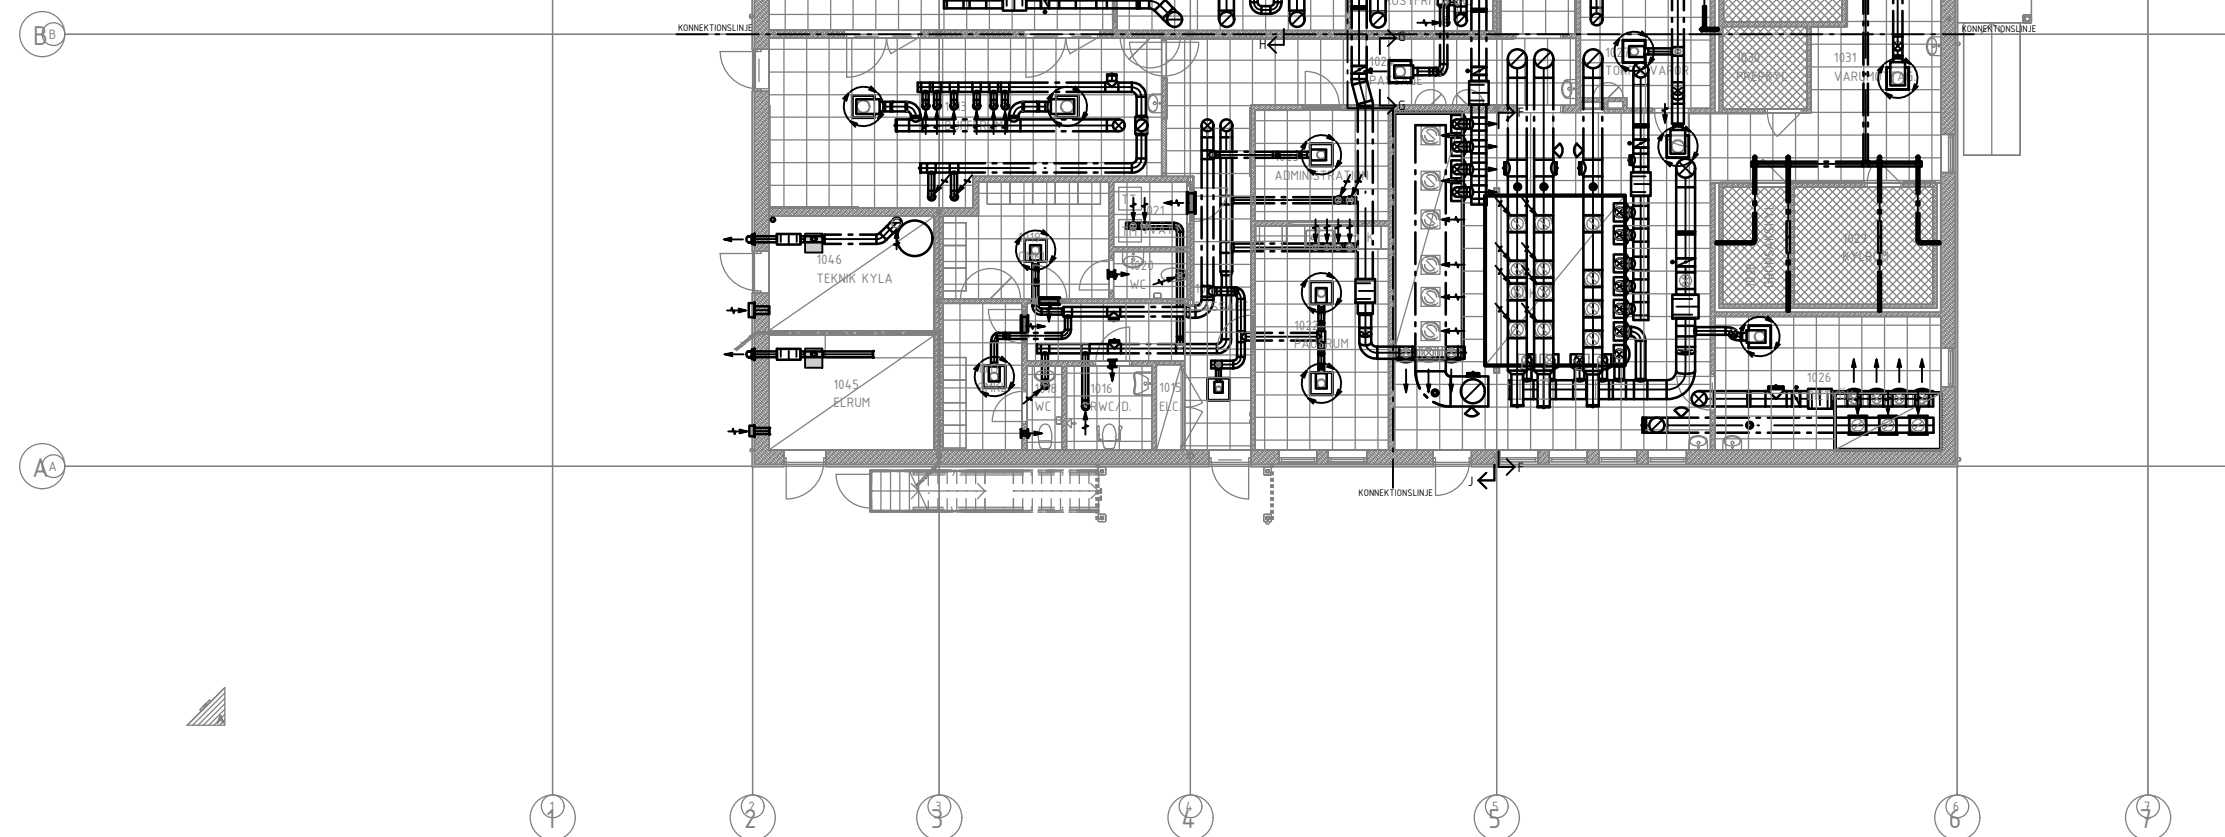

SAMMANSTÄLLNING AV TOTALA LUFTFLÖDEN  
FÖR REDOVISNING AV GRUND-, OCH FORCERINGSFLÖDEN,  
SE FLÖDESSCHEMA: V-57-8-501

|                                                                                                 |                                                                                |   |                                                                                              |
|-------------------------------------------------------------------------------------------------|--------------------------------------------------------------------------------|---|----------------------------------------------------------------------------------------------|
| <b>1001 VINDFÅNG</b><br>TD201-125-600+Alsd 100-125<br>20/-                                      | <b>1002 TYST MATSAL</b><br>TD201-250-600+Alsd 200-250<br>3xFD101-160<br>80/80  | <b>1003 TVÄTT</b><br>2xFD101 Ø160<br>-65                                                                        | <b>1003 VAGNHALL</b><br>2xFD101 Ø160<br>-50                                                  |
| <b>1002 TORKRUM</b><br>TD201-125-600+Alsd 100-125<br>25/-                                       | <b>1012 DISKINLÄMMNING</b><br>TD201-200-600 +Alsd 160-200<br>50/-              | <b>1022 PAUSRUM</b><br>2xTD201-200-600+Alsd 160-200<br>4xFD101-160<br>100/100                                   | <b>1034 PASSAGE</b><br>2xTD201-250-600+Alsd 200-250<br>170/-                                 |
| <b>1003 PASSAGE</b><br>TD201-125-600+Alsd 100-125<br>25/-                                       | <b>1013 BUFFÉRUM</b><br>2xTD201-315-600+Alsd 250-315<br>8xFD101-160<br>215/215 | <b>1023 ADMINISTRATION</b><br>1xTD201-200-600+Alsd 160-200<br>2xFD101-160<br>40/40                              | <b>1035 STÅD/FÖRRÅD/KEM</b><br>FD101-160<br>-/25                                             |
| <b>1004 KAPPRUM</b><br>2xTD201-200-600+Alsd 200-120/-                                           | <b>1014 PASSAGE</b><br>TD201-125-600 +Alsd 100-125<br>20/-                     | <b>1024 PASSAGE</b><br>TD201-250-600 +Alsd 200-250<br>80/-                                                      | <b>1036 FÖRRÅD</b><br>FD101-160<br>-/25                                                      |
| <b>1005 PASSAGE</b><br>1xTD201-125-600+Alsd 100-125<br>2xFD301-315<br>20/260                    | <b>1016 RWC/DUSCH</b><br>FD101 Ø160<br>-25                                     | <b>1025 KÖK</b><br>1xTD201-315-600+Alsd 250-315<br>140/-<br>IK2011 840/1200<br>IK2012 500/840<br>IK2013 650/750 | <b>1037 ROSTFRITT FÖRRÅD</b><br>FD101-160<br>-/25                                            |
| <b>1006 KAPPRUM</b><br>2xTD201-200-600+Alsd 160-200<br>120/-                                    | <b>1017 OMKLÄDNING</b><br>TD201-200-600 +Alsd 160-200<br>55/-                  | <b>1026 DIETKÖK</b><br>IK202<br>4xTD Ø250, 3xFD Ø315<br>430/480                                                 | <b>1038 DISKRUM</b><br>2xTD201-315-600+Alsd 250-315<br>200/-<br>IK401 390/450<br>IK402 -/250 |
| <b>1007 RWC</b><br>FD101-160<br>-/25                                                            | <b>1018 WC</b><br>FD101 Ø160<br>-25                                            | <b>1027 TORRA VAROR</b><br>TD201-200-600 +Alsd 160-200<br>50/-                                                  | <b>1039 VAGNRUM FÖRSKOLA</b><br>FD101 Ø160<br>-20                                            |
| <b>1008 WC</b><br>FD101-160<br>-/25                                                             | <b>1019 OMKLÄDNING</b><br>TD201-200-600 +Alsd 160-200<br>65/-                  | <b>1031 VARUMOTTAGNING</b><br>2xTD201-315-600+Alsd 250-315<br>280/-                                             | <b>1040 PASSAGE</b><br>TD201-200-600 +Alsd 160-200<br>50/-                                   |
| <b>1009 MATSAL</b><br>8xTD201-315-600+Alsd 250-315<br>4xFD201-400-600+Alsd 315-400<br>1020/1020 | <b>1020 WC</b><br>FD101 Ø160<br>-25                                            |   |                                                                                              |

FÖRKLARINGAR:

| ALLMÄNT                   |                         |
|---------------------------|-------------------------|
| LUFTMÄNGDER ANGIVNA I l/s |                         |
| A                         | AVLUFT                  |
| U                         | UTELUFT                 |
| F                         | FRÅNLUFT                |
| T                         | TILLUFT                 |
| LA                        | LUFTBEHANDLINGSAGGREGAT |
| KF                        | KANALFLÄKT              |
| INKL                      | INKLÄDNAD AV KANAL      |

T-rör, X-rör, böj, T-rör med extra påstick ska vara fabrikstillverkade produkter.


| KANALTYPEN |                                               |
|------------|-----------------------------------------------|
| 11         | FÖRZINKAD STÅLPLÅT, TÄTHET 0                  |
| 14         | KANALER AV STÅLPLÅT I<br>VÄTSKETÄT UTFÖRANDE, |

| TILLUFTSDON/FRÅNLUFTSDON          |
|-----------------------------------|
| TD201 TAKDON, TILLUFT             |
| TD801 TALLRIKSVENTIL, TILLUFTSDON |
| FD101 KONTROLLVENTIL              |
| FD201 INFÄLLT TAKDON, FRÅNLUFT    |
| FD301 TRÄDNÄTSGALLER, FRÅNLUFT    |
| FD401 TRÄDNÄTSGALLER, CIRKULÄRT   |
| IK201-1,-2,-3 IMKÅPA, KÖK         |
| IK202 IMKÅPA, DIET                |
| IK401 DISKKÅPA, TUNNELDISK        |
| IK402 DISKKÅPA, GROVDISK          |
| OD101/102 ÖVERLUFTSDON            |

| UTELUFTS/AVLUFTSGALLER/HUVAR |                                 |
|------------------------------|---------------------------------|
| AD101                        | AVLUFTSVÄGGALLER                |
| AD102                        | AVLUFTSVÄGGHUV                  |
| AD103                        | AVLUFTSVÄGGALLER                |
| AD201                        | AVLUFTSHUV TAKPLACERAD FÖR LA01 |
| UD101                        | UTELUFTSVÄGGALLER               |
| UD102                        | UTELUFTSVÄGGHUV                 |
| UD201                        | UTELUFTSHUV TAKPLACERAD         |

| ÖVRIGT |                                         |
|--------|-----------------------------------------|
| LD101  | LUDDÄMPARE, CIRKULÄR ANSLUTNING         |
| LD201  | REKTANGULÄR LUDDÄMPARE MED INV. BAFFLAR |
| LD202  | REKTANGULÄR LUDDÄMPARE MED INV. BAFFLAR |
| LD501  | FLEXIBEL KANAL LUDDÄMPARE               |
| RL101  | RENSLUCKA CIRKULÄR                      |
| RL102  | RENSLUCKA REKTANGULÄR                   |
| SP101  | VRIDSPJÄLL, MANUELLT                    |
| SP201  | INJUSTERINGSPJÄLL TYP IRIS              |
| SP401  | REKTANGULÄR SPJÄLL, MANUELLT            |
| SP701  | CIRKULÄR SPJÄLL MED HYLLO FÖR MOTOR     |
| SP702  | REKTANGULÄR SPJÄLL MED HYLLO FÖR MOTOR  |
| SP8XX  | SPJÄLL MED MOTOR                        |

| ISOLERING |                         |
|-----------|-------------------------|
| /K403     | KONDENSISOLERING 30mm   |
| /K405     | KONDENSISOLERING 50mm   |
| /K713     | CELLGUMMI, ULTIMA 13 MM |
| /V315     | VÄRMEISOLERING, 150mm   |

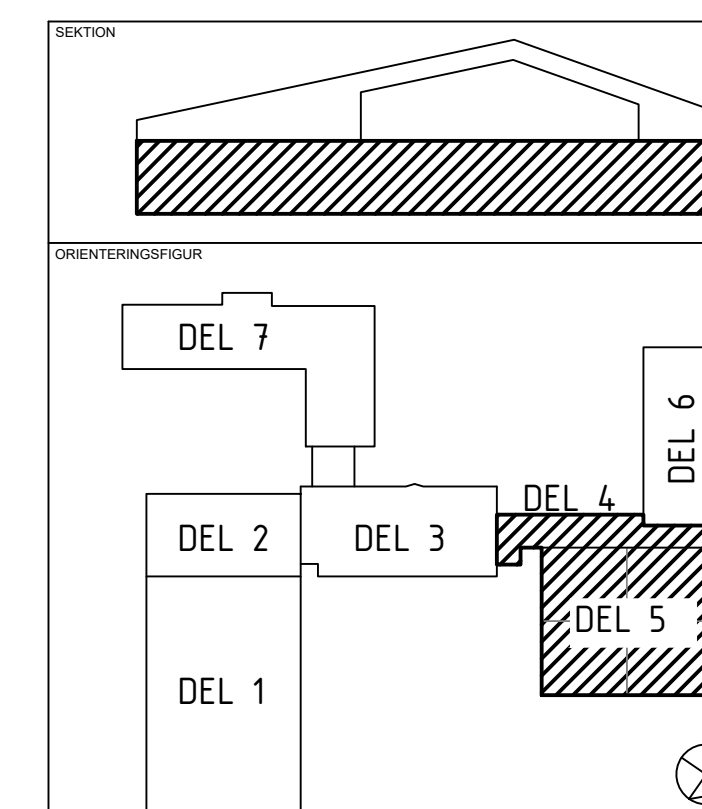

|        |                      |
|--------|----------------------|
| STATUS | FÖRFRÅGNINGSUNDERLAG |
|--------|----------------------|

|          |
|----------|
| HANDLING |
|----------|

|            |                 |    |
|------------|-----------------|----|
| DATUM      | GODKÄND AV      | AN |
| 2024-12-20 | DAVID N.BACKMAN | -  |

BESTÄLLARE



ROBERTSFORS KOMMUN

PROJEKTNAMN

CENTRAALKÖK

OMRÅDE

ROBERTSFORS KOMMUN

|               |                   |
|---------------|-------------------|
| PROJEKTNUMMER | ADRESS            |
| -             | YTTRE RINGVÄGEN 4 |

|              |                   |
|--------------|-------------------|
| -            | TYRE KINGSVALEN 4 |
| DIARIENUMMER | FASTIGHET         |
| -            | FORDONET 1        |

|           |                      |
|-----------|----------------------|
| DISCIPLIN | FÖRETAG              |
| LE        | NORCONSULT SVERIGE A |

|               |           |
|---------------|-----------|
| UPPDAGSNUMMER | SKAPAD AV |
| 108 83 71     | PLT       |

|               |                     |
|---------------|---------------------|
| TELEFON       | KONTAKTPERSON       |
| 010 141 80 00 | DAVID NYMAN BACKMAN |

|               |                        |
|---------------|------------------------|
| BYGGNADSVÄRDE | PLUSHÖJD (RH 2000)     |
| -             | +44,60, +45,07, +45,54 |

|             |            |           |
|-------------|------------|-----------|
| VÄNINGSPLAN | VÄNINGSDEL | DELOMRÅDE |
| 1           | -          | DEL 4, 5  |

|               |                              |
|---------------|------------------------------|
| SYSTEM        | 57 SAMMANSATT LUFTBEHANDLING |
| SPECIFIKATION |                              |

|                  |       |
|------------------|-------|
| SPECIFIKATION    |       |
| ÖVERSIKT         |       |
| BITARINFORMATION | SKALA |

|                 |       |    |
|-----------------|-------|----|
| RITINGSKATEGORI | SKALA | FO |
| PLAN            | 1:200 | A  |
| DOKUMENTNUMMER  |       | AN |

|                |    |
|----------------|----|
| DOKUMENTNUMMER | AN |
| V-57-1-100     | -  |

FÖRLÄGGNING DON  
I RAMVERK  
SKALA 1:20

SKALA 1:200

0 1 2 5 10 15 20  
METER

|          |
|----------|
| FILNAMN: |
|----------|