

FÖRKLARINGAR:

ALLMÄNT	
LUFTMANGDER ANGIVNA I l/s	
A	AVLUFT
U	UTLUFT
F	FRÅNLUFT
T	TILLUFT
LA	LUFTBEHANDLINGSAGGREGAT
KF	KANALFLÄKT
INKL	INKLÄDNAD AV KANAL

T-rör, X-rör, böj, T-rör med extra påstick ska vara fabriksfärdiga produkter.



KANALTYP	
11	FÖRZINKAD STÅLPLÅT, TÄTHET C
14	KANALER AV STÅLPLÅT I VÄTSKETÄT UTFÖRANDE,

TILLUFTSDON/FRÅNLUFTSDON	
TD201	TAKDON, TILLUFT
TD801	TALLRIKSVENTIL, TILLUFTSDON
FD101	KONTROLLVENTIL
FD201	INFÄLLT TAKDON, FRÅNLUFT
FD301	TRÄDNÄTSGALLER, FRÅNLUFT
FD401	TRÄDNÄTSGALLER, CIRKULÄRT
IK201-1-2,-3	IMKÅPA, KÖK
IK202	IMKÅPA, DIET
IK401	DISKKÅPA, TUNNELDISK
IK402	DISKKÅPA, GROVDISK
OD101/102	ÖVERLUFTSDON

UTLUFTS/AVLUFTSGALLER/HUVAR	
AD101	AVLUFTSVÄGGALLER
AD102	AVLUFTSVÄGGHUV
AD103	AVLUFTSVÄGGALLER
AD201	AVLUFTSHUV TAKPLACERAD FÖR LA01
UD101	UTLUFTSVÄGGALLER
UD102	UTLUFTSVÄGGHUV
UD201	UTLUFTSHUV TAKPLACERAD

ÖVRIGT	
LD101	LJUDDÄMPARE, CIRKULÄR ANSLUTNING
LD201	REKTANGULÄR LJUDDÄMPARE MED INV. BAFFLAR
LD202	REKTANGULÄR LJUDDÄMPARE MED INV. BAFFLAR
LD501	FLEXIBEL KANALLJUDDÄMPARE
RL101	RENSLUCKA CIRKULÄR
RL102	RENSLUCKA REKTANGULÄR
SP101	VRIKSPJÄLL, MANUELLT
SP201	INJUSTERINGSSPJÄLL TYP IRIS
SP401	REKTANGULÄR SPJÄLL, MANUELLT
SP701	CIRKULÄRT SPJÄLL MED HYLLA FÖR MOTOR
SP702	REKTANGULÄRT SPJÄLL MED HYLLA FÖR MOTOR
SP8XX	SPJÄLL MED MOTOR

ISOLERING	
/K403	KONDENSISOLERING 30mm
/K405	KONDENSISOLERING 50mm
/K713	CELLGUMMI, ULTIMA 13 MM
/V315	VÄRMEISOLERING, 150mm

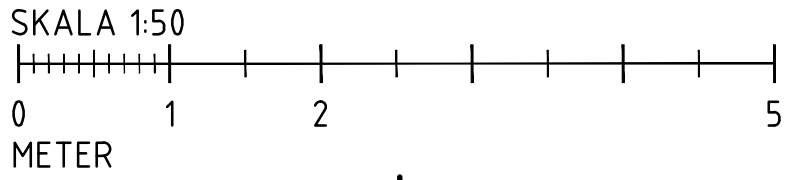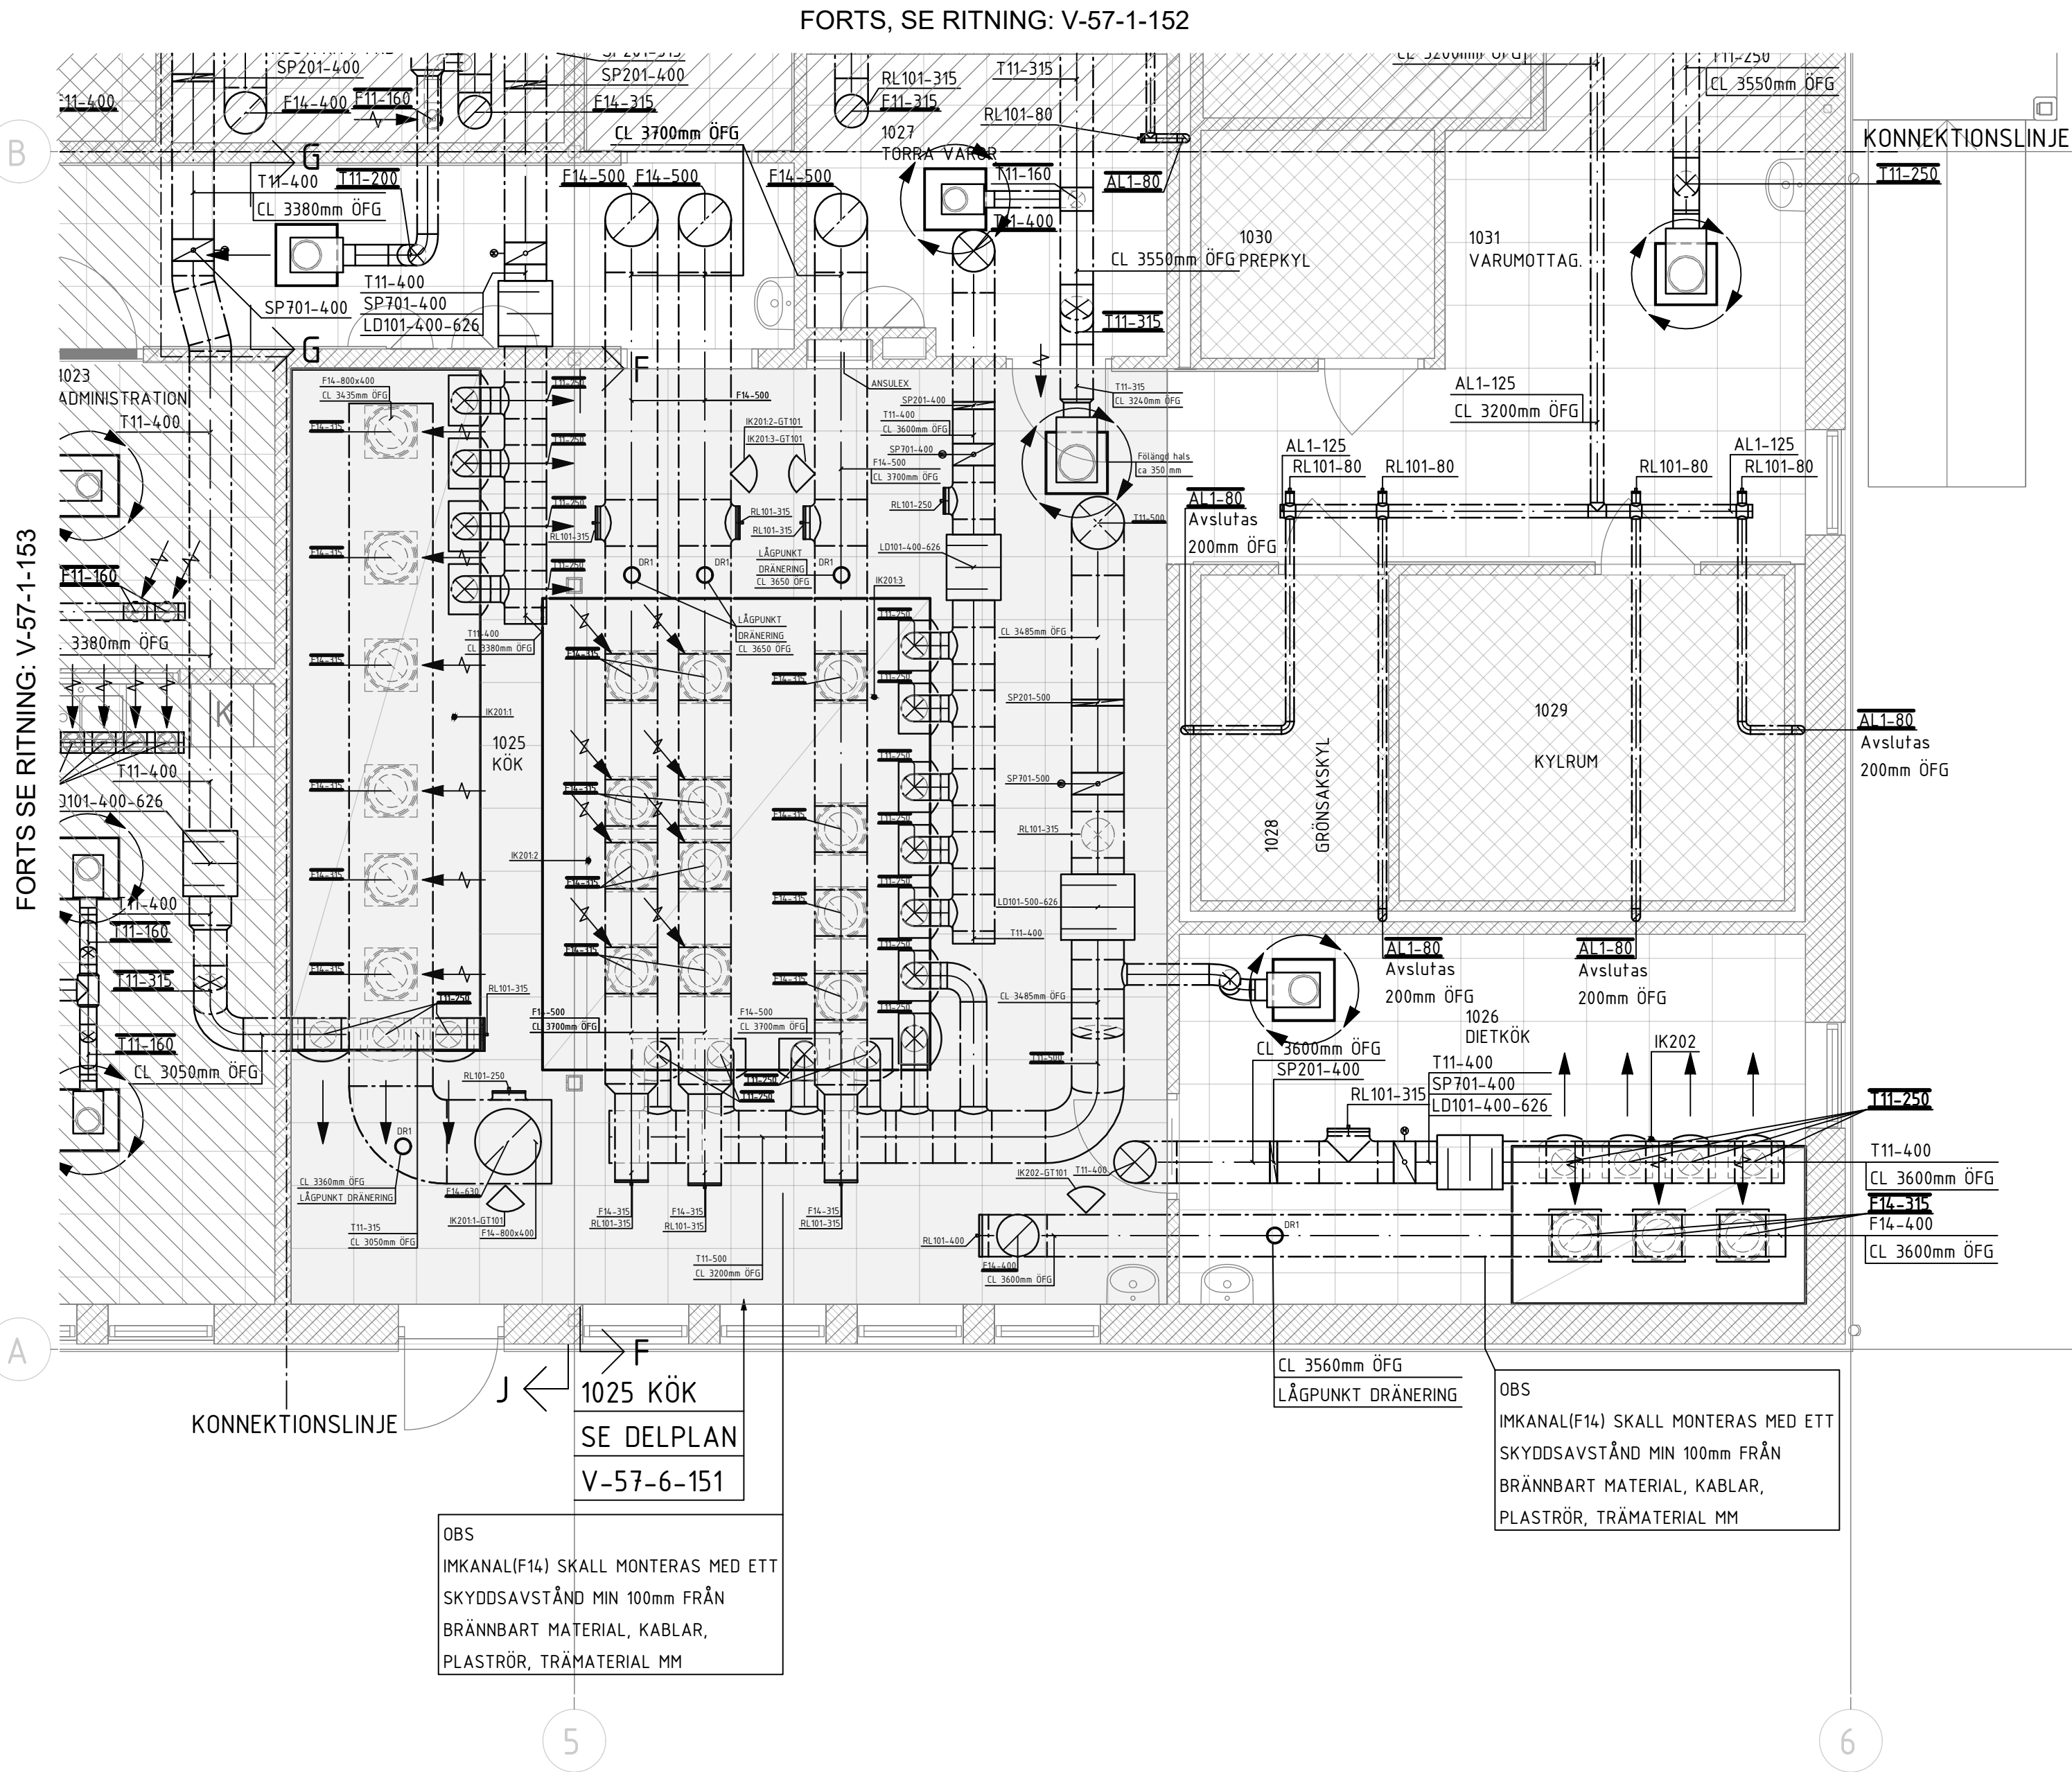


1024 PASSAGE
TD201-250-600 +ALSd 200-250
80/-

1025 KÖK
1xTD201-315-600+ALSd 250-315
140/-
IK201:1 840/1200
IK201:2 500/840
IK201:3 650/750

1026 DIETKÖK
IK202
4xTD Ø250, 3xTD Ø315
430/480

1027 TORRA VARÖR
TD201-200-600 +ALSd 160-200
50/-

1031 VARUMOTTAGNING
2xTD201-315-600+ALSd 250-315
280/-

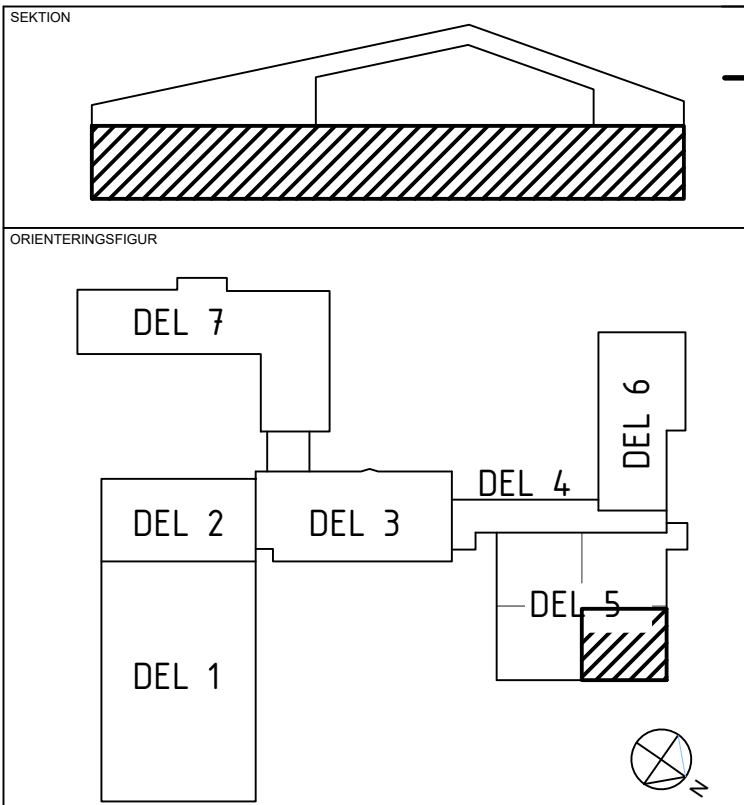

SEKTION

ORIENTERINGSPOL

DEL 1 DEL 2 DEL 3 DEL 4 DEL 5 DEL 6 DEL 7

STATUS

FÖRFRÅGNINGSUNDERLAG

HANDLING

DATUM 2024-12-20 GODKÄND AV DAVID N.BACKMAN ANDRINGS PM -

BESTÄLLARE

ROBERTSFORS KOMMUN

PROJEKTNAMN

CENTRAALKÖK

ROBERTSFORS KOMMUN

OMRADE

PROJEKTNUMMER

ADRESS

YTTRE RINGVÄGEN 4

DIARIENUMMER

FASTIGHET

FORDONET 1

DISCIPLIN

FÖRETAG

NORCONSULT SVERIGE AB

UPPDRAGSNUMMER

SKAPAD AV

PLT

TELEFON

KONTAKTPERSON

DAVID NYMAN BACKMAN

BYGGNADSVÄRDE

FLUSHÖJD (RH 2000)

+44,60, +45,07, +45,54 (FG)

VÄNINGSPLAN

VÄNINGSDEL

DEL 4, 5

SYSTEM

57 SAMMANSATT LUFTBEHANDLING

DELPLAN

PLAN

SKALA

1:50

FORMAT

A1

ANDRNING

-

V-57-1-154