


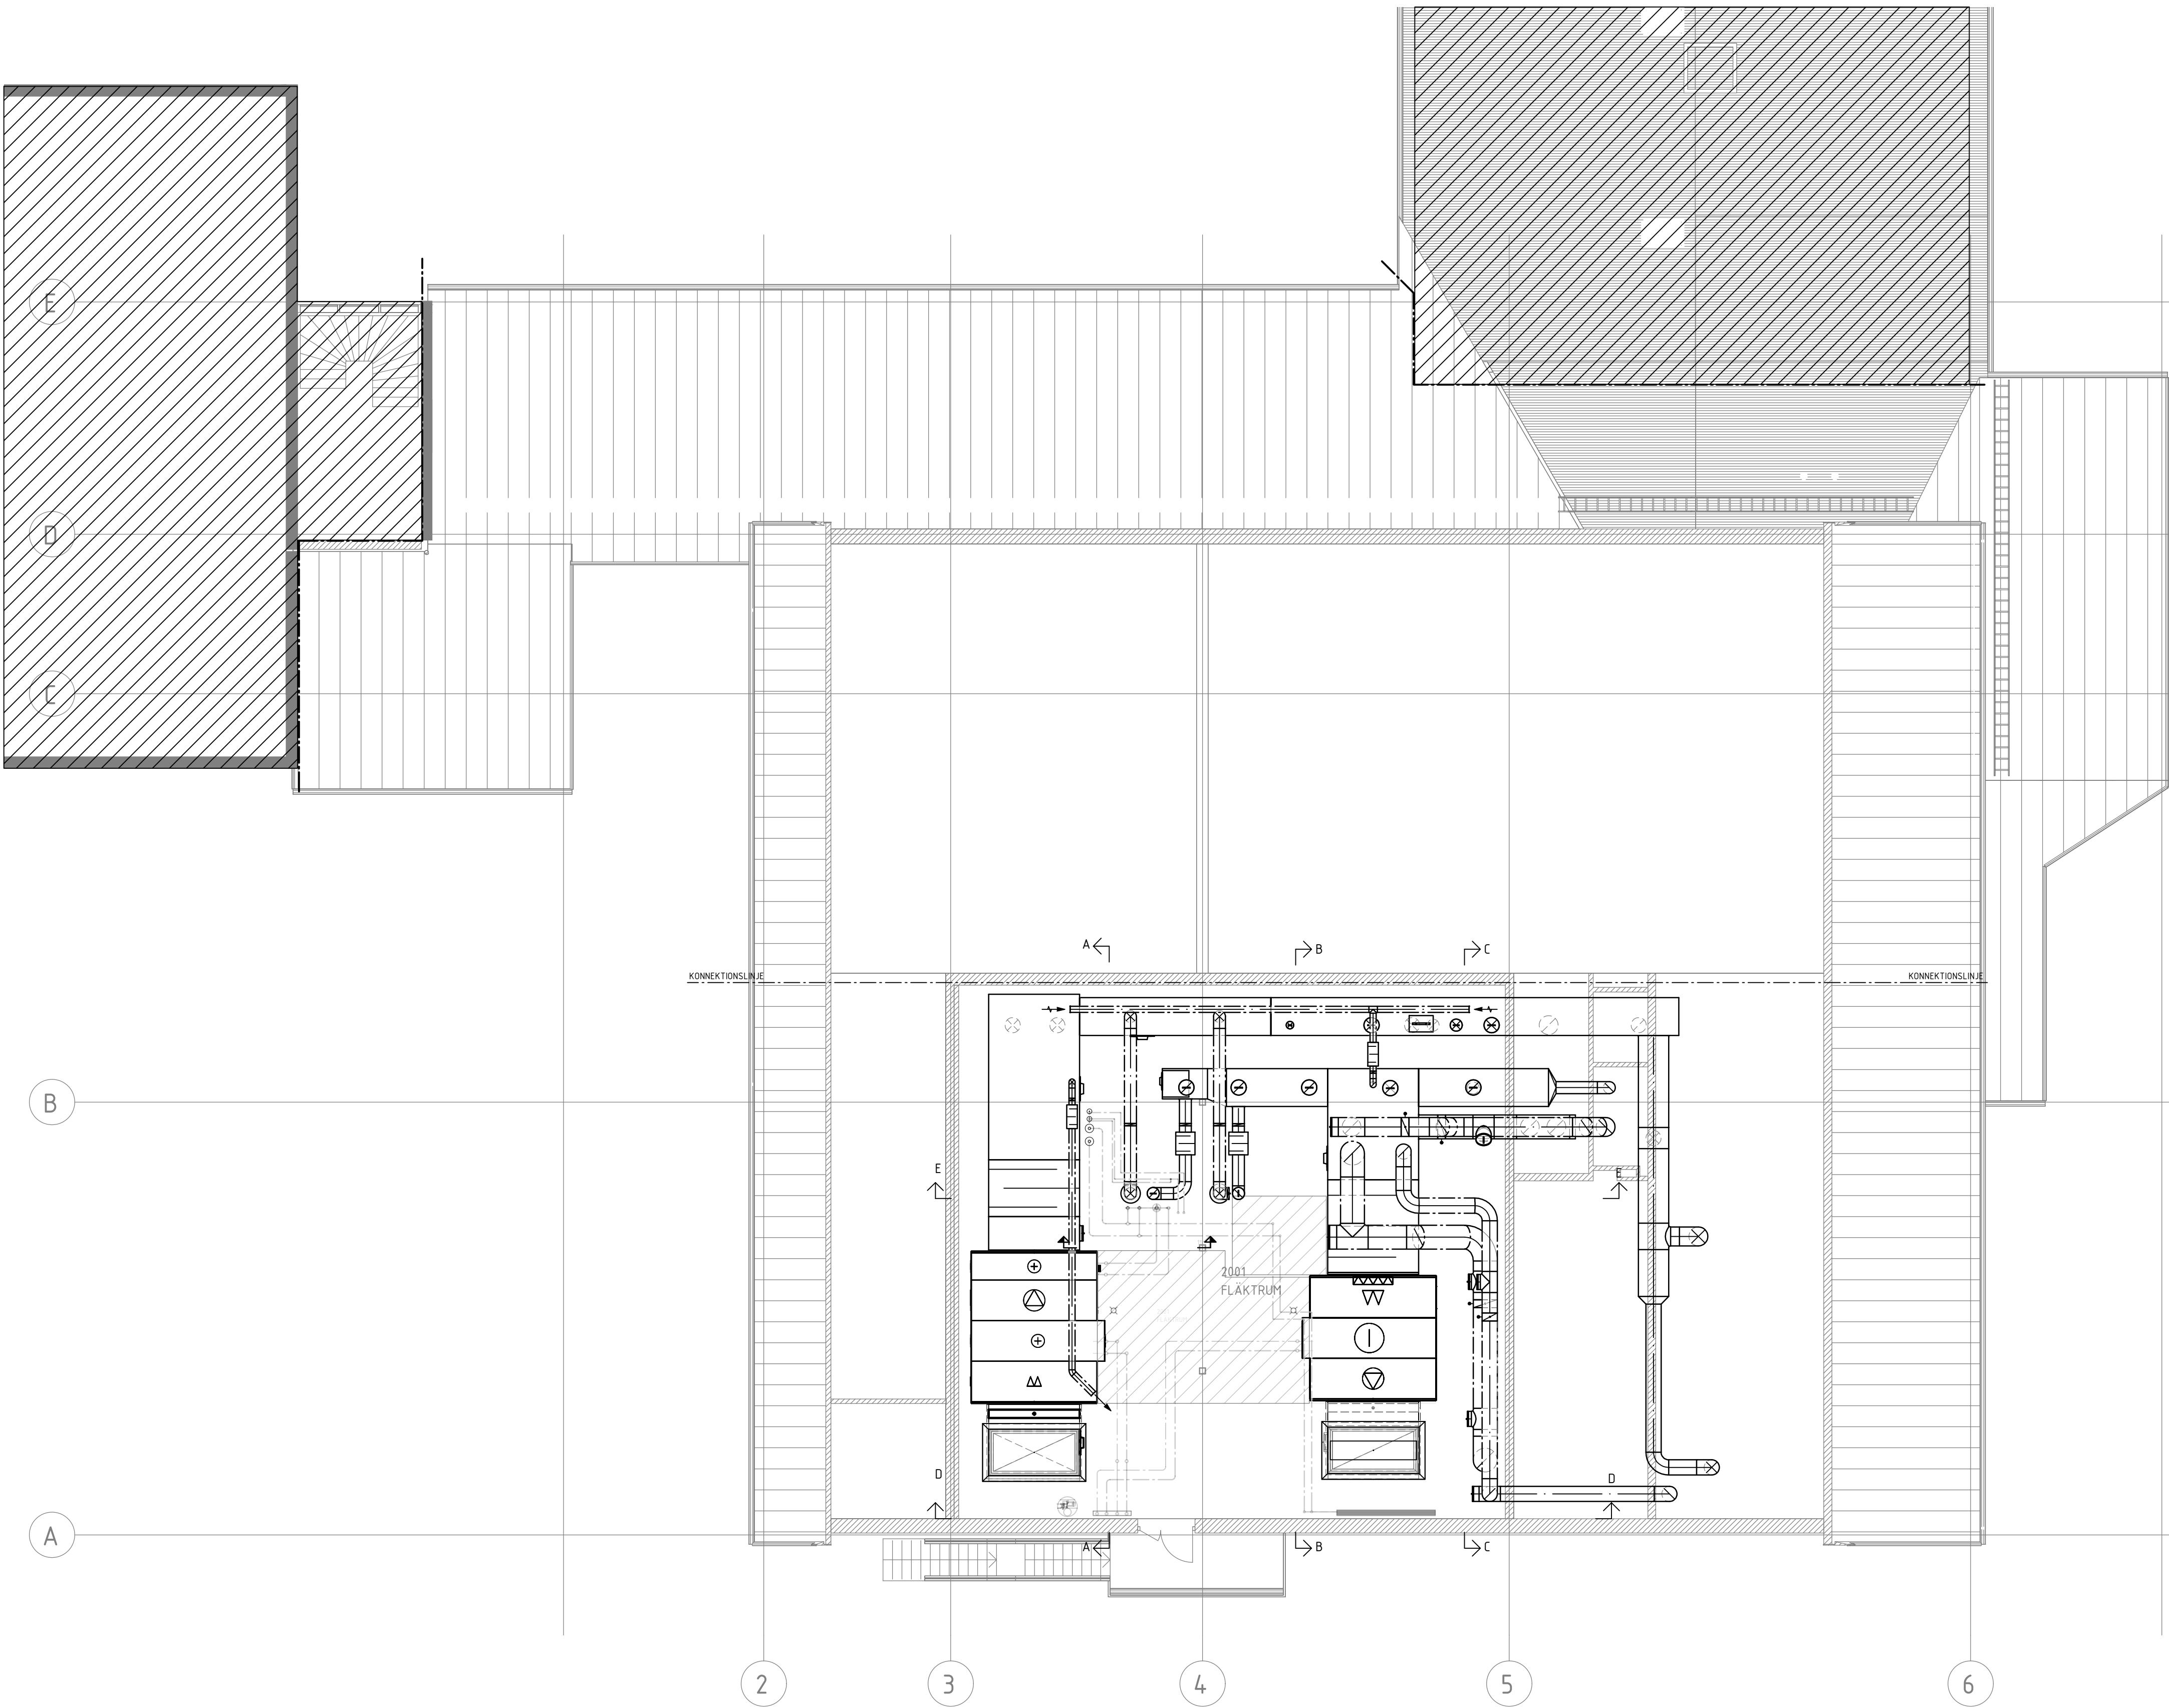

FÖRKLARINGAR:

ALLMÄNT	
LUFTMÄNGDER ANGIVNA I l/s	
A	AVLUFT
U	UTLUFT
F	FRÅNLUFT
T	TILLUFT
LA	LUFTBEHANDLINGSAGGREGAT
KF	KANALFLÄKT
INKL	INKLÄDNAD AV KANAL
T-rör, X-rör, böj, T-rör med extra påstick ska vara fabriksfärdiga produkter.	
KANALTYP	
11	FÖRZINKAD STÅLPLÅT, TÄTHET C
14	KANALER AV STÅLPLÅT I VÄTSKETÄT UTFÖRANDE,
TILLUFTSDON/FRÅNLUFTSDON	
TD201	TAKDON, TILLUFT
TD801	TALLRIKSVENTIL, TILLUFTSDON
FD101	KONTROLLVENTIL
FD201	INFÄLLT TAKDON, FRÅNLUFT
FD301	TRÄDNÄTSGALLER, FRÅNLUFT
FD401	TRÄDNÄTSGALLER, CIRKULÄRT
IK201-1,-2,-3	IMKÅPA, KÖK
IK202	IMKÅPA, DIET
IK401	DISKKÅPA, TUNNELDISK
IK402	DISKKÅPA, GROVDISK
OD101/102	ÖVERLUFTSDON

UTLUFTS/AVLUFTSGALLER/HUVAR	
AD101	AVLUFTSVÄGGALLER
AD102	AVLUFTSVÄGGHUV
AD103	AVLUFTSVÄGGALLER
AD201	AVLUFTSHUV TAKPLACERAD FÖR LA01
UD101	UTLUFTSVÄGGALLER
UD102	UTLUFTSVÄGGHUV
UD201	UTLUFTSHUV TAKPLACERAD
ÖVRIGT	
LD101	LJUDDÄMPARE, CIRKULÄRT ANSLUTNING
LD201	REKTANGULÄRT LJUDDÄMPARE MED INV. BÄFFLAR
LD202	REKTANGULÄRT LJUDDÄMPARE MED INV. BÄFFLAR
LD501	FLEXIBEL KANALLJUDDÄMPARE
RL101	RENSLUCKA CIRKULÄRT
RL102	RENSLUCKA REKTANGULÄRT
SP101	VRIKSPJÄLL, MANUELLT
SP201	INJUSTERINGSSPJÄLL TYP IRIS
SP401	REKTANGULÄRT SPJÄLL, MANUELLT
SP701	CIRKULÄRT SPJÄLL MED HYLLA FÖR MOTOR
SP702	REKTANGULÄRT SPJÄLL MED HYLLA FÖR MOTOR
SP8XX	SPJÄLL MED MOTOR
ISOLERING	
/K403	KONDENSISOLERING 30mm
/K405	KONDENSISOLERING 50mm
/K713	CELLGUMMI, ULTIMA 13 MM
/V315	VÄRMEISOLERING, 150mm

SEKTION

ORIENTERINGSPOL

STATUS

HANDLING

DATUM

2024-12-20

GODKÄND AV

DAVID N.BACKMAN

ÄNDRINGS PM

BESTÄLLARE

ROBERTSFORS KOMMUN

ROBERTSFORS KOMMUN

PROJEKTNAMN

CENTRALEKÖ

OMRADE

ROBERTSFORS KOMMUN

PROJEKTNUMMER

YTTRE RINGVÄGEN 4

DIARIENUMMER

FÖRORDNET 1

DISCIPLIN

NORCONSULT SVERIGE AB

UPPDRAGSNUMMER

PLT

TELEFON

DAVID NYMAN BACKMAN

BYGGNADSVÄRDE

+44,60, +45,07, +45,54 (FG)

VÄNINGSPLAN

2

VÄNINGSDEL

DEL 4, 5

SYSTEM

57 SAMMANSATT LUFTBEHANDLING

ÖVERSIKTSPLAN

PLAN

SKALA

1:100

FORMAT

A1

DOKUMENTNUMMER

V-57-1-200

