FÖRKLARINGAR:

ALLMÄNT

LUFTMÄNGDER ANGIVNA I l/s

A	AVLUFT
U	UTELUFT
F	FRÅNLUFT
T	TILLUFT
LA	LUFTBEHANDLINGSAGGREGAT
KF	KANALFLÄKT
INKL	INKLÄDNAD AV KANAL

T-rör, X-rör, böj, T-rör med extra påstick ska vara fabrikstillverkade produkter.

KANALTYPER

11	FÖRZINKAD STÅLPLÅT, TÄTHET C
14	KANALER AV STÅLPLÅT I VÄTSKETÄT UTFÖRANDE,

TILLUFTSDON/FRÅNLUFTSDON

TD201	TAKDON, TILLUFT
TD801	TALLRIKSVENTIL, TILLUFTSDON
FD101	KONTROLLVENTIL
FD201	INFÄLLT TAKDON, FRÅNLUFT
FD301	TRÅDNÄTSGALLER, FRÅNLUFT
FD401	TRÅDNÄTSGALLER, CIRKULÄRT
IK201-1,-2,-3	IMKÅPA, KÖK
IK202	IMKÅPA, DIET
IK401	DISKKÅPA, TUNNELDISK
IK402	DISKKÅPA, GROVDISK
OD101/102	ÖVERLUFTSDON

UTELUFTS/AVLUFTSGALLER/HUVAR

AD101	AVLUFTSVÄGGALLER
AD102	AVLUFTSVÄGGHUV
AD103	AVLUFTSVÄGGALLER
AD201	AVLUFTSHUV TAKPLACERAD FÖR LA01
UD101	UTELUFTSVÄGGALLER
UD102	UTELUFTSVÄGGHUV
UD201	UTELUFTSHUV TAKPLACERAD

ÖVRIGT

LD101	LJUDDÄMPARE, CIRKULÄR ANSLUTNING
LD201	REKTANGULÄR LJUDDÄMPARE MED INV. BAFFLAR
LD202	REKTANGULÄR LJUDDÄMPARE MED INV. BAFFLAR
LD501	FLEXIBEL KANALLJUDDÄMPARE
RL101	RENSLUCKA CIRKULÄR
RL102	RENSLUCKA REKTANGULÄR
SP101	VRIDSPJÄLL, MANUELLT
SP201	INJUSTERINGSSPJÄLL TYP IRIS
SP401	REKTANGULÄR SPJÄLL, MANUELLT
SP701	CIRKULÄRT SPJÄLL MED HYLLA FÖR MOTOR
SP702	REKTANGULÄRT SPJÄLL MED HYLLA FÖR MOTOR
SP8XX	SPJÄLL MED MOTOR

ISOLERING

/K403	KONDENSISOLERING 30mm
/K405	KONDENSISOLERING 50mm
/K713	CELLGUMMI, ULTIMA 13 MM
/V315	VÄRMEISOLERING, 150mm

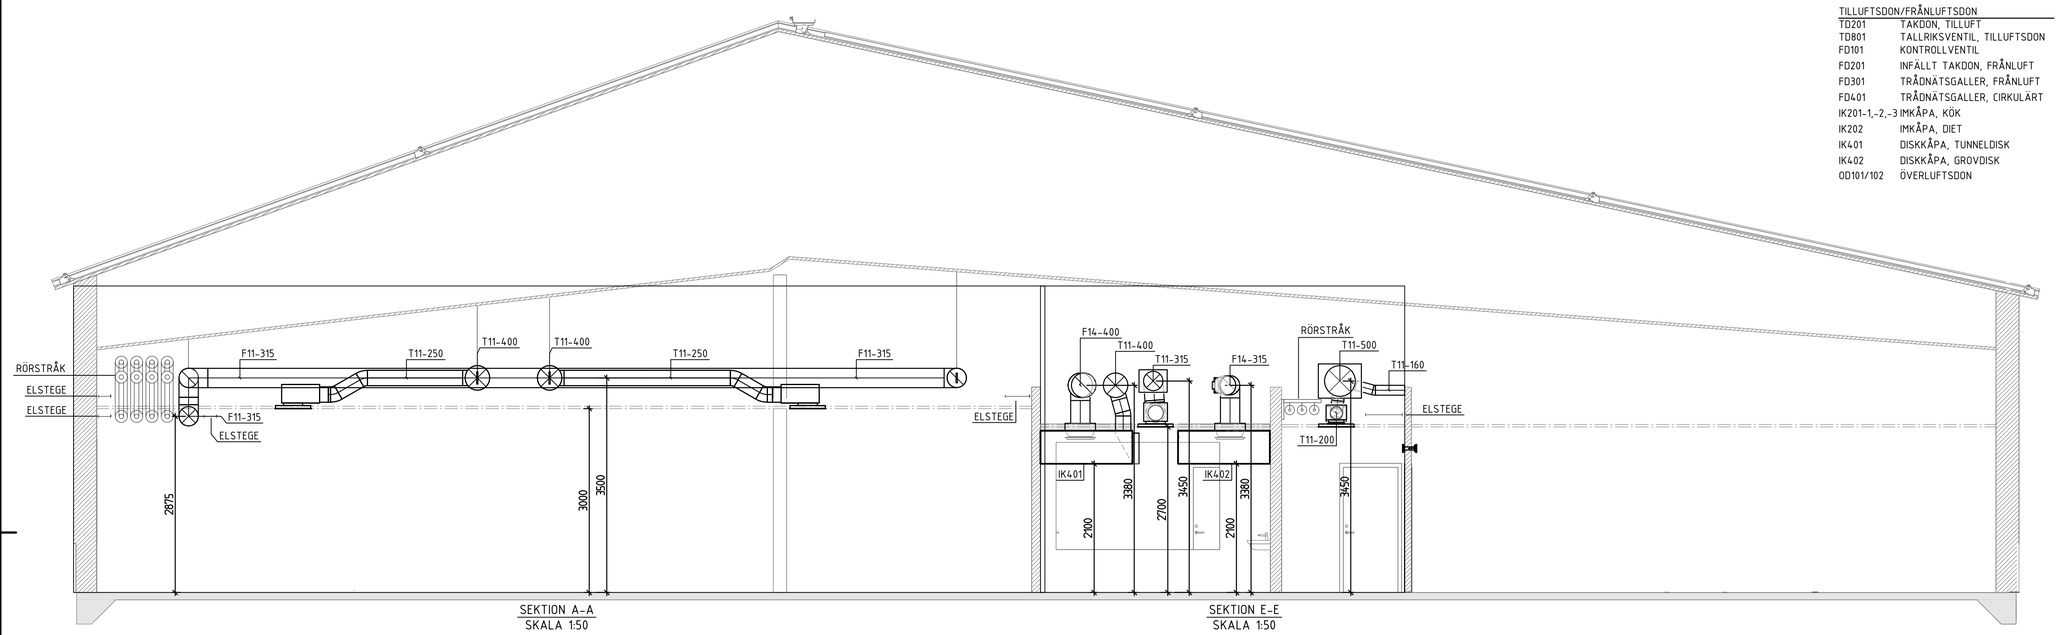

SEKTION A-A
SKALA 1:50

SEKTION E-E
SKALA 1:50

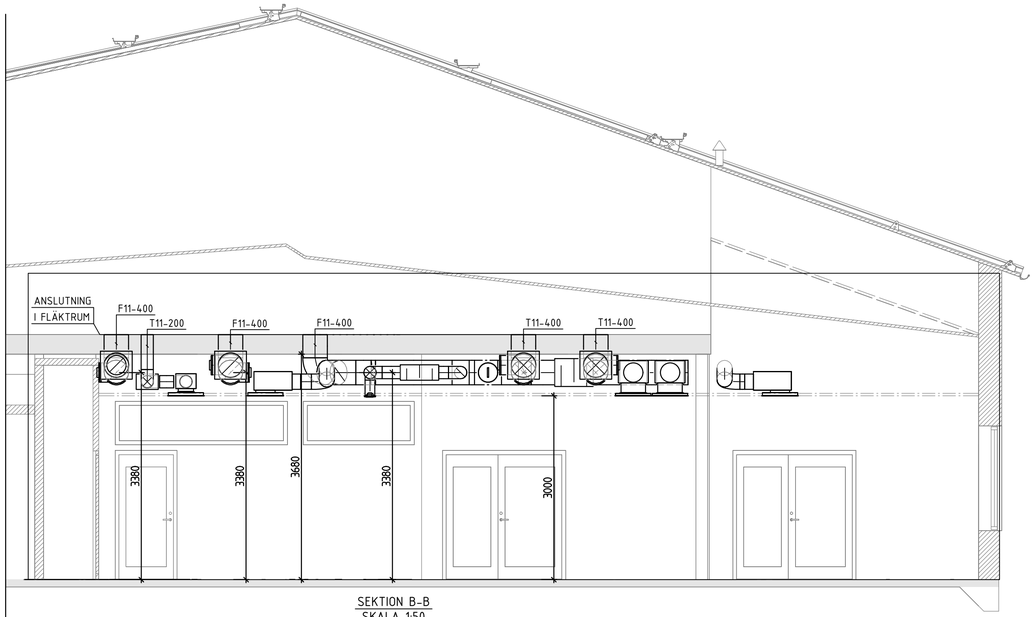

SEKTION B-B
SKALA 1:50

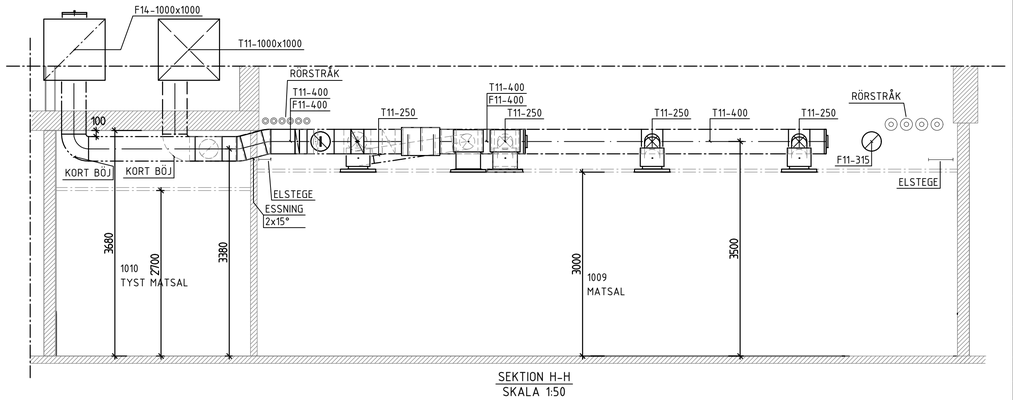

SEKTION H-H
SKALA 1:50

SKALA 1:50

0 1 2 5

METER

SEKTION

ORIENTERINGSFIGUR

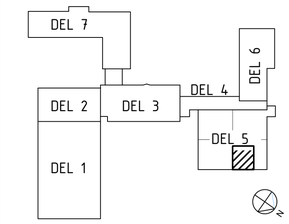

STATUS
FÖRFRÅGNINGSUNDERLAG

HANDLING
–

DATUM	GODKÄND AV	ÄNDRINGS PM
2024-12-20	DAVID N.BACKMAN	–

BESTÄLLARE

ROBERTSFORS KOMMUN

PROJEKTNAMN
CENTRALKÖK

OMRÅDE
ROBERTSFORS KOMMUN

PROJEKTNUMMER	ADRESS
–	YTTRE RINGVÄGEN 4
DIARIENUMMER	FASTIGHET
–	FORDONET 1
DISCIPLIN	FÖRETAG
LE	NORCONSULT SVERIGE AB
UPPDRAGSNUMMER	SKAPAD AV
108 83 71	PLT
TELEFON	KONTAKTPERSON
010 141 80 00	DAVID NYMAN BACKMAN
BYGGNADSVERK	PLUSHÖJD (RH 2000)
–	+44,60, +45,07, +45,54 (FG)
VÅNINGSPLAN / VÅNINGSDEL	DELOMRÅDE
1 / –	DEL 4, 5

SYSTEM
57 SAMMANSATT LUFTBEHANDLING

SPECIFIKATION
SEKTIONER

RITNINGSKATEGORI	SKALA	FORMAT
PLAN	1:50	A1
DOKUMENTNUMMER		ÄNDRING
V-57-2-101		–

FILNAMN:
TE X:\108\83\V\08377\5 ARBETSMATERIAL\02 BIM\V1-2D\MODELLUPPDRAG PLOTTAD 2024-12-20 11:16 AV ANVÄNDARE FETELU