


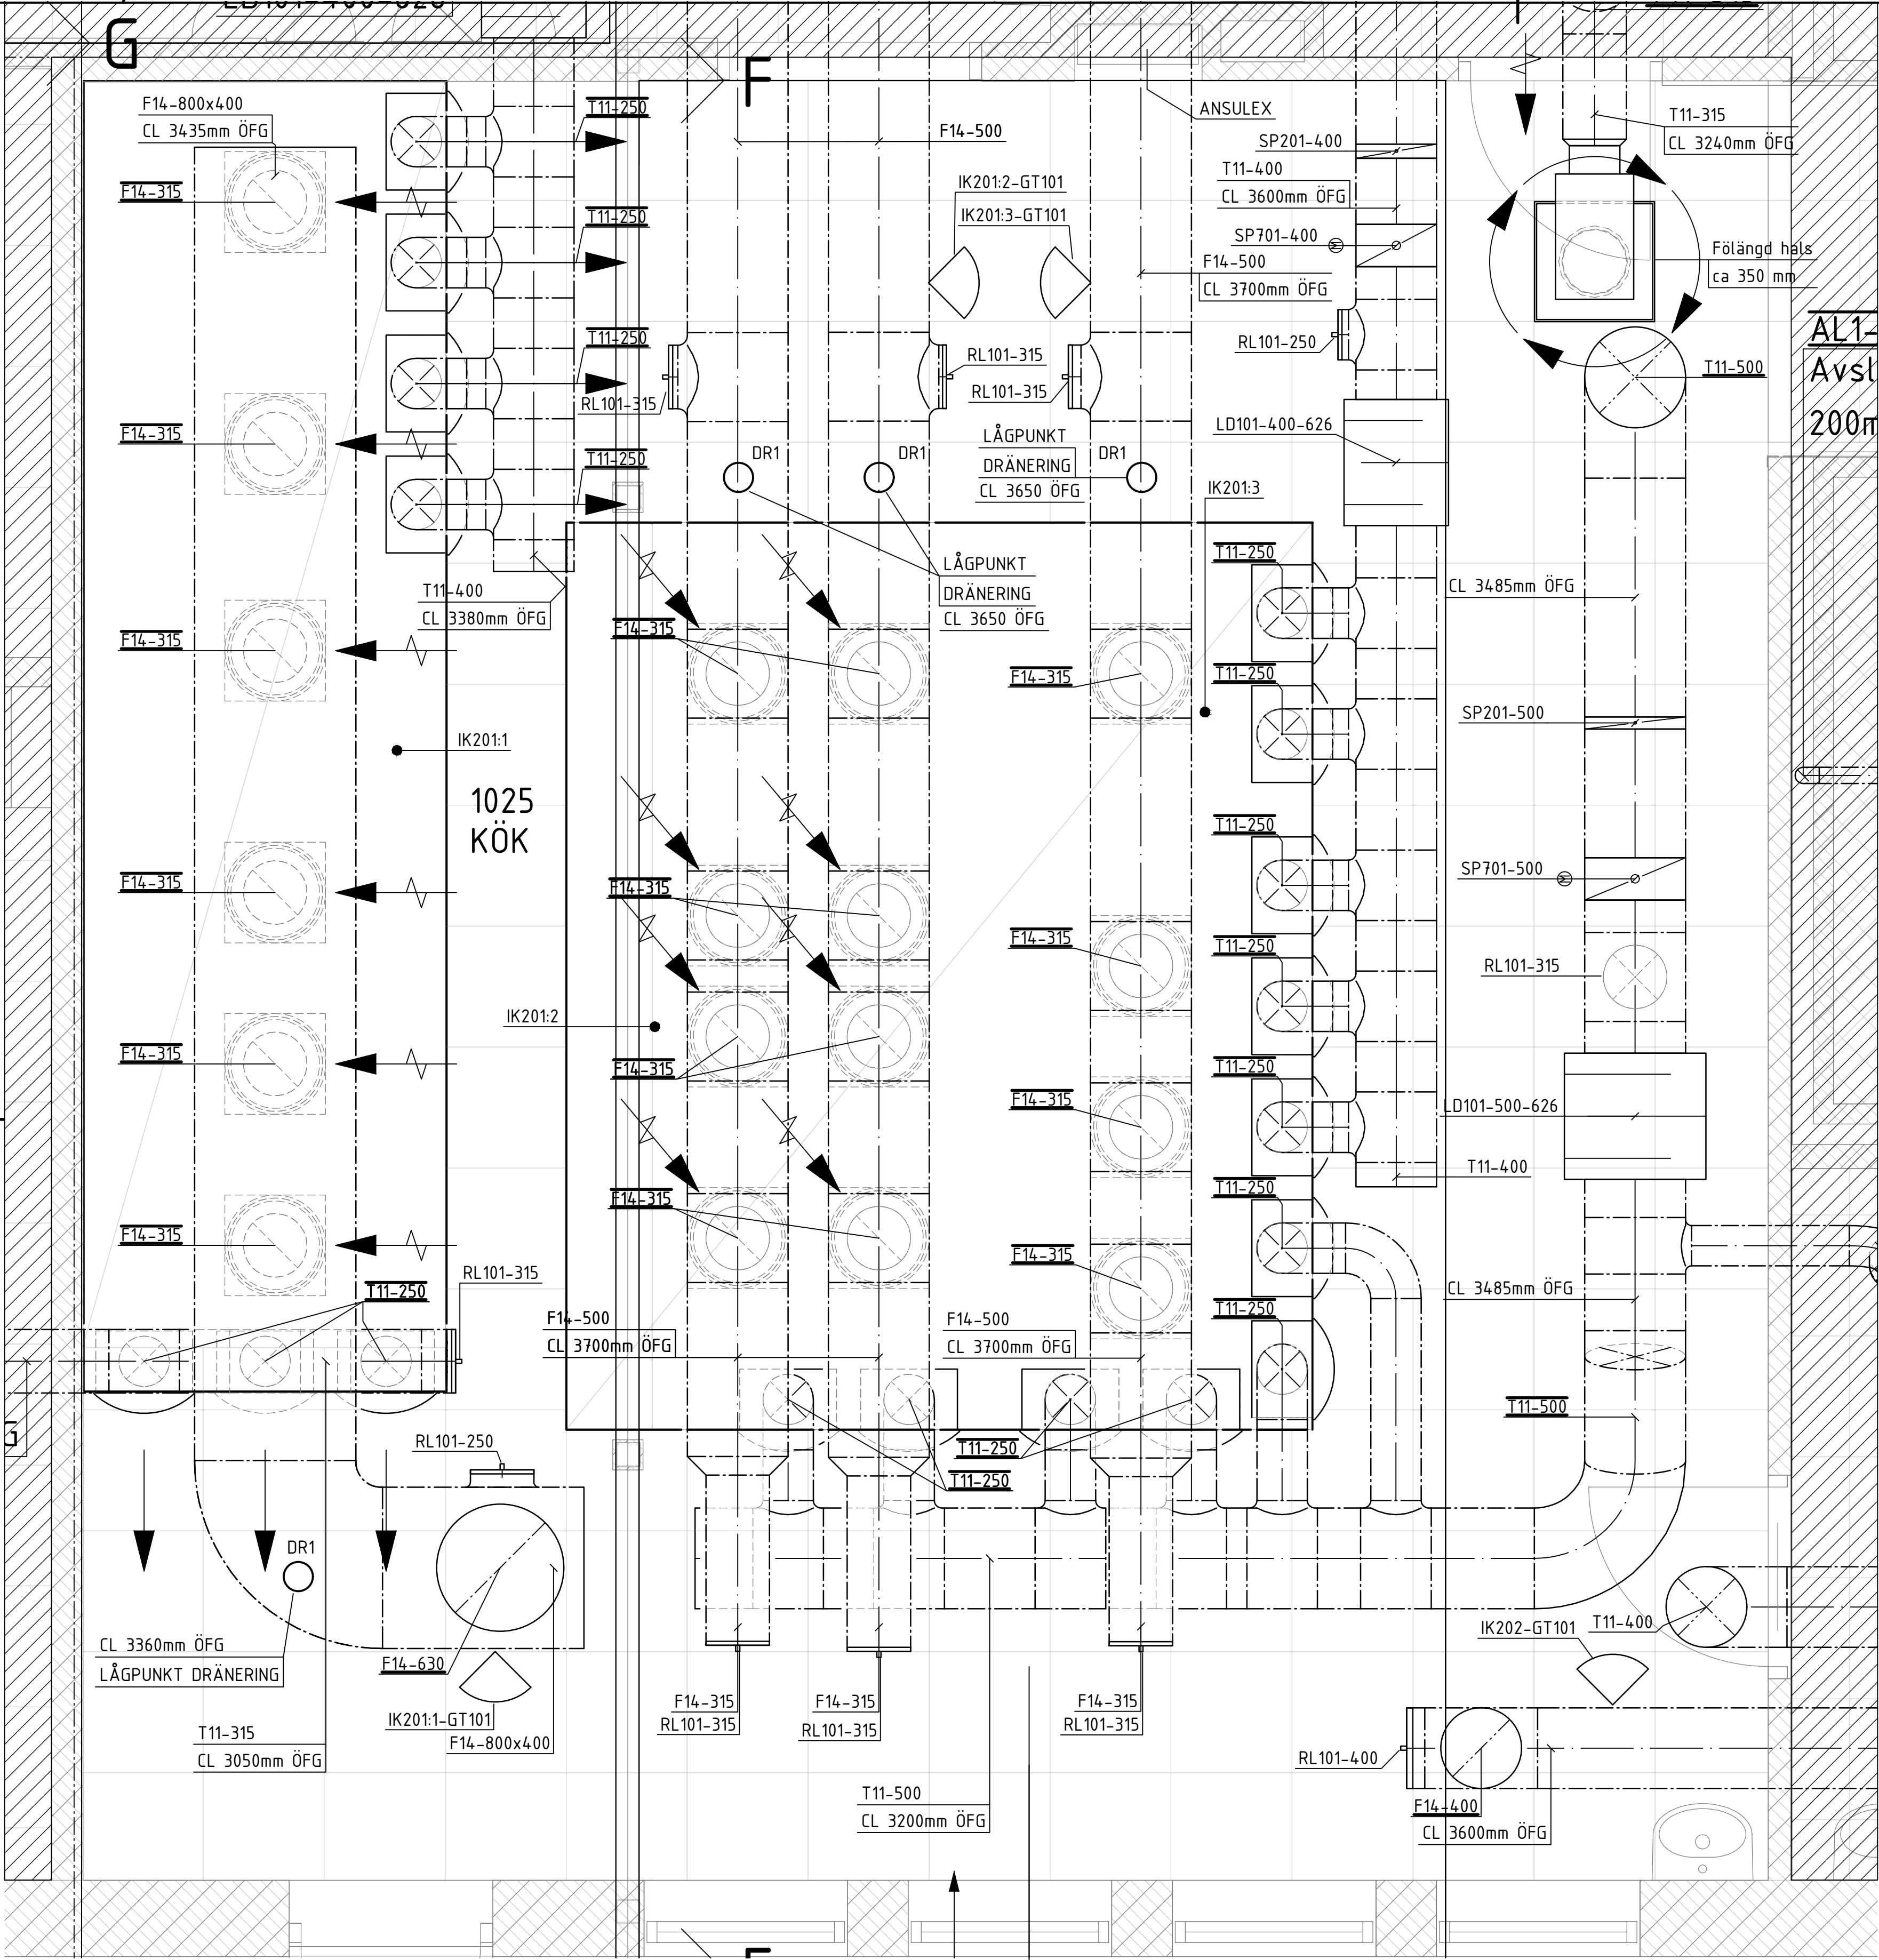

FÖRKLARINGAR:

ALLMÄNT	
LUFTMÄNGDER ANGIVNA I l/s	
A	AVLUFT
U	UTLUFT
F	FRÅNLUFT
T	TILLUFT
LA	LUFTBEHANDLINGSAGGREGAT
KF	KANALFLÄKT
INKL	INKLÄDNAD AV KANAL

T-rör, X-rör, böj, T-rör med extra påstick ska vara fabriksfärdiga produkter.


KANALTYP	
11	FÖRZINKAD STÅLPLÅT, TÄTHET C
14	KANALER AV STÅLPLÅT I VÄTSKETÄT UTFÖRANDE,

TILLUFTSDON/FRÅNLUFTSDON	
TD201	TAKDON, TILLUFT
TD801	TALLRIKSVENTIL, TILLUFTSDON
FD101	KONTROLLVENTIL
FD201	INFÄLLT TAKDON, FRÅNLUFT
FD301	TRÄDNÄTSGALLER, FRÅNLUFT
FD401	TRÄDNÄTSGALLER, CIRKULÄRT
IK201-1-2,-3	IMKÅPA, KÖK
IK202	IMKÅPA, DIET
IK401	DISKKÅPA, TUNNELDISK
IK402	DISKKÅPA, GROVDISK
OD101/102	ÖVERLUFTSDON

UTLUFTS/AVLUFTSGALLER/HUVAR	
AD101	AVLUFTSVÄGGALLER
AD102	AVLUFTSVÄGGHUV
AD103	AVLUFTSVÄGGALLER
AD201	AVLUFTSHUV TAKPLACERAD FÖR LA01
UD101	UTLUFTSVÄGGALLER
UD102	UTLUFTSVÄGGHUV
UD201	UTLUFTSHUV TAKPLACERAD

ÖVRIGT	
LD101	LJUDDÄMPARE, CIRKULÄRT ANSLUTNING
LD201	REKTANGULÄRT LJUDDÄMPARE MED INV. BAFFLAR
LD202	REKTANGULÄRT LJUDDÄMPARE MED INV. BAFFLAR
LD501	FLEXIBEL KANALLJUDDÄMPARE
RL101	RENSLUCKA CIRKULÄRT
RL102	RENSLUCKA REKTANGULÄRT
SP101	VRIDSPJÄLL, MANUELLT
SP201	INJUSTERINGSSPJÄLL TYP IRIS
SP401	REKTANGULÄRT SPJÄLL, MANUELLT
SP701	CIRKULÄRT SPJÄLL MED HYLLA FÖR MOTOR
SP702	REKTANGULÄRT SPJÄLL MED HYLLA FÖR MOTOR
SP8XX	SPJÄLL MED MOTOR

ISOLERING	
/K403	KONDENSISOLERING 30mm
/K405	KONDENSISOLERING 50mm
/K713	CELLGUMMI, ULTIMA 13 MM
/V315	VÄRMEISOLERING, 150mm

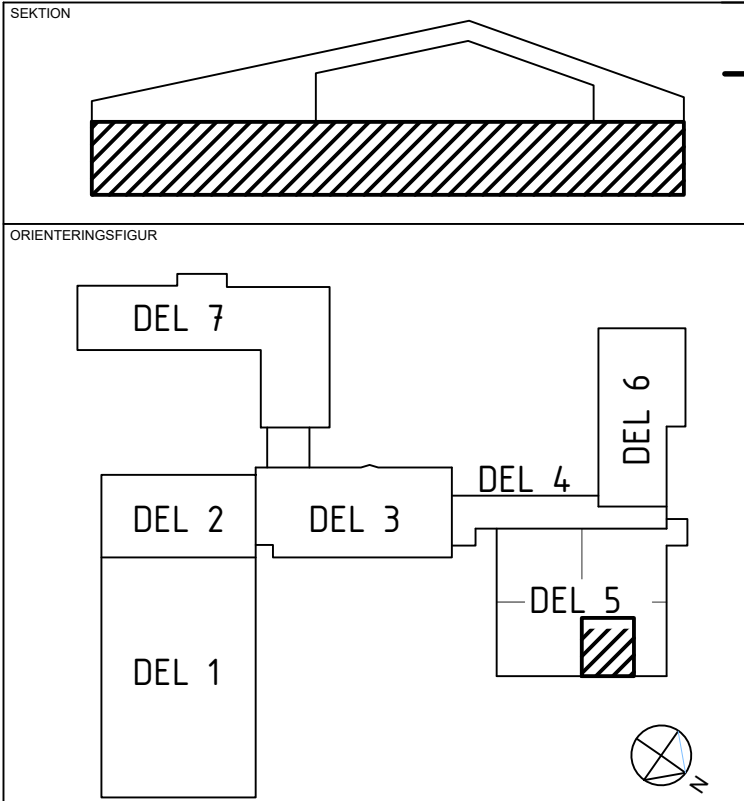

SEKTION		
ORIENTERINGSSKISS		
STATUS		
HANDLING		
DATUM		
GODKÄND AV		
BESTÄLLARE		
ROBERTSFORS KOMMUN		
CENTRALEKÖ		
ROBERTSFORS KOMMUN		
PROJEKTNAMN		
OMRÅDE		
PROJEKTNUMMER		
ADRESS		
FASTIGHET		
FÖRORDNET 1		
DISCIPLIN		
FÖRETAG		
NORCONSULT SVERIGE AB		
UPPDRAGSNUMMER		
SKAPAD AV		
PLT		
TELEFON		
KONTAKTPERSON		
DAVID NYMAN BACKMAN		
BYGGNADSVÄRDE		
FLUSHÖJD (RH 2000)		
+44,60, +45,07, +45,54 (FG)		
VÄNINGSPLAN		
VÄNINGSDEL		
DEL 4, 5		
SYSTEM		
57 SAMMANSATT LUFTBEHANDLING		
BESKRIVNING		
DELPLAN		
RITNINGSKATEGORI		
PLAN		
SKALA		
1:20		
FORMAT		
A1		
DOKUMENTNUMMER		
V-57-6-151		

OBS
IMKANAL(F14) SKALL MONTERAS MED ETT
SKYDDSAVSTÅND MIN 100mm FRÅN
BRÄNNBART MATERIAL, KABLAR,
PLASTRÖR, TRÄMATERIAL MM

