


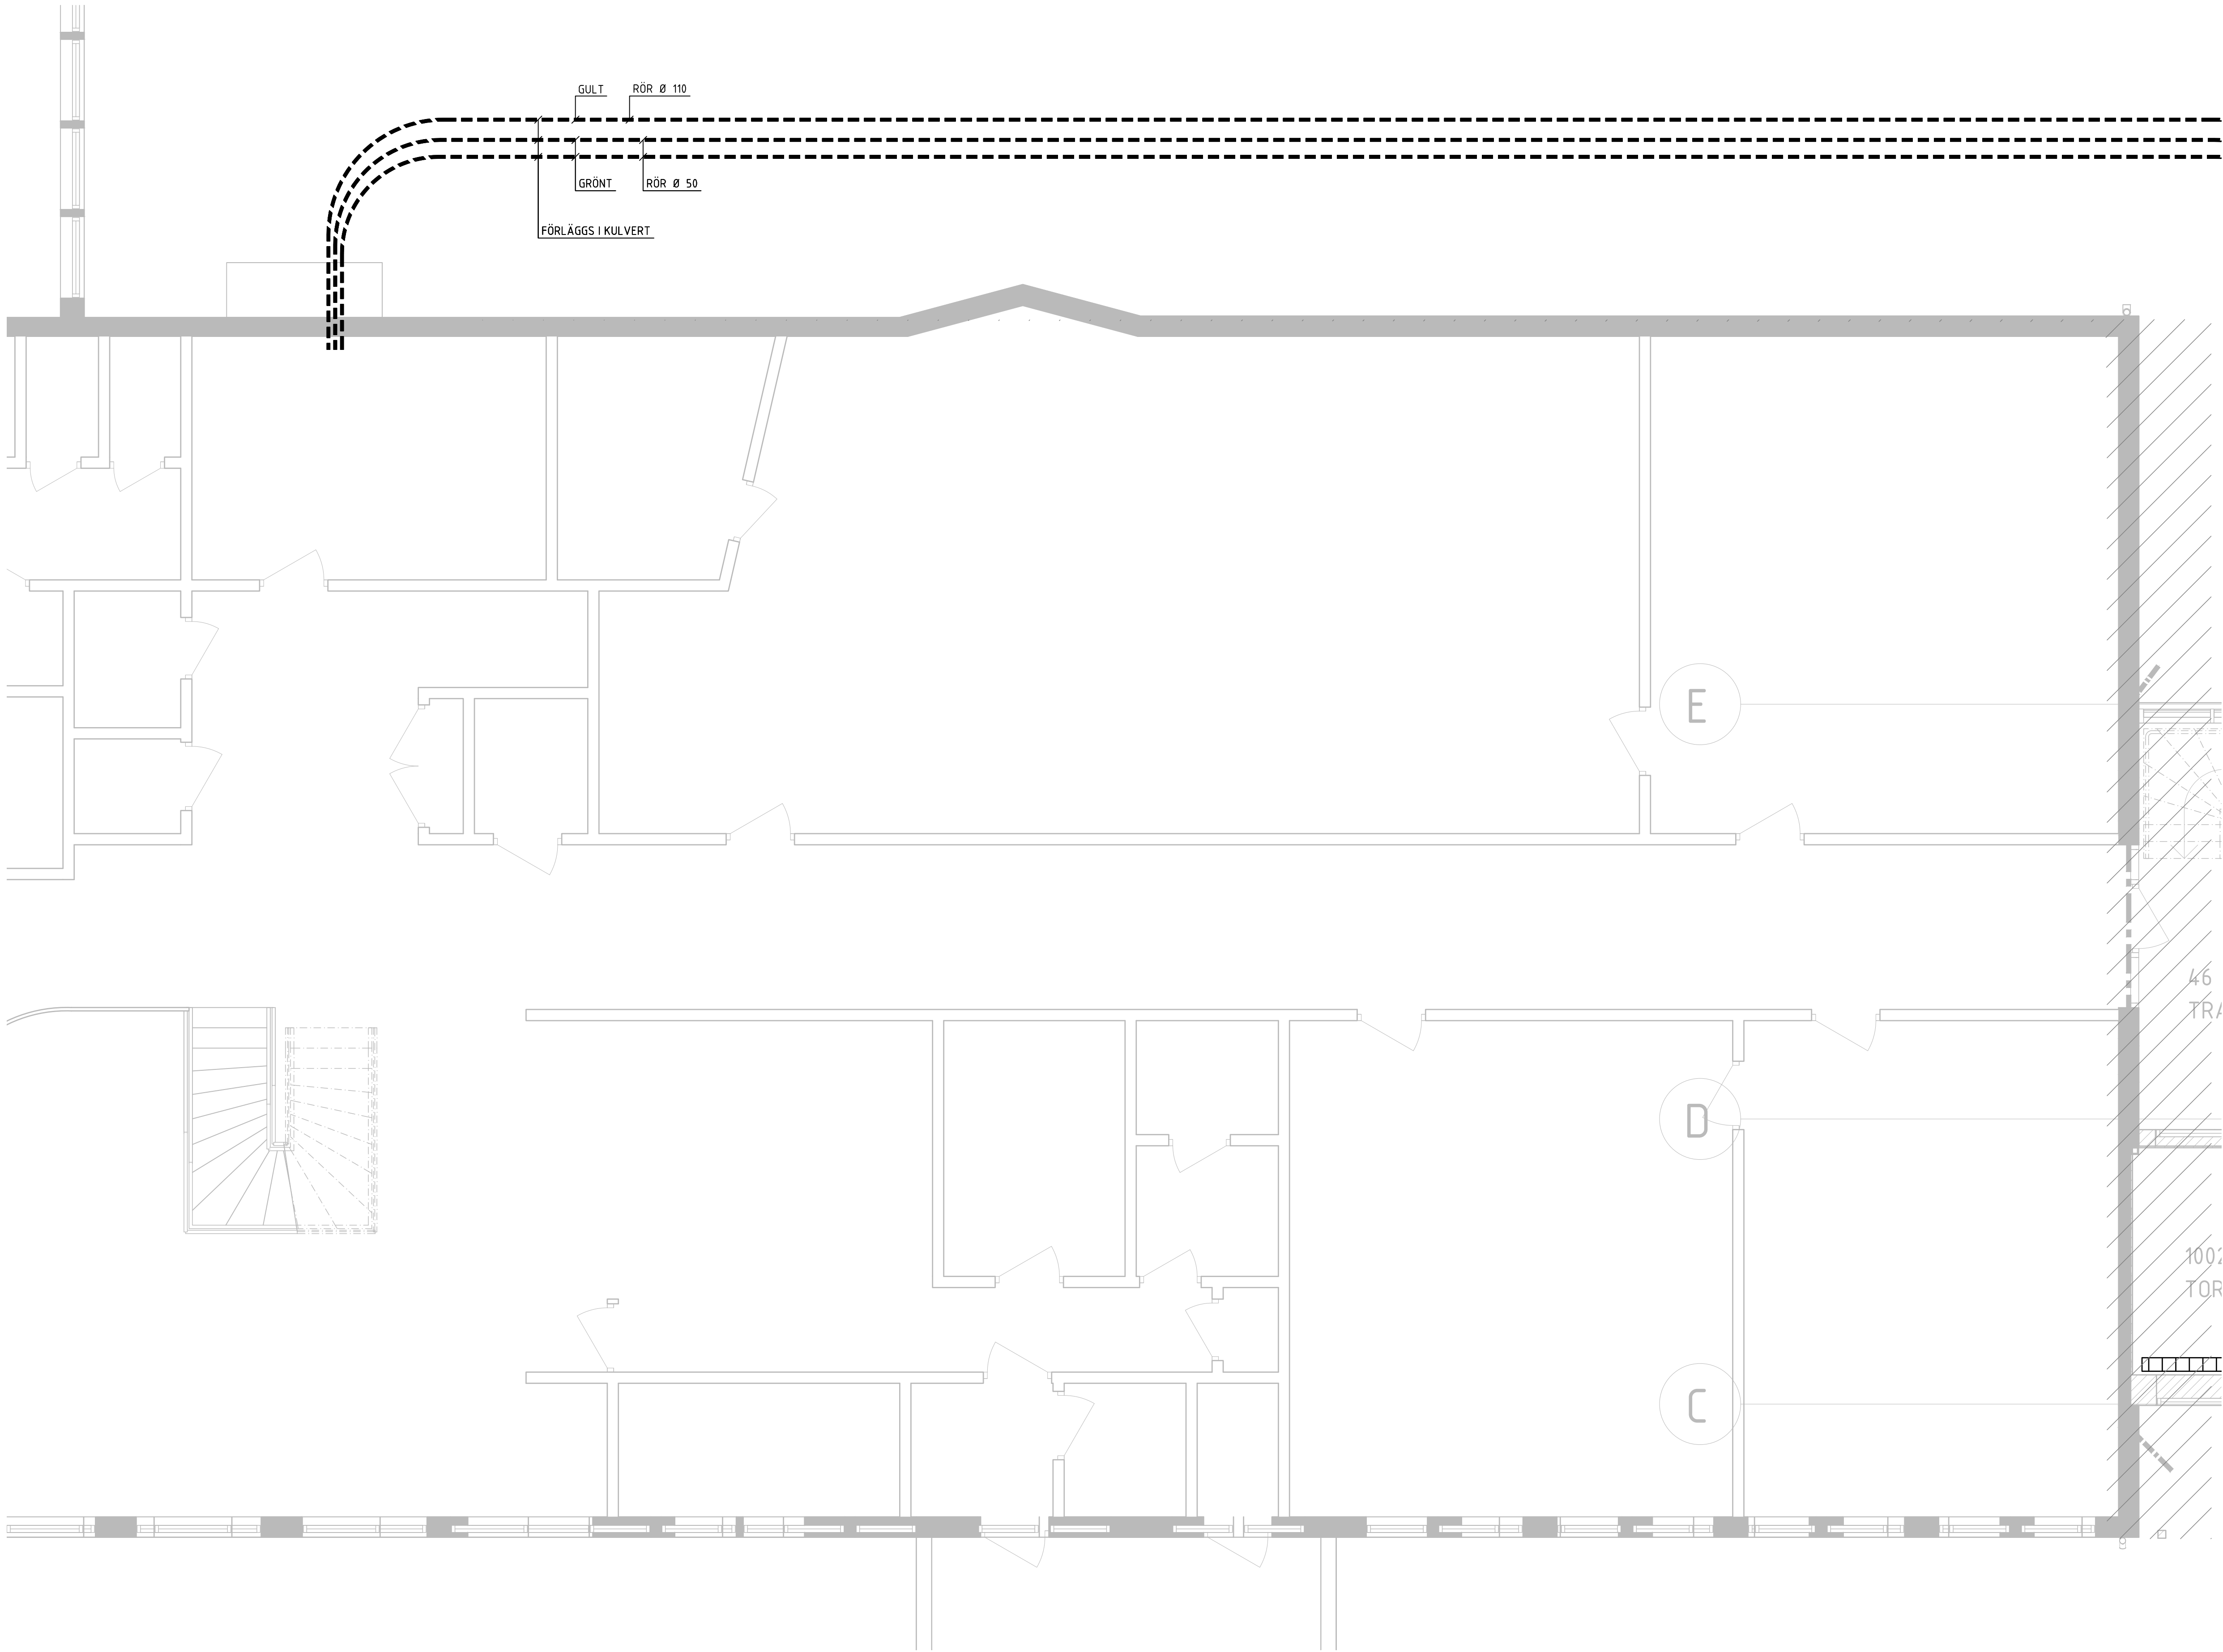



ANVISNINGAR
SAMORDNING MED ANDRA
ENTREPRENÖRER PÅ PLATS.

DÄR INGET ANNAT ANGES:
KABELSKYDDSRÖR Ø50
HALOGENFRITT MATERIAL

SYMBOLFÖRKLARINGAR

--- KABELSKYDDSRÖR ØXX

- 1 KANALISATIONEN MYNNAR I KABELGRAV
- 2 KANALISATIONEN MYNNAR VID FÖRBRUKARE
MOT VÄGG. KANALISATIONEN MYNNAR UR
PLATTAN VID FÖRBRUKARE OCH CENTRAL

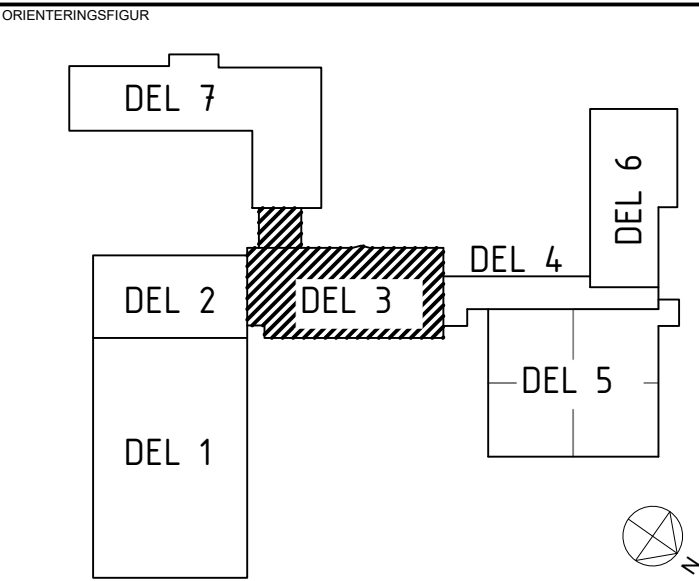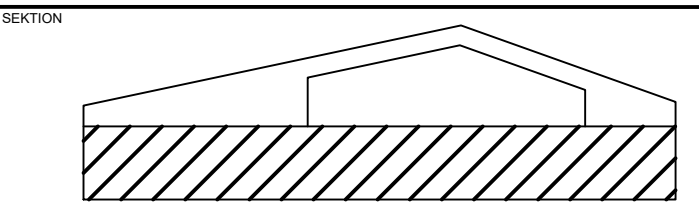

STATUS
FÖRFRÅGNINGSUNDERLAG
HANDLING
BYGGHANDLING
DATUM
2024-12-20
FÖRBERED AV
GIN
ÄNDRINGS PM
-



PROJEKTNAMN
CENTRALKÖK
OMRÅDE
ROBERTSFORS KOMMUN

PROJEKTNUMMER	YTTRE RINGVÄGEN 4	
DÅRELSNUMMER	FASTIGHET FORDONET 1	
DISCIPLIN	FÖRETAG NORCONSULT SVERIGE AB	
UPPDRAGSNUMMER	SKAPAD AV GIN	
1088371		
TELEFON	KONTAKTPERSON TOMAS BERGSTRÖM	
010 141 80 00		
BYGGNADSVÄRDE	FÖLJESKEDVÄRDE +45,54 (FG)	
VÄNINGSPLAN	VÄNINGSDEL	DELOMRÅDE
1		DEL 3

SYSTEM KANALISATION		
SPECIFIKATION PLAN 1		
BYGGNADSVÄRDE	SKALA 1:50	FORMAT A1
PLANER		ÄNDRING
DOCUMENTNUMMER E-61-1-311		-

