


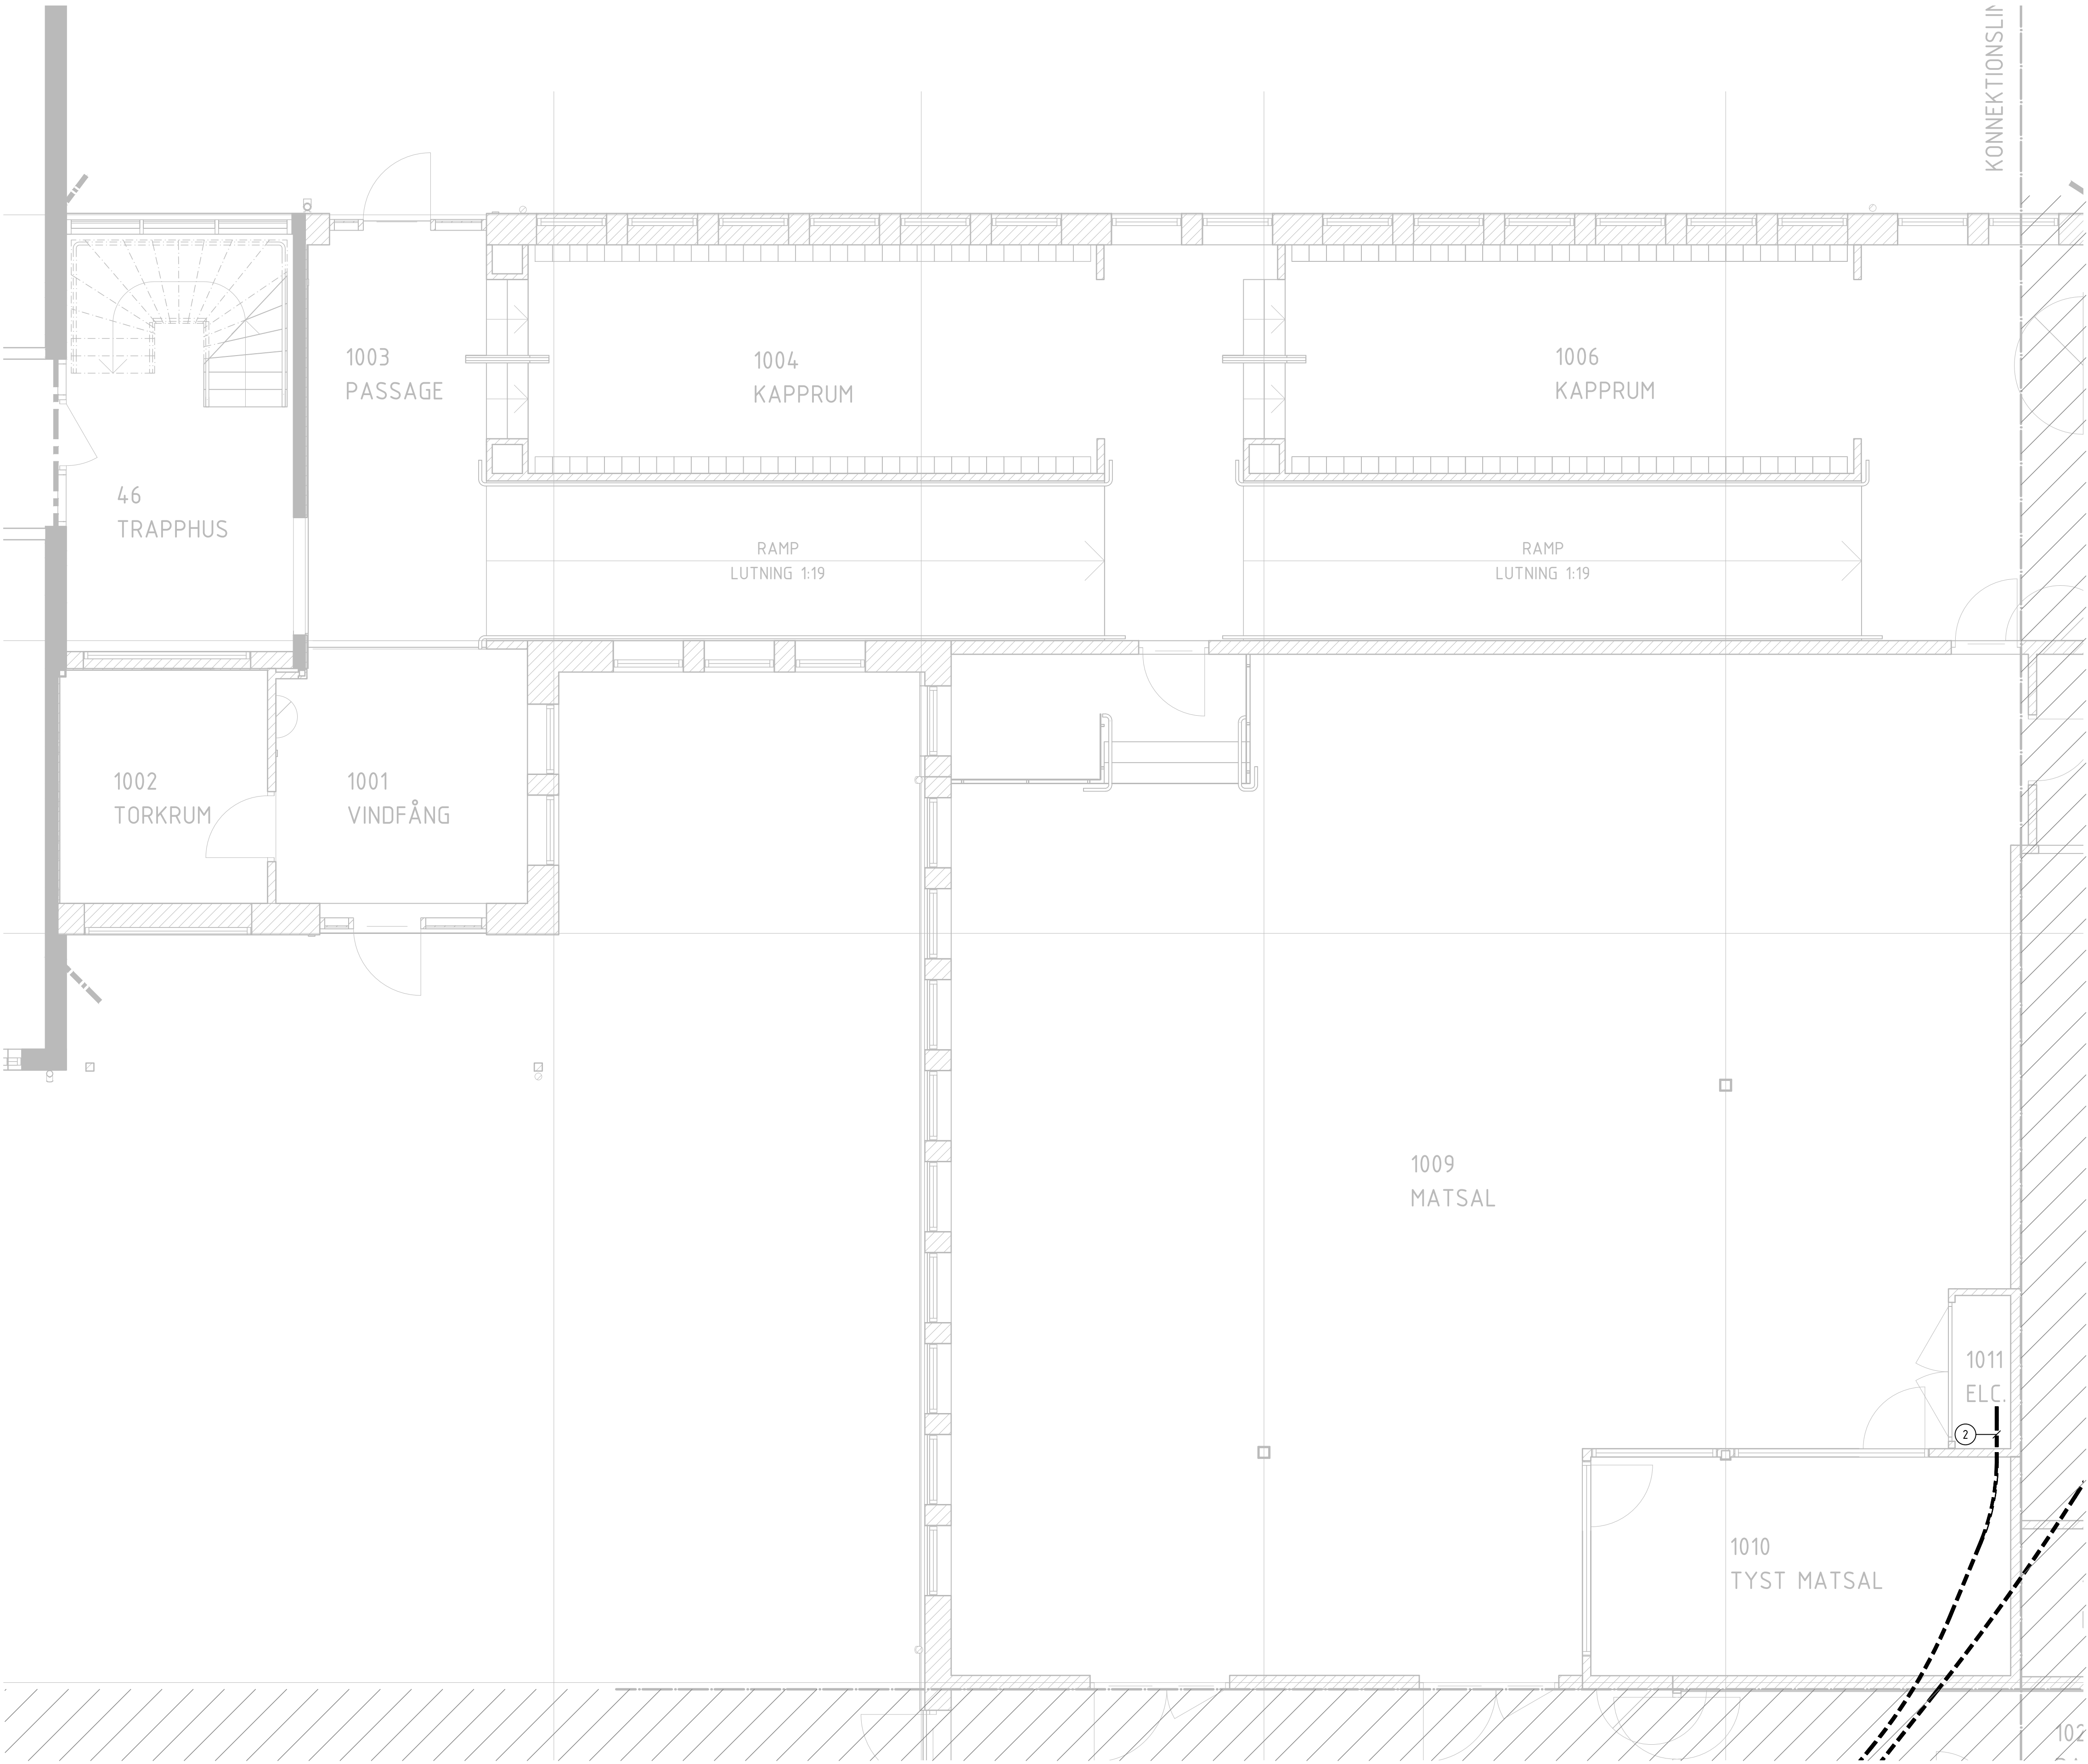



ANVISNINGAR.
SAMORDNING MED ANDRA
ENTREPRENÖRER PÅ PLATS.

DÄR INGET ANNAT ANGES:
KABELSKYDDSRÖR Ø50
HALOGENFRITT MATERIAL

SYMBOLFÖRKLARINGAR

--- KABELSKYDDSRÖR ØXX

- ① KANALISATIONEN MYNNAR I KABELGRAV
- ② KANALISATIONEN MYNNAR VID FÖRBRUKARE
MOT VÄGG. KANALISATIONEN MYNNAR UR
PLATTAN VID FÖRBRUKARE OCH CENTRAL

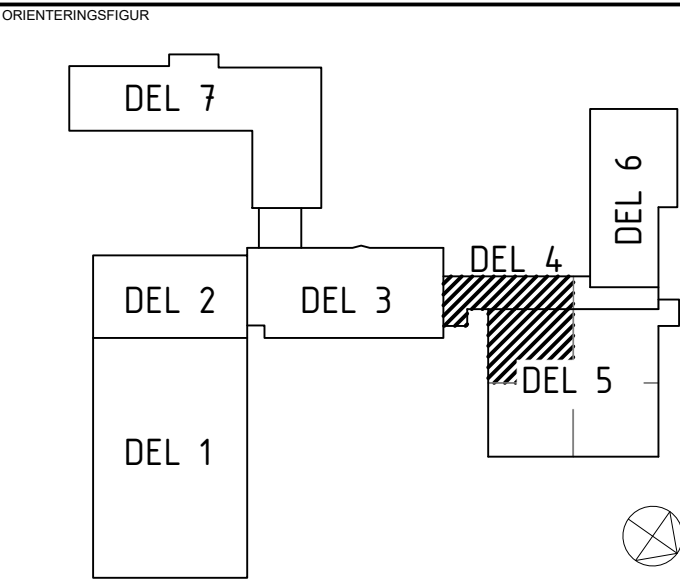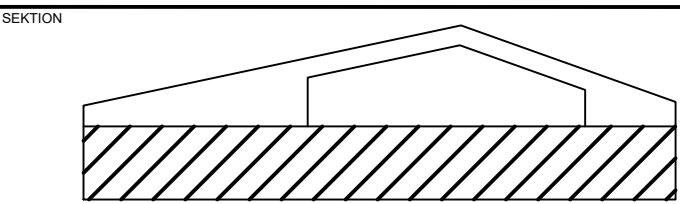

STATUS
FÖRFRÅGNINGSUNDERLAG

HANDLING
BYGGHANDLING

DATUM
2024-12-20

LOKALISERING
GIN

REKVISIT
-



PROJEKTNAMN
CENTRALKÖK

OBJEKT
ROBERTSFORS KOMMUN

PROJEKTNUMMER
YTTRE RINGVÄGEN 4

DIREKTÖR
FORDONET 1

DISCIPLIN
NORCONSULT SVERIGE AB

UPPDRAGSNUMMER
1088371

TELEFON
010 141 80 00

BYGGNADSVÄRDE
+45,54 (FG)

VÄNINGSPLAN
1

VÄNINGSDEL
DEL 4.1, 5.1

SYSTEM
KANALISATION

SPESIFIKATION
BOTTENPLATTA

PLANER
E-61-1-501

