


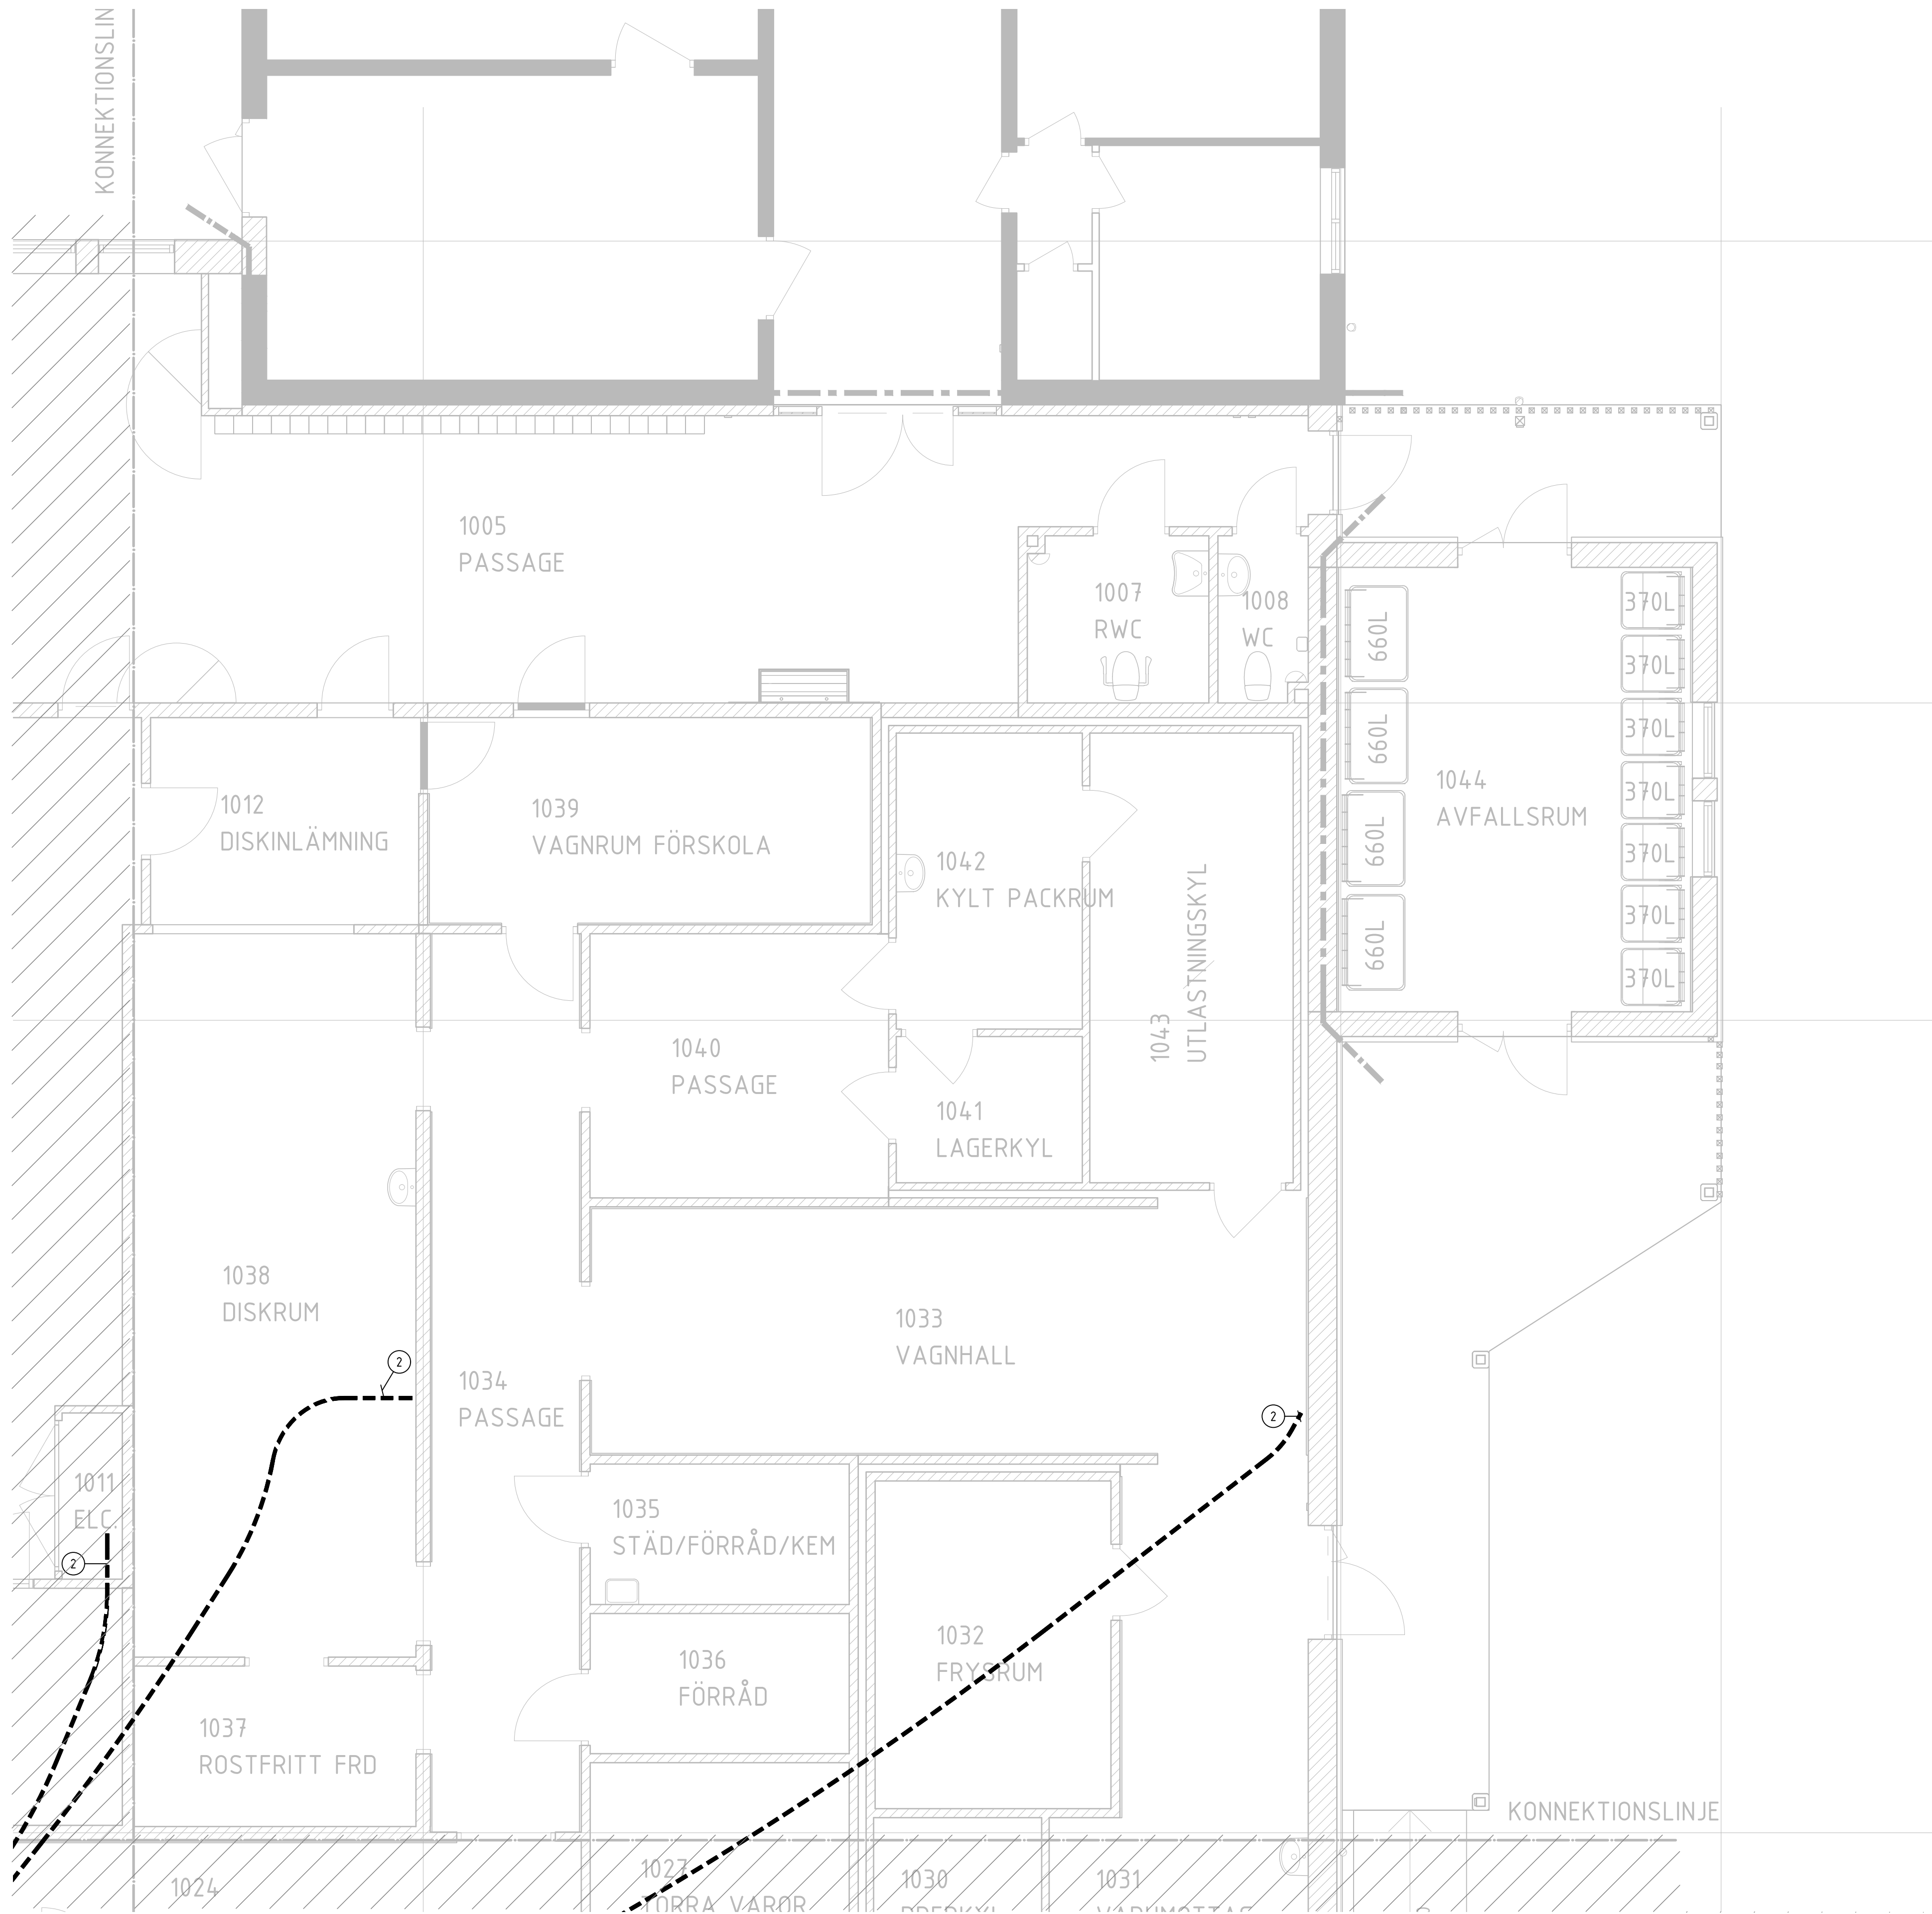

ANVISNINGAR.
SAMORDNING MED ANDRA
ENTREPRENÖRER PÅ PLATS.

DÄR INGET ANNAT ANGES:
KABELSKYDDSRÖR 450
HALOGENFRITT MATERIAL

SYMBOLFÖRKLARINGAR

--- KABELSKYDDSRÖR ØXX

- ① KANALISATIONEN MYNNAR I KABELGRAV
② KANALISATIONEN MYNNAR VID FÖRBRUKARE
MOT VÄGG. KANALISATIONEN MYNNAR UR
PLATTAN VID FÖRBRUKARE OCH CENTRAL

SEKTION

ORIENTERINGSFIGUR

STATUS

HANDLING

DATUM

LODPAKAD AV

ÄNDRINGS PM

BESTÄLLARE

PROJEKTNAMN

OMRÅDE

PROJEKTNUMMER

ADRESS

DIREKTOR

FASTIGHET

DISCIPLIN

FÖRETAG

UPPDRAGSNUMMER

SKAPAD AV

TELEFON

KONTAKTPERSON

BYGGNADSVÄRDE

PLANSKYDDSVÄRDE

YNNINGSPLAN

VANNINGDE

DELOMRÅDE

SYSTEM

SPECIFICATION

FORMAT

SKALA

ÄNDRING

DOCUMENTNUMMER

FÖRFRÅGNINGSUNDERLAG

BYGGHANDLING

2024-12-20

GIN

-

ROBERTSFORS
KOMMUN

CENTRALEKÖK

ROBERTSFORS KOMMUN

YTTRE RINGVÄGEN 4

FORDONET 1

NORCONSULT SVERIGE AB

GIN

010 141 80 00

TOMAS BERGSTRÖM

+45,54 (FG)

DEL 4,2, 5,2

KANALISATION

BOTTENPLATTA

PLANER

E-61-1-502

1:50

A1

-

