



ANVISNINGAR
SAMORDNING MED ANDRA
ENTREPRENÖRER PÅ PLATS.

DÄR INGET ANNAT ANGES:
KABELSKYDDSRÖR Ø50
HALOGENFRITT MATERIAL

SYMBOLFÖRKLARINGAR

--- KABELSKYDDSRÖR ØXX

- ① KANALISATIONEN MYNNAR I KABELGRAV
② KANALISATIONEN MYNNAR VID FÖRBRUKARE
MOT VÄGG. KANALISATIONEN MYNNAR UR
PLATTAN VID FÖRBRUKARE OCH CENTRAL

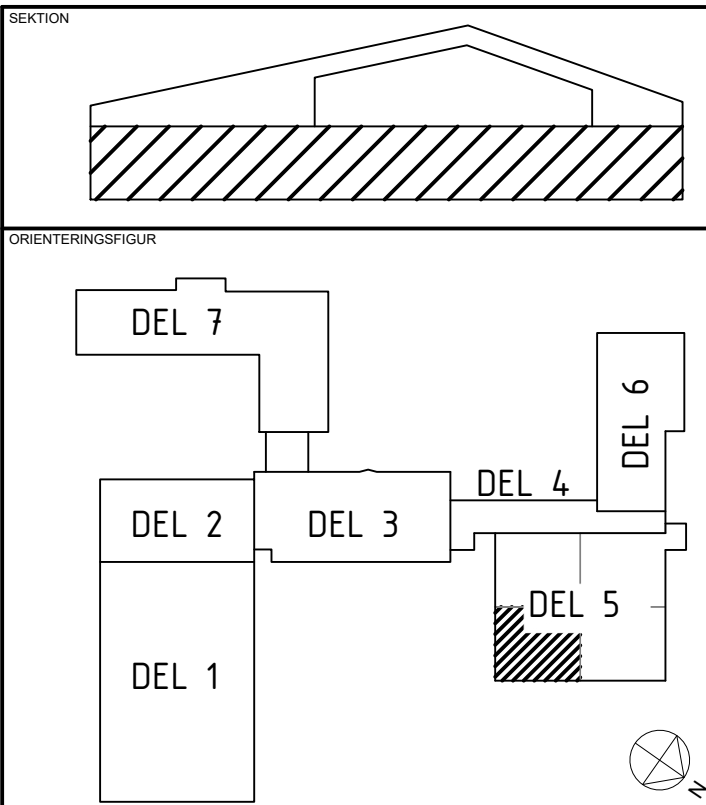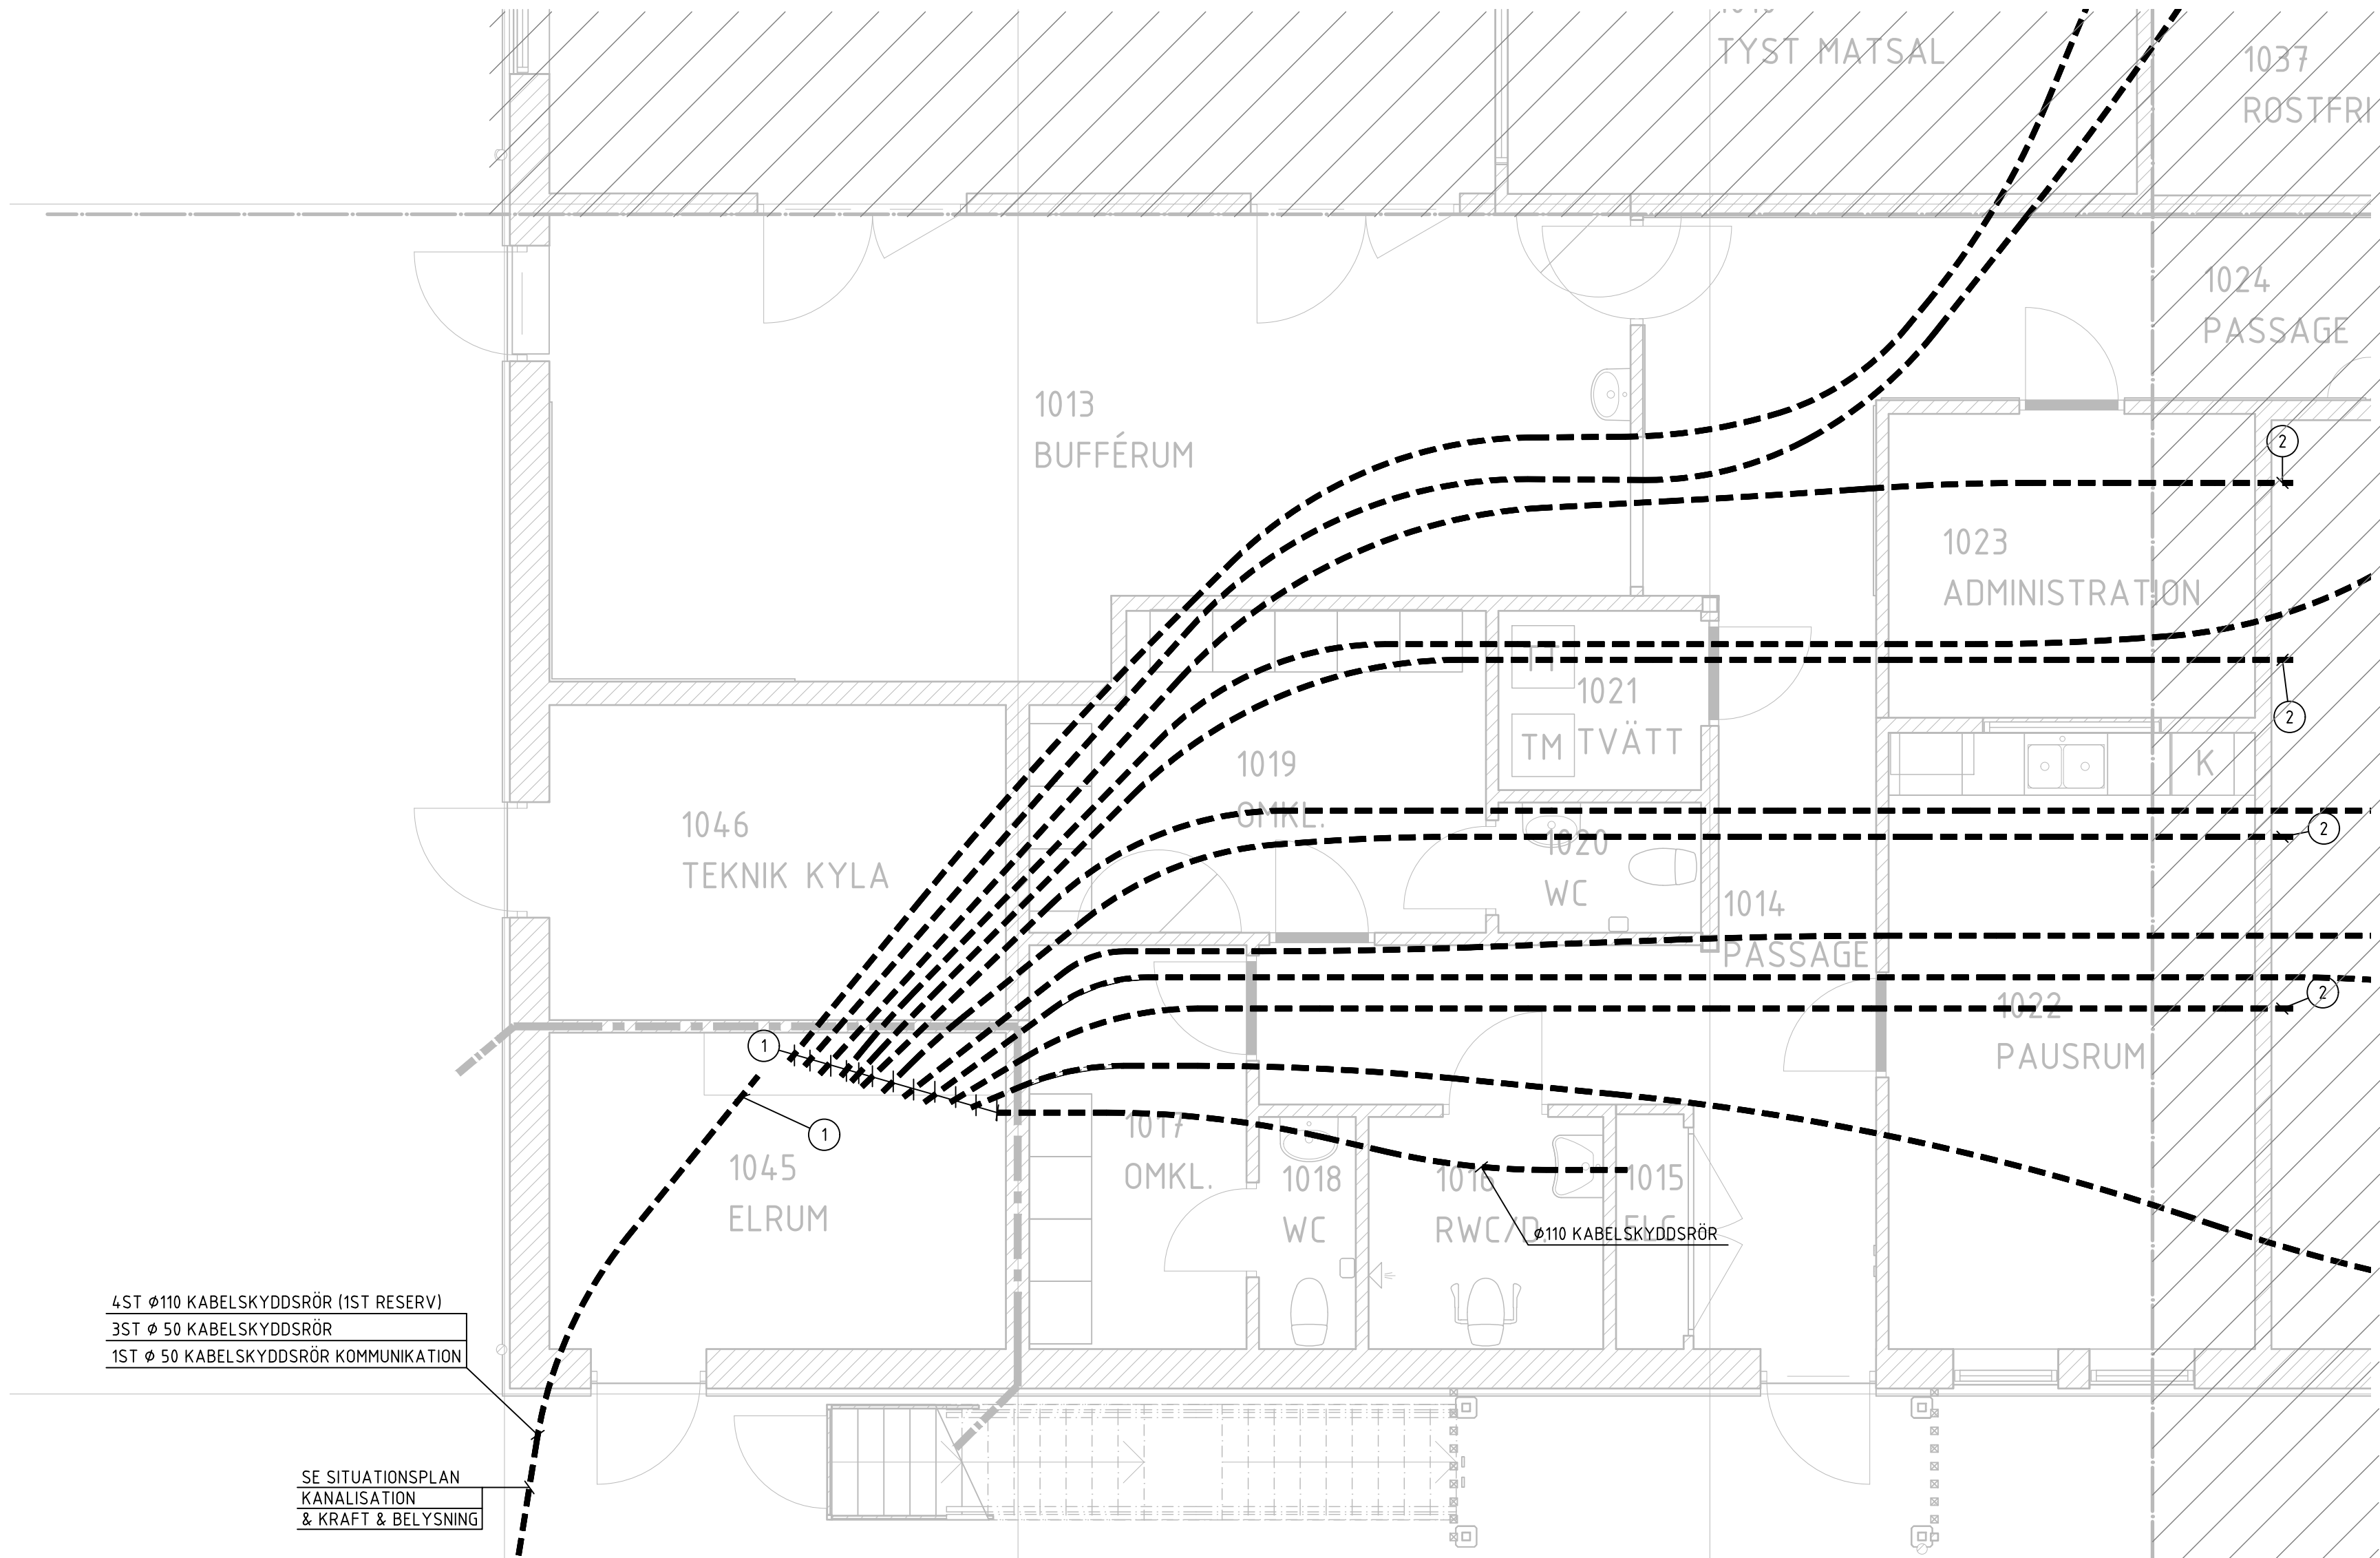

STATUS
FÖRFRÅGNINGSUNDERLAG
HANDLING
BYGGHANDLING
DATUM
2024-12-20
TECKNAD AV
GIN
ÄNDRINGS PM
-



PROJEKTNAMN CENTRAALKÖK		
OMRÅDE ROBERTSFORS KOMMUN		
PROJEKTNUMMER	ADRESS YTTRE RINGVÄGEN 4	
DÄRRETNAMN	FASTIGHET FORDONET 1	
DISCIPLIN	FÖRETAG NORCONSULT SVERIGE AB	
UPPDRAGSNUMMER 1088371	SKAPAD AV GIN	
TELEFON 010 141 80 00	KONTAKTPERSON TOMAS BERGSTRÖM	
BYGGNADSVÄRDE	FÖLJESKEDVÄRDE +45,54 (FG)	
VÄNINGSPLAN 1	VÄNINGSDEL	DELOMRÅDE DEL 5.3
SYSTEM KANALISATION		
SPECIFICATION BOTTENPLATTA		
TECKNINGSSTADIER PLANER	SKALA 1:50	FORMAT A1
DOCUMENTNUMMER E-61-1-503	ÄNDRING -	