



ANVISNINGAR
SAMORDNING MED ANDRA
ENTREPRENÖRER PÅ PLATS.

DÄR INGET ANNAT ANGES:
KABELSKYDDSRÖR 450
HALOGENFRITT MATERIAL

SYMBOLFÖRKLARINGAR

--- KABELSKYDDSRÖR ØXX

- ① KANALISATIONEN MYNNAR I KABELGRAV
② KANALISATIONEN MYNNAR VID FÖRBRUKARE
MOT VÄGG. KANALISATIONEN MYNNAR UR
PLATTAN VID FÖRBRUKARE OCH CENTRAL

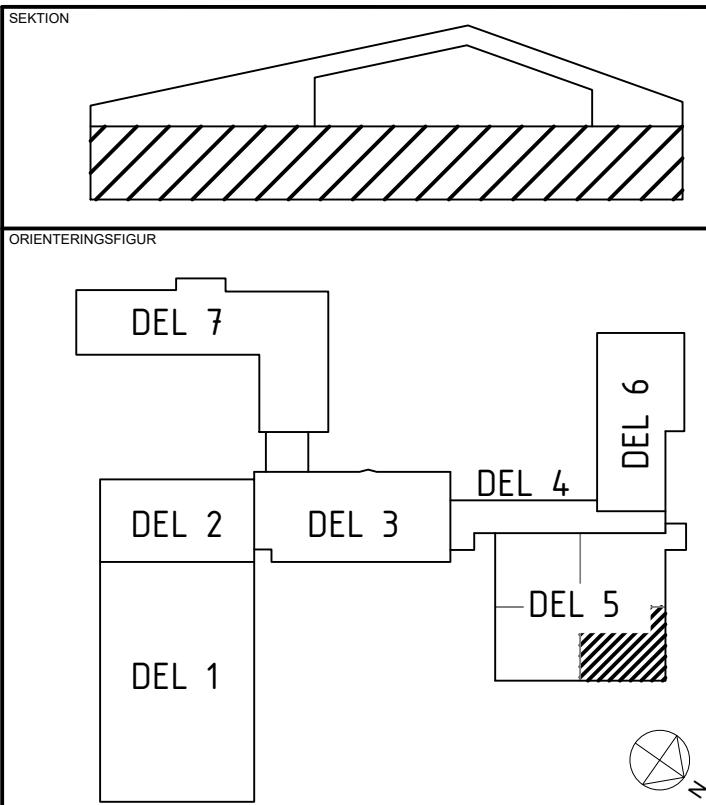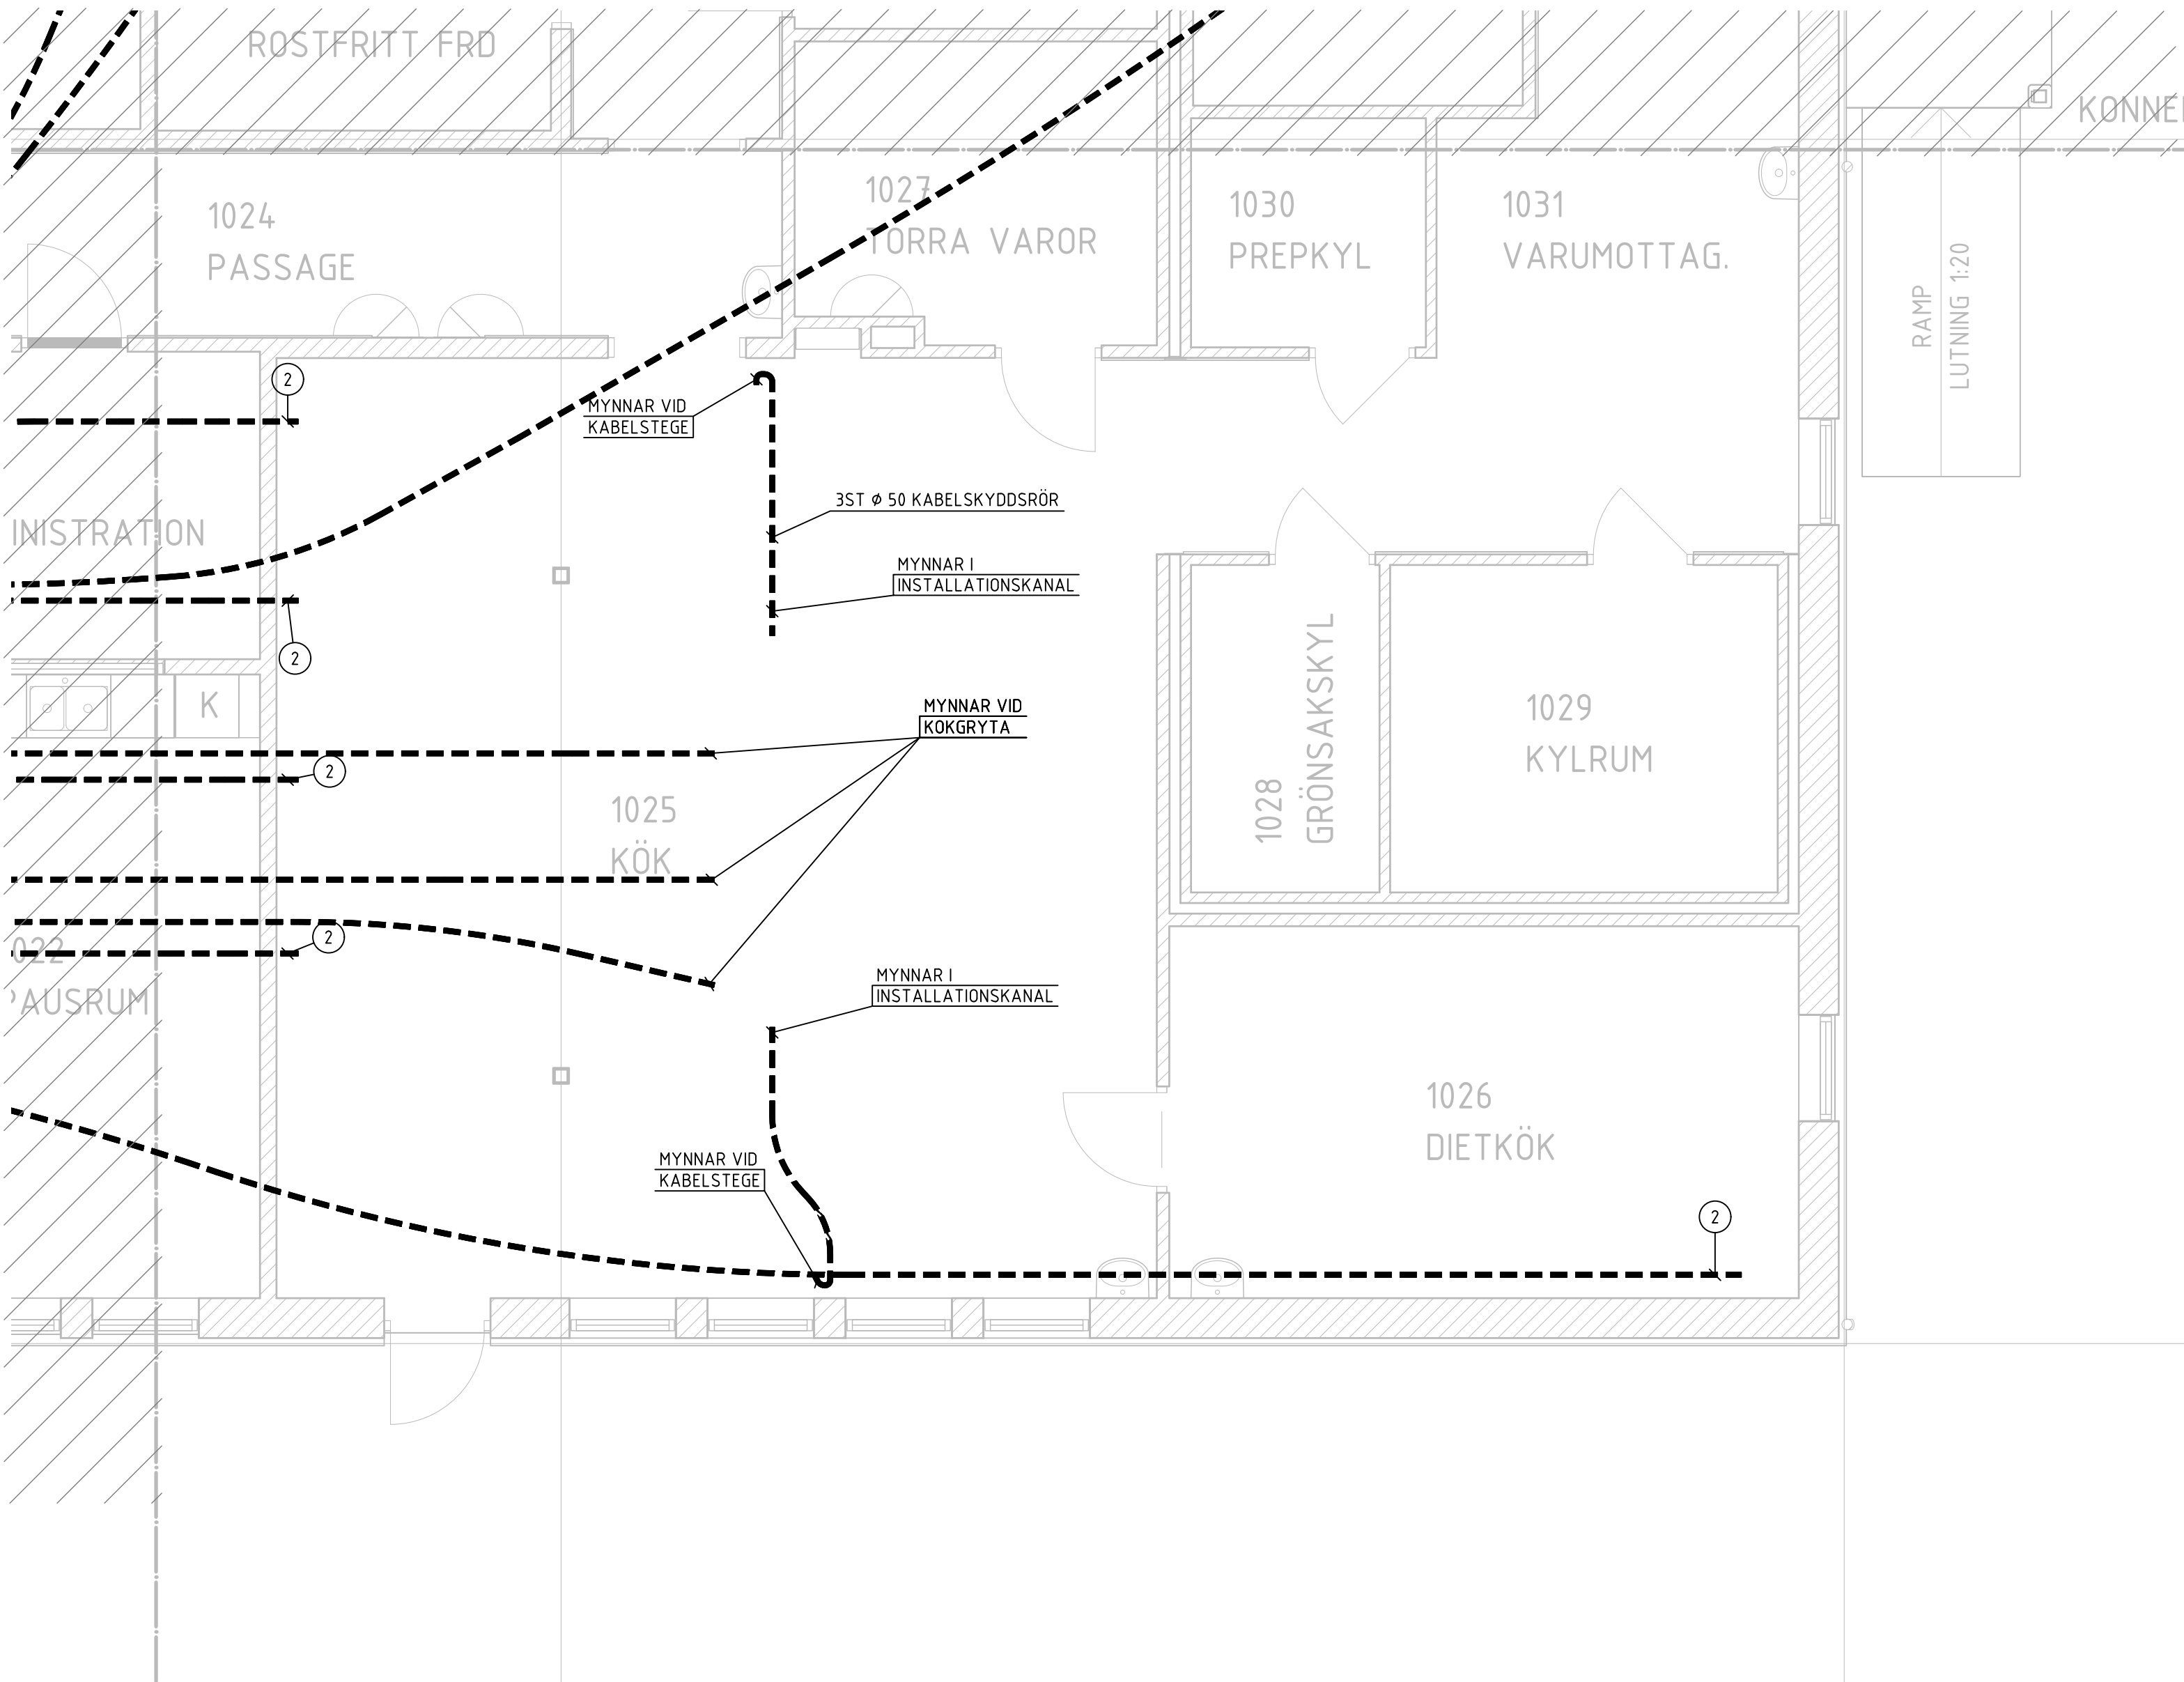

STATUS
FÖRFRÅGNINGSUNDERLAG
HANDLING
BYGGHANDLING
DATUM
2024-12-20
TIOGRAND AV
GIN
ÄNDRINGS PM
-



ROBERTSFORS
KOMMUN

PROJEKTNAMN
CENTRAALKÖK
OMRÅDE
ROBERTSFORS KOMMUN
PROJEKTNUMMER
ADRESS
YTTRE RINGVÄGEN 4
DÄRRETNUMMER
FASTIGHET
FORDONET 1
DISCIPLIN
FÖRETAG
NORCONSULT SVERIGE AB
UPPDRAGSNUMMER
1088371
SKAPAD AV
GIN
TELEFON
010 141 80 00
KONTAKTPERSON
TOMAS BERGSTRÖM
BYGGNADSVÄRK
+45,54 (FG)
VÄNINGSPLAN
1
VÄNINGSDEL
DELOMRÅDE
DEL 5.4
SYSTEM
KANALISATION
SPECIFICATION
BOTTENPLATTA
TITEL
PLANER
SKALA
1:50
FORMAT
A1
DOKUMENTNUMMER
E-61-1-504
ÄNDRING
-