


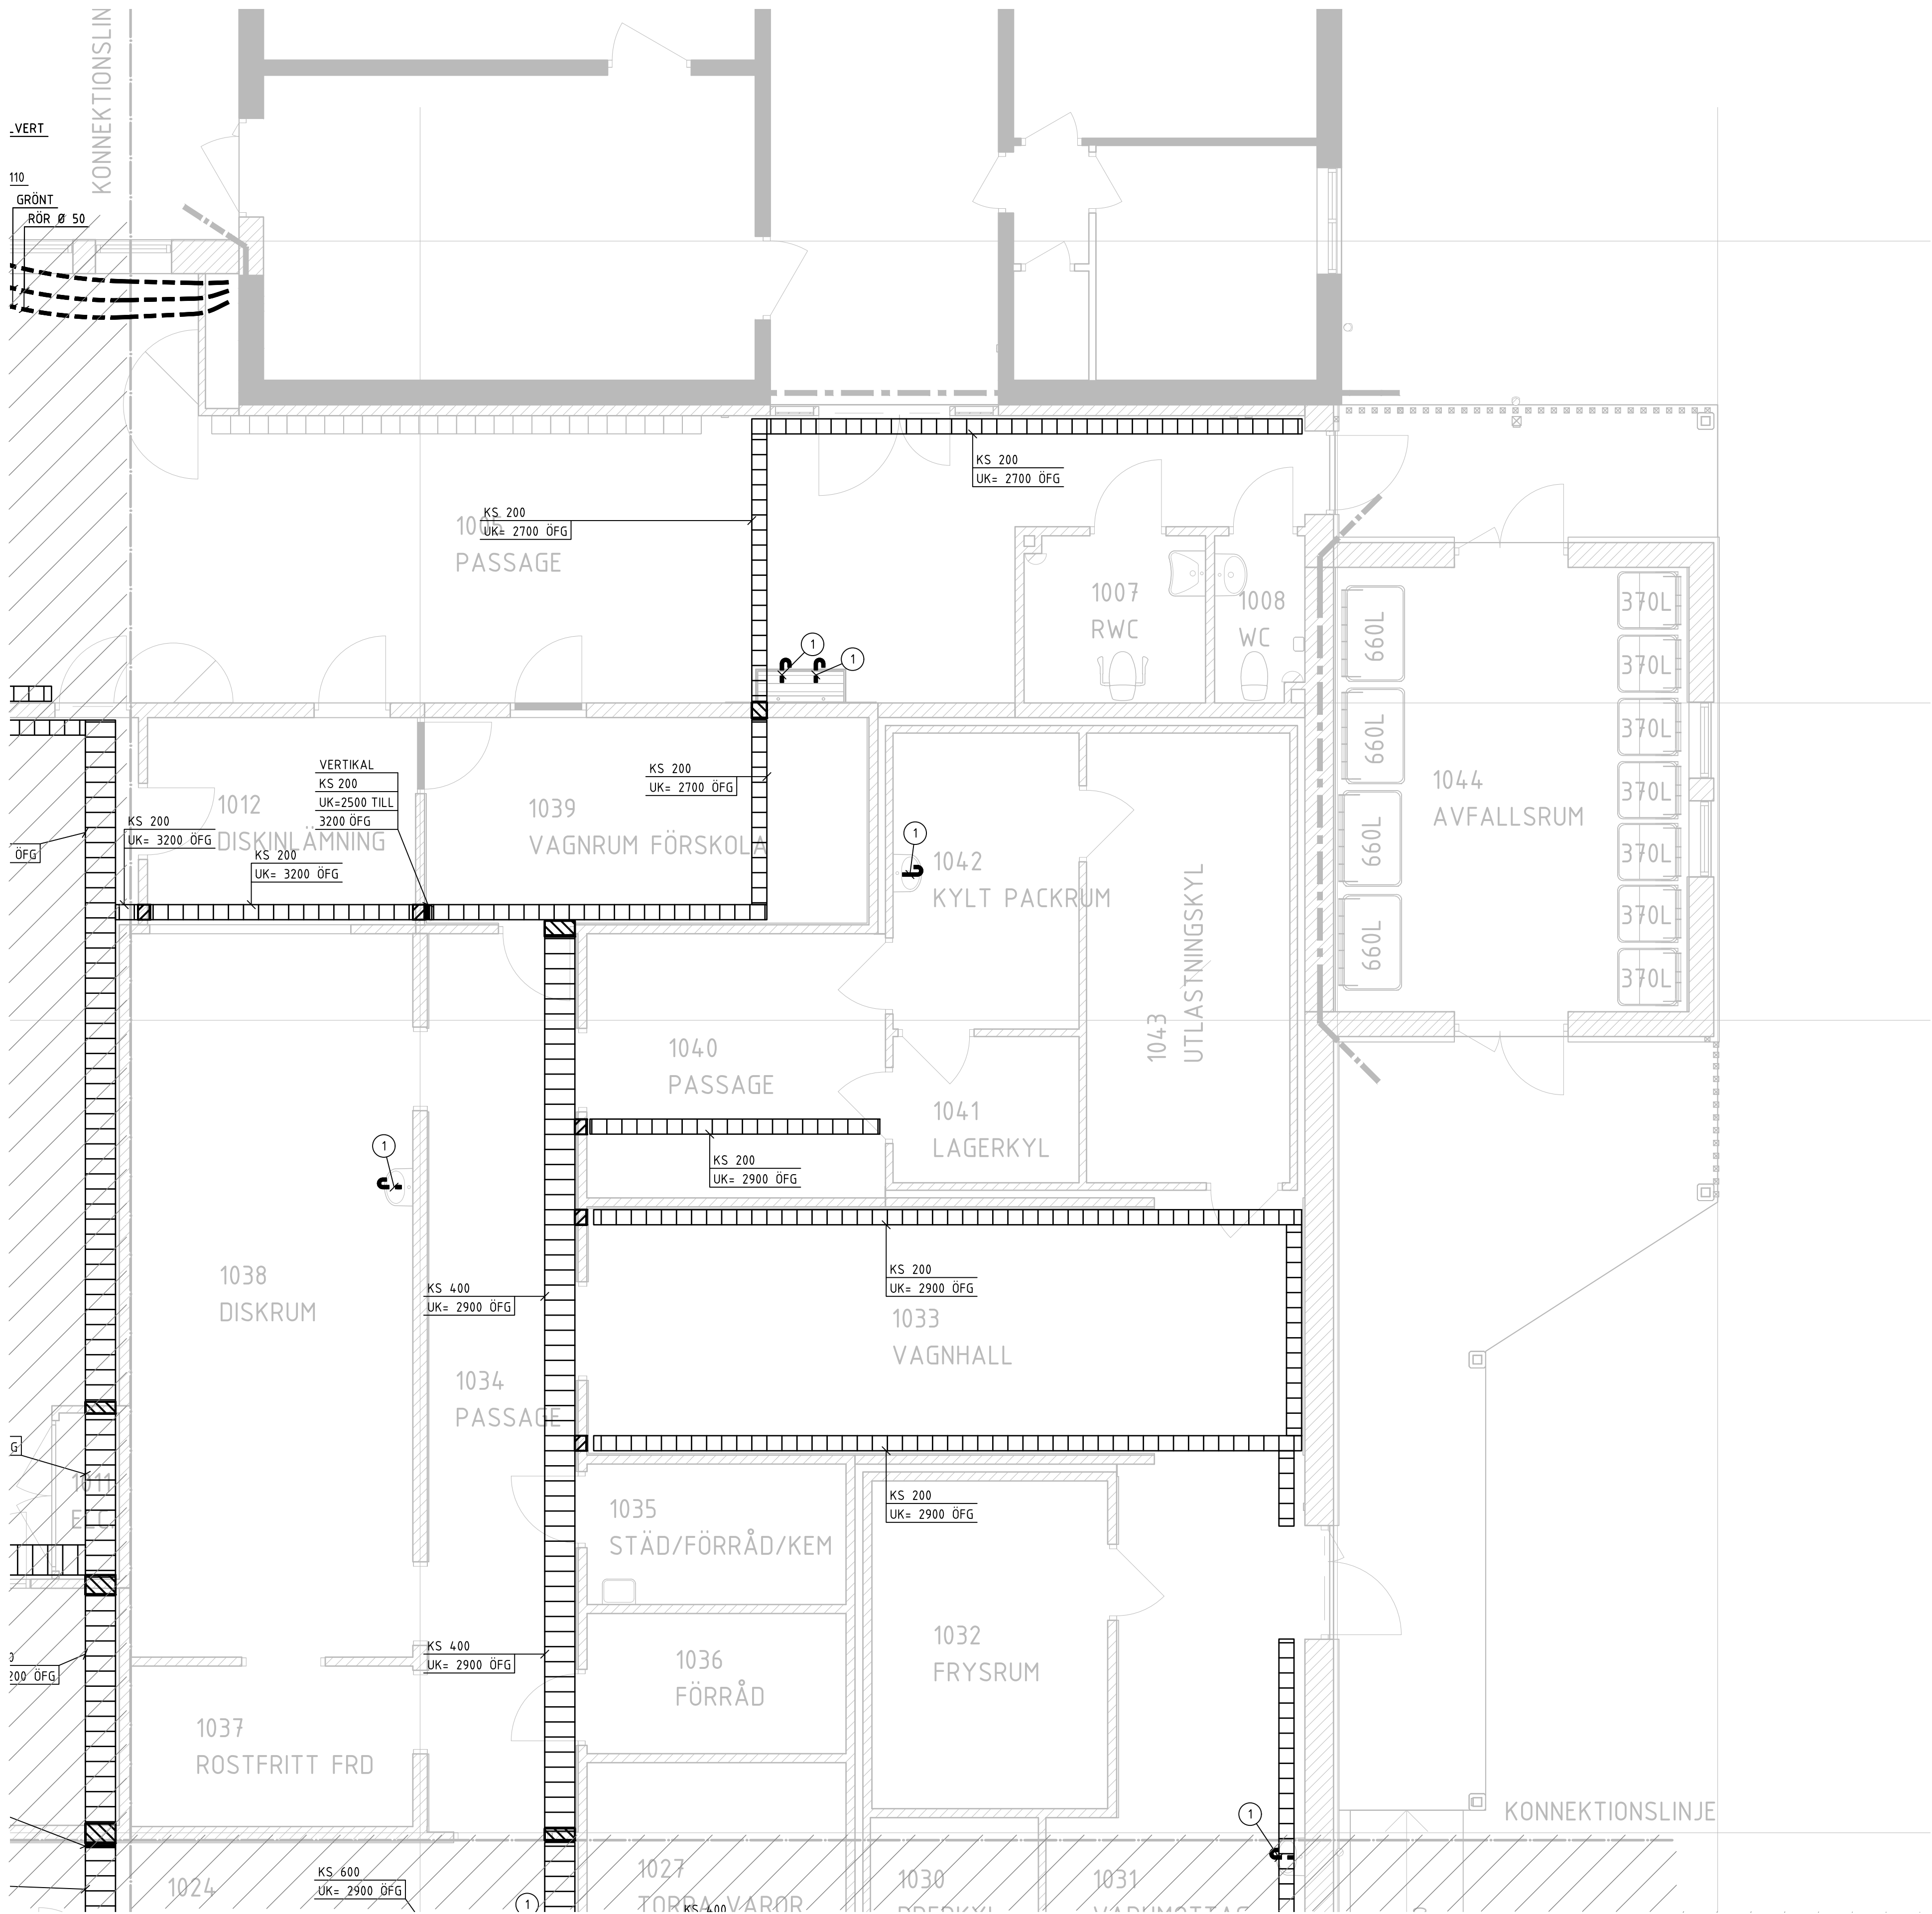


ANVISNINGAR
SAMORDNING MED ANDRA
ENTREPRENÖRER PÅ PLATS.
HÖJD ANGES I MM ÖFG

SYMBOLFÖRKLARINGAR

- KABELSTEGE, MED STORLEK
- VERTIKALKABELSTEGE, MED STORLEK
- FÖNSTERBÄNKSANAL, FBK
- VERTIKAL FÖNSTERBÄNKSANAL
- FLEXRÖR ØXX

- Ø16 RÖR MYNNAR UNDER HANDFAT OCH OVAN
UNDERTAK FÖR AUTOMATISK BLANDARE
- Ø16 RÖR MYNNAR +15 PÅ VÄGG OCH OVAN
UNDERTAK, FÖR TERMOSTATER
- TELEDOSA TYP E14-20700 MED TÄCKLOCK E14-20710
OCH MONTAGEPLÅT E14-20714.
MONTERAS I VÄGG BAKOM BILDSKÄRM.
- KABELSKYDDSRÖR 1 ST Ø50MM, 1 ST Ø32MM,
1 ST Ø25MM OCH 2 ST Ø20MM.
FÖRLÄGGS I VÄGG MELLAN TELEDOSA OCH KABEL-
STEGE.

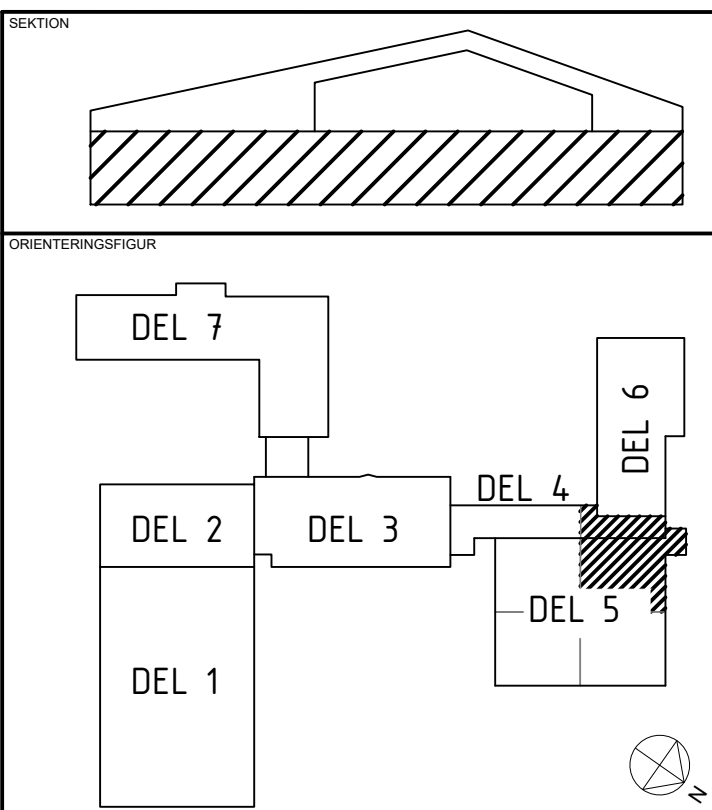

STATUS
FÖRFRÅGNINGSUNDERLAG

HANDLING
BYGGHANDLING

DATA
2024-12-20

LOKALISERING
GIN

ÄNDRINGAR
-



PROJEKTNAMN
CENTRALEK

ORDBÄRIG
ROBERTSFORS KOMMUN

PROJEKTNUMMER
YTTERE RINGVÄGEN 4

FASTIGHET
FORDONET 1

DISCIPLIN
E

FÖRETAG
NORCONSULT SVERIGE AB

UPPDRAGSNUMMER
1088371

SKAPAD AV
GIN

TELEFON
010 141 80 00

KONTAKTPERSON
TOMAS BERGSTRÖM

BYGGKOSTNAD
+45,54 (FG)

VÄNINGSPLAN
1

VÄNINGSDEL
DEL 4,2, 5,2

SYSTEM
KANALISATION

SPECIFIKATION
PLAN 1

SKALA
1:50

FORMAT
A1

ÄNDRINGAR
-

DOCUMENTNUMMER
E-61-1-512

