
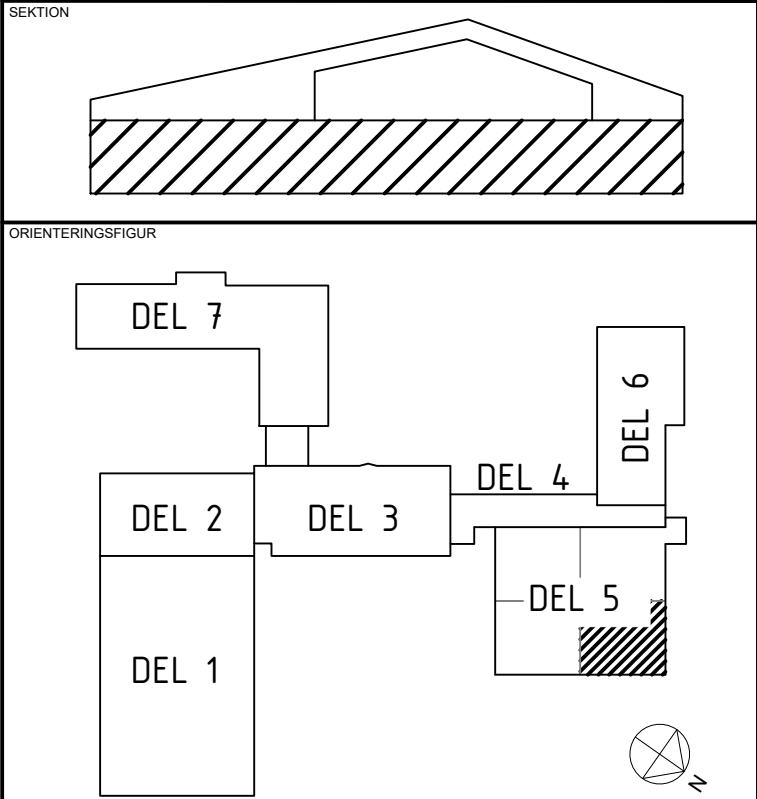
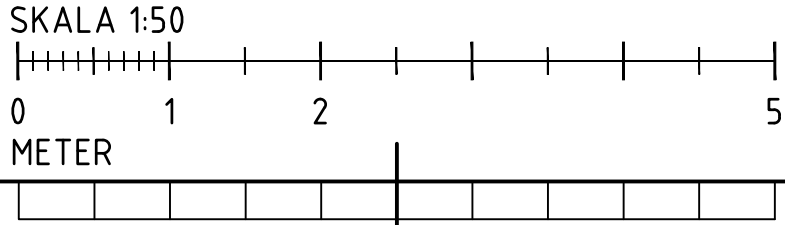


ANVISNINGAR
SAMORDNING MED ANDRA
ENTREPRENÖRER PÅ PLATS.
HÖJD ANGES I MM ÖFG

SYMBOLFÖRKLARINGAR

- ▬ KABELSTEGE. MED STORLEK
- ▬ VERTIKALKABELSTEGE. MED STORLEK
- ▬ FÖNSTERBÄNKKANAL, FBK
- ▬ VERTIKAL FÖNSTERBÄNKKANAL
- FLEXRÖR ØXX

- ① Ø16 RÖR MYNNAR UNDER HANDFAT OCH OVAN
UNDERTAK FÖR AUTOMATISK BLANDARE
- ② Ø16 RÖR MYNNAR +15 PÅ VÄGG OCH OVAN
UNDERTAK, FÖR TERMOSTATER
- ③ TELEDOSA TYP E14-20700 MED TÄCKLOCK E14-20710
OCH MONTAGEPLÅT E14-20714.
MONTERAS I VÄGG BAKOM BILDSKÄRM.
- ④ KABELSKYDDSRÖR 1 ST Ø50MM, 1 ST Ø32MM,
1 ST Ø25MM OCH 2 ST Ø20MM.
FÖRLÄGGS I VÄGG MELLAN TELEDOSA OCH KABEL-
STEGE.

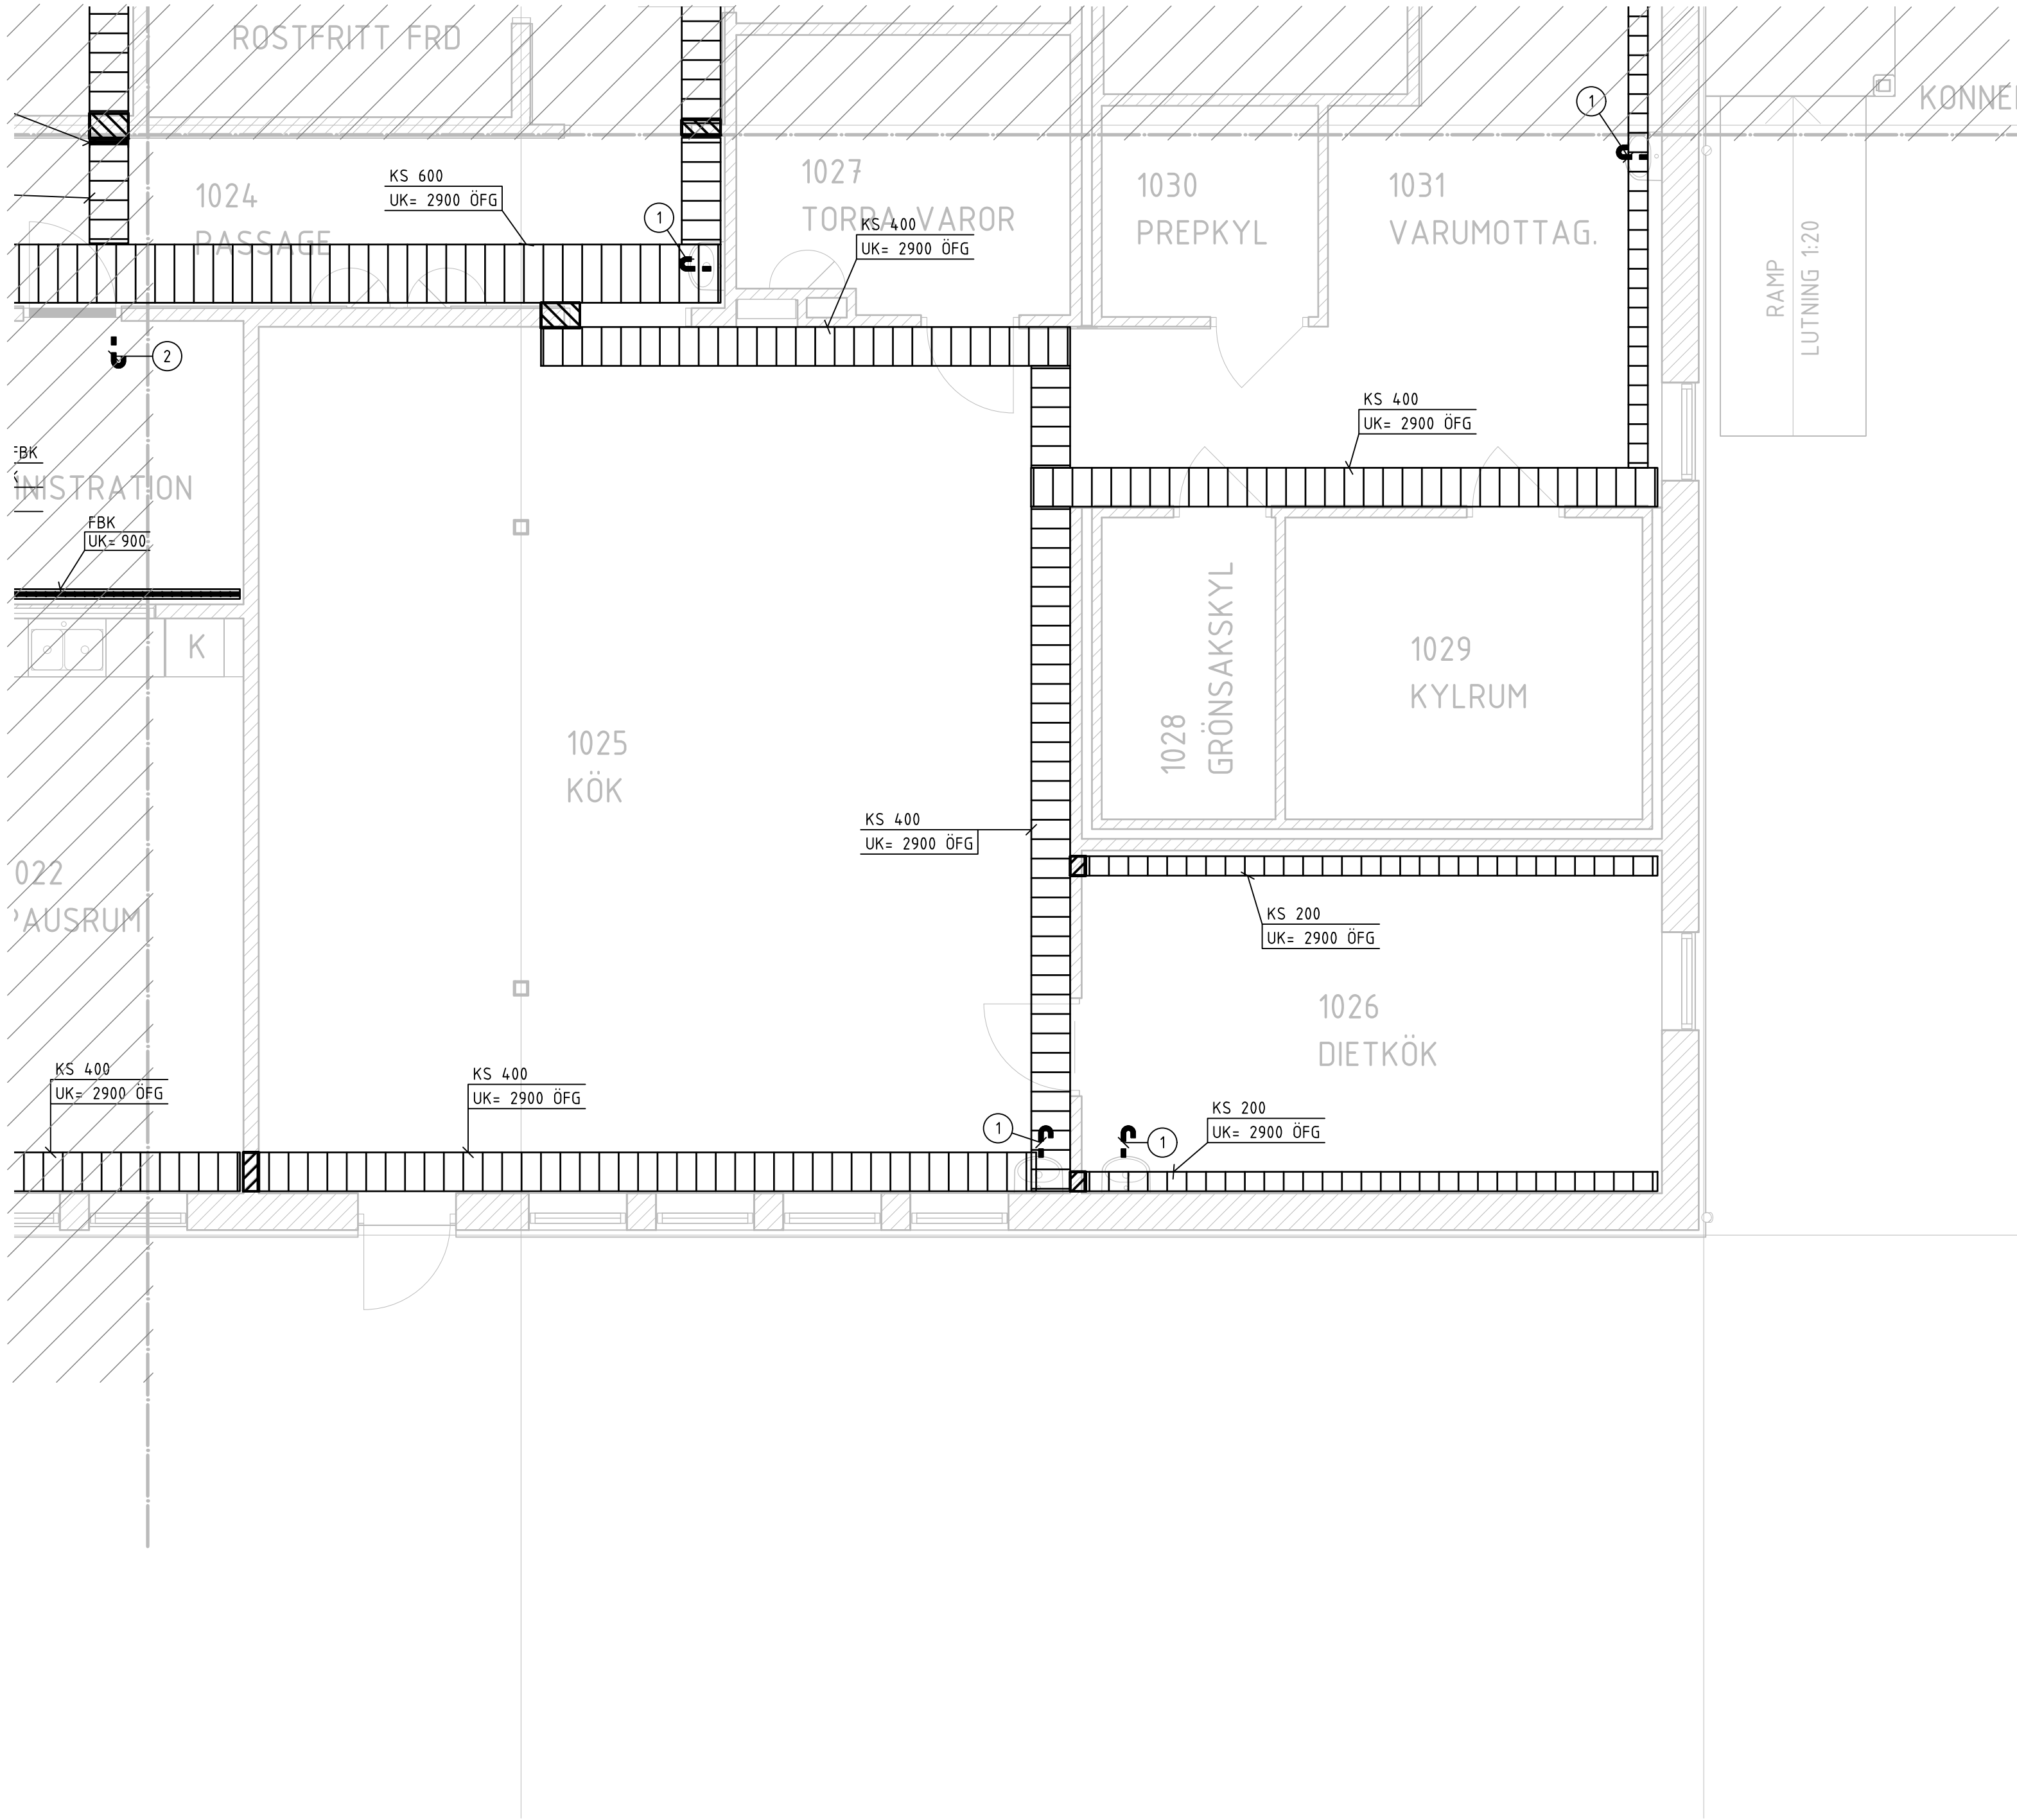

STATUS		
FÖRFRÅGNINGSUNDERLAG		
HANDLING		
BYGGHANDLING		
DATUM	2024-12-20	LODPAKAD AV
BYGGHÄRRE	GIN	ÄNDRINGS PM
BESTÄLLARE		
 ROBERTSFORS KOMMUN		
PROJEKTNAMN		
CENTRALKÖK		
OBJEKT		
ROBERTSFORS KOMMUN		
PROJEKTNUMMER	YTTRE RINGVÄGEN 4	
DÄRRETNUMMER	FASTIGHET	
DISCIPLIN	FORDONET 1	
UPPDRAGSNUMMER	NORCONSULT SVERIGE AB	
1088371	SKAPAD AV	
TELEFON	GIN	
BYGGHÄRRE	KONTAKTPERSON	
010 141 80 00	TOMAS BERGSTRÖM	
BYGGHÄRRE	FÖLJESKIVAN (2024)	
BYGGHÄRRE	+45,54 (FG)	
VÄNINGSPLAN	VÄNINGSDEL	DELOMRÅDE
1		DEL 5.4
SYSTEM		
KANALISATION		
SPECIFIKATION		
PLAN 1		
BYGGHÄRRE	SKALA	FORMAT
PLANER	1:50	A1
BYGGHÄRRE	ÄNDRING	
E-61-1-514		-