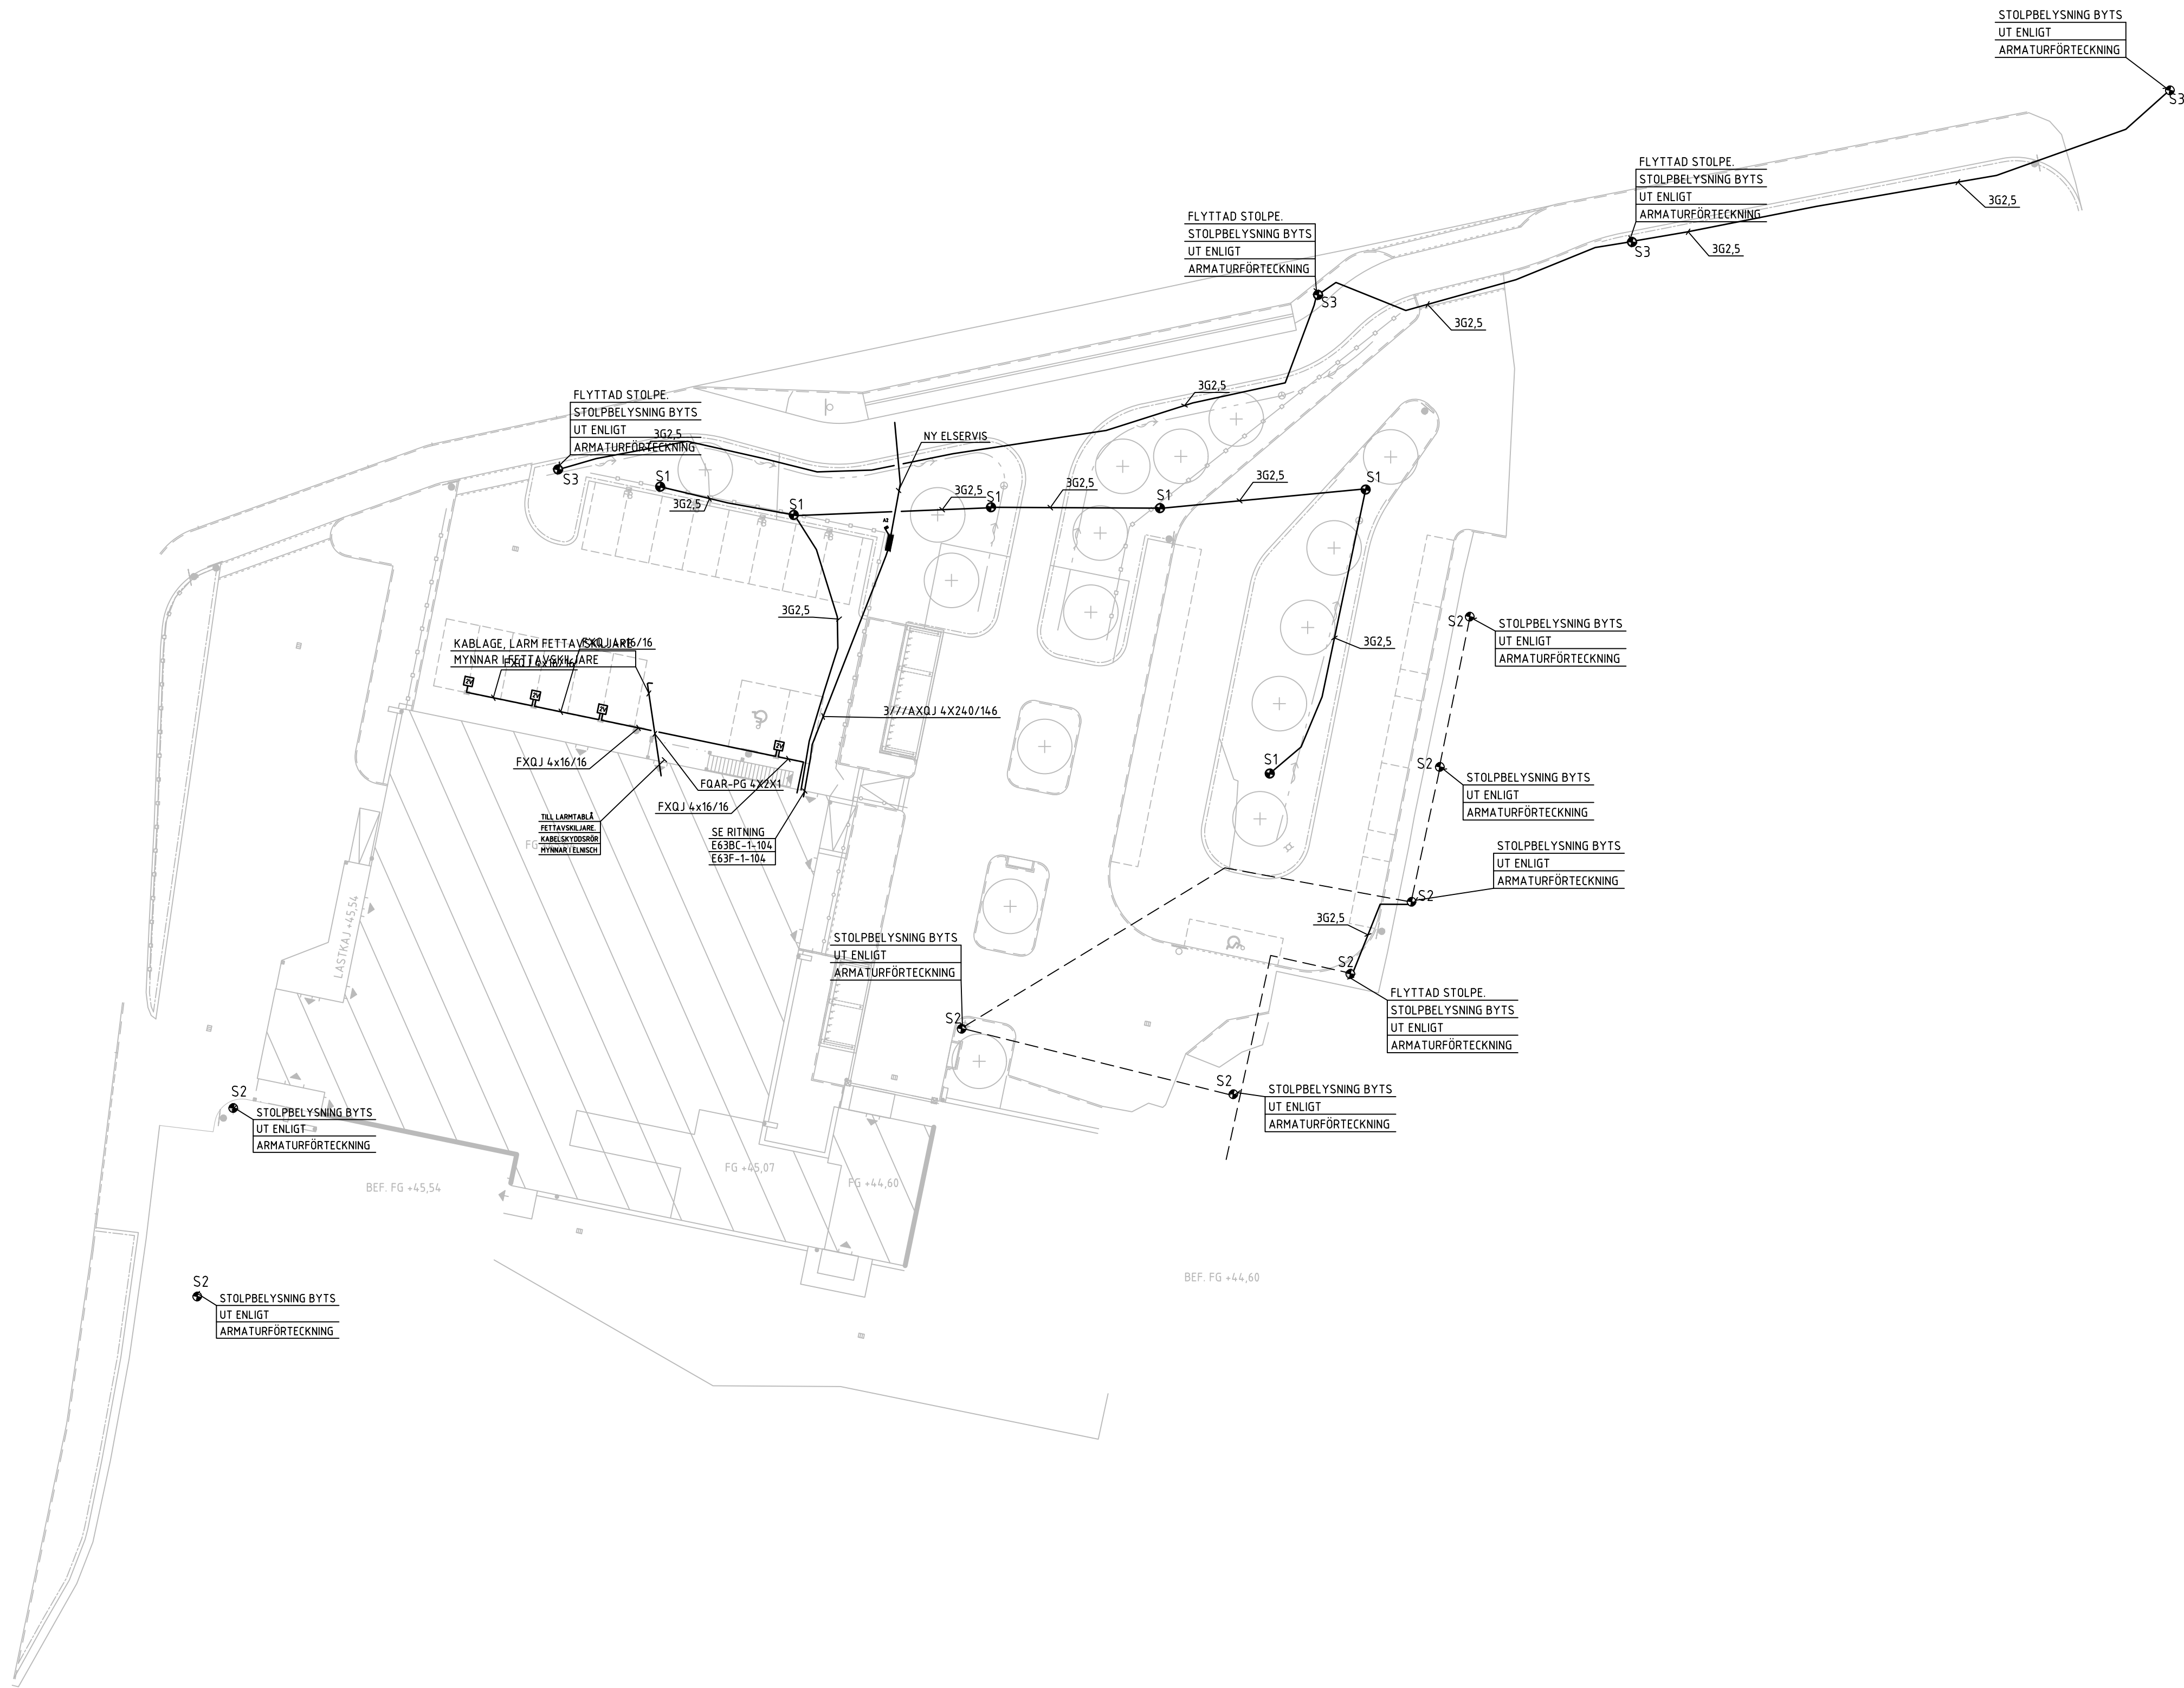


ANVISNINGAR
DÄR INGET ANNAT ANGES GÄLLER:
KABEL FÖRLAGGS I KABELSKYDDSRÖR
HALOGENFRITT MATERIAL

SYMBOLFÖRKLARINGAR

- MARKMÄTARSKÄP
- DUBBEL MOTORVÄRMARE, TYP ENLIGT
TEKNISK BESKRIVNING
- BELYSNINGSTOLPE TYP
ENLIGT ARMATURFÖRTECKNING
- KABEL

HÄNVISNINGAR

- SE ÄVEN
- TEKNISK BESKRIVNING EL
- ARMATURFÖRTECKNING

STATUS FÖRFRÅGNINGSUNDERLAG			
HANDLING BYGGHANDLING			
DATUM 2024-12-20	GÖRANÄS AV GIN	ÄNDRINGS PM -	
BESTÄLLARE ROBERTSFORS KOMMUN			
PROJEKTNAMN CENTRALKÖK			
OMRÅDE ROBERTSFORS KOMMUN			
PROJEKTNUMMER 108 83 71	ADRESS YTTRE RINGVÄGEN 4		
DOKUMENTNUMMER	FASTIGHET FORDONET 1		
DISCIPLIN E	FÖRETAG NORCONSULT SVERIGE AB		
UPPDRAGSNUMMER 1088371	SKAPAD AV GIN		
TELEFON 010 141 80 00	KONTAKTPERSON TOMAS BERGSTRÖM		
BYGGNADSVÄRK	PÅLÖSNING (ROT 2020)		
VÄNINGSPLAN	VÄNINGSDEL	DELOMRÅDE	
SYSTEM KRAFT & BELYSNING			
SITUATIONSPLAN			
RETNINGSKATEGORI PLANER	SKALA 1:300	FORMAT A1	
DOKUMENTNUMMER E-63-1-001	ÄNDRING -		