
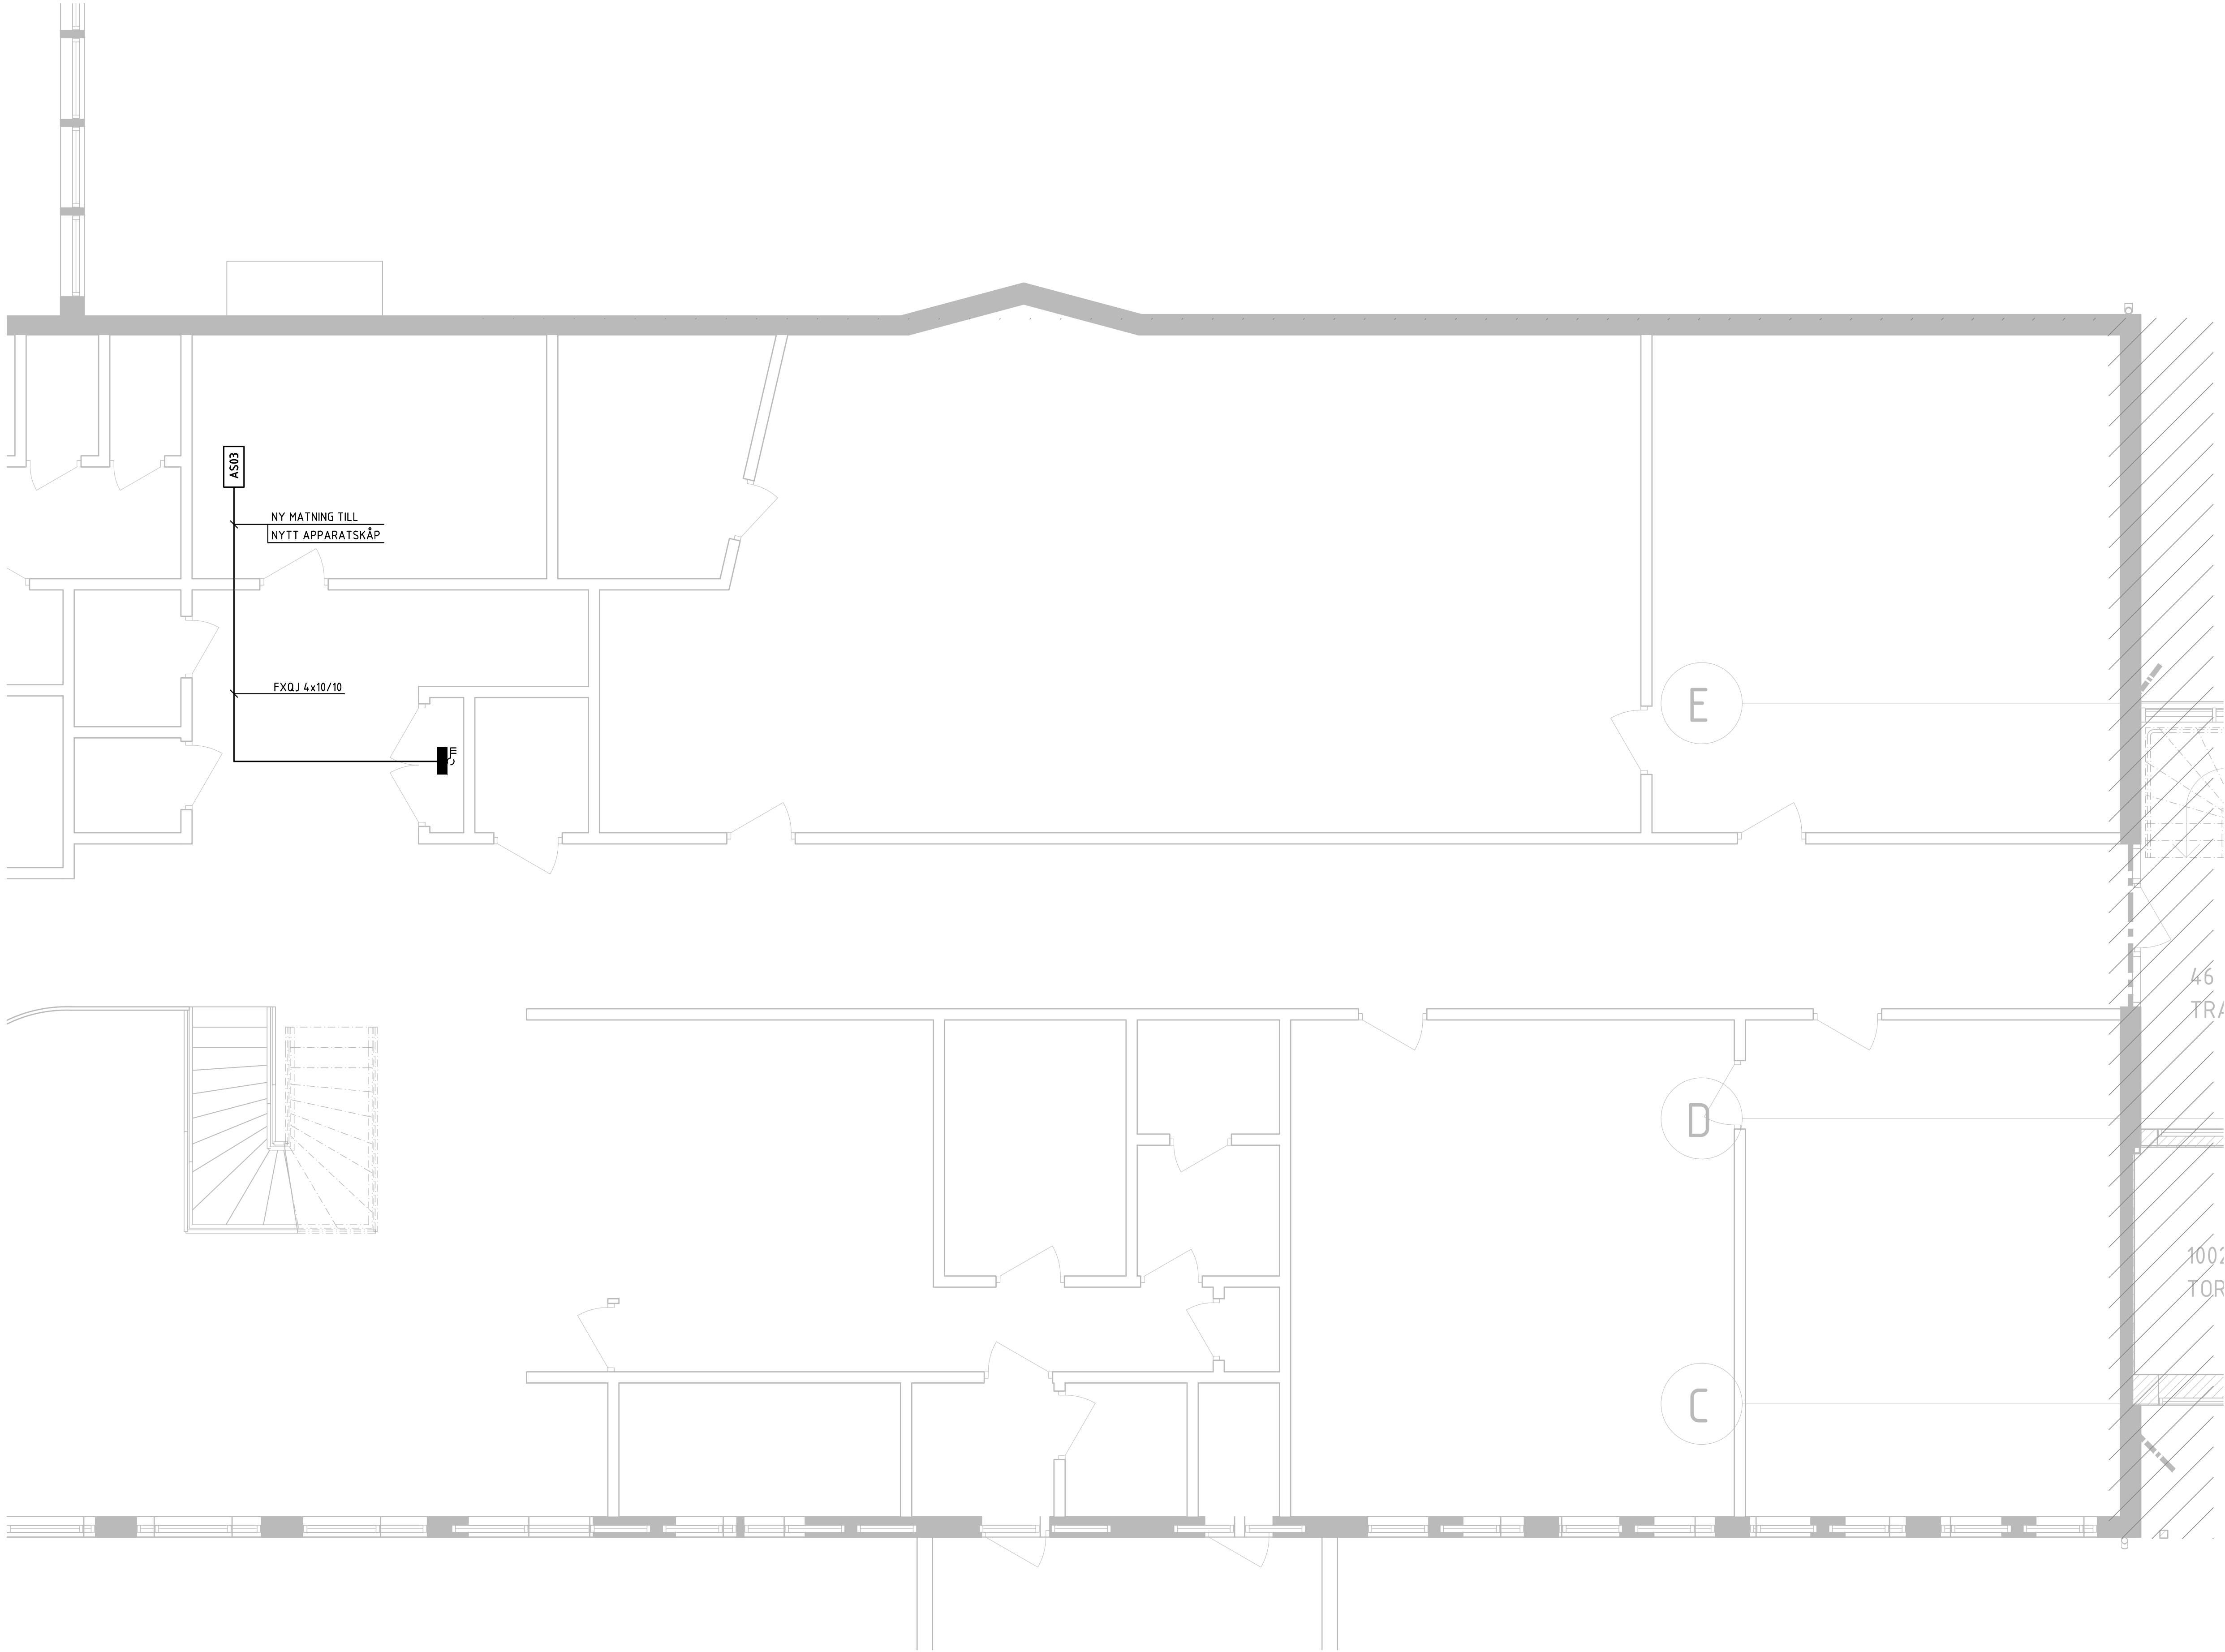
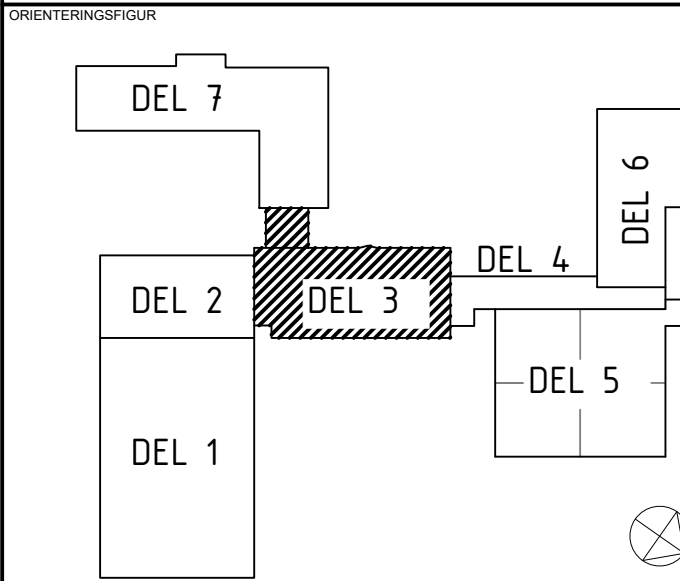


ANVISNINGAR
DÄR INGET ANNAT ANGES GÄLLER:
INFÄLLT MONTAGE PRIORITERAS DÄR BYGGNADS
KONSTRUKTIONEN TILLÅTER. VID UPL. MONTAGE FÖRLÄGGS
KABLAGE I EL-LIST
BRANDTÄTNING I SAMMA KLASS SOM VÄGGENS
BRANDKLASS.
HÖJD ANGES METER ÖFG.
STRÖMBRYTARE +1,0, UTTAG +0,3
HALOGENFRITT MATERIAL
KABEL 30/15
STRECKAT AVSER BEFINTLIGT
FYLLD SYMBOL = INFÄLLD. EJ FYLLD = UTANPÅLIGGANDE.
SYMBOLFÖRKLARINGAR

- 2VÄGS UTTAG
1VÄGS UTTAG
STÄDUTTAG 1VÄGSUTTAG +0,9.
2VÄGS UTTAG PLACERAS OVAN UNDERTAK
CEE 3FAS 16A UTTAG +1,8
3VÄGS UTTAG I FÖNSTERBÄNKSCHANAL
2POLIG SÄKERHETSBRYTARE
3POLIG SÄKERHETSBRYTARE MED MÄRKSTRÖM
2POLIG SÄKERHETSBRYTARE FÖR DÖRRAUTOMATIK
MONTERAS I ANSLUTNING TILL AUTOMATIKEN.
GVF 1-VÄGS UTTAG PLACERAS I SKÅP FÖR
GOLVVÄRMEFÖRDELARE
DÖRRAUTOMATIK
ARMBÄGSKONTAKT, HÖJD CC +0,8

- CENTRAL
KABEL
BEFINTLIG KABEL
KABLAR FÖRLÄGGS I KANALISATION I MARK/PLATTA
SPIRAKABEL MED UTTAG FÖR MATNING TILL
LADDVAGN. DOSA OVAN UNDERTAK
VÄGGUTTAG PÅ DOSPLÅT PÅ KABELSTEGE FÖR
ANSLUTNING AV AKTIV SKYLTT FÖR HÖRSLINGA.
ANSLUTNING FLÄKTUFTVÄRME
MATNING TABLÅ FETTAVSKILJARE
MATNING SCHUNT
FRÄNLUFTSFLÄKT
MATNING KYLRUM. +1,7
INKOPPLING TRAFÖ FÖR BLANDARE. OVAN UNDERTAK
MATNING VÄRMEKABEL, PLACERING SAMORDNAS
MATNING AVFROSTNING. +1,7
MONTERAS PÅ DOSPLÅT PÅ KABELSTEGE.
STRÖMFÖRSÖRJNING MANÖVERPANEL LJUD.
ANSLUTS TILL MP ENLIGT E64ED1-512.
STRÖMFÖRSÖRJNING ANSLUTS TILL INBROTTSALARM-
CENTRAL.

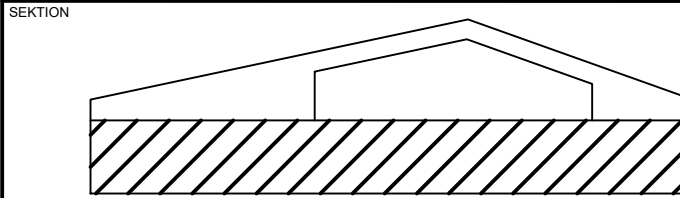

STATUS
FÖRFRÅGNINGSUNDERLAG
HANDLING
BYGGHANDLING
DATUM
2024-12-20
TODDAD AV
GIN
ÄNDRINGS PM
-



PROJEKTNAMN
CENTRALEKÖ
OMRÅDE
ROBERTSFORS KOMMUN
PROJEKTNUMMER
YTTERE RINGVÄGEN 4
DÅRENSNUMMER
FASTIGHET
FORDONET 1
DISCIPLIN
FÖRETAG
NORCONSULT SVERIGE AB
UPPDRAGSNUMMER
1088371
SKAPAD AV
GIN
TELEFON
010 141 80 00
KONTAKTPERSON
TOMAS BERGSTRÖM
BYGGNADSVÄRK
+45,54 (FG)
VÄNINGSPLAN
1
VÄNINGSDEL
DEL 3
SYSTEM
KRAFT
SPECIFIKATION
PLAN 1
TITEL
PLANER
SKALA
1:50
FORMAT
A1
DOKUMENTNUMMER
E-63BC-1-311
ÄNDRING
-