
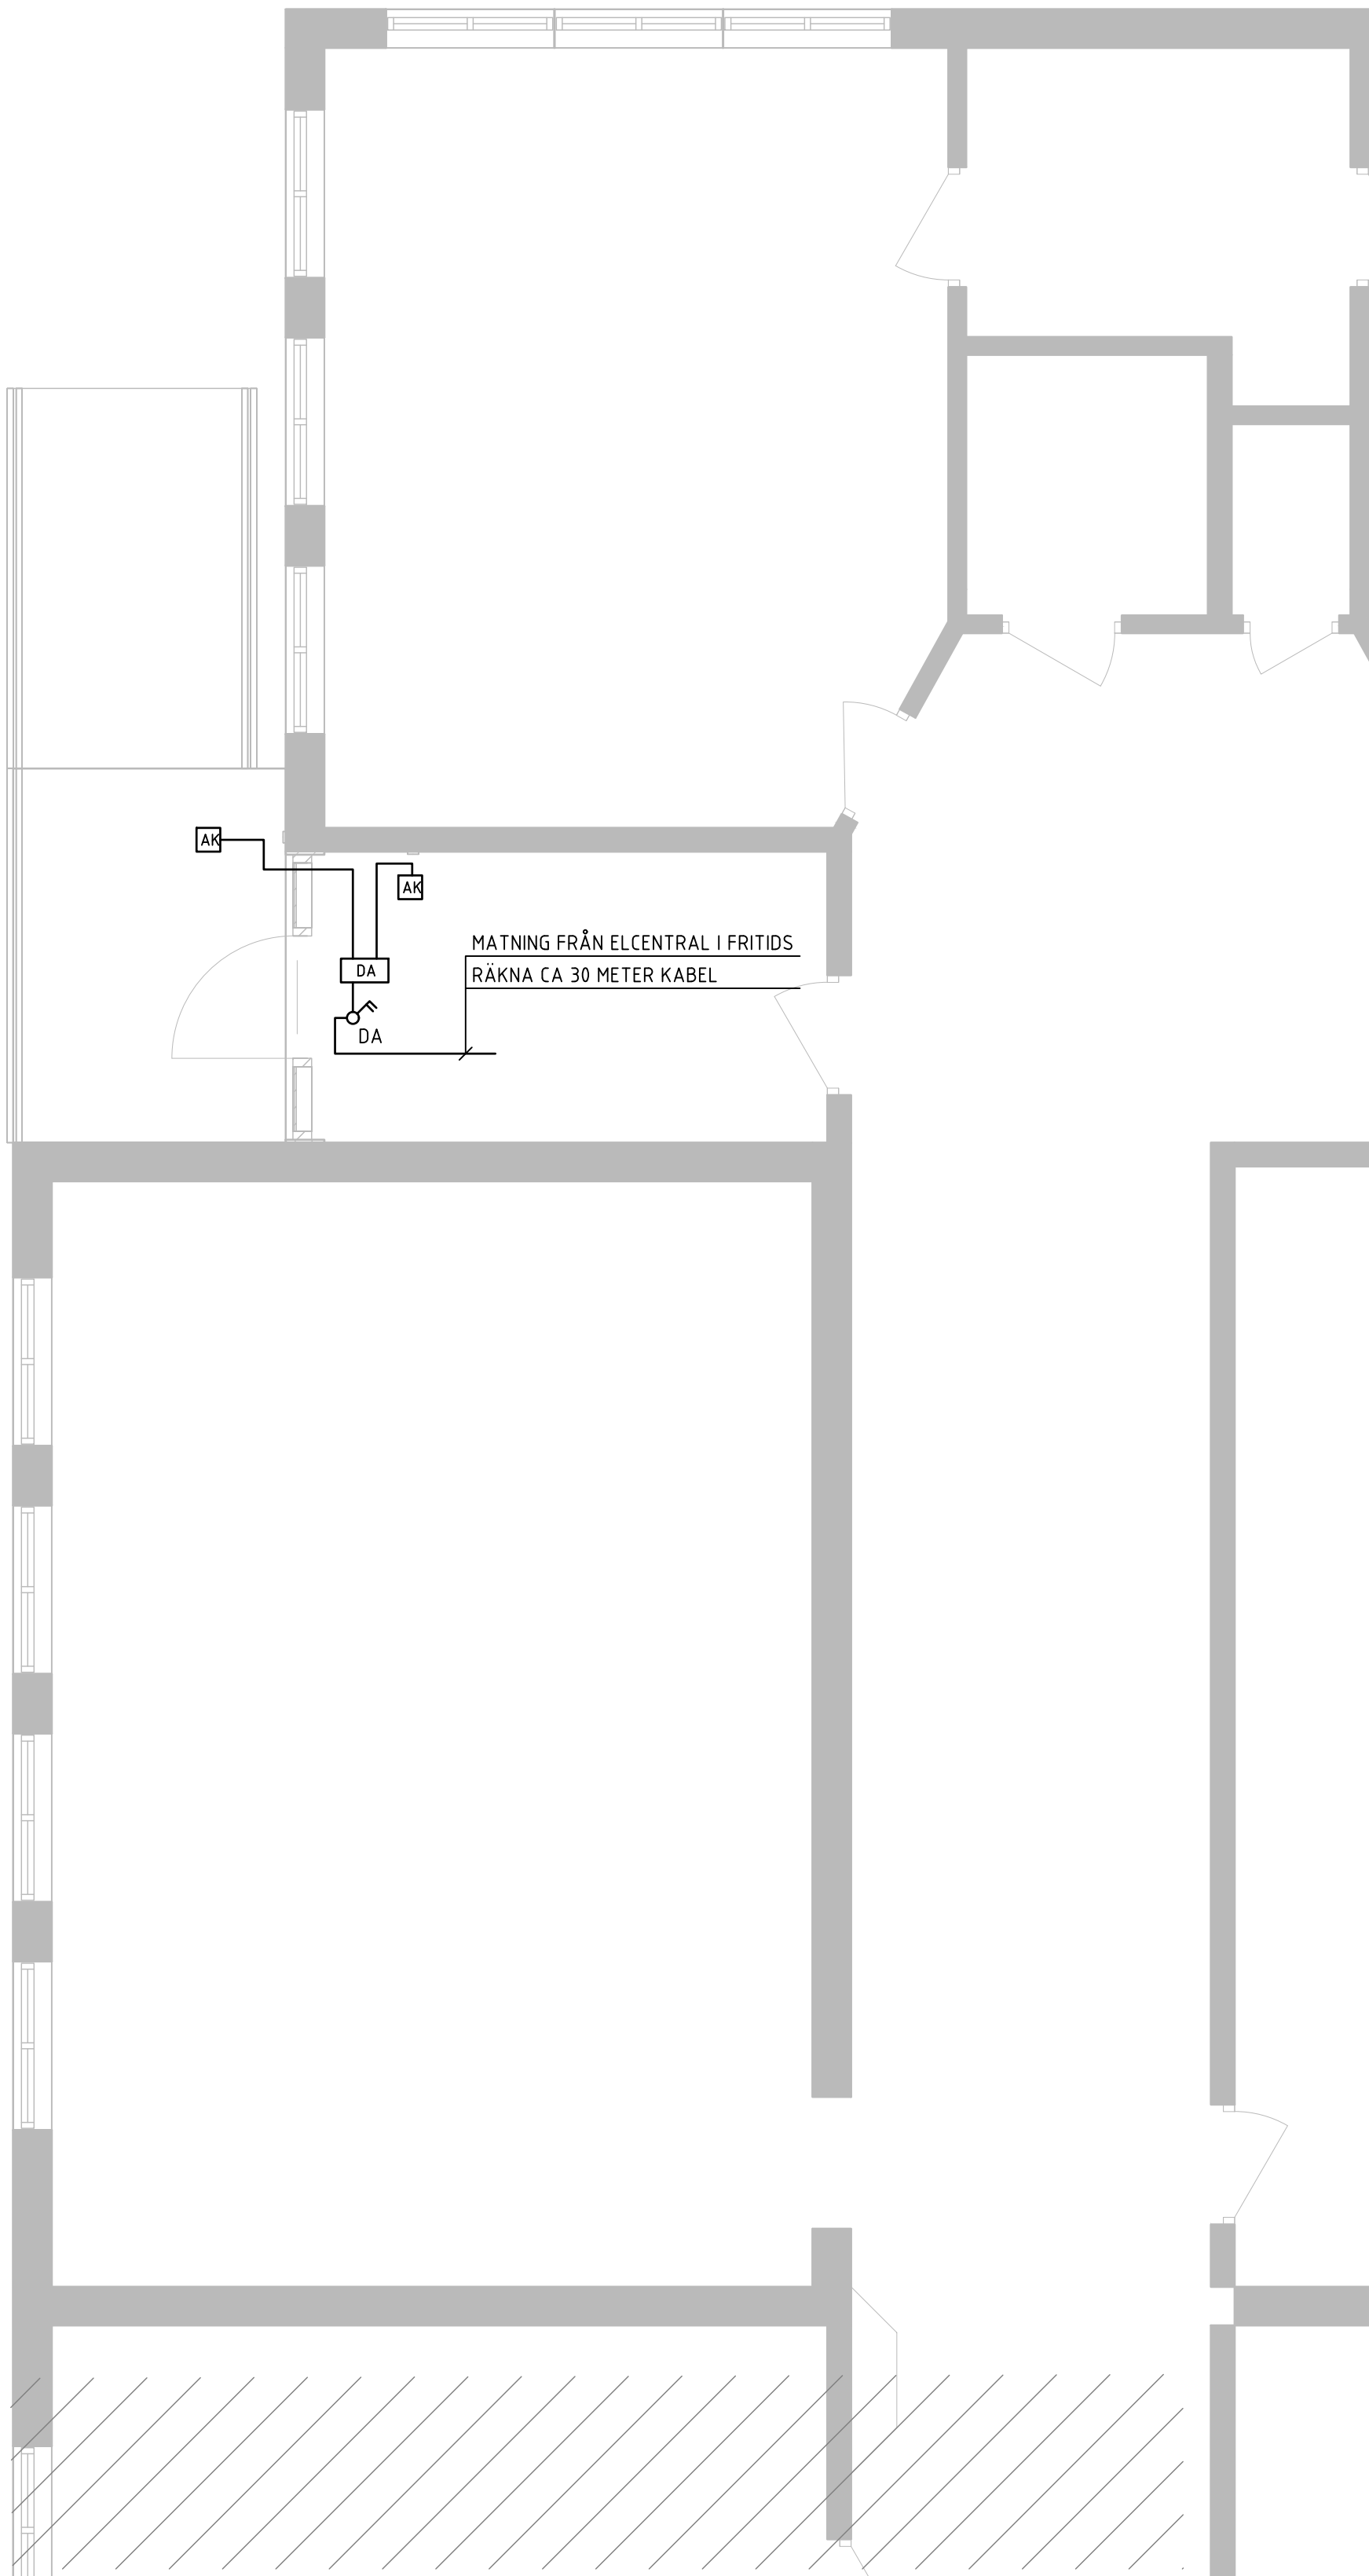
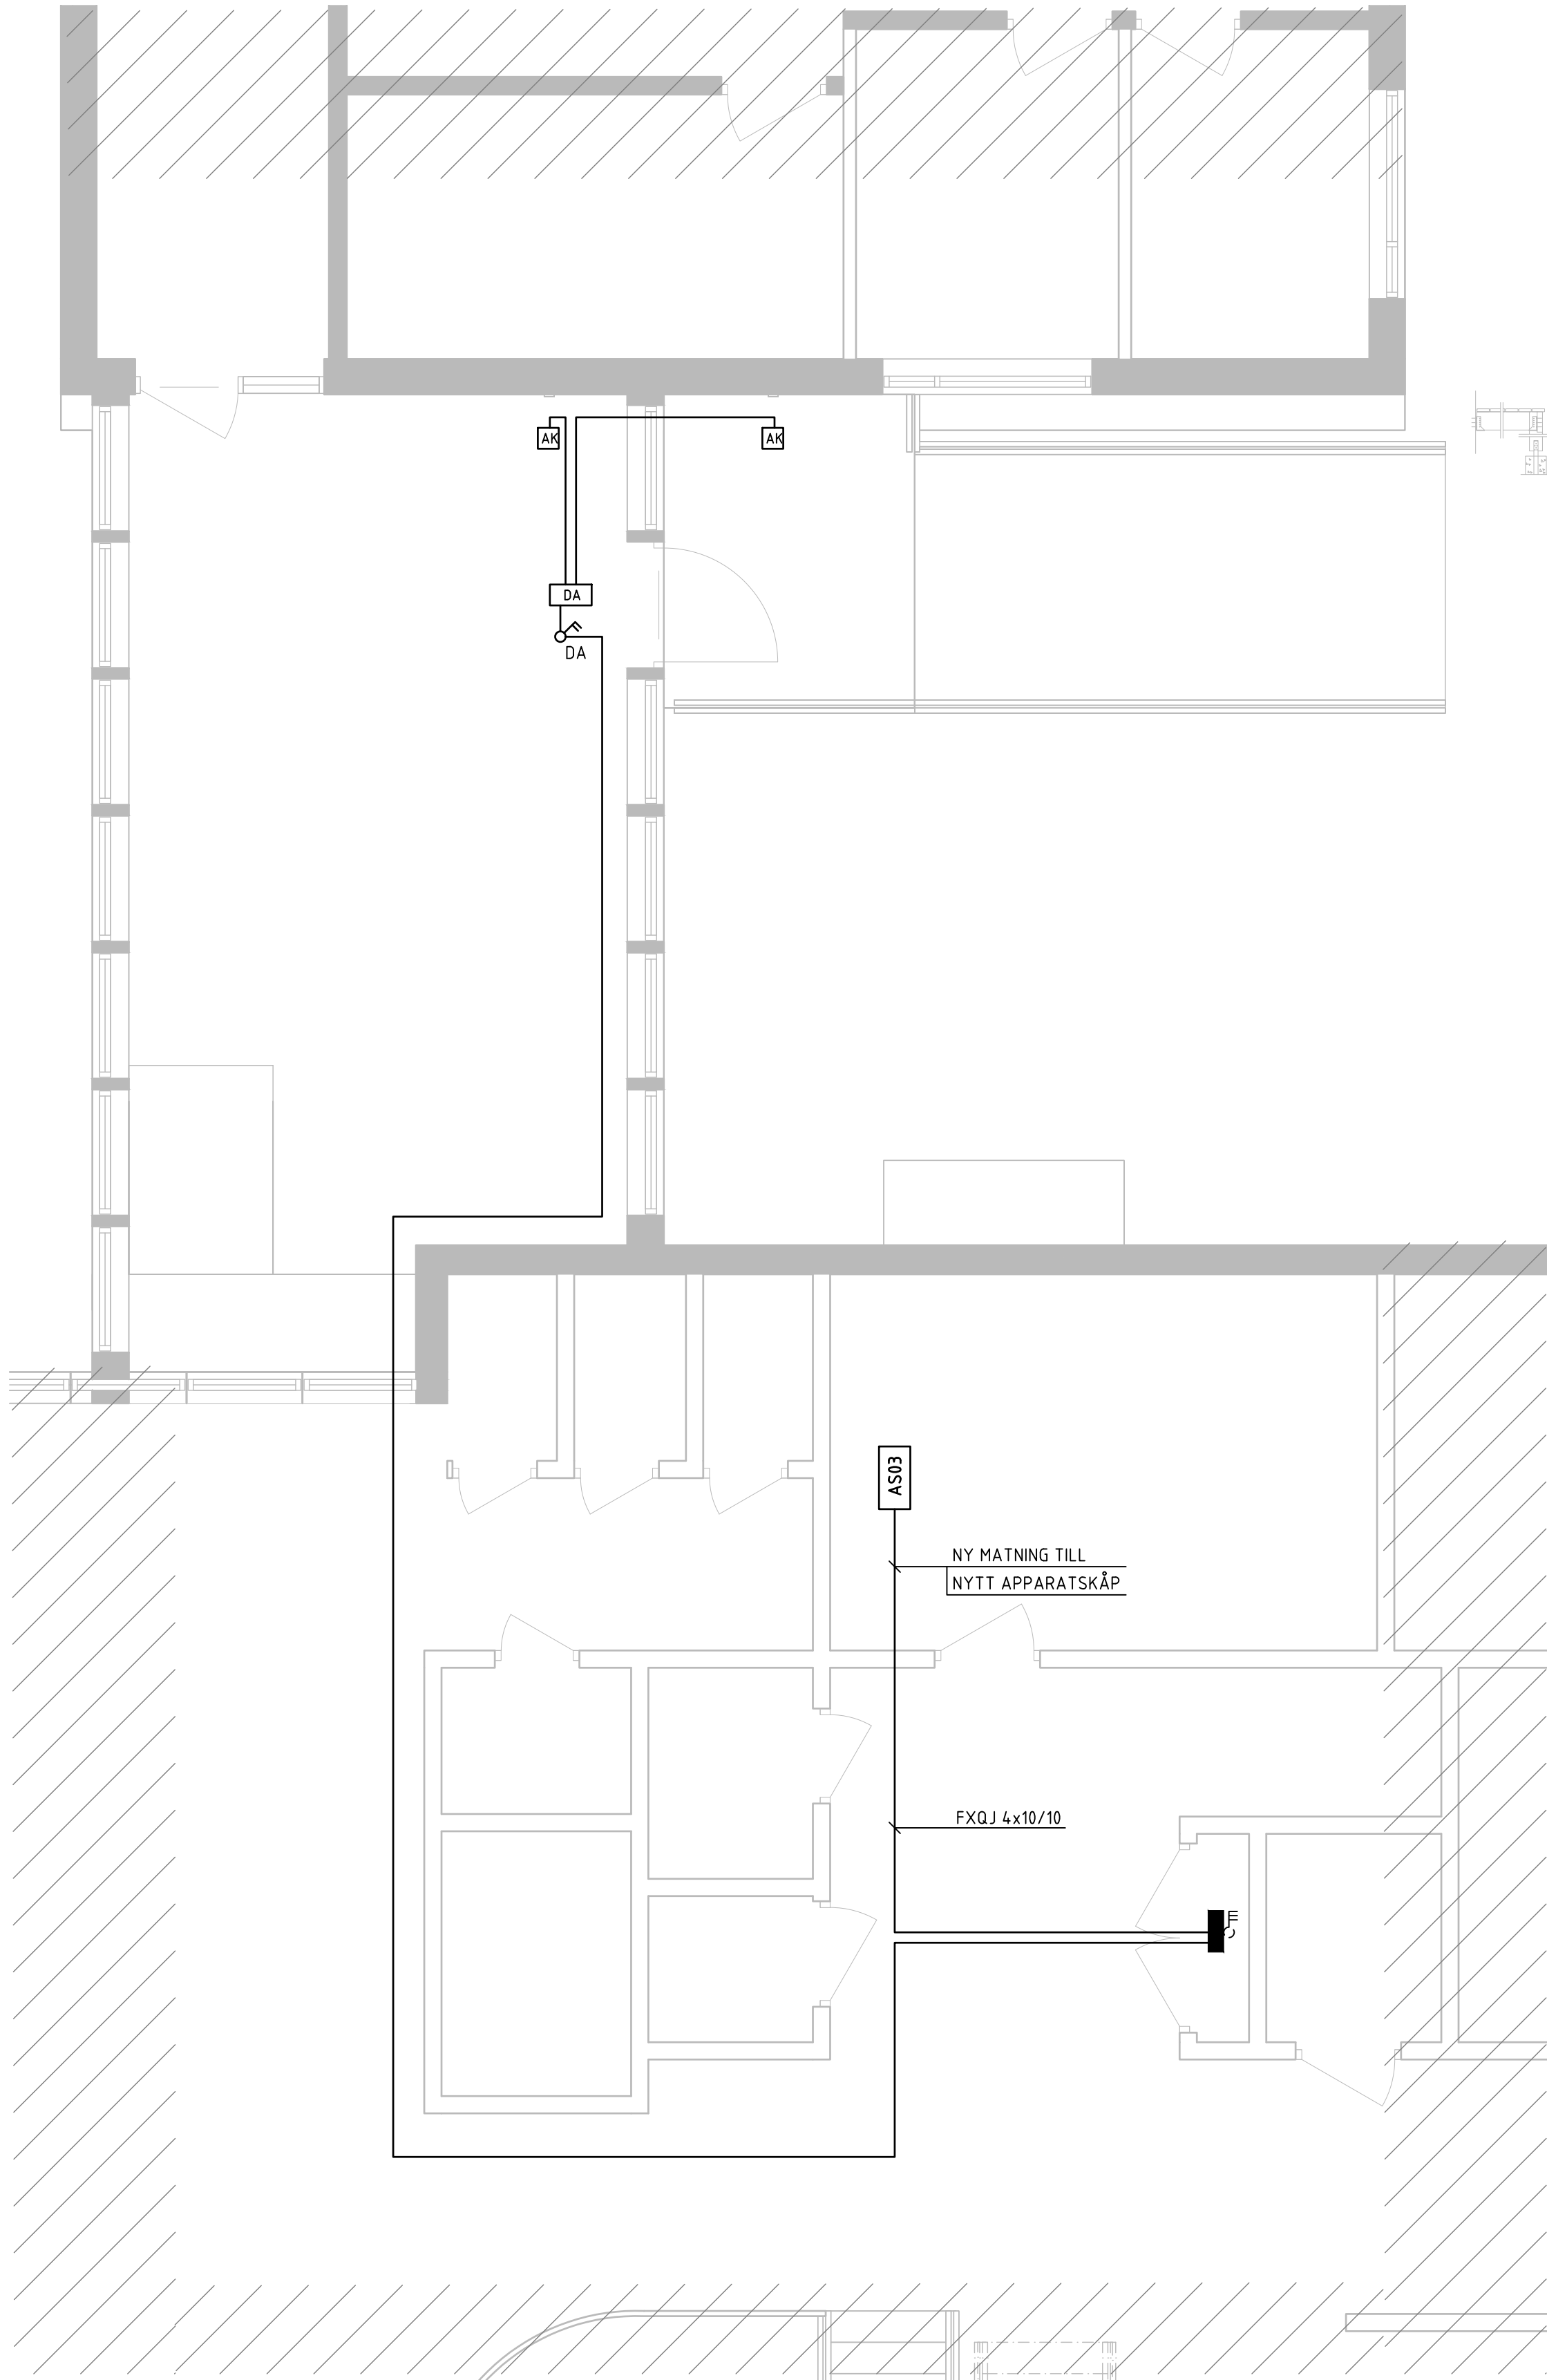


- ANVISNINGAR**
- DÄR INGET ANNAT ANGES GÄLLER:
INFÄLLT MONTAGE PRIORITERAS DÄR BYGGNADES
KONSTRUKTIONEN TILLÅTER. VID UPL. MONTAGE FÖRLÄGGS
KABLAG I EL-LIST
BRANDTÄTNING I SAMMA KLASS SOM VÄGGENS
BRANDKLASS.
HÖJD ANGES METER ÖFG.
STRÖMBRYTARE +1,0, UTTAG +0,3
HALOGENFRITT MATERIAL
KABEL 3015
STRECKAT AVSER BEFINTLIGT
FYLLD SYMBOL = INFÄLLD. EJ FYLLD = UTANPÅLIGGANDE.
SYMBOLFÖRKLARINGAR
- 2VÄGS UTTAG
1VÄGS UTTAG
STÄDUTTAG 1VÄGSUTTAG +0,9
2VÄGS UTTAG PLACERAS OVAN UNDERTAK
CEE 3FAS 16A UTTAG +1,8
3VÄGS UTTAG I FÖNSTERBÄNSKANAL
2POLIG SÄKERHETSBRYTARE
3POLIG SÄKERHETSBRYTARE MED MÄRKSTRÖM
2POLIG SÄKERHETSBRYTARE FÖR DÖRRAUTOMATIK
MONTERAS I ANSLUTNING TILL AUTOMATIKEN.
GVF 1-VÄGS UTTAG PLACERAS I SKÅP FÖR
GOLVVÄRMEFÖRDELARE
DÖRRAUTOMATIK
ARMBÄGSKONTAKT, HÖJD CC +0,8
- CENTRAL
KABEL
BEFINTLIG KABEL
- 1 KABLAR FÖRLÄGGS I KANALISATION I MARK/PLATTA
2 SPIRALKABEL MED UTTAG FÖR MATNING TILL
LADDVAGN. DOSA OVAN UNDERTAK
3 VÄGGUTTAG PÅ DOSPLÅT PÅ KABELSTEGE FÖR
ANSLUTNING AV AKTIV SKYLTT FÖR HÖRSLINGA.
4 ANSLUTNING FLÄKTLUFTVÄRME
5 MATNING TABLÅ FETTAVSKILJARE
6 MATNING SCHUNT
7 FRÄNLUFTSFLÄKT
8 MATNING KYLRUM. +1,7
9 INKOPPLING TRAFÖ FÖR BLANDARE. OVAN UNDERTAK
10 MATNING VÄRMEKABEL, PLACERING SAMORDNAS
11 MATNING AVFROSTNING. +1,7
12 MONTERAS PÅ DOSPLÅT PÅ KABELSTEGE.
13 STRÖMFÖRSÖRJNING MANÖVERPANEL I JUD.
14 ANSLUTS TILL MP ENLIGT E64ED-1-S12.
STRÖMFÖRSÖRJNING ANSLUTS TILL INBROTTSALARM-CENTRAL.

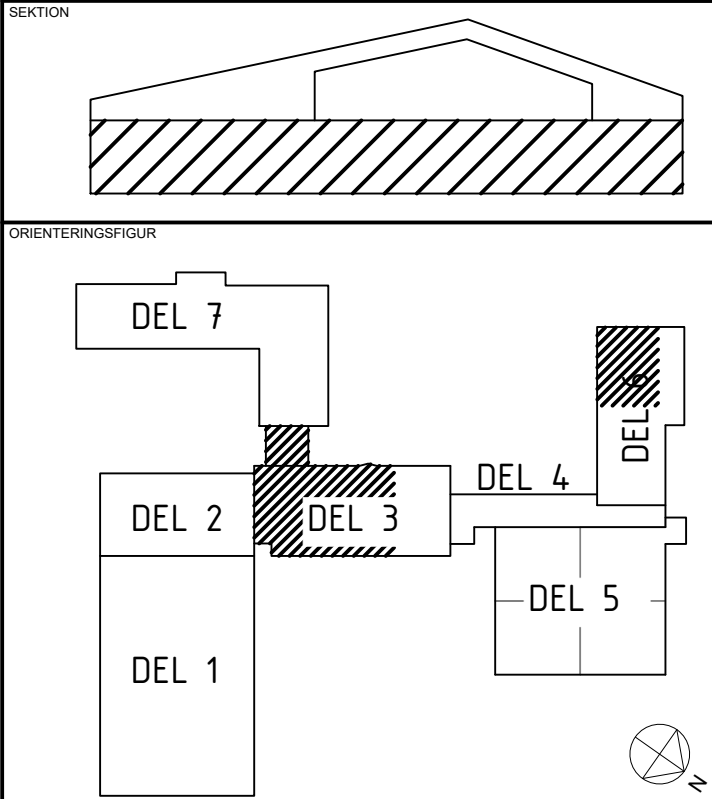

STATUS
FÖRFRÅGNINGSUNDERLAG

HANDLING
BYGGHANDLING

DATUM
2024-12-20

LODPAKAD AV
GIN

ÄNDRINGS PM
-



PROJEKTNAMN CENTRALEKÖK		
OMRÅDE ROBERTSFORS KOMMUN		
PROJEKTNUMMER	ADRESS YTRE RINGVÄGEN 4	
DARIENUMMER	FASTIGHET FORDONET 1	
DISCIPLIN	FÖRETAG NORCONSULT SVERIGE AB	
UPPDRAGSNUMMER	SKAPAD AV GIN	
TELEFON	KONTAKTPERSON 010 141 80 00 TOMAS BERGSTRÖM	
BYGGNADSVÄRDE	BYGGNADSVÄRDE +45,54 (FG)	
VÄNINGSPLAN	VÄNINGSDEL	DELOMRÅDE
1		DEL 3, DEL 6
SYSTEM KRAFT		
SPECIFIKATION PLAN 1		
PLANER	SKALA 1:50	FORMAT A1
DOCUMENTNUMMER	ÄNDRING E-63BC-1-312	