


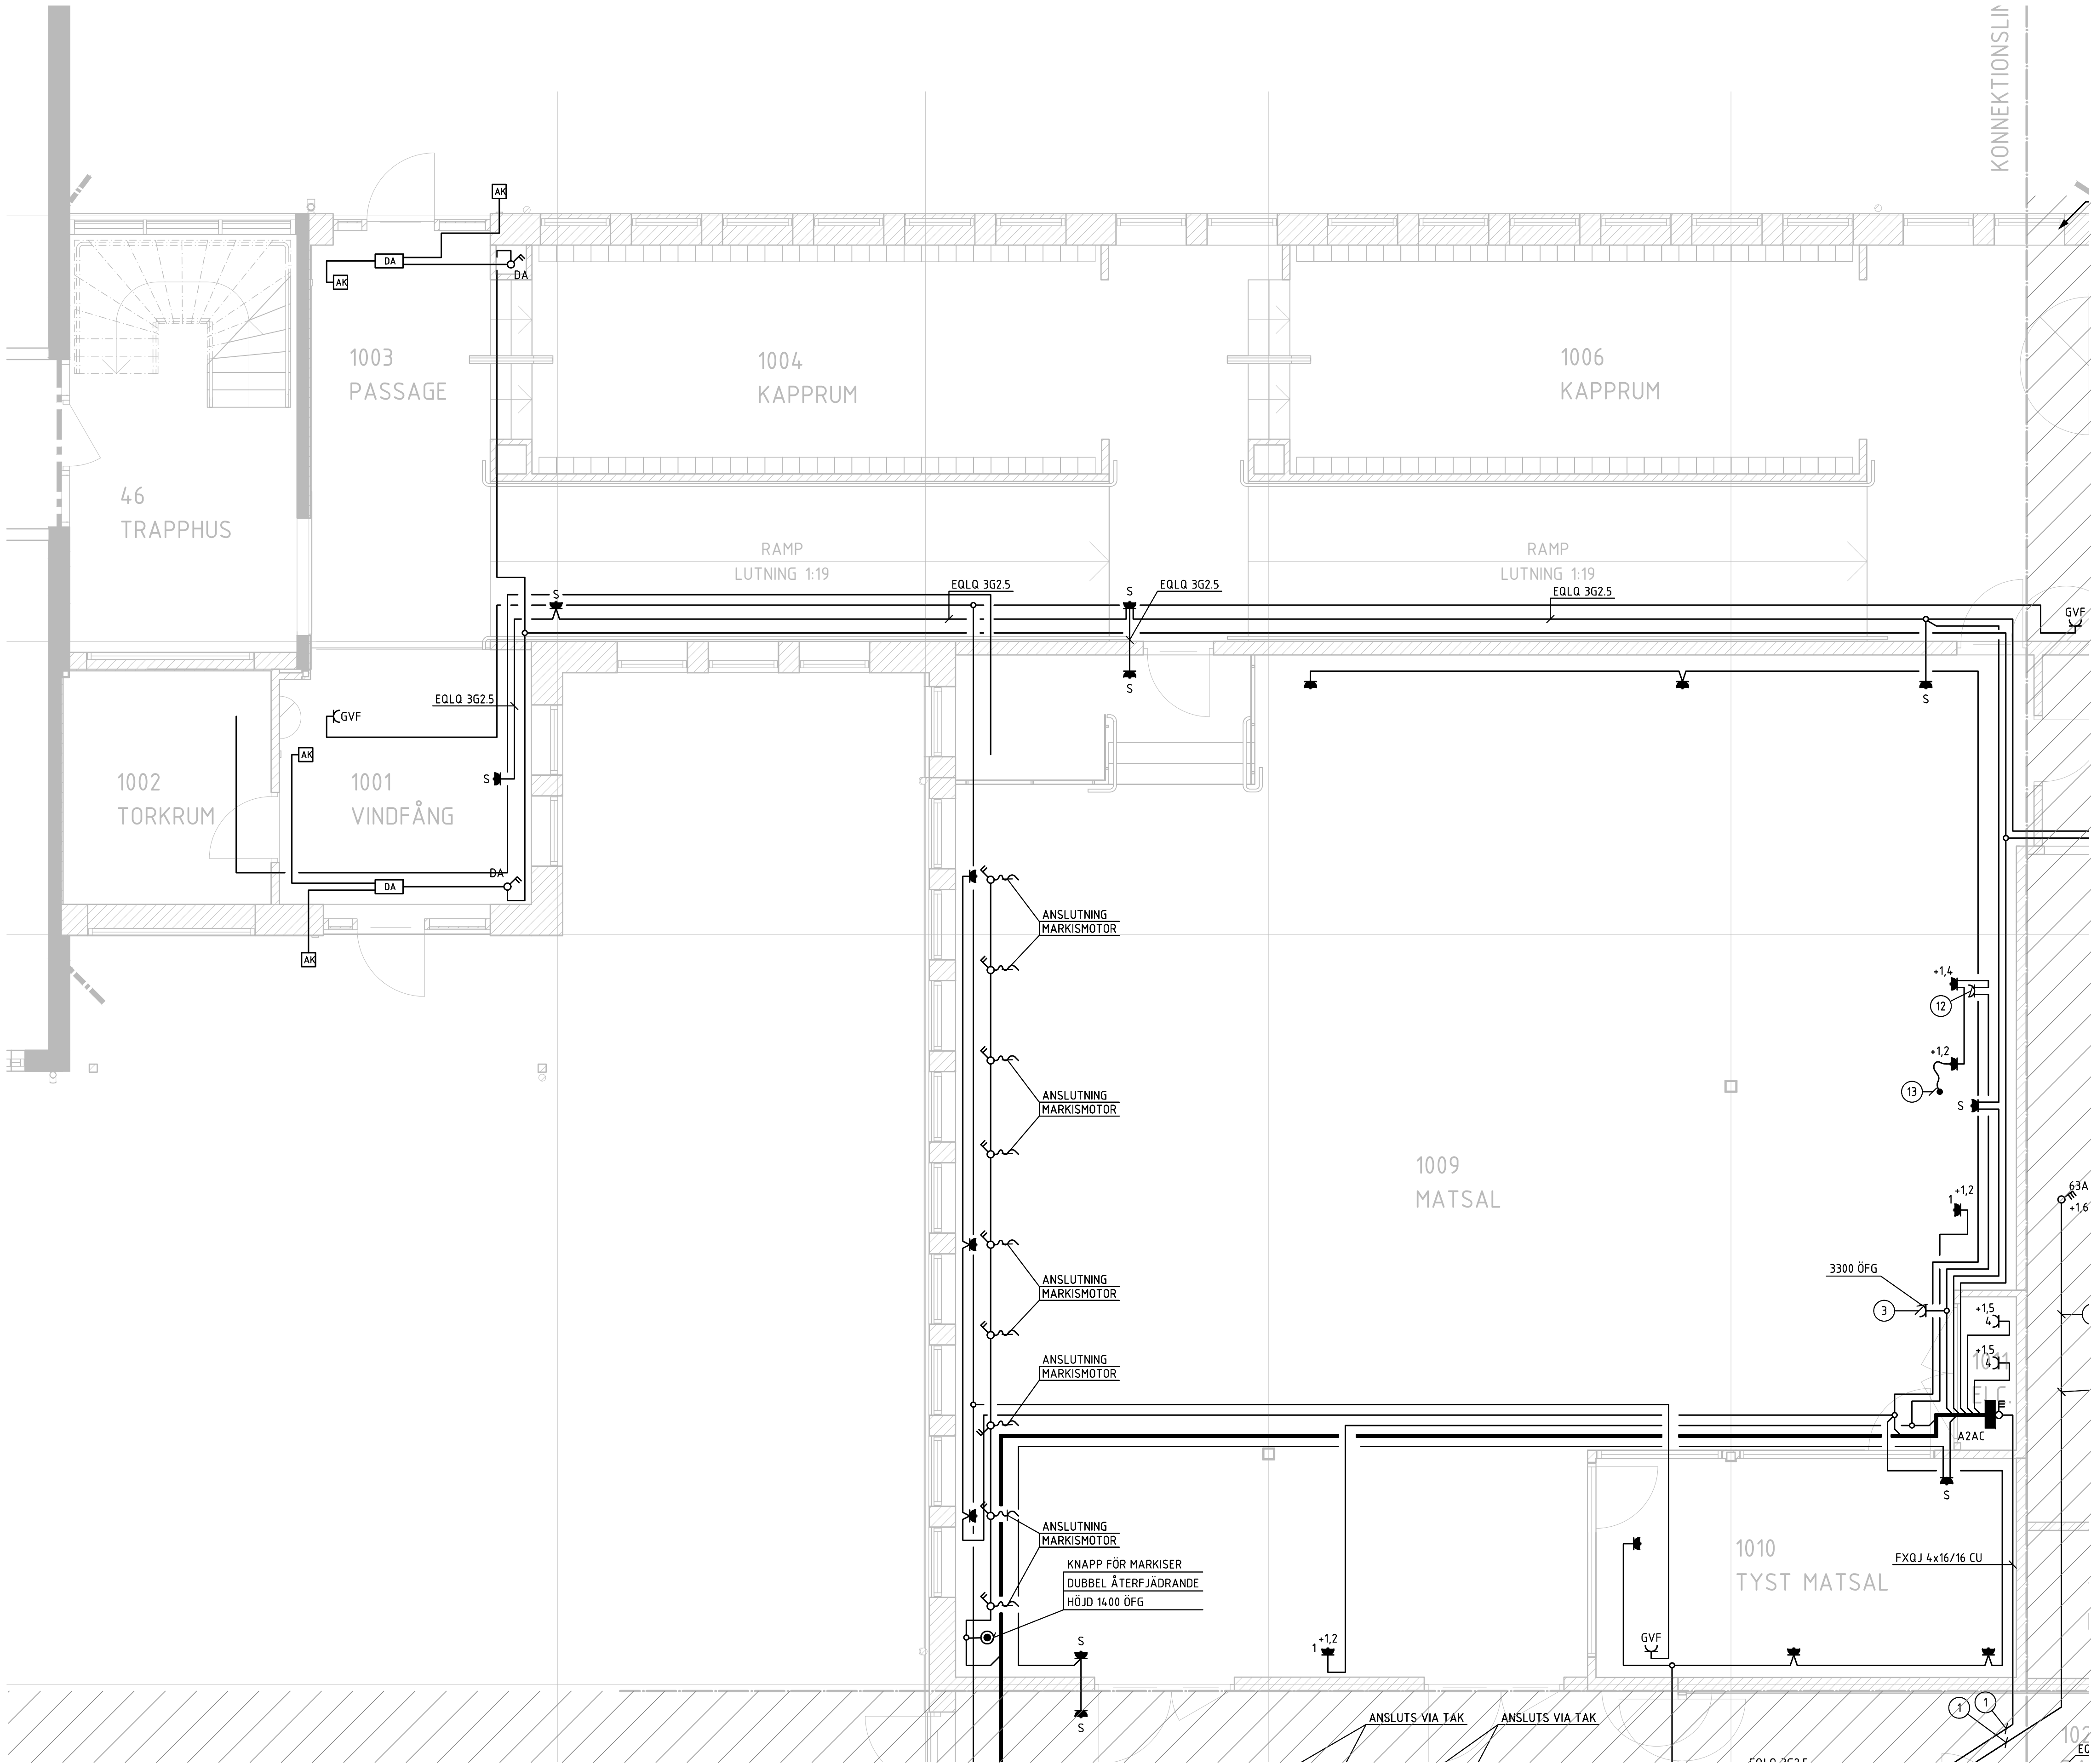

ANVISNINGAR
DÄR INGET ANNAT ANGES GÄLLER:
INFÄLLT MONTAGE PRIORITERAS DÄR BYGGNADS
KONSTRUKTIONEN TILLÅTER. VID UPL. MONTAGE FÖRLÄGGS
KABLAGET I EL-LIST
BRANDTÄTNING I SAMMA KLASS SOM VÄGGENS
BRANDKLASS.
HÖJD ANGES METER ÖFG.
STRÖMBRYTARE +1,0, UTTAG +0,3
HALOGENFRITT MATERIAL
KABEL 3G1,5
STRECKAT AVSER BEFINTLIGT
FYLLD SYMBOL = INFÄLLD. EJ FYLLD = UTANPÅLIGGANDE.
SYMBOLFÖRKLARINGAR

- 2VÄGS UTTAG
1VÄGS UTTAG
STÅDUTTAG 1VÄGSUTTAG +0,9
2VÄGS UTTAG PLACERAS OVAN UNDERTAK
CEE 3FAS 16A UTTAG +1,8
3VÄGS UTTAG I FÖNSTERBÄNSKANAL
2POLIG SÄKERHETSBRYTARE
3POLIG SÄKERHETSBRYTARE MED MÄRKSTRÖM
2POLIG SÄKERHETSBRYTARE FÖR DÖRRAUTOMATIK
MONTERAS I ANSLUTNING TILL AUTOMATIKEN.


GVF 1-VÄGS UTTAG PLACERAS I SKÅP FÖR
GOLVVÄRMEFÖRDELARE

DÖRRAUTOMATIK

ARMBÄGSKONTAKT, HÖJD CC +0,8

CENTRAL
KABEL
BEFINTLIG KABEL

- 1 KABLAR FÖRLÄGGS I KANALISATION I MARK/PLATTA
2 SPIRAKABEL MED UTTAG FÖR MATNING TILL
LADDVAGN. DOSA OVAN UNDERTAK
3 VÄGGUTTAG PÅ DOSPLÅT PÅ KABELSTEGE FÖR
ANSLUTNING AV AKTIV SKYLTT FÖR HÖRSLINGA.
4 ANSLUTNING FLÄKTLUFTVÄRME
5 MATNING TABLÅ FETTAVSKILJARE
6 MATNING SCHUNT
7 FRÄNLUFTSFLÄKT
8 MATNING KYLRUM. +1,7
9 INKOPPLING TRAFÖ FÖR BLANDARE. OVAN UNDERTAK
10 MATNING VÄRMEKABEL, PLACERING SAMORDNAS
11 MATNING AVFRÖSTNING. +1,7
12 MONTERAS PÅ DOSPLÅT PÅ KABELSTEGE.
13 STRÖMFÖRSÖRJNING MANÖVERPANEL I JUD.
ANSLUTS TILL MP ENLIGT E64ED-1-512.
14 STRÖMFÖRSÖRJNING ANSLUTS TILL INBROTTSALARM-
CENTRAL.

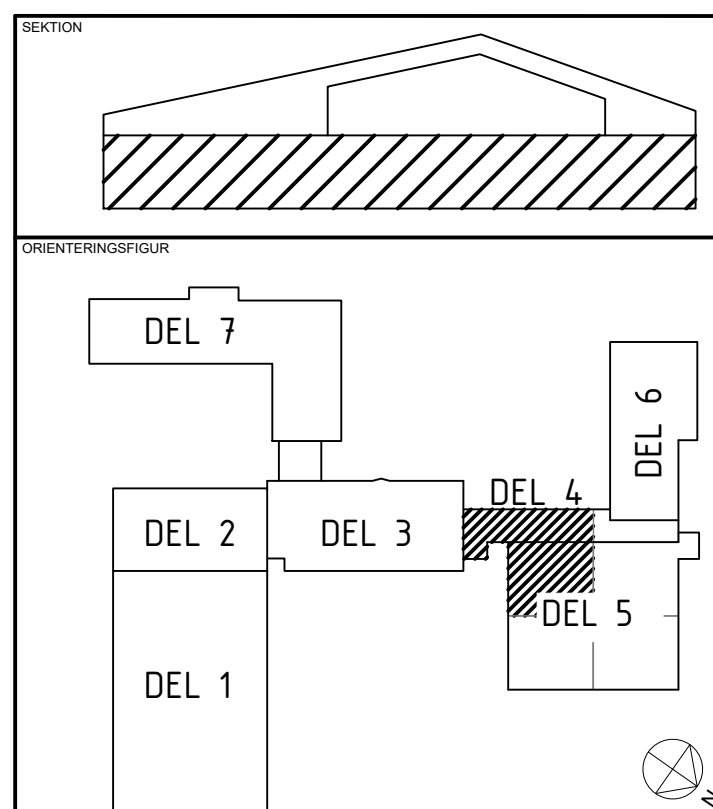

STATUS
FÖRFRÅGNINGSUNDERLAG
HANDLING
BYGGHANDLING
DATUM
2024-12-20
TODDAD AV
GIN
ÄNDRINGS PM
-



PROJEKTNAMN
CENTRALEKÖ
OBJEKT
ROBERTSFORS KOMMUN
PROJEKTNUMMER
YTTERE RINGVÄGEN 4
DIREKTÖR
FORDONET 1
DISCIPLIN
FORETAG
NORCONSULT SVERIGE AB
UPPDRAGSNUMMER
1088371
SKAPAD AV
GIN
TELEFON
010 141 80 00
KONTAKTPERSON
TOMAS BERGSTRÖM
BYGGNADSVÄRDE
+45,54 (FG)
VÄNINGSPLAN
1
VÄNINGSDEL
DEL 4.1, 5.1

SYSTEM
KRAFT
SPECIFIKATION
PLAN 1
TITEL
PLANER
SKALA
1:50
FORMAT
A1
DOKUMENTNUMMER
E-63BC-1-511
ÄNDRING
-