
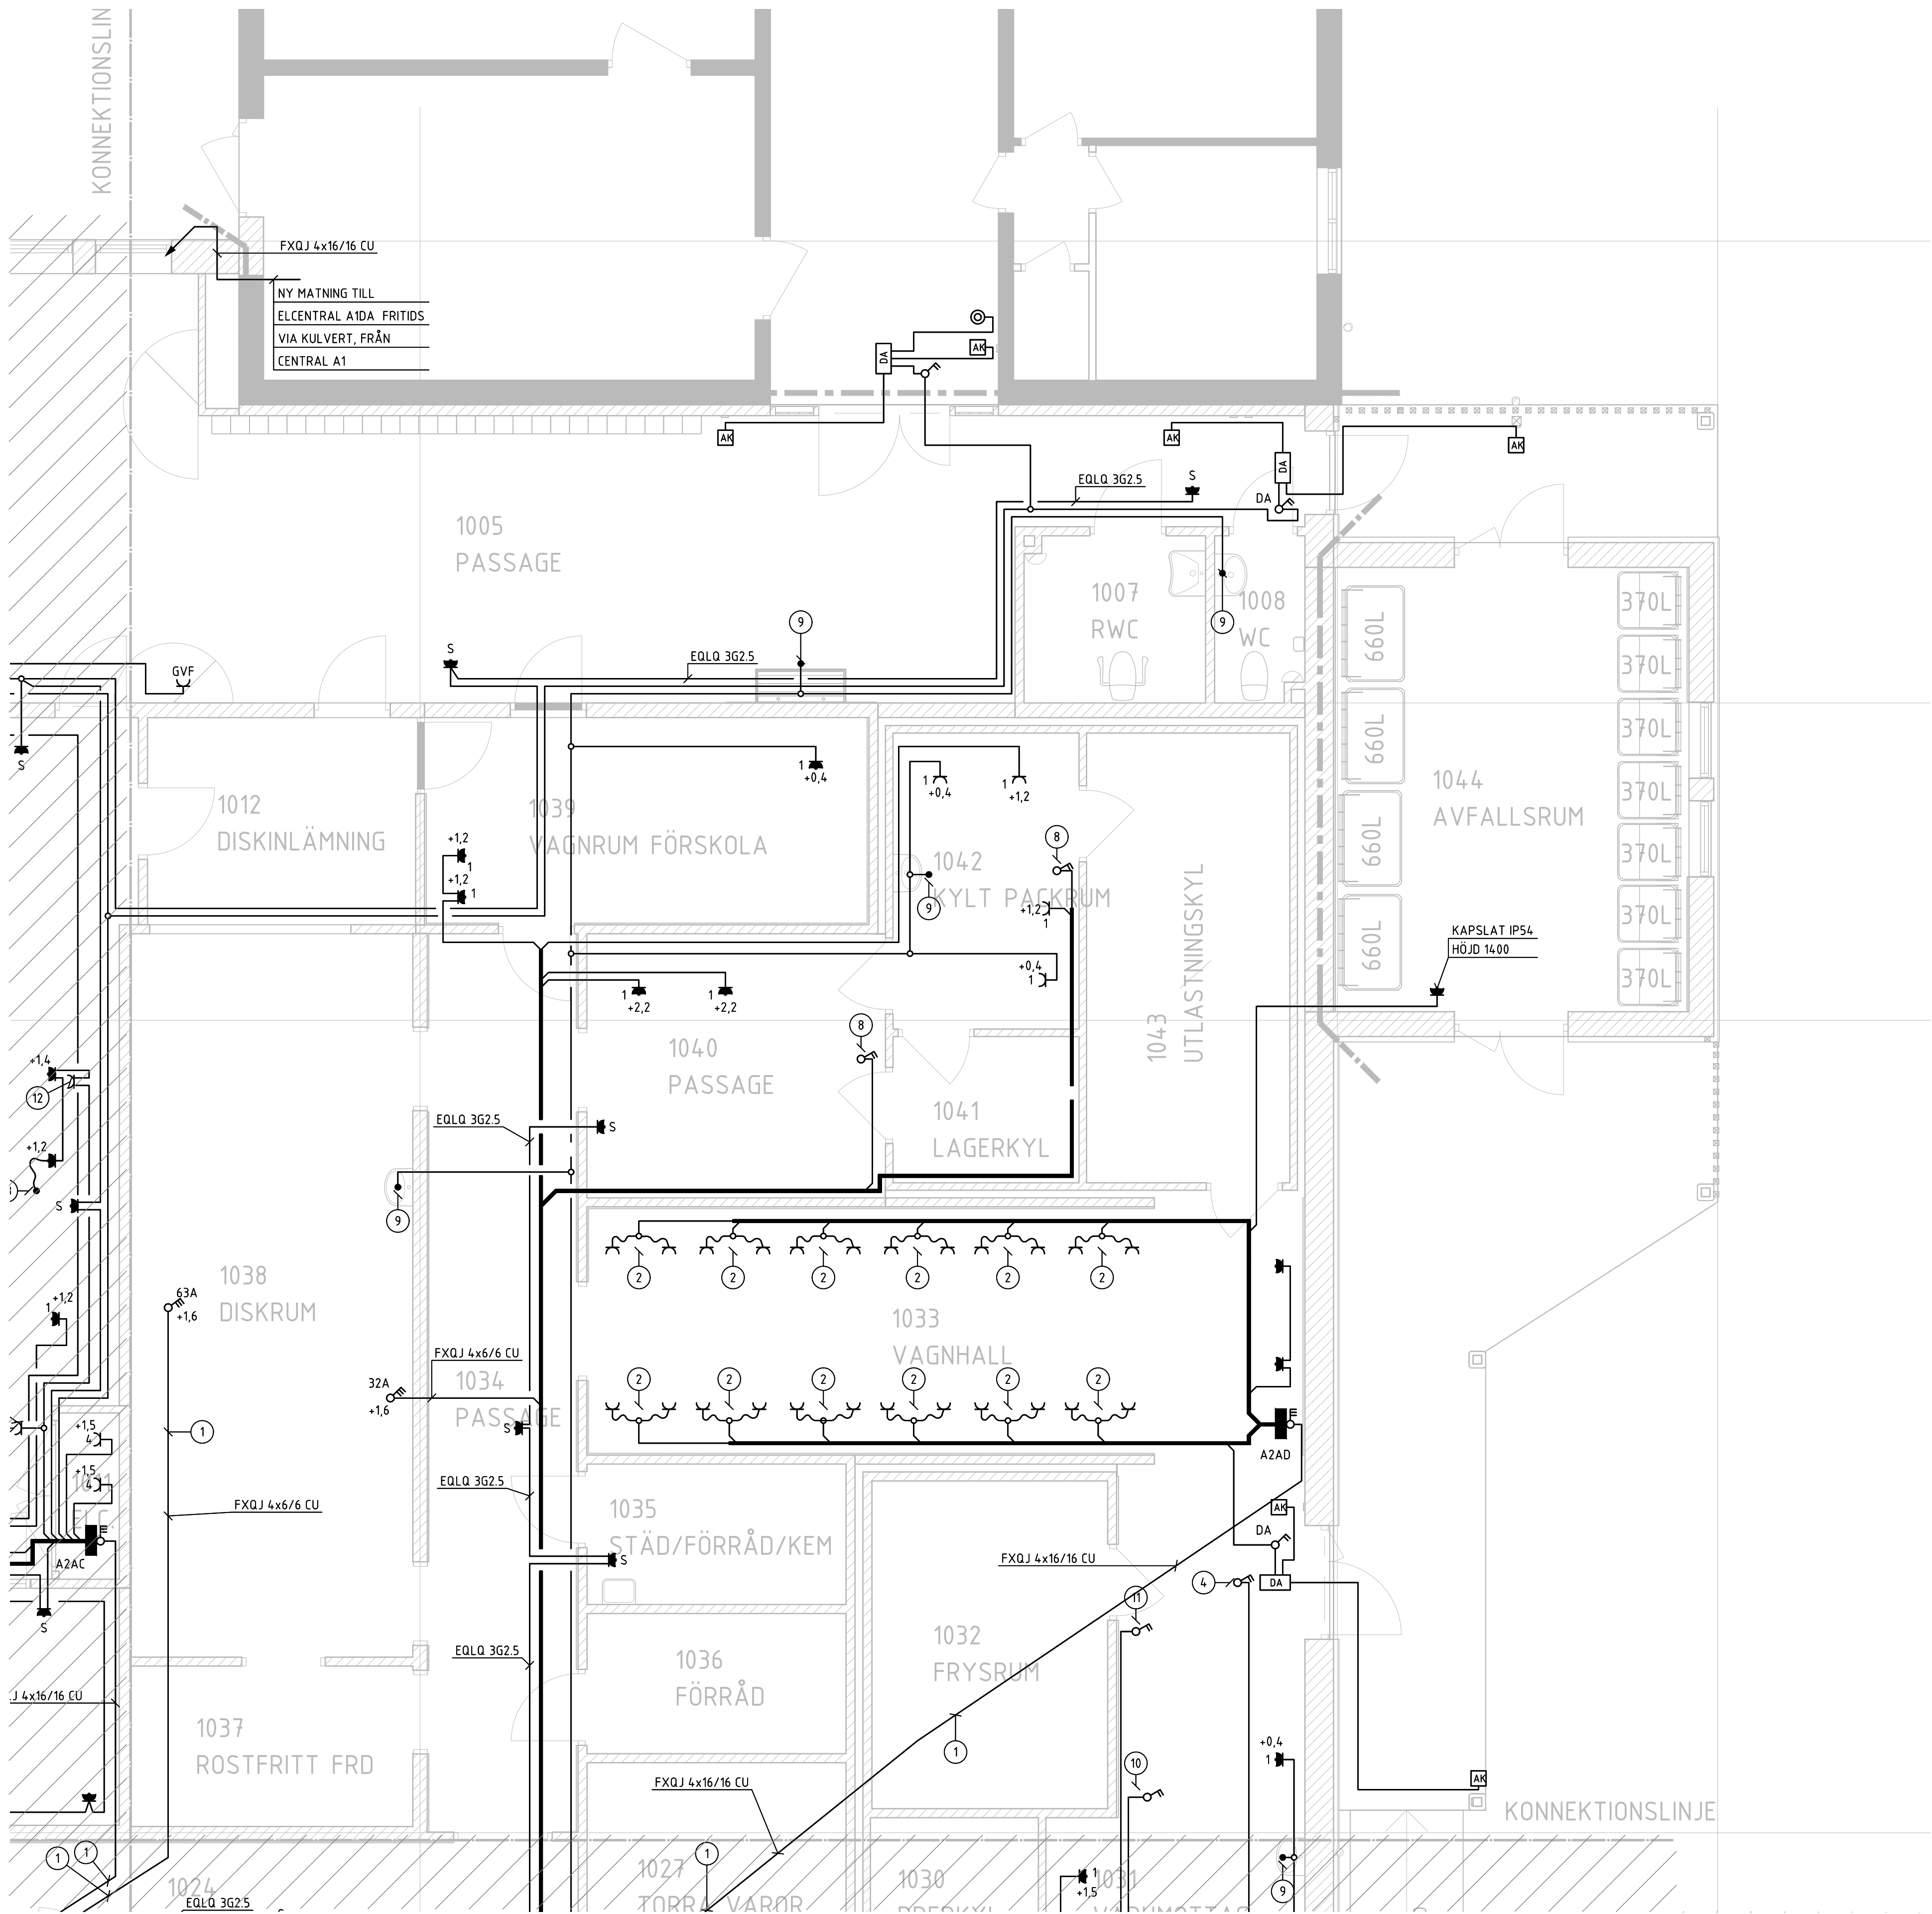


ANVISNINGAR
DÄR INGET ANNAT ANGES GÄLLER:
INFÄLLT MONTAGE PRIORITERAS DÄR BYGGNADS
KONSTRUKTIONEN TILLÅTER. VID UPL. MONTAGE FÖRLÄGGS
KABLAG I EL-LIST
BRANDTÄTNING I SAMMA KLASS SOM VÄGGENS
BRANDKLASS.
HÖJD ANGES METER ÖFG.
STRÖMBRYTARE +1,0, UTTAG +0,3
HALOGENFRITT MATERIAL
KABEL 3G2,5
STRECKAT AVSER BEFINTLIGT
FYLLO SYMBOL = INFÄLLD. EJ FYLLD = UTANPÅLUGGANDE.
SYMBOLFÖRKLARINGAR

- 2VÄGS UTTAG
1VÄGS UTTAG
STÄDUTTAG 1VÄGSUTTAG +0,9
2VÄGS UTTAG PLACERAS OVAN UNDERTAK
CEE 3FAS 16A UTTAG +1,8
3VÄGS UTTAG I FÖNSTERBÄNSKANAL
2POLIG SÄKERHETSBRYTARE
3POLIG SÄKERHETSBRYTARE MED MÄRKSTRÖM
2POLIG SÄKERHETSBRYTARE FÖR DÖRRAUTOMATIK
MONTERAS I ANSLUTNING TILL AUTOMATIKEN.
GVF 1-VÄGS UTTAG PLACERAS I SKÅP FÖR
GOLVVÄRMEFÖRDELARE
DÖRRAUTOMATIK
ARMBÄGSKONTAKT, HÖJD CC +0,8

- CENTRAL
KABEL
BEFINTLIG KABEL
1 KABLAR FÖRLÄGGS I KANALISATION I MARK/PLATTA
2 SPIRAKABEL MED UTTAG FÖR MATNING TILL
LADDVAGN. DOSA OVAN UNDERTAK
3 VÄGGUTTAG PÅ DOSPLÅT PÅ KABELSTEGE FÖR
ANSLUTNING AV AKTIV SKYLTT FÖR HÖRSLINGA.
4 ANSLUTNING FLÄKTUFTVÄRME
5 MATNING TABLÅ FETTAVSKILJARE
6 MATNING SCHUNT
7 FRÄNLUFTSFLÄKT
8 MATNING KYLRUM. +1,7
9 INKOPPLING TRAFÖ FÖR BILDARE. OVAN UNDERTAK
10 MATNING VÄRMEKABEL, PLACERING SAMORDNAS
11 MATNING AVFROSTNING. +1,7
12 MONTERAS PÅ DOSPLÅT PÅ KABELSTEGE.
13 STRÖMFÖRSÖRJNING MANÖVERPANEL L.I.J.D.
ANSLUTS TILL MP ENLIGT E64ED-1-512.
14 STRÖMFÖRSÖRJNING ANSLUTS TILL INBROTTSALARM-
CENTRAL.

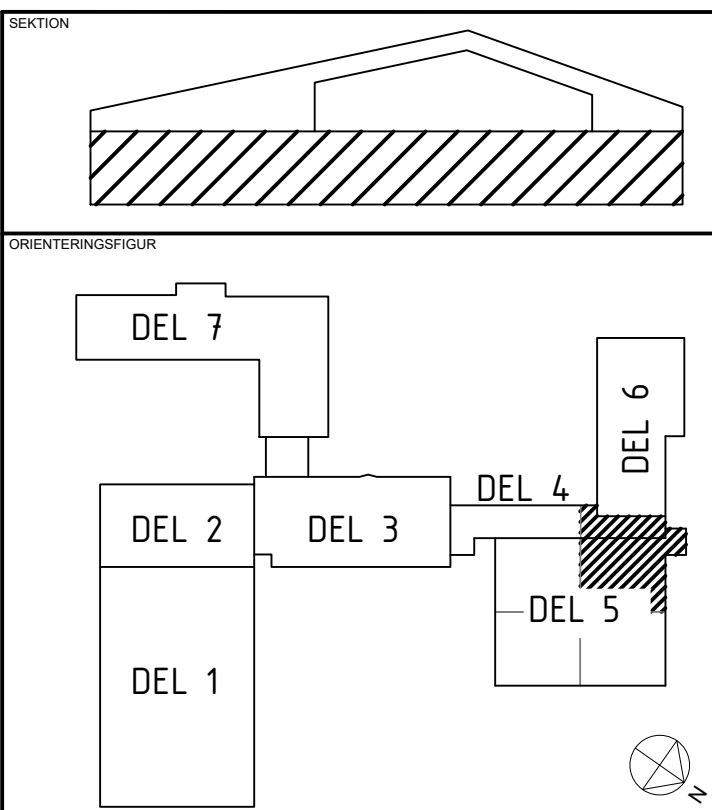

STATUS
FÖRFRÅGNINGSUNDERLAG
HANDLING
BYGGHANDLING
DATUM
2024-12-20
TODDAD AV
GIN
ÄNDRING PM
-



PROJEKTNAMN CENTRALEKÖ		
OMRÅDE ROBERTSFORS KOMMUN		
PROJEKTNUMMER	YTRE RINGVÄGEN 4	
DÄRRETNAMN	FORDONET 1	
DISCIPLIN	FÖRETAG NORCONSULT SVERIGE AB	
UPPDAGSRUMMER	1088371	SKAPAD AV GIN
TELEFON	010 141 80 00	KONTAKTPERSON TOMAS BERGSTRÖM
BYGGNADSRUM		PLÅTSÄRVTID +45,54 (FG)
VÄNINGSPLAN	1	DELNR DEL 4.2, 5.2
SYSTEM KRAFT		
SPECIFIKATION PLAN 1		
BYGGNADSRUM	PLANER	SKALA 1:50
BYGGNADSRUM	E-63BC-1-512	FORMAT A1
BYGGNADSRUM		ÄNDRING -