
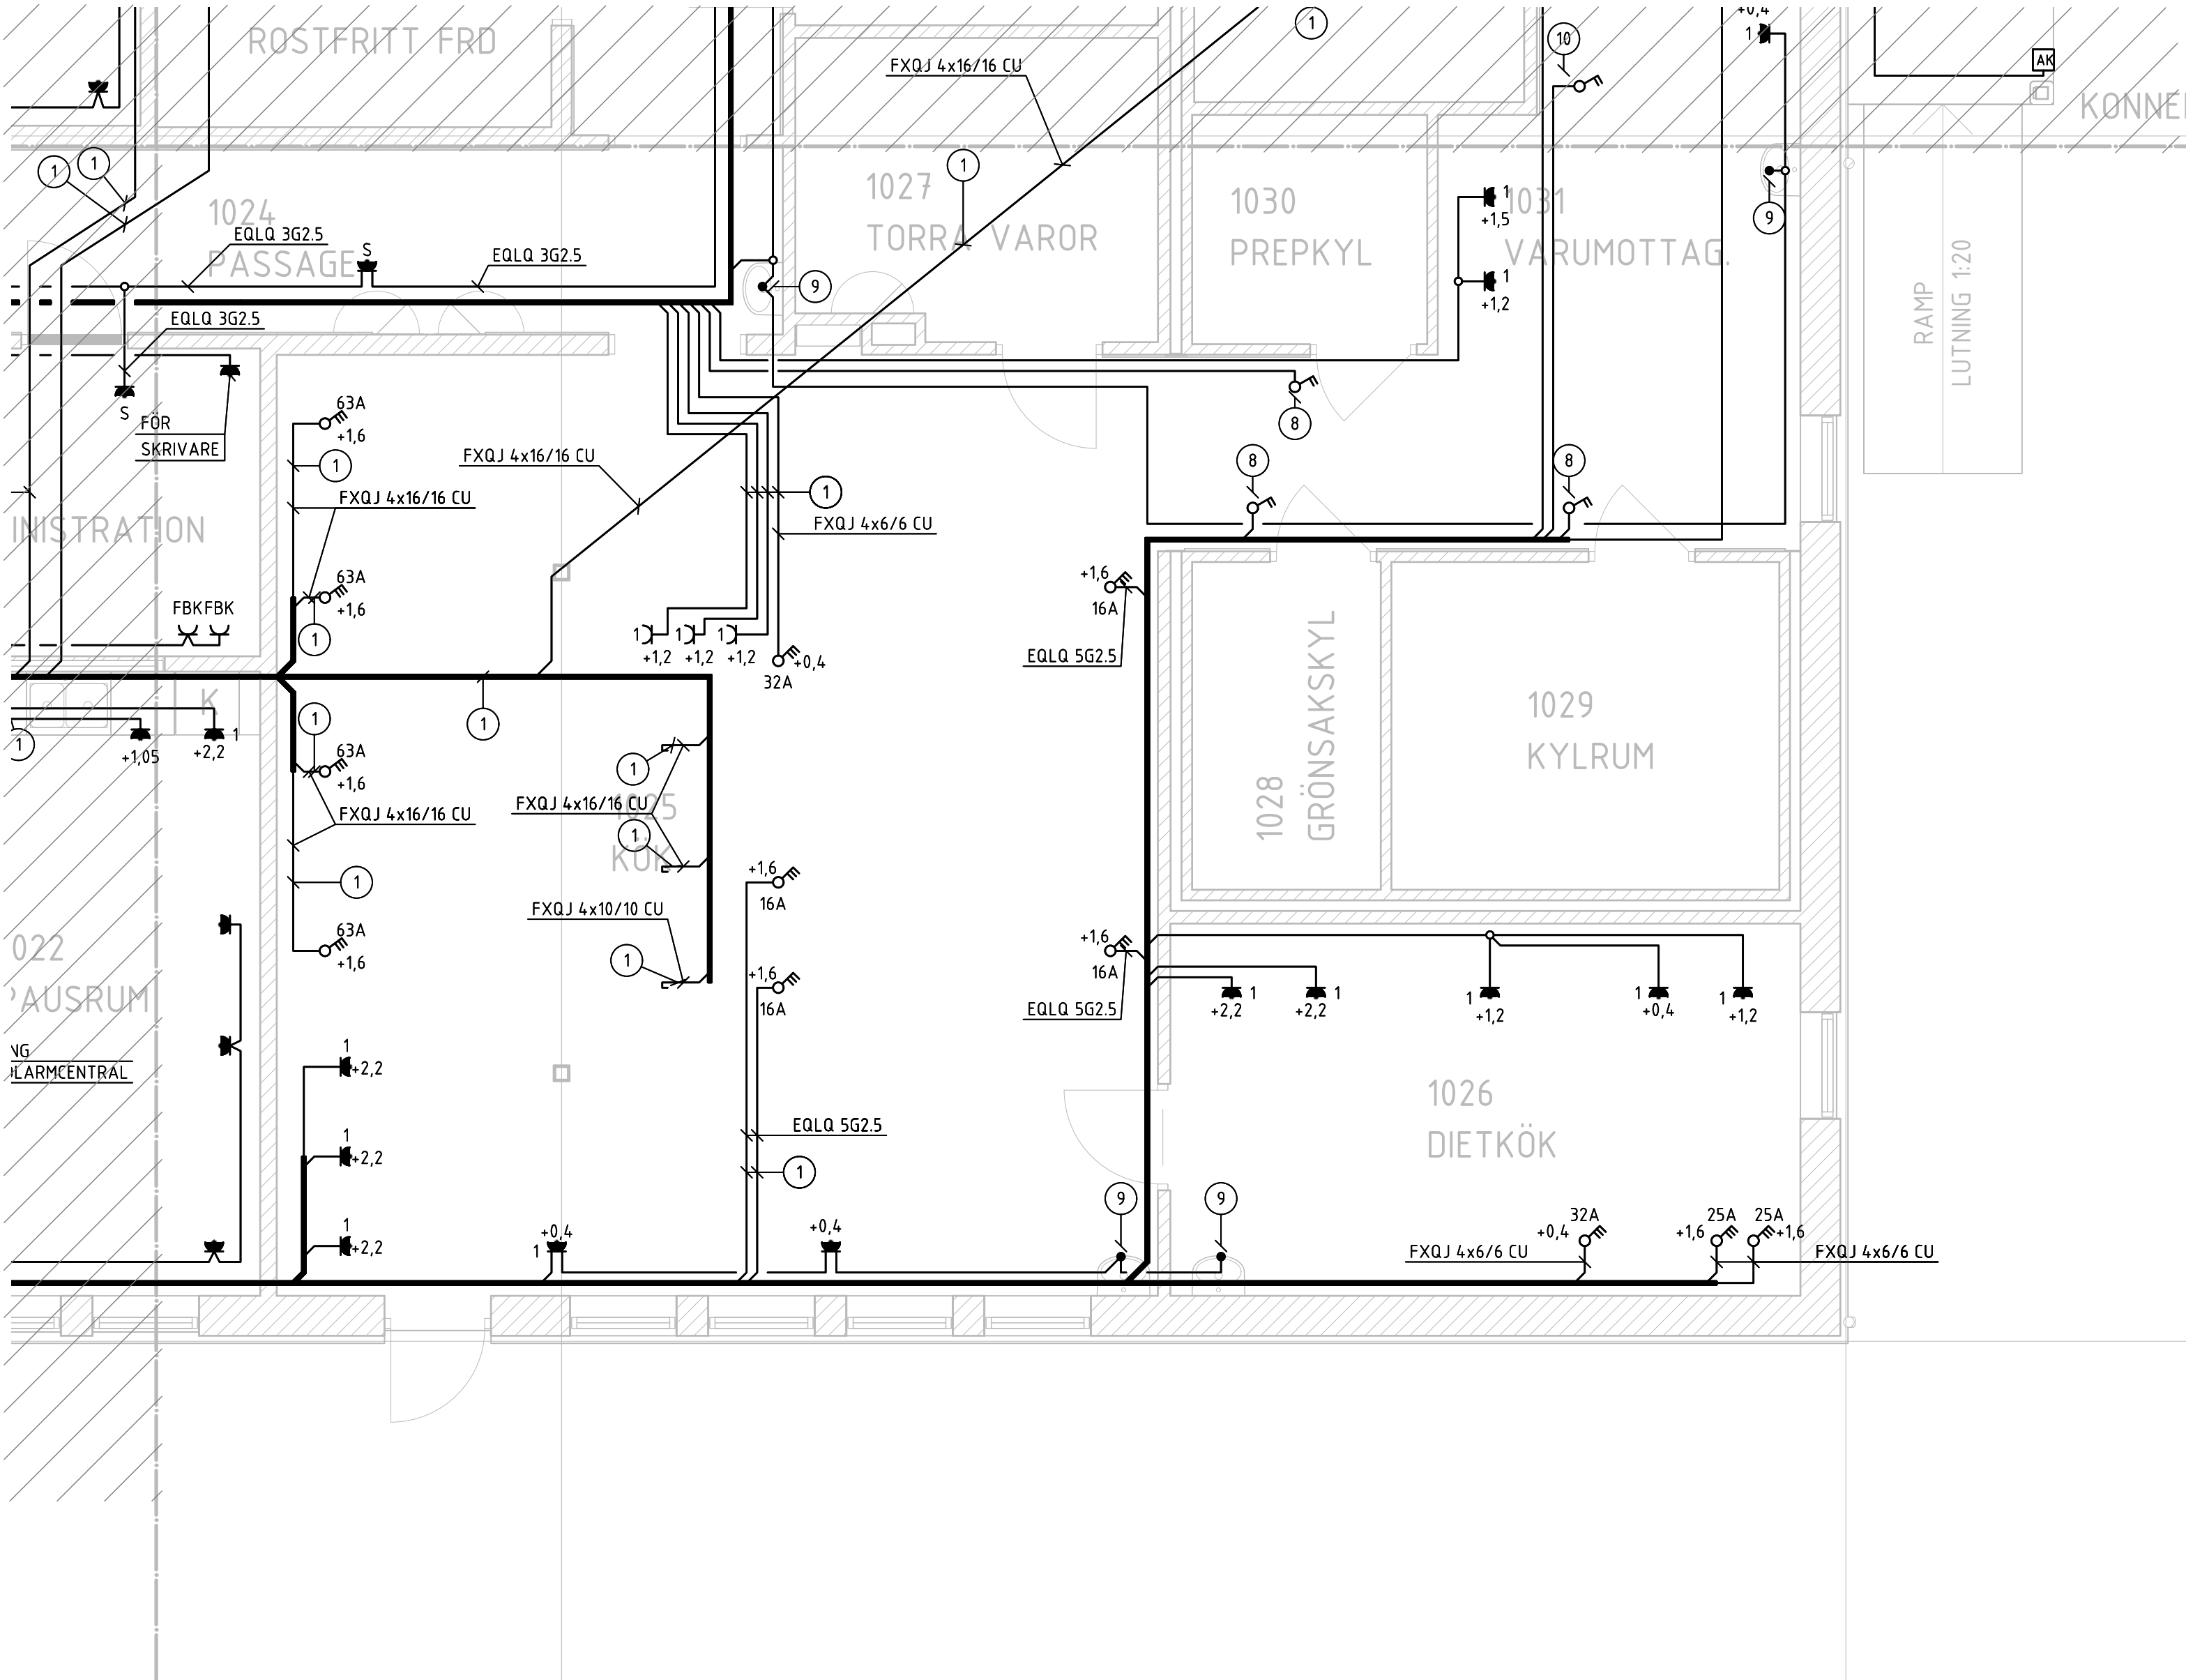


**ANVISNINGAR**  
DÄR INGET ANNAT ANGES GÄLLER:  
INFÄLLT MONTAGE PRIORITERAS DÄR BYGGNADS  
KONSTRUKTIONEN TILLÅTER. VID UPL. MONTAGE FÖRLÄGGS  
KABLAGET I EL-LIST  
BRANDTÄTNING I SAMMA KLASS SOM VÄGGENS  
BRANDKLASS.  
HÖJD ANGES METER ÖFG.  
STRÖMBRYTARE +1.0, UTTAG +0.3  
HALOGENFRITT MATERIAL  
KABEL 3G1.5  
STRECKAT AVSER BEFINTLIGT  
FYLLO SYMBOL = INFÄLLD. EJ FYLLD = UTANPÅLIGGANDE.  
**SYMBOLFÖRKLARINGAR**

- 2 VÄGS UTTAG
- 1 VÄGS UTTAG
- STÄDUTTAG 1 VÄGSUTTAG +0.9
- 2 VÄGS UTTAG PLACERAS OVAN UNDER TAK
- CEE 3FAS 16A UTTAG +1.8
- 3 VÄGS UTTAG I FÖNSTERBÄNNSKANAL
- 2POLIG SÄKERHETSBRYTARE
- 3POLIG SÄKERHETSBRYTARE MED MÄRKSTRÖM
- 2POLIG SÄKERHETSBRYTARE FÖR DÖRRAUTOMATIK  
MONTERAS I ANSLUTNING TILL AUTOMATIKEN.
- GUF 1-VÄGS UTTAG PLACERAS I SKÅP FÖR  
GOLVVÄRMEFÖRDELARE
- DÖRRAUTOMATIK
- ARBÄGSKONTAKT, HÖJD CC +0.8

- CENTRAL
- KABEL
- BEFINTLIG KABEL
- KABLAR FÖRLÄGGS I KANALISATION I MARK/PLATTA
- SPIRALKABEL MED UTTAG FÖR MATNING TILL  
LADDVAGN. DOSA OVAN UNDER TAK
- VÄGGUTTAG PÅ DOSPLÅT PÅ KABELSTEGE FÖR  
ANSLUTNING AV AKTIV SKYLTT FÖR HÖRSLINGA.
- ANSLUTNING FLÄKT/LUFTVÄRME
- MATNING TABLÅ FETTAVSKILJARE
- MATNING SCHUNT
- FRÄNLUFTSFLÄKT
- MATNING KYLRUM. +1.7
- INKOPPLING TRAFÖ FÖR BLANDARE. OVAN UNDER TAK
- MATNING VÄRMEKABEL, PLACERING SAMORDNAS
- MATNING AVFROSTNING. +1.7
- MONTERAS PÅ DOSPLÅT PÅ KABELSTEGE.
- STRÖMFÖRSÖRJNING MANÖVERPANEL L. J. J. J.
- ANSLUTS TILL MP ENLIGT E64ED.1-512.
- STRÖMFÖRSÖRJNING ANSLUTS TILL INBROTTSALARM-  
CENTRAL.

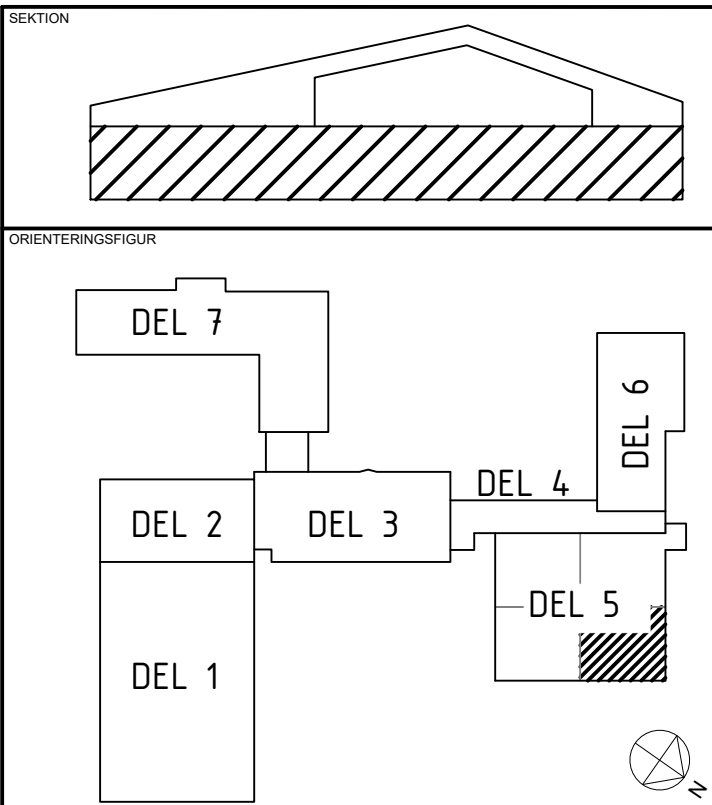

STATUS  
**FÖRFRÅGNINGSUNDERLAG**  
HANDLING  
**BYGGHANDLING**  
DATUM  
2024-12-20  
TODDAD AV  
GIN  
ÄNDRINGS PM  
-



PROJEKTNAMN  
**CENTRALEKÖK**  
OBJEKT  
**ROBERTSFORS KOMMUN**  
PROJEKTNUMMER  
ADRESS  
YTTRE RINGVÄGEN 4  
DARIENUMMER  
FASTIGHET  
FORDONET 1  
DISCIPLIN  
FÖRETAG  
NORCONSULT SVERIGE AB  
UPPDAGSRUMMER  
SKAPAD AV  
1088371  
GIN  
TELEFON  
KONTAKTPERSON  
010 141 80 00  
TOMAS BERGSTRÖM  
BYGGNADSVÄRKE  
PÅLÖSNINGSVÄRDE  
+45.54 (FG)  
VÄNINGSPLAN  
VÄNINGSDEL  
DELOMRÅDE  
1  
DEL 5.4  
SYSTEM  
KRAFT  
SPECIFIKATION  
PLAN 1  
TITEL  
PLANER  
SKALA  
1:50  
FORMAT  
A1  
DOCUMENTNUMMER  
E-63BC-1-514  
ÄNDRING  
-