

ANVISNINGAR



DÄR INGET ANNAT ANGES GÄLLER:
INFÄLLT MONTAGE PRIORITERAS DÄR BYGGNADES
KONSTRUKTIONEN TILLÅTER. VID UPL. MONTAGE FÖRLÄGGS
KABLAGET I EL-LIST
BRANDTÄTNING I SAMMA KLASS SOM VÄGGENS
BRANDKLASS.
HÖJD ANGES METER ÖFG.
STRÖMBRYTARE +1,0, UTTAG +0,3
HALOGENFRITT MATERIAL
KABEL 3015
STRECKAT AVSER BEFINTLIGT
FYLLD SYMBOL = INFÄLLD. EJ FYLLD = UTANPÅLIGGANDE.

SYMBOLFÖRKLARINGAR

- 2VÄGS UTTAG
1VÄGS UTTAG
STÅDUTTAG 1VÄGSUTTAG +0,9.
2VÄGS UTTAG PLACERAS OVAN UNDERTAK
CEE 3FAS 16A UTTAG +1,8
3VÄGS UTTAG I FÖNSTERBÄNKSCHANAL
2POLIG SÄKERHETSBRYTARE
3POLIG SÄKERHETSBRYTARE MED MÄRKSTRÖM
2POLIG SÄKERHETSBRYTARE FÖR DÖRRAUTOMATIK
MONTERAS I ANSLUTNING TILL AUTOMATIKEN.
GVF 1-VÄGS UTTAG PLACERAS I SKÅP FÖR
GOLVVÄRMEFÖRDELARE
DÖRRAUTOMATIK
ARMBÄGSKONTAKT, HÖJD CC +0,8

- CENTRAL
KABEL
BEFINTLIG KABEL

- 1 KABLÄR FÖRLÄGGS I KANALISATION I MARK/PLATTA
2 SPIRALKABEL MED UTTAG FÖR MATNING TILL
LADDVAGN. DOSA OVAN UNDERTAK
3 VÄGGUTTAG PÅ DOSPLÅT PÅ KABELSTEGE FÖR
ANSLUTNING AV AKTIV SKYLTVÄRME
4 ANSLUTNING FLÄKTUFTVÄRME
5 MATNING TABLÅ FETTAVSKILJARE
6 MATNING SCHUNT
7 FRÄNLUFTSFLÄKT
8 MATNING KYLRUM. +1,7
9 INKOPPLING TRAFÖ FÖR BLANDARE. OVAN UNDERTAK
10 MATNING VÄRMEKABEL, PLACERING SAMORDNAS
11 MATNING AVFROSTNING. +1,7
12 MONTERAS PÅ DOSPLÅT PÅ KABELSTEGE.
13 STRÖMFÖRSÖRJNING MANÖVERPANEL I LUD.
ANSLUTS TILL MP ENLIGT E64ED-1-S12.
14 STRÖMFÖRSÖRJNING ANSLUTS TILL INBROTTSALARM-
CENTRAL.

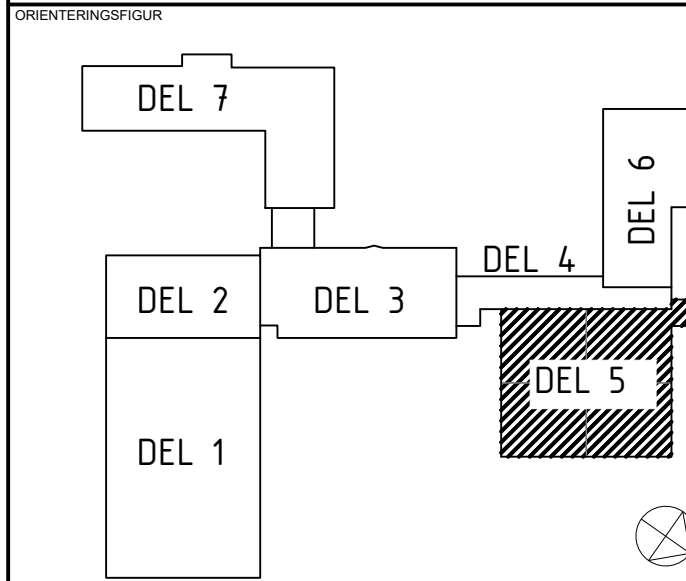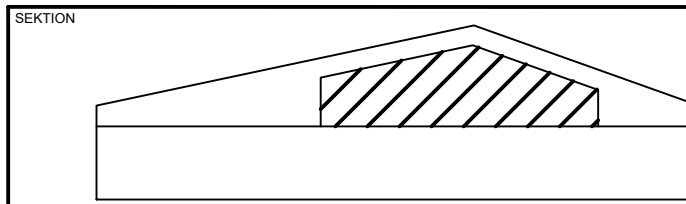

STATUS
FÖRFRÅGNINGSUNDERLAG
HANDLING
BYGGHANDLING
DATUM
2024-12-20
TODDAD AV
GIN
ÄNDRINGS PM
-



PROJEKTNAMN
CENTRALEKÖ
OMRÄDE
ROBERTSFORS KOMMUN
PROJEKTNUMMER
YTRE RINGVÄGEN 4
DARIENUMMER
FORDONET 1
DISCIPLIN
FÖRETAG
NORCONSULT SVERIGE AB
UPPDRAGSNUMMER
1088371
SKAPAD AV
GIN
TELEFON
010 141 80 00
KONTAKTPERSON
TOMAS BERGSTRÖM
BYGGNADSVÄRK
+45,54 (FG)
VÄNINGSPLAN
2
VÄNINGSDEL
DELOMRÅDE
DEL 5
SYSTEM
KRAFT
SPECIFIKATION
PLAN 2
SKALA
1:50
FORMAT
A1
DOCUMENTNUMMER
E-63BC-1-521
ÄNDRING
-

