


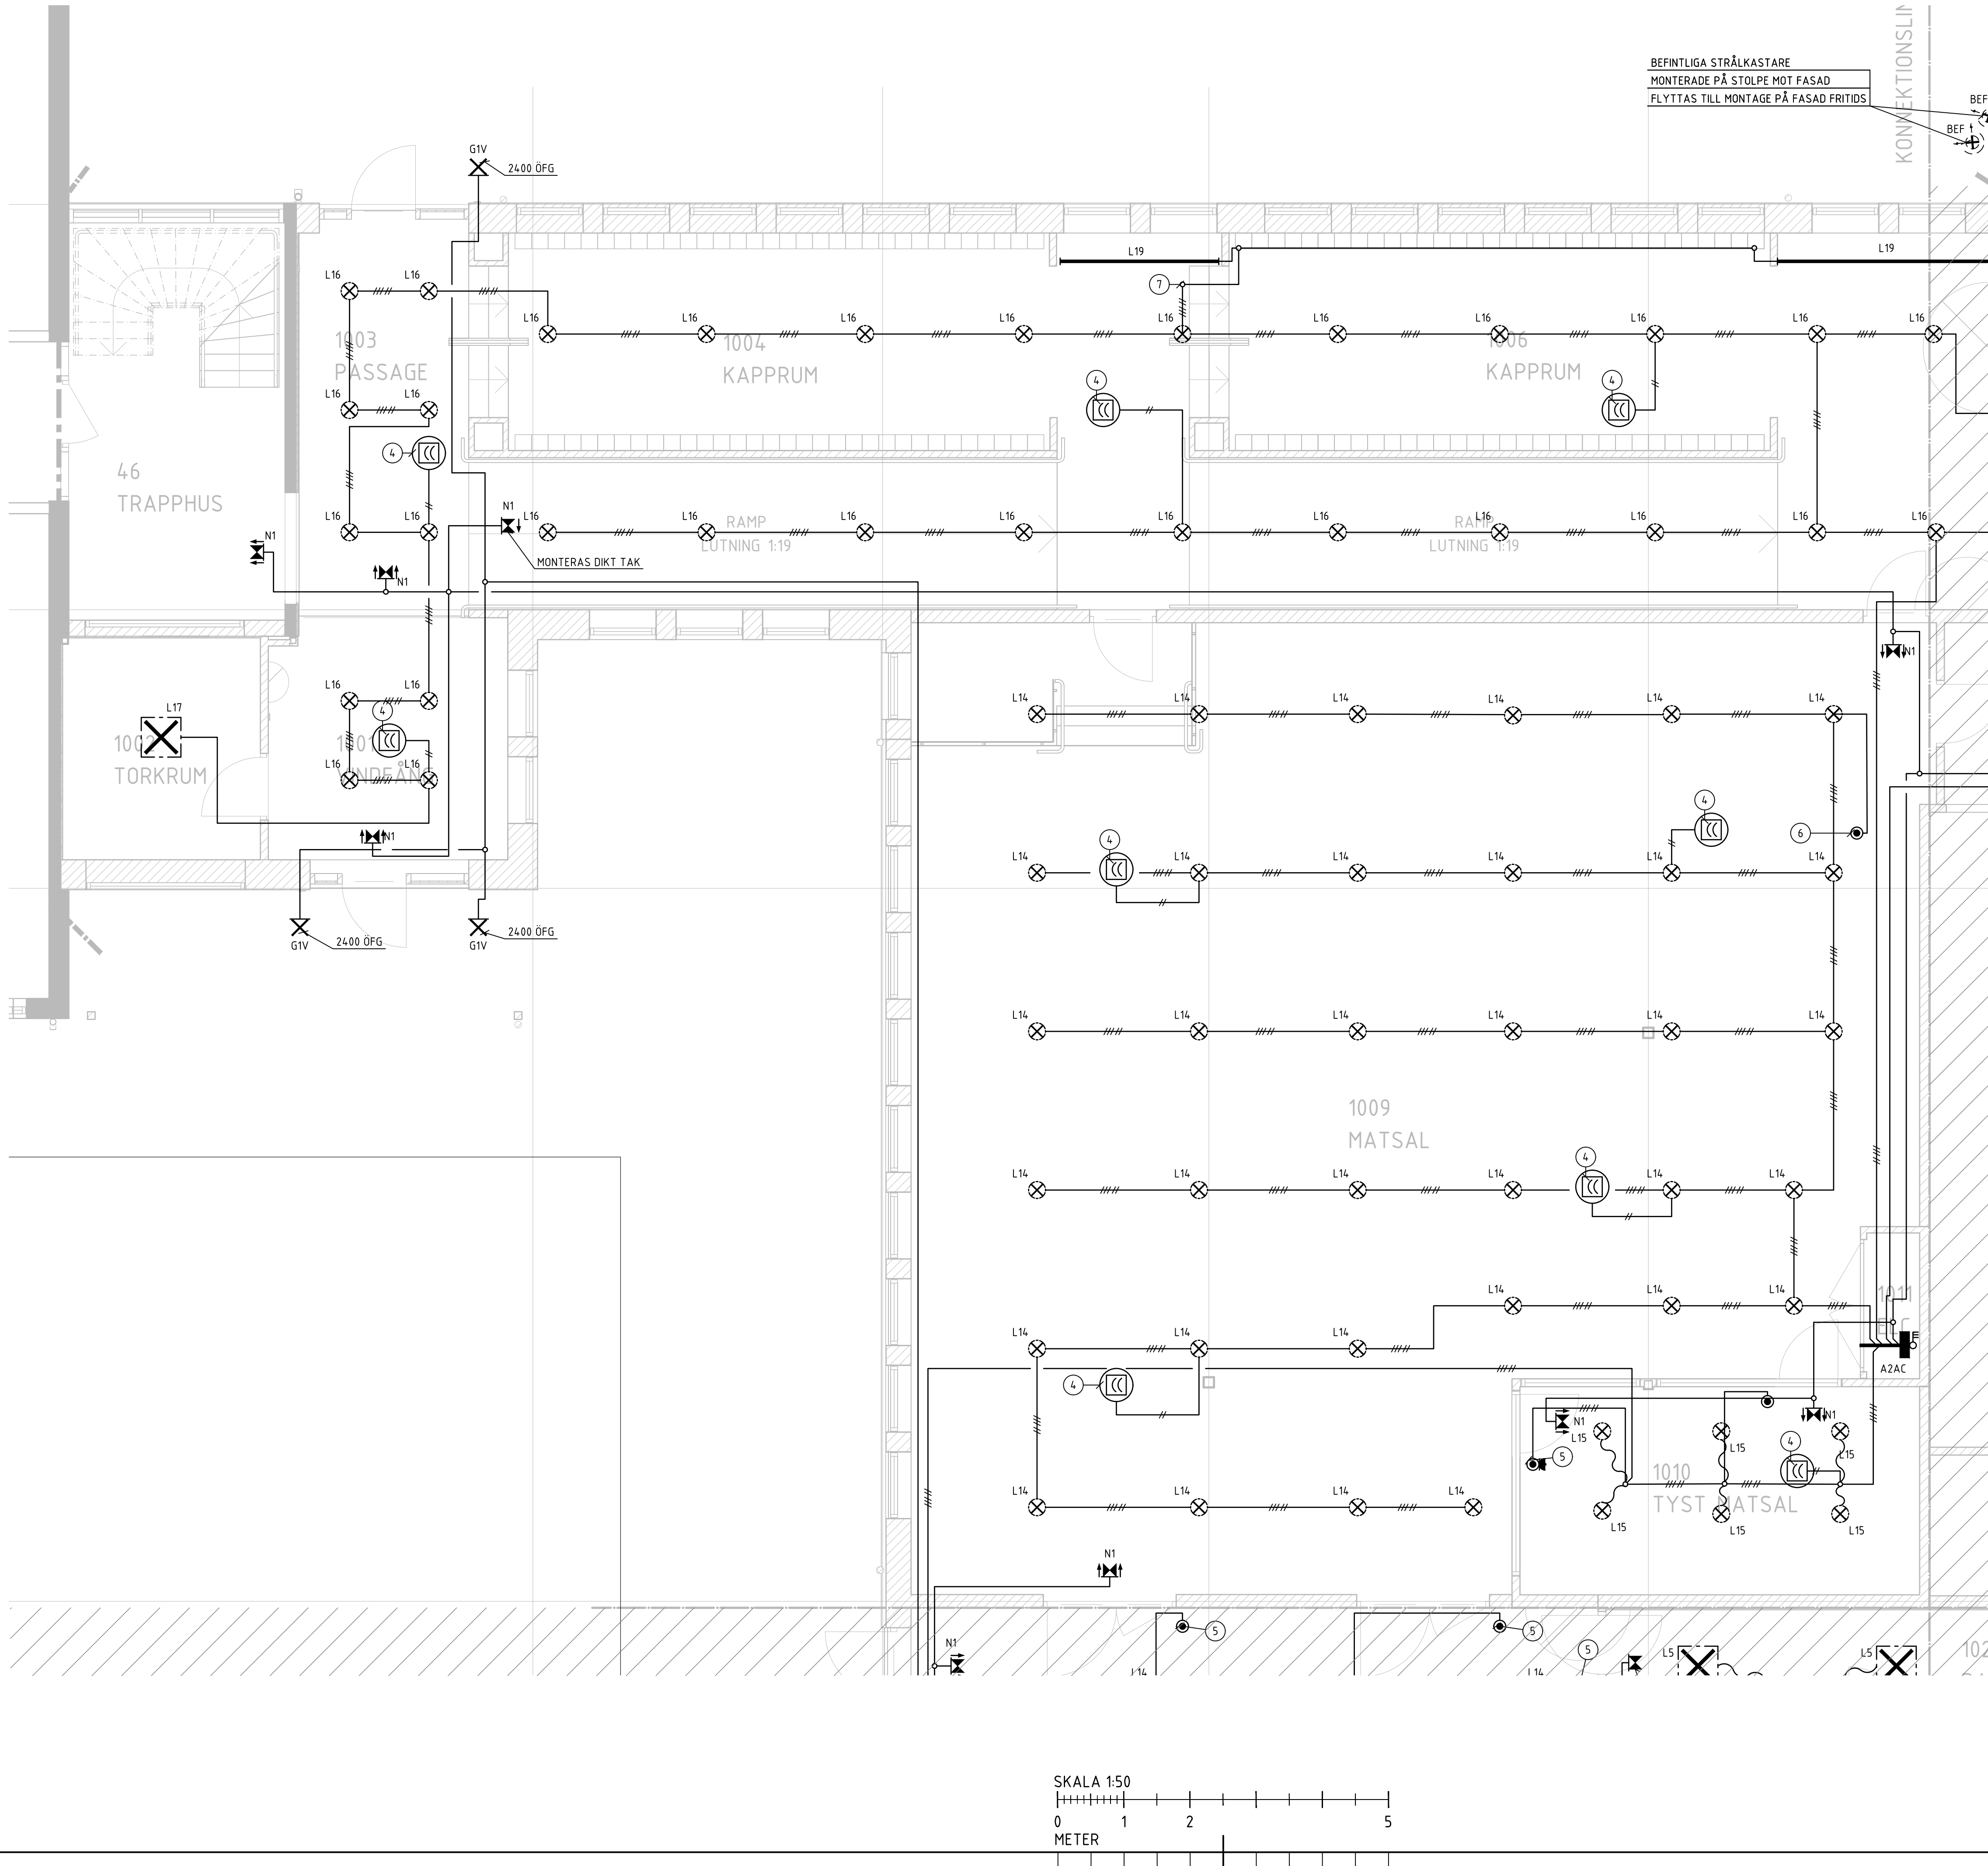

BEFINTLIGA STRÅLKASTARE  
MONTERADE PÅ STOLPE MOT FASAD  
FLYTAS TILL MONTAGE PÅ FASAD FRITIDS

ANVISNINGAR  
DÄR INGET ANNAT ANGES GÄLLER:  
HALOGENFRITT MATERIAL  
KABEL 3G15  
HÖJD ANGES I METER.

SYMBOLFÖRKLARINGAR

- STRÖMSTÄLLARE IPOLIG
- STRÖMSTÄLLARE KRON
- STRÖMSTÄLLARE TRAPPKOPPLING
- STRÖMSTÄLLARE DIMMER
- TRYCKKNAPP

- 1 ANSLUTNING AV BELYSNING I KYL-/FRYSRUM
- 2 UTTAG FÖR LADDNING AV HANDLAMP 0,5 M.Ö.G.
- 3 ANSLUTNING AV BEFINTLIG LEDNING TILL STOLPBELYSNING.
- 4 PIR-SENSOR TYP HELVAR 320 E17 046 29
- 5 ÅTERFJÄDRANDE TRYCKKNAPP MED INGÅNGSENHET HELVAR MINI 444 E17 045 88
- 6 SCENMODUL HELVAR 136W + RAM 2305

HÄNVISNINGAR  
SE ÄVEN:  
- ARMATURFÖRTECKNING

SEKTION

ORIENTERINGSFIGUR

STATUS

HANDLING

DATUM

2024-12-20

TECKNAD AV

GIN

ÄNDRINGS PM

-

ROBERTSFORS KOMMUN

PROJEKTNAMN

CENTRALEKÖ

OBJÄGDE

ROBERTSFORS KOMMUN

PROJEKTNUMMER

YTTRE RINGVÄGEN 4

DÄRRETNUMMER

FORDONET 1

DISCIPLIN

E

FORETAG

NORCONSULT SVERIGE AB

UPPDRAGSNUMMER

1088371

SKAPAD AV

GIN

TELEFON

010 141 80 00

KONTAKTPERSON

TOMAS BERGSTRÖM

BYGGNADSVÄRDE

+45,54 (FG)

VÄNINGSPLAN

1

VÄNINGSDEL

DEL 4.1, 5.1

SYSTEM

BELYSNING

SPECIFIKATION

PLAN 1

SKALA

1:50

FORMAT

A1

DOCUMENTNUMMER

E-63F-1-511

ÄNDRING

-