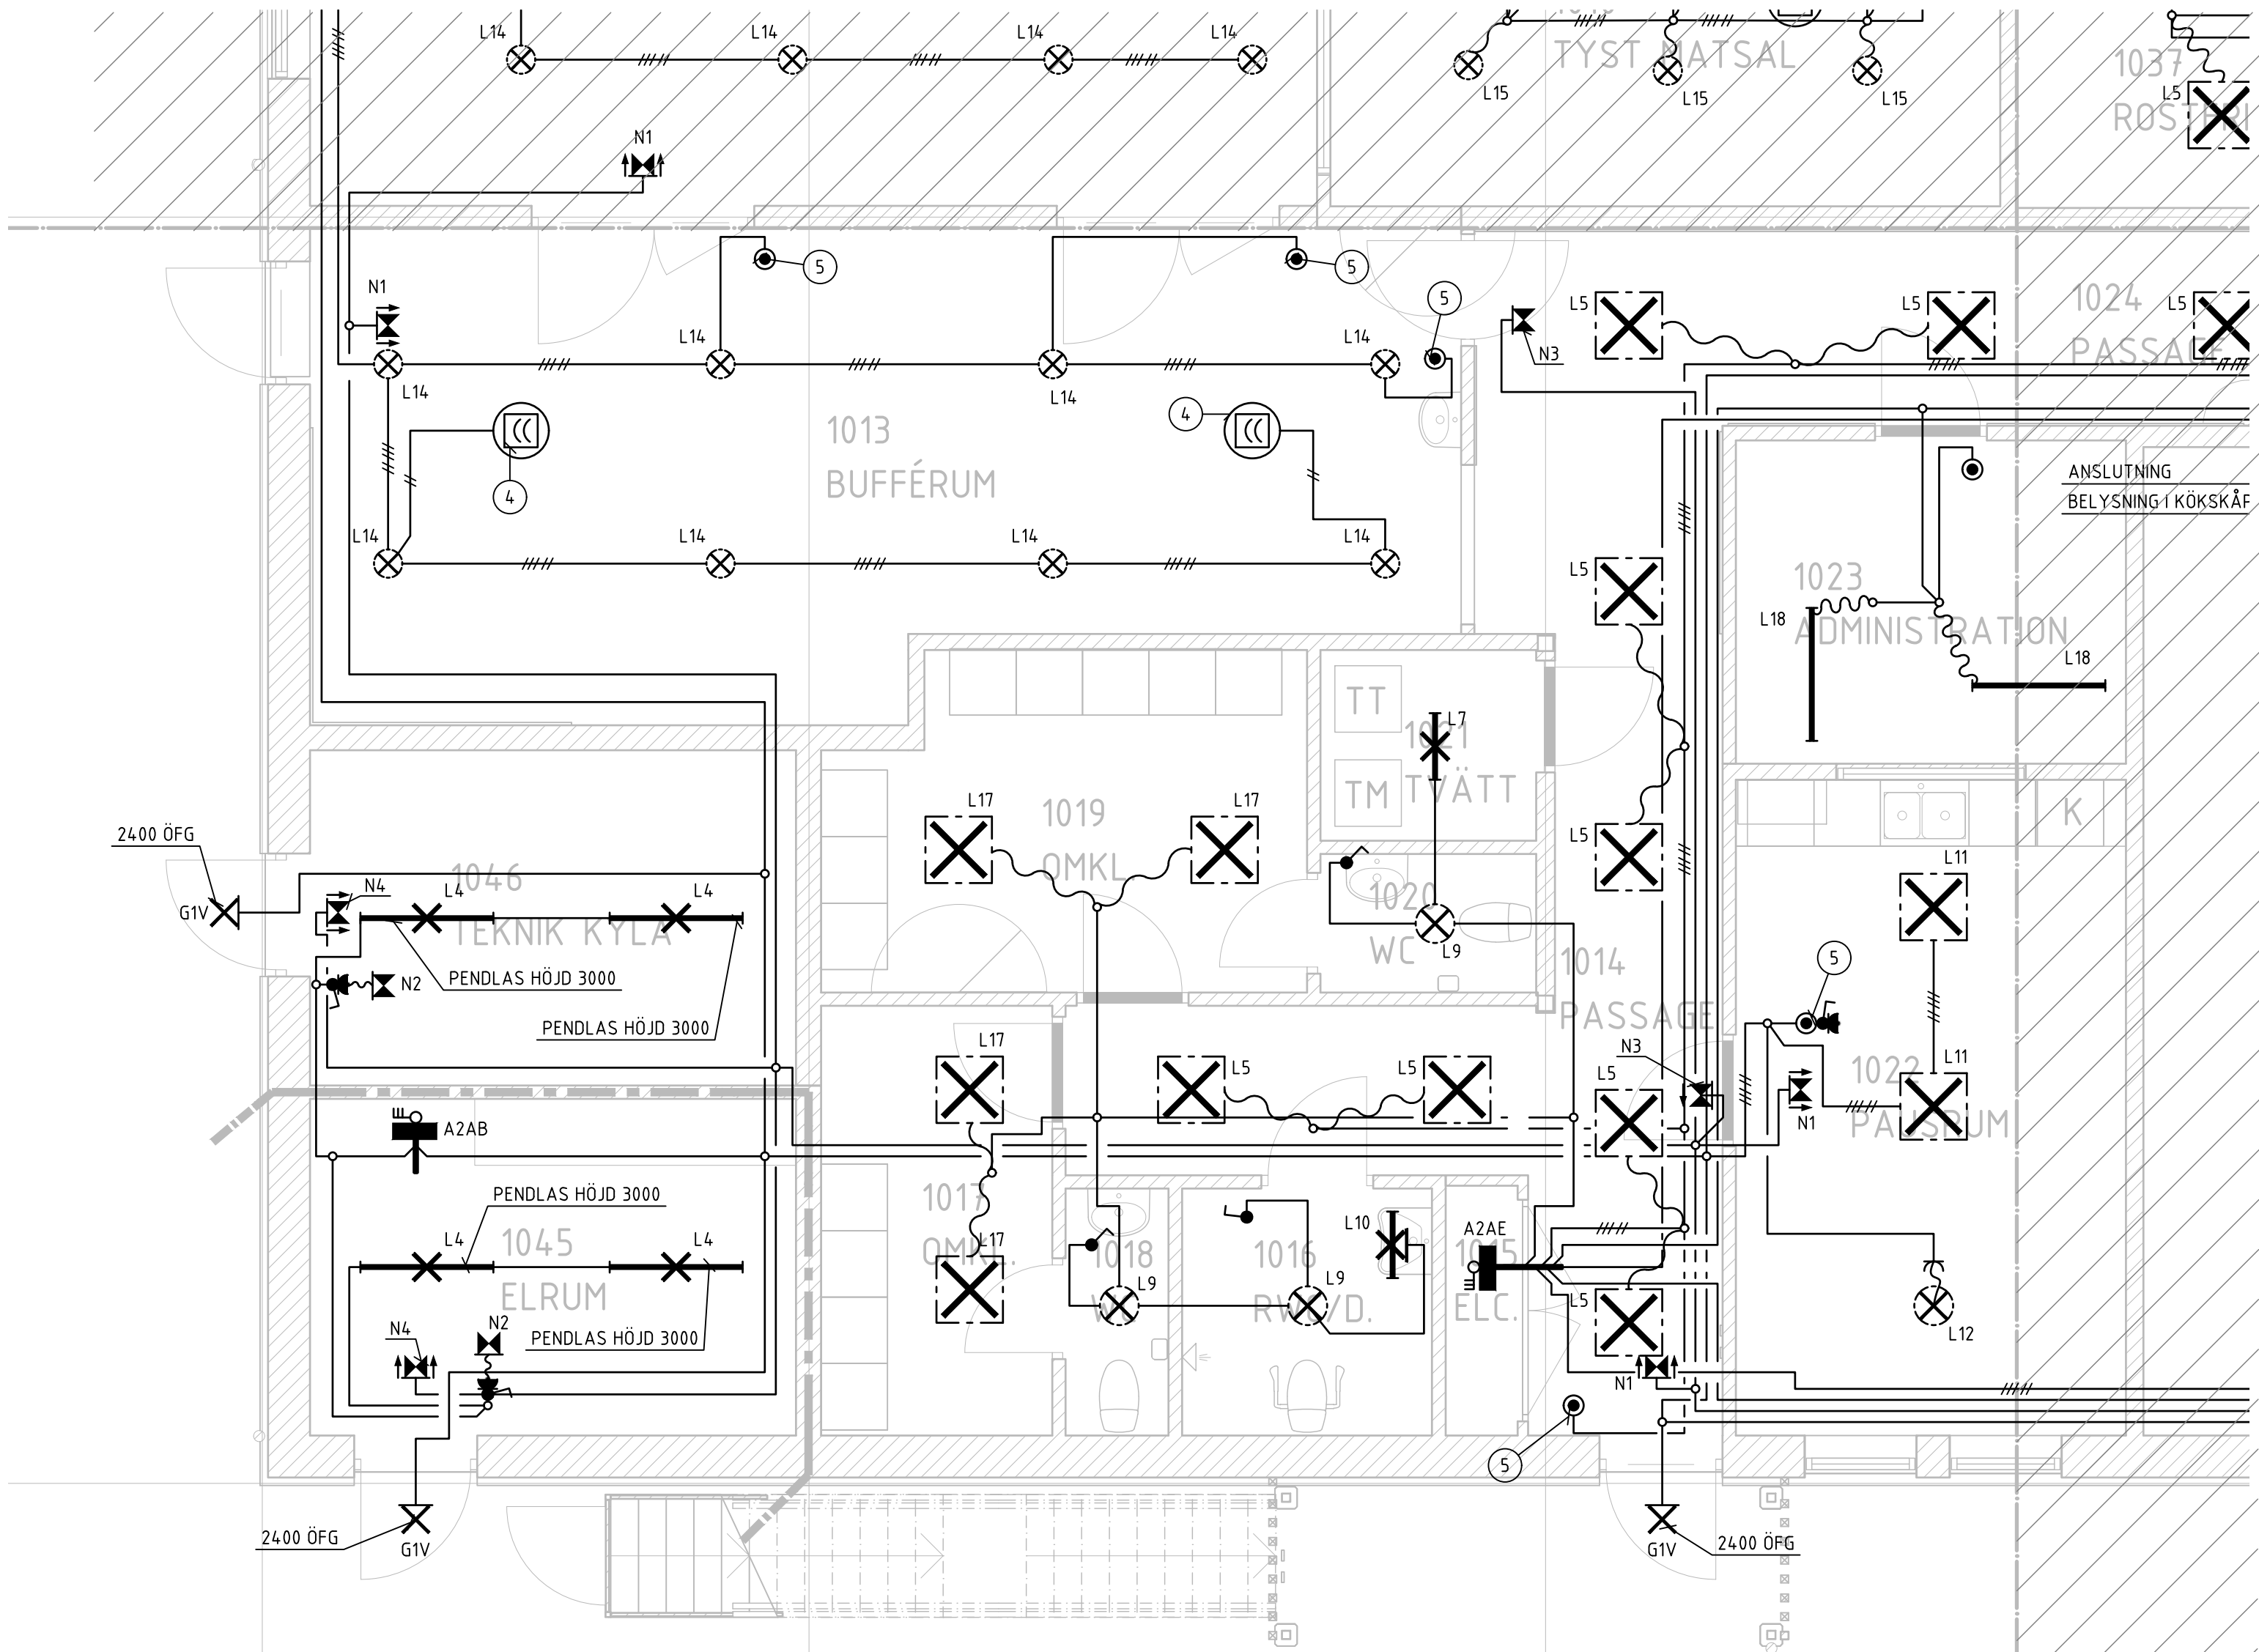


ANVISNINGAR
DÄR INGET ANNAT ANGES GÄLLER:
HALOGENFRITT MATERIAL
KABEL 3G15
HÖJD ANGES I METER.


SYMBOLFÖRKLARINGAR

- STRÖMSTÄLLARE IPOLIG
- STRÖMSTÄLLARE KRON
- STRÖMSTÄLLARE TRAPPKOPPLING
- STRÖMSTÄLLARE DIMMER
- TRYCKKNAPP

- ANSLUTNING AV BELYSNING I KYL-/FRYSRUM
- UTTAG FÖR LADDNING AV HANDLAMP 0,5 M.Ö.G.
- ANSLUTNING AV BEFINTLIG LEDNING TILL STOLPBELYSNING.
- PIR-SENSOR TYP HELVAR 320 E17 046 29
- ÅTERFJÄDRANDE TRYCKKNAPP MED INGÅNGSENHET
HELVAR MINI 444 E17 045 88
- SCENMODUL HELVAR 136W + RAM 2305

HÄNVISNINGAR

- SE ÄVEN:
- ARMATURFÖRTECKNING

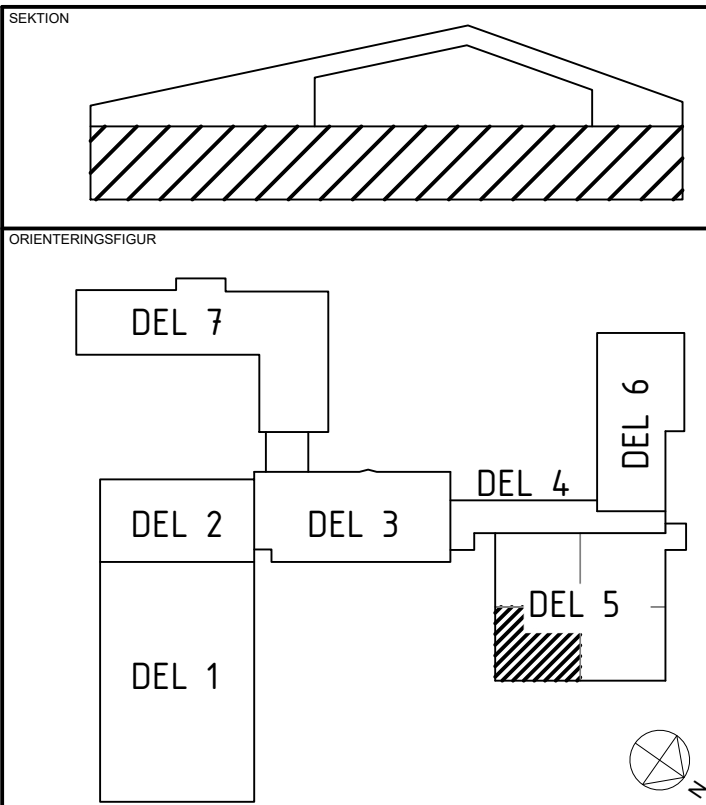

STATUS
FÖRFRÅGNINGSUNDERLAG

HANDLING
BYGGHANDLING

DATUM
2024-12-20

SKAPAD AV
GIN

ÄNDRINGS PM
-



PROJEKTNAMN
CENTRALEKÖK

OMRÅDE
ROBERTSFORS KOMMUN

PROJEKTNUMMER
ADRESS
YTRE RINGVÄGEN 4

DÄRRETNAMN
FASTIGHET
FORDONET 1

DISCIPLIN
FÖRETAG
NORCONSULT SVERIGE AB

UPPDRAGSNUMMER
SKAPAD AV
1088371 GIN

TELEFON
KONTAKTPERSON
010 141 80 00 TOMAS BERGSTRÖM

BYGGNADSVÄRDE
FÖLJESKIVOR (2024)
+45,54 (FG)

VÄNINGSPLAN
VÄNINGSDEL
DELOMRÅDE
1 DEL 5.3

SYSTEM
BELYSNING

SPECIFIKATION
PLAN 1

SKALA
1:50

FORMAT
A1

ANSÖKNING
E-63F-1-513

ÄNDRING
-