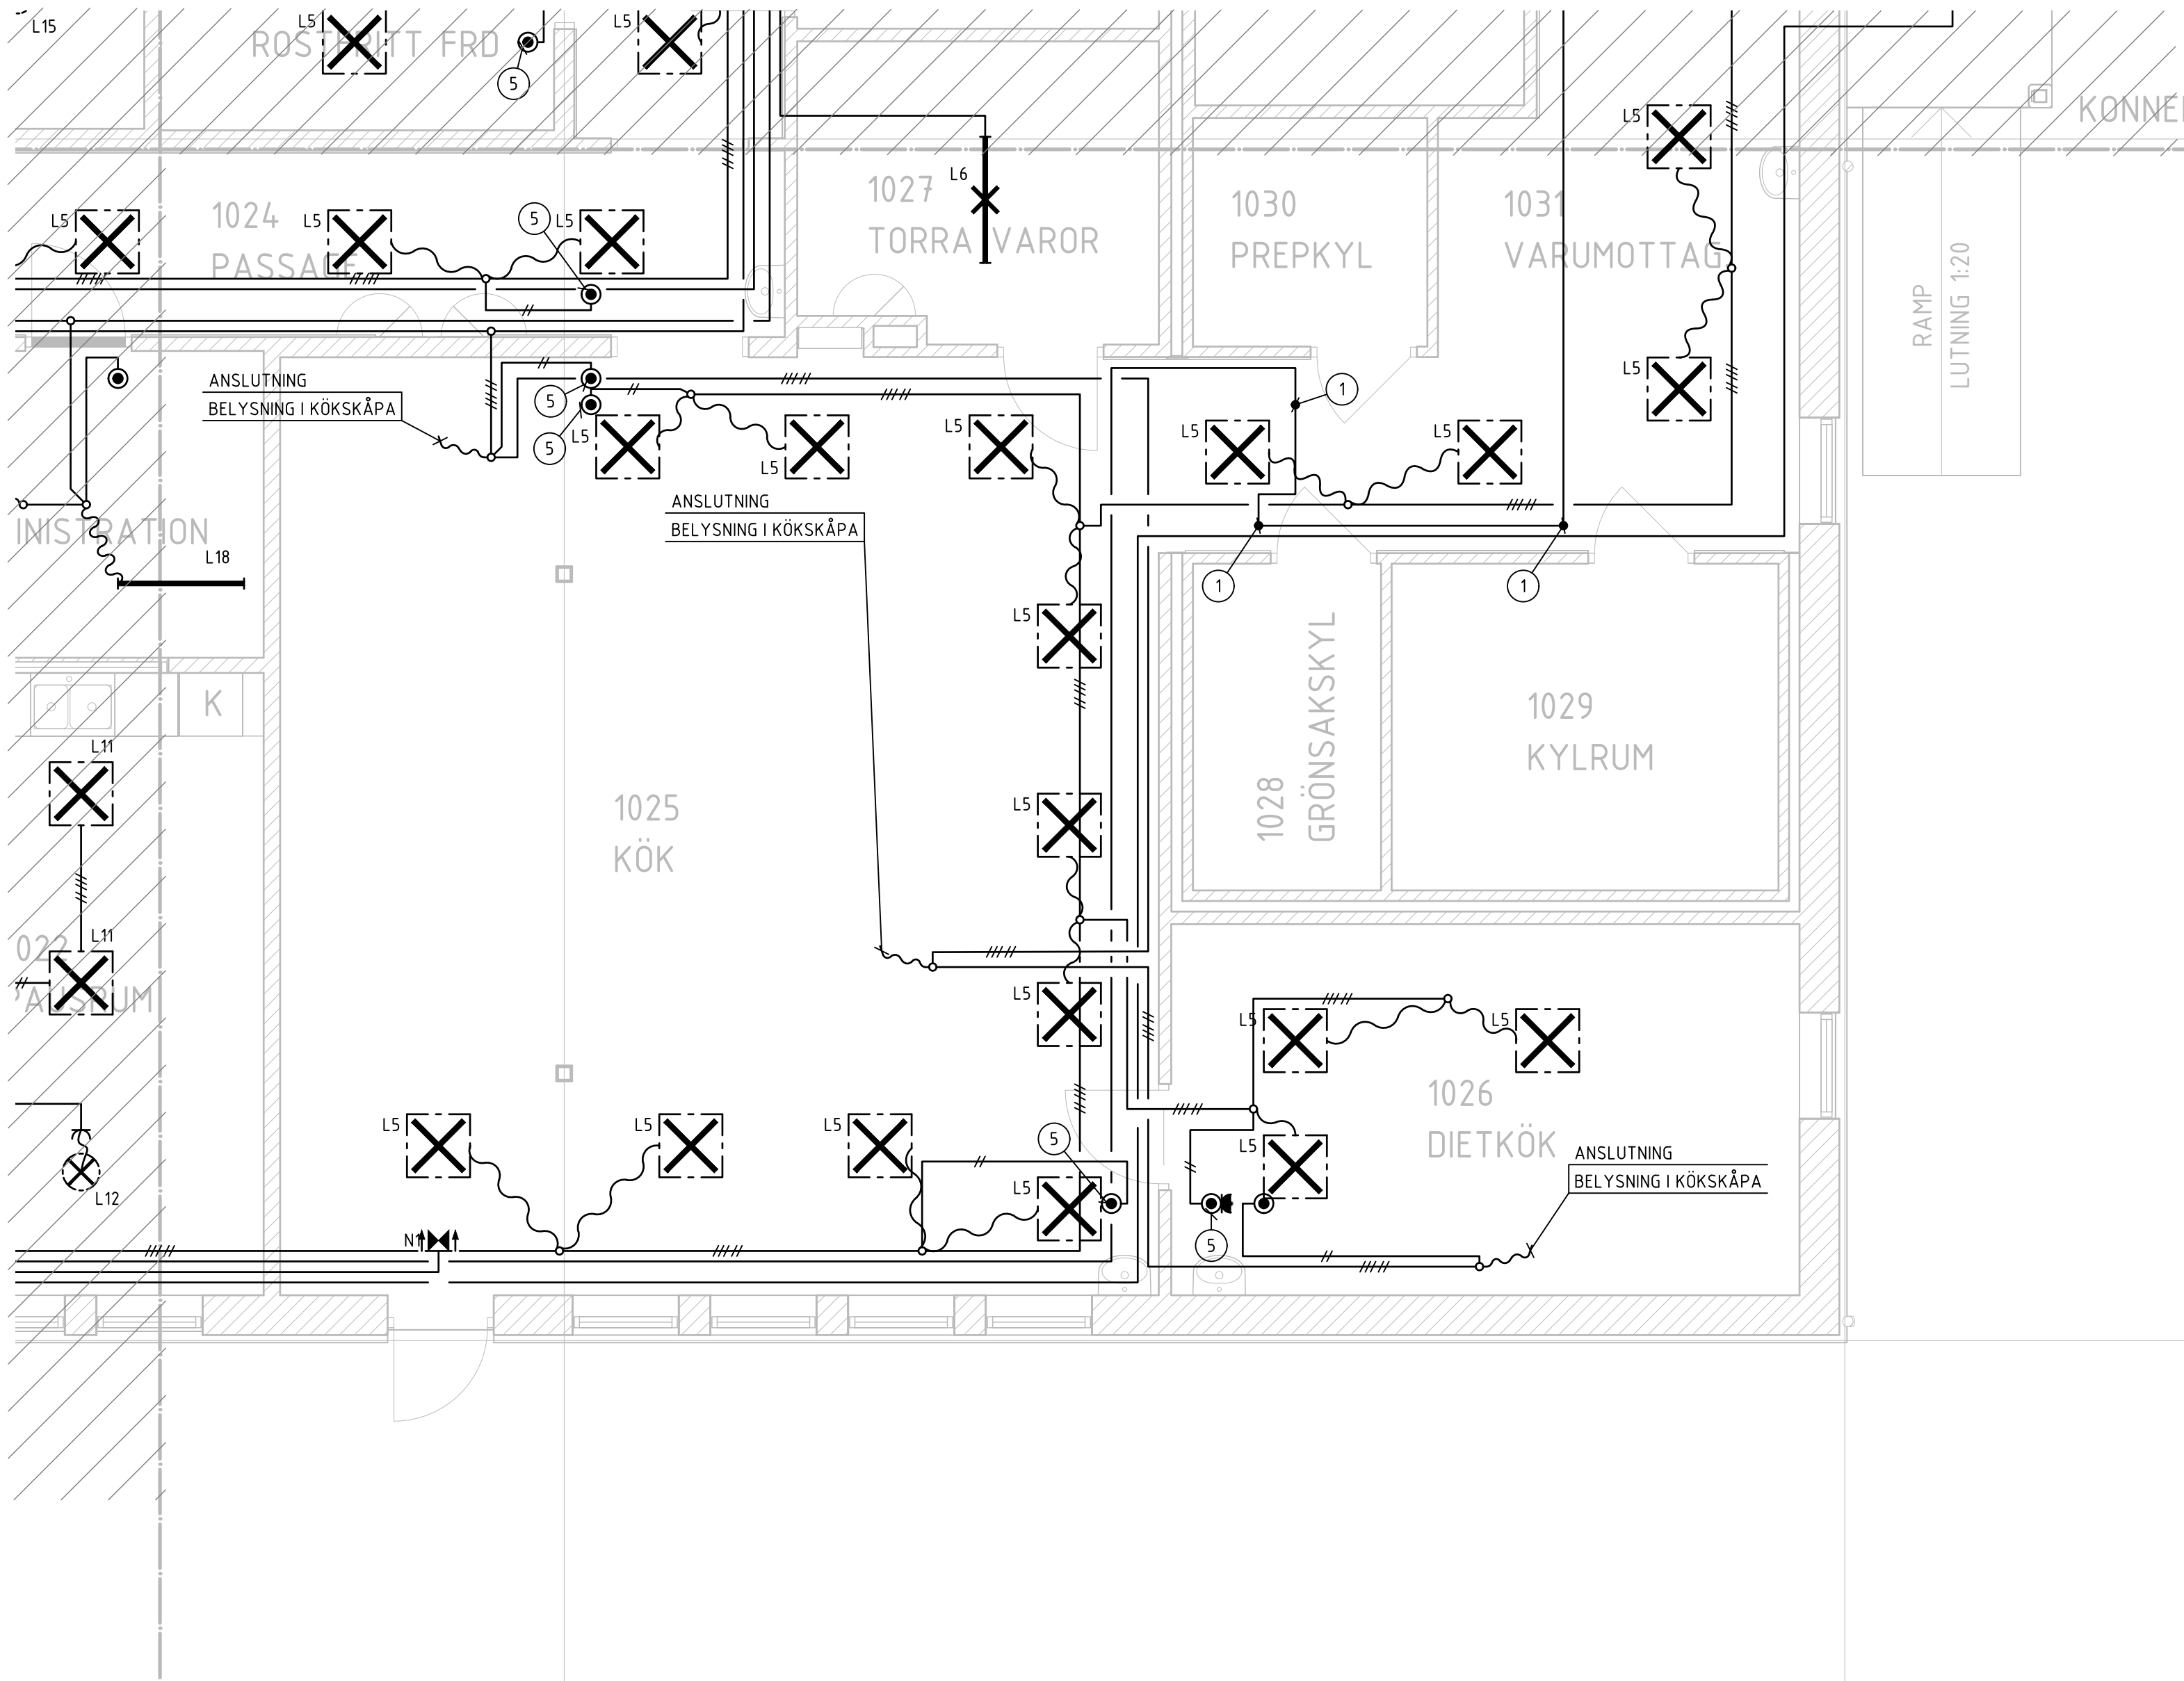


ANVISNINGAR
DÄR INGET ANNAT ANGES GÄLLER:
HALOGENFRITT MATERIAL
KABEL 3G15
HÖJD ANGES I METER.

SYMBOLFÖRKLARINGAR

- STRÖMSTÄLLARE IPOLIG
- STRÖMSTÄLLARE KRON
- STRÖMSTÄLLARE TRAPPKOPPLING
- STRÖMSTÄLLARE DIMMER
- TRYCKKNAPP

- ANSLUTNING AV BELYSNING I KYL-/FRYSRUM
- UTTAG FÖR LADDNING AV HANDLAMPA 0,5 M.Ö.G.
- ANSLUTNING AV BEFINTLIG LEDNING TILL STOLPBELYSNING.
- PIR-SENSOR TYP HELVAR 320 E17 046 29
- ÅTERFJÄDRANDE TRYCKKNAPP MED INGÅNGSENHET
HELVAR MINI 444 E17 045 88
- SCENMODUL HELVAR 136W + RAM 2305

HÄNVISNINGAR
SE ÄVEN:
- ARMATURFÖRTECKNING

SEKTION

ORIENTERINGSFIGUR

STATUS

FÖRFRÅGNINGSUNDERLAG

HANDLING

BYGGHANDLING

DATA

2024-12-20

LOPPAD AV

GIN

ÄNDRINGS PM

-

BESTÄLLARE

ROBERTSFORS KOMMUN

PROJEKTNAMN

CENTRALEKÖK

OMRÅDE

ROBERTSFORS KOMMUN

PROJEKTNUMMER

ADRESS

YTTRE RINGVÄGEN 4

DÄRRETNAMN

FASTIGHET

FORDONET 1

DISCIPLIN

FÖRETAG

NORCONSULT SVERIGE AB

UPPDRAGSNUMMER

SKAPAD AV

1088371

GIN

TELEFON

KONTAKTPERSON

010 141 80 00

TOMAS BERGSTRÖM

BYGGNADSVÄRDE

FÖLJESKIVOR (2024)

+45,54 (FG)

VÄNINGSPLAN

VÄNINGSDEL

DELOMRÅDE

1

DEL 5.4

SYSTEM

BELYSNING

SPECIFICATION

PLAN 1

BYGGNADSVÄRDE

PLANER

SKALA

1:50

FORMAT

A1

DOCUMENTNUMMER

ÄNDRING

E-63F-1-514

-