


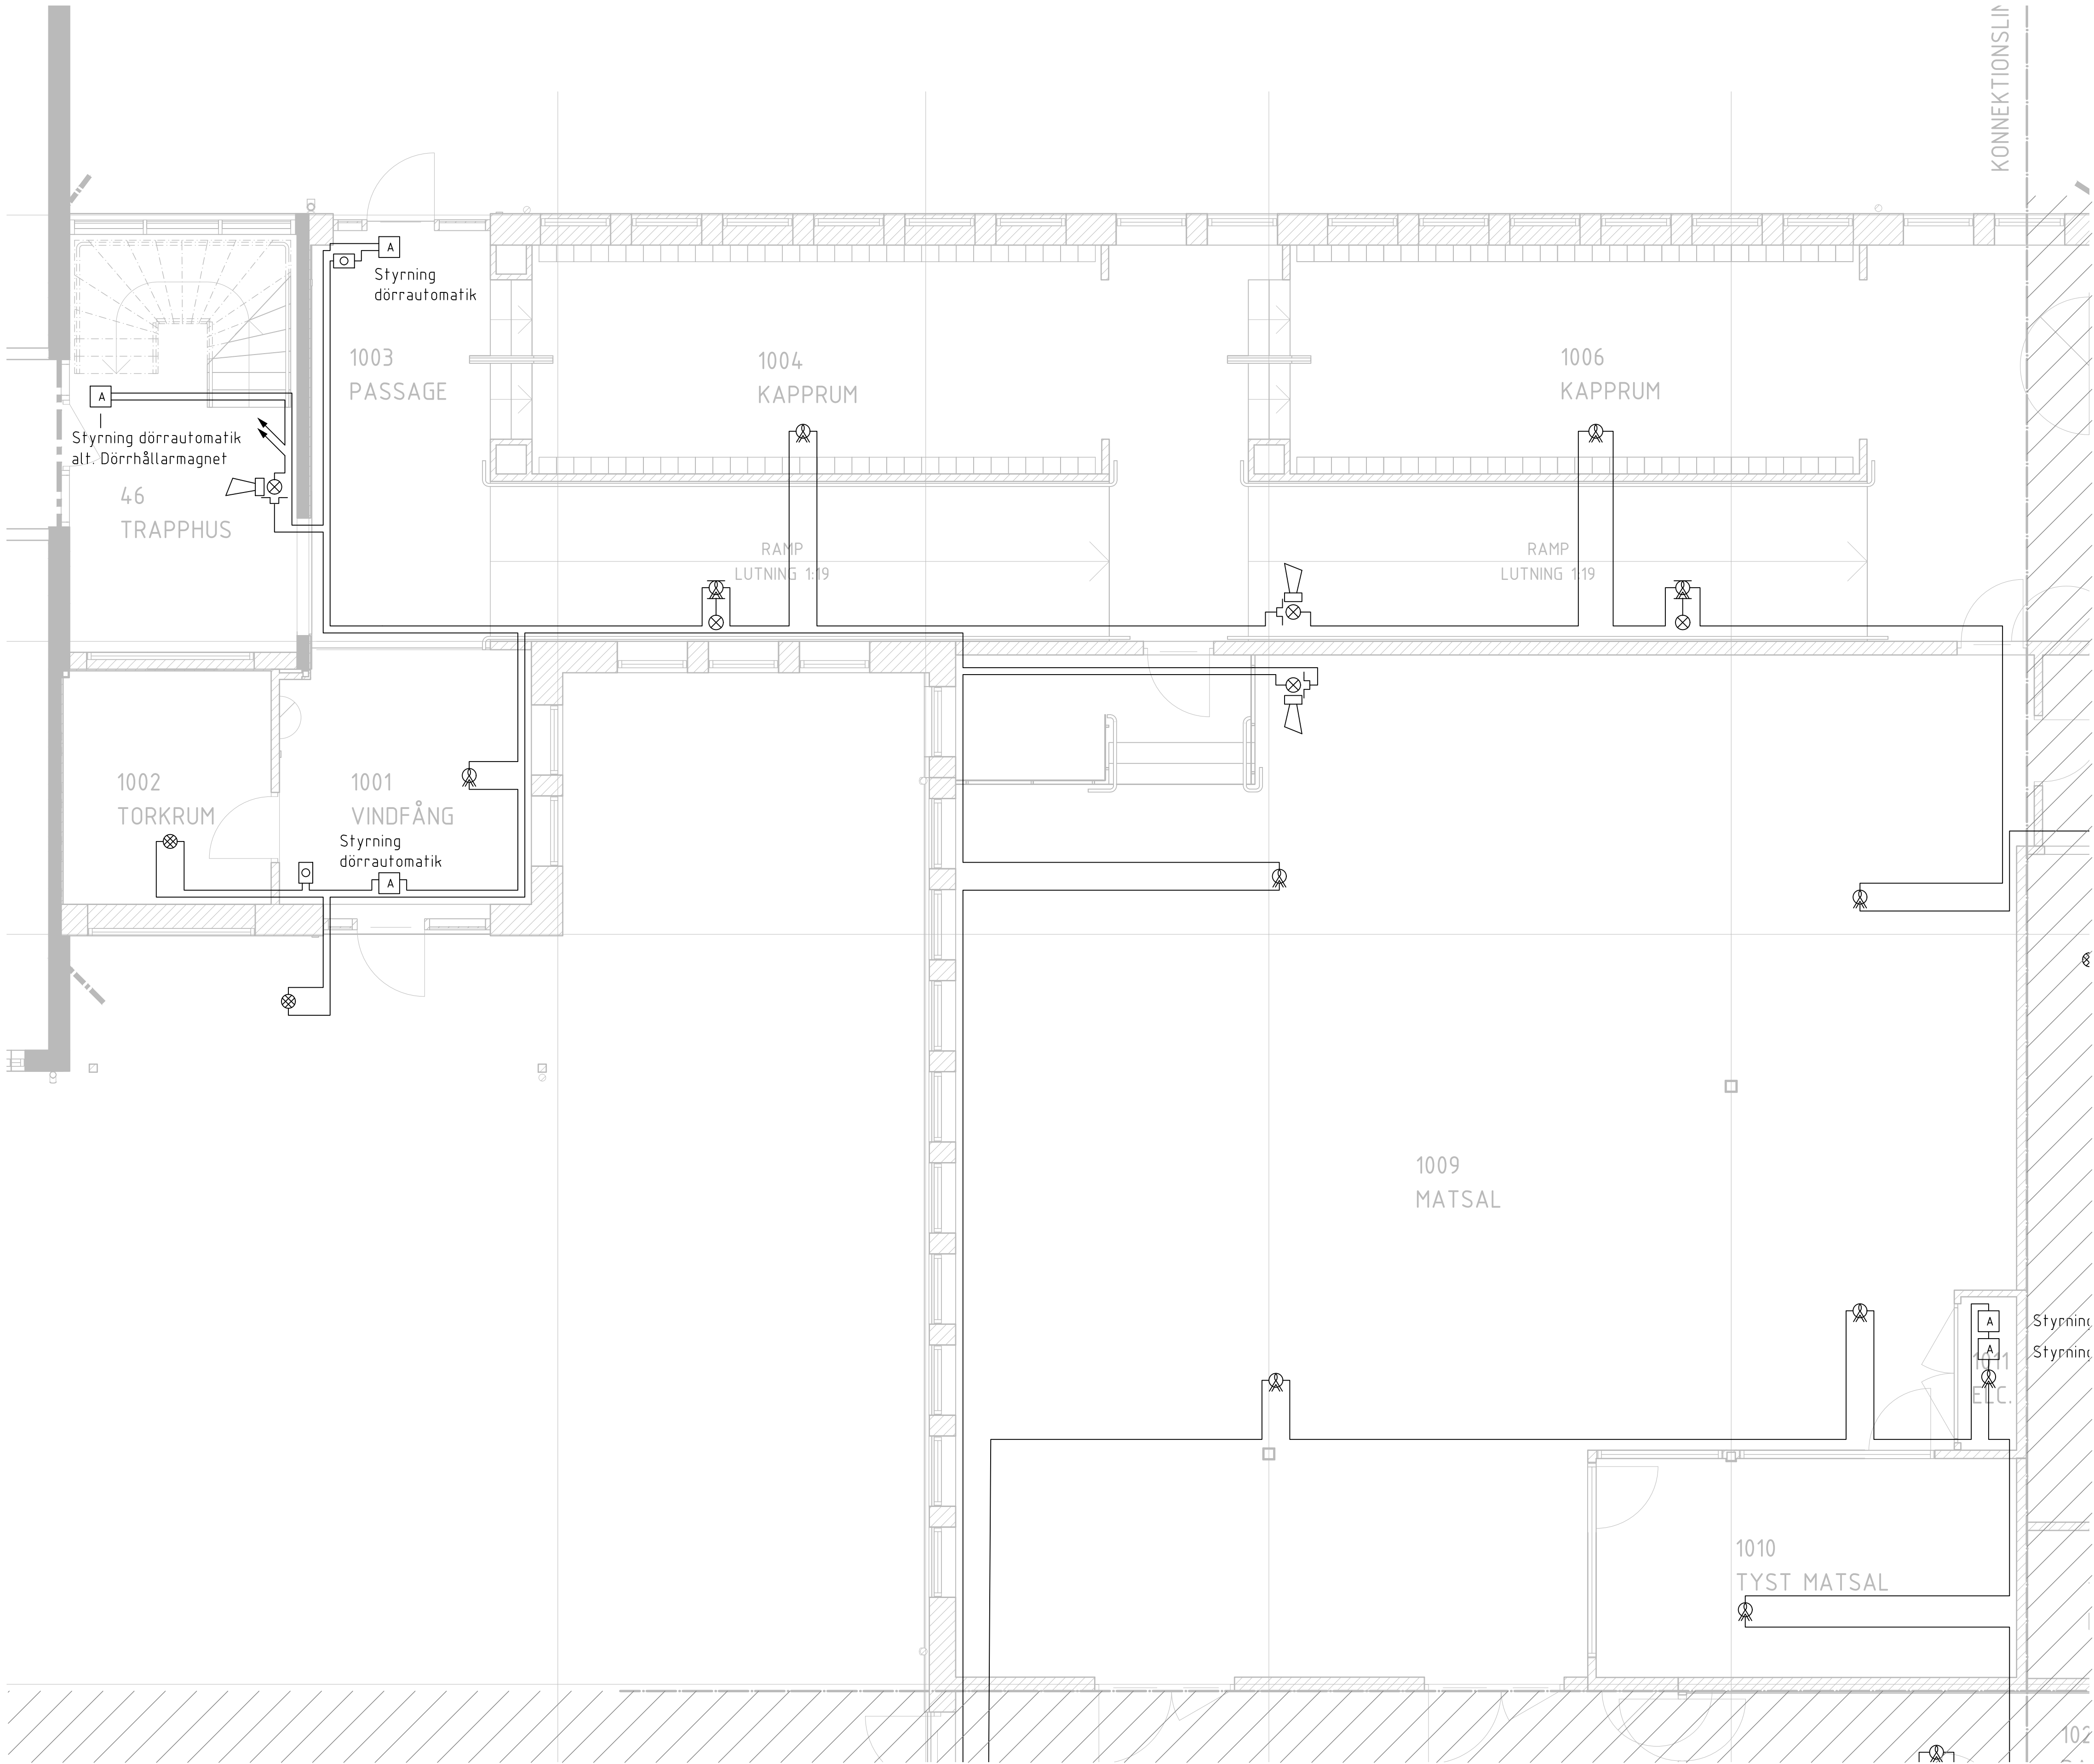


ANVISNINGAR
DETEKTORER MONTERAS DIKT TAK/UNDERTAK DÄR EJ
ANNAT ANGES.
EXAKT PLACERING DETEKTORER ANPASSAS EFTER:
MIN 0,5m - FRÄNLUFTSDON, VÄGG, ARMATUR ELLER ANNAT
SOM INTE ÄR INFALLT I TAK/UNDERTAK.
ADRESSENHETER MONTERAS OVAN UNDERTAK I EGEN
KAPSLING.
INDIKERING "DOLD DETEKTOR" MONTERAS PÅ VÄGG I TAK-
VINKEL ALT. I UNDERTAKS RAMVERK I ANSLUTNING TILL
DETEKTOR.
SAMTLIGA LÄRMDON MONTERAS PÅ VÄGG 100mm NEDAN
UNDERTAK DÄR EJ ANNAT ANGES.
KABELSTRÄK GENOM VÄGG BRANDTÄTAS MED SAMMA
BRANDKLÄSSNING SOM VÄGG.

KABEL DÄR EJ ANNAT ANGES: ELQYB 2X1 RÖD

SYMBOLFÖRKLARINGAR

- CA BRANDLARMSCENTRAL / BFT
- LS LARMSÄNDARE
- RÖKDETEKTOR ADRESSERBAR
- DOLD RÖKDETEKTOR ADRESSERBAR
- HISSBAR DETEKTOR
- INDIKERING DOLD DETEKTOR
- RÖKDETEKTOR MED MÄTKAMMARE
MONTERAS I VENTILATIONSAGGREGAT
- KAPSLAD VÄRMEDETEKTOR ADRESSERBAR
- KAPSLAD VÄRMEDETEKTOR KONVENTIONELL
- A ADRESSENHET
- BIBRANDSKÄP, MONTERAS +1200mm ÖG
- KOMBILÄRMDON BLIXT/SIREN,
MONTERAS +2300 ÖG
- ROTORLJUS RÖD, IP65, MONTERAS +3500mm ÖM
- NS NYCKELSKÄP, MONTERAS I VÄGG +1800mm ÖM

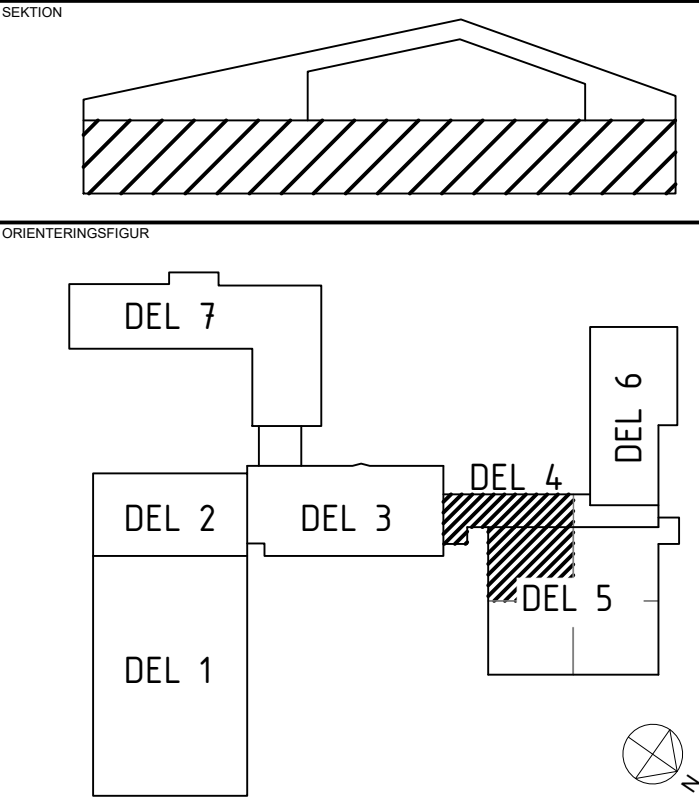

STATUS
FÖRFRÅGNINGSUNDERLAG
HANDLING
BYGGHANDLING
DATUM: 2024-12-20
TIOGRAND AV: T. BERGSTRÖM
ÄNDRINGS PM: -
BESTÄLLARE:



PROJEKTNAMN		CENTRALEKÖK	
OBJEKT		ROBERTSFORS KOMMUN	
PROJEKTNUMMER		YTTRE RINGVÄGEN 4	
DIARENUMMER		FASTIGHET FORDONET 1	
DISCIPLIN		FÖRETAG NORCONSULT SVERIGE	
UPPDRAGSNUMMER		SKAPAD AV OPN	
1088371			
TELEFON		KONTAKTPERSON TOMAS BERGSTRÖM	
010 141 80 00			
BYGGNADSVÄRDE		PÅSKYDDSD (RM 2000) +45,54 (FG)	
VÄNINGSPLAN		DELNUMMER	
1		DEL 4.1, 5.1	
SYSTEM		BRAND- & UTRYMNINGSLARM	
SPECIFIKATION			
PLAN 1			
RITNINGSKATEGORI		SKALA	FORMAT
PLANER		1:50	A1
E-64CBB-1-511			ÄNDRING
DOKUMENTNUMMER			-

