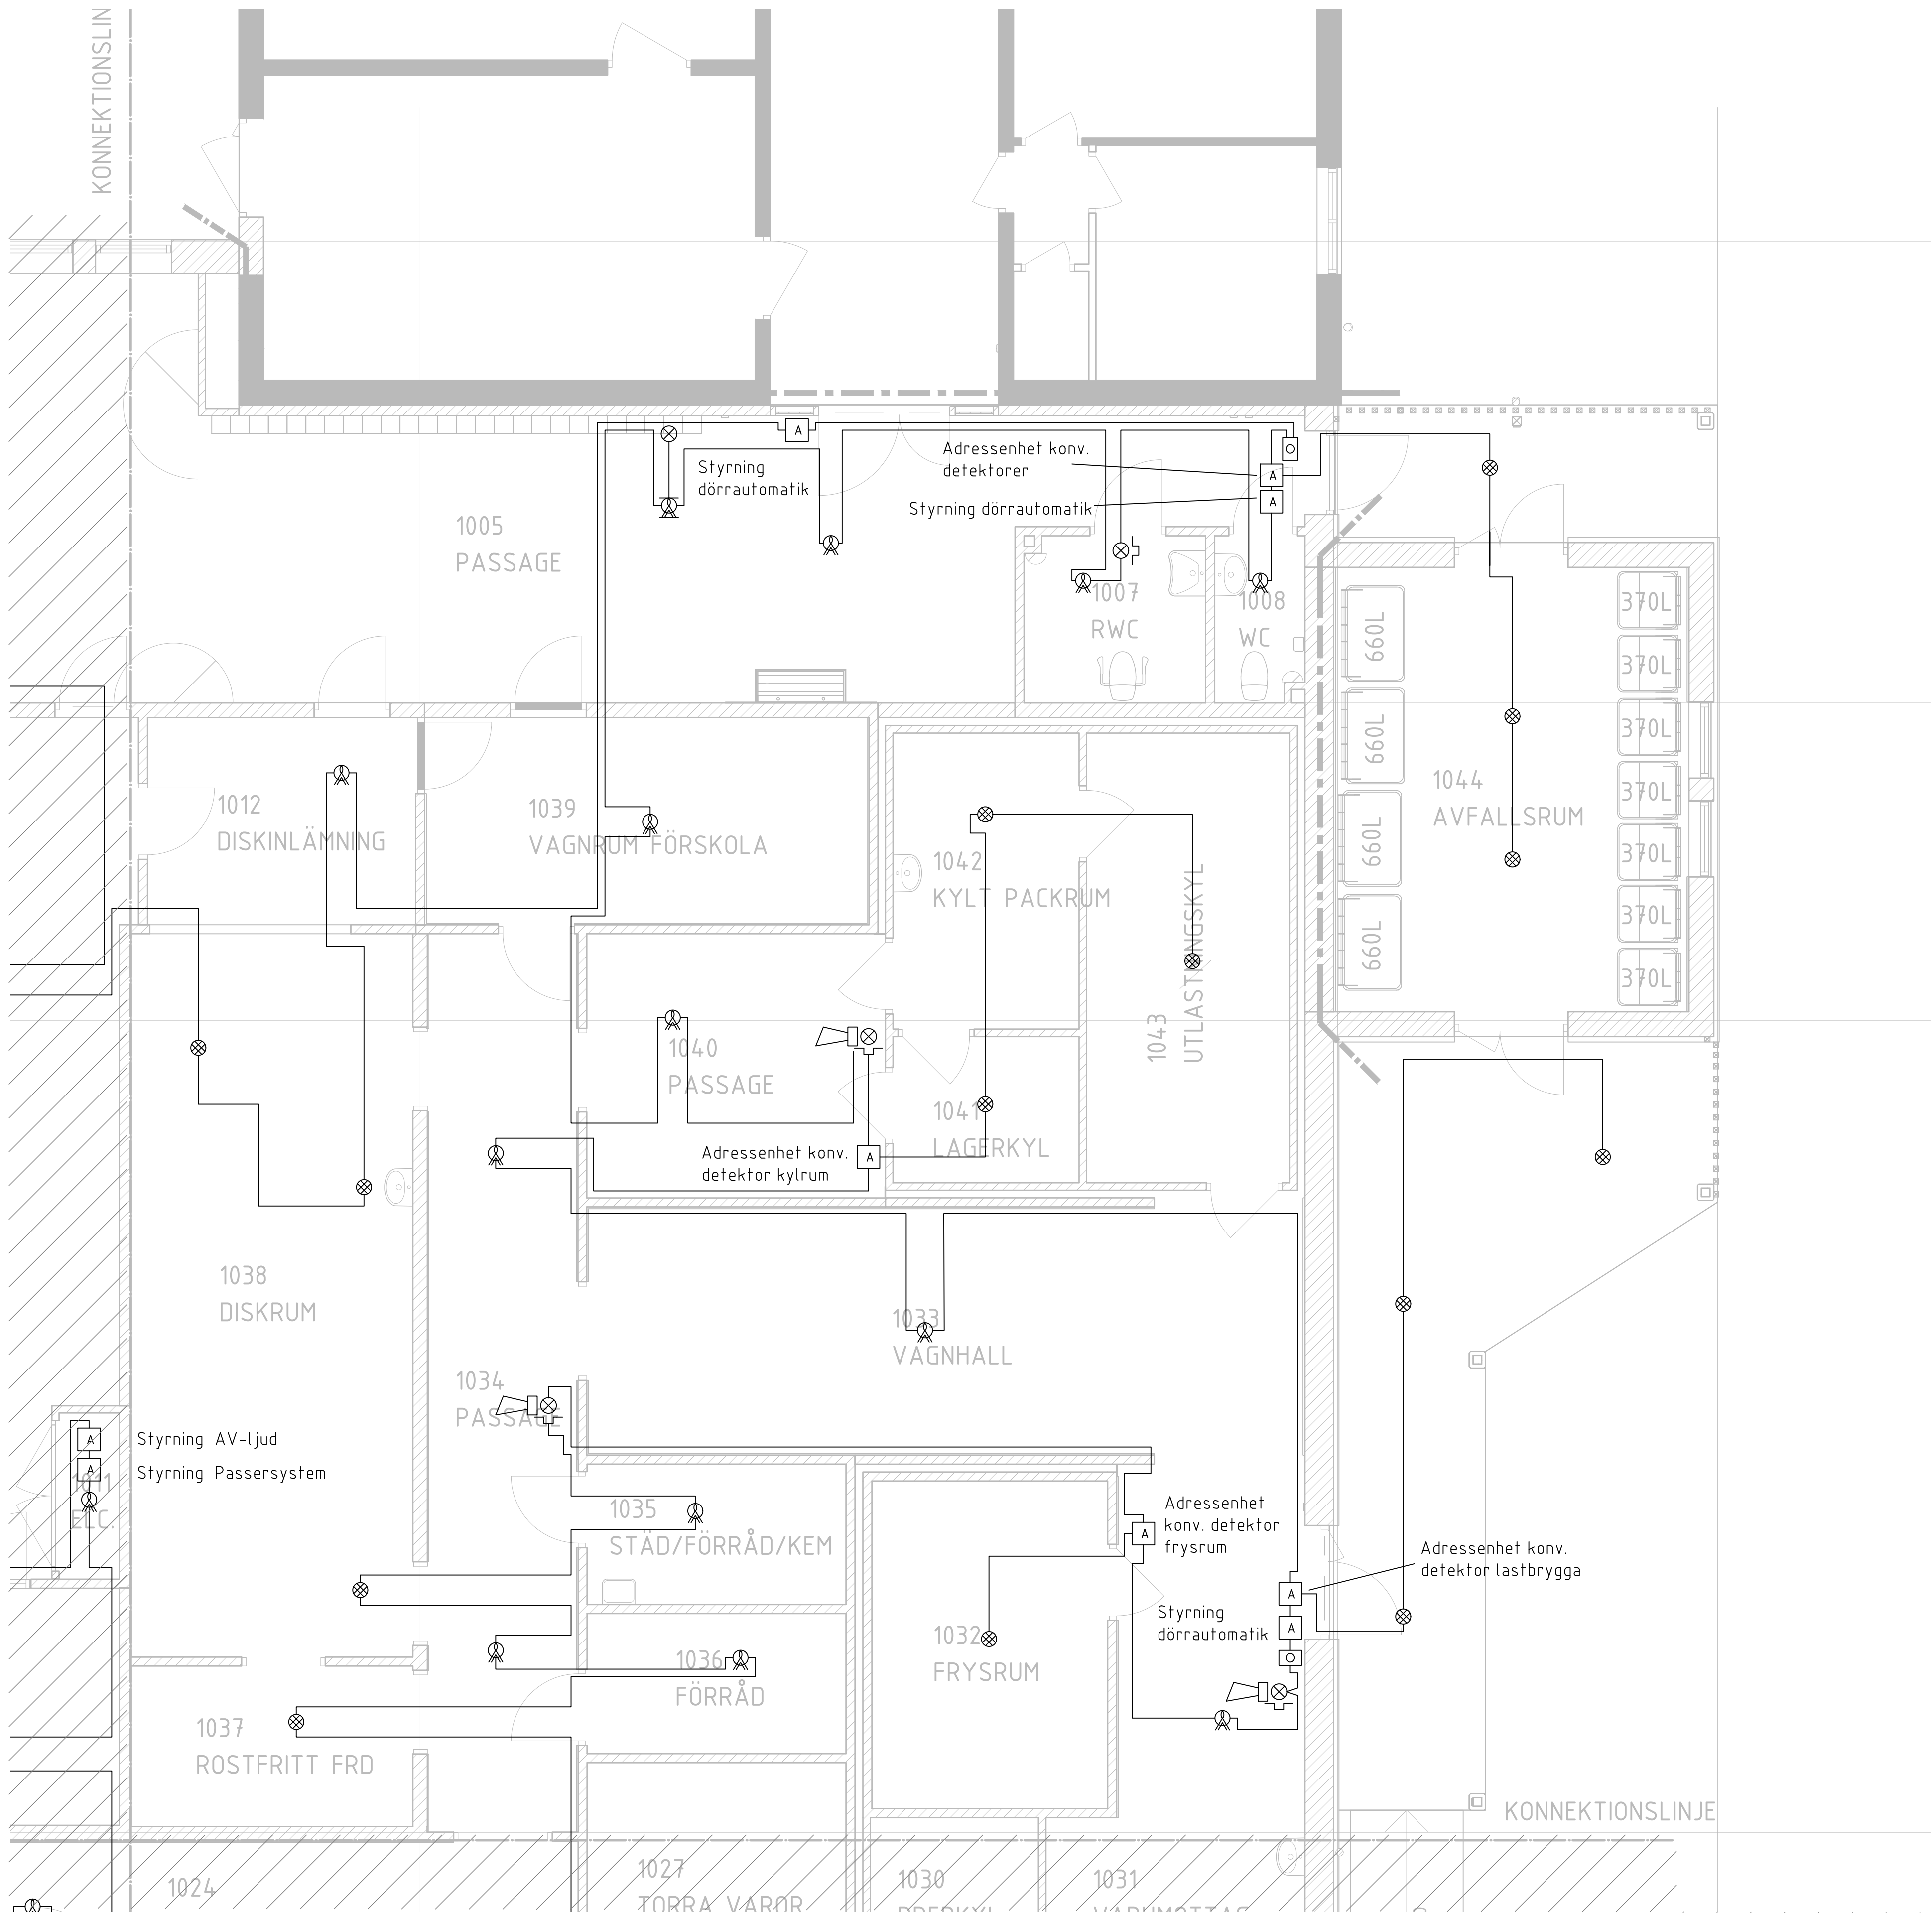


ANVISNINGAR

DETEKTORER MONTERAS DIKT TAK/UNDERTAK DÄR EJ
ANNAT ANGES.
EXAKT PLACERING DETEKTORER ANPASSAS EFTER:
MIN 0,5m - FRÄNLUFTSDON, VÄGG, ARMATUR ELLER ANNAT
SOM INTE ÄR INFÄLLT I TAK/UNDERTAK.
ADRESSEHETER MONTERAS OVAN UNDERTAK I EGEN
KAPSLING.
INDIKERING "DOLD DETEKTOR" MONTERAS PÅ VÄGG I TAK-
VINKEL ALT. I UNDERTAKS RAMVERK I ANSLUTNING TILL
DETEKTOR.
SAMTLIGA LARMÖN MONTERAS PÅ VÄGG 100mm NEDAN
UNDERTAK DÄR EJ ANNAT ANGES.
KABELSTRÅK GENOM VÄGG BRANDTÄTAS MED SAMMA
BRANDKLÄSSNING SOM VÄGG.

KABEL DÄR EJ ANNAT ANGES: ELQYB 2X1 RÖD

SYMBOLFÖRKLARINGAR

- CA BRANDLARMSCENTRAL / BFT
- LS LARMSÄNDARE
- RÖKDETEKTOR ADRESSERBAR
- DOLD RÖKDETEKTOR ADRESSERBAR
- HISSBAR DETEKTOR
- INDIKERING DOLD DETEKTOR
- RÖKDETEKTOR MED MÄTKAMMARE
MONTERAS I VENTILATIONSAGGREGAT
- KAPSLAD VÄRMEDETEKTOR ADRESSERBAR
- KAPSLAD VÄRMEDETEKTOR KONVENTIONELL
- A ADRESSEHET
- BIBRANDSKÅP, MONTERAS +1200mm ÖG
- KOMBILARMÖN BLIXT/SIREN,
MONTERAS +2300 ÖG
- ROTORLJUS RÖD, IP65, MONTERAS +3500mm ÖM
- NS NYCKELSKÅP, MONTERAS I VÄGG +1800mm ÖM

SEKTION			
ORIENTERINGSFIGUR			
STATUS			
FÖRFRÅGNINGSUNDERLAG			
HANDLING			
BYGGHANDLING			
DATUM		2024-12-20	
TIOGÅRD AV		T. BERGSTRÖM	
ÄNDRING		PM	
BESTÄLLARE		-	
ROBERTSFORS KOMMUN			
PROJEKTNAMN			
CENTRALEKÖK			
ORFÄRE			
ROBERTSFORS KOMMUN			
PROJEKTNUMMER		ADRESS	
YTTRE RINGVÄGEN 4		FORDONET 1	
DISCIPLIN		FÖRETAG	
E		NORCONSULT SVERIGE AB	
UPPDRAGSNUMMER		SKAPAD AV	
1088371		OPN	
TELEFON		KONTAKTPERSON	
010 141 80 00		TOMAS BERGSTRÖM	
BYGGNADSVÄRDE		PRIS/STYCKE	
+45,54 (FG)		-	
VÄNINGSPLAN		VÄNINGSDEL	
1		DEL 4.2, 5.2	
SYSTEM			
BRAND- & UTRYMNINGSLARM			
SPECIFIKATION			
PLAN 1			
TITEL		SKALA	
PLANER		1:50	
DOCUMENTNUMMER		ÄNDRING	
E-64CBB-1-512		-	