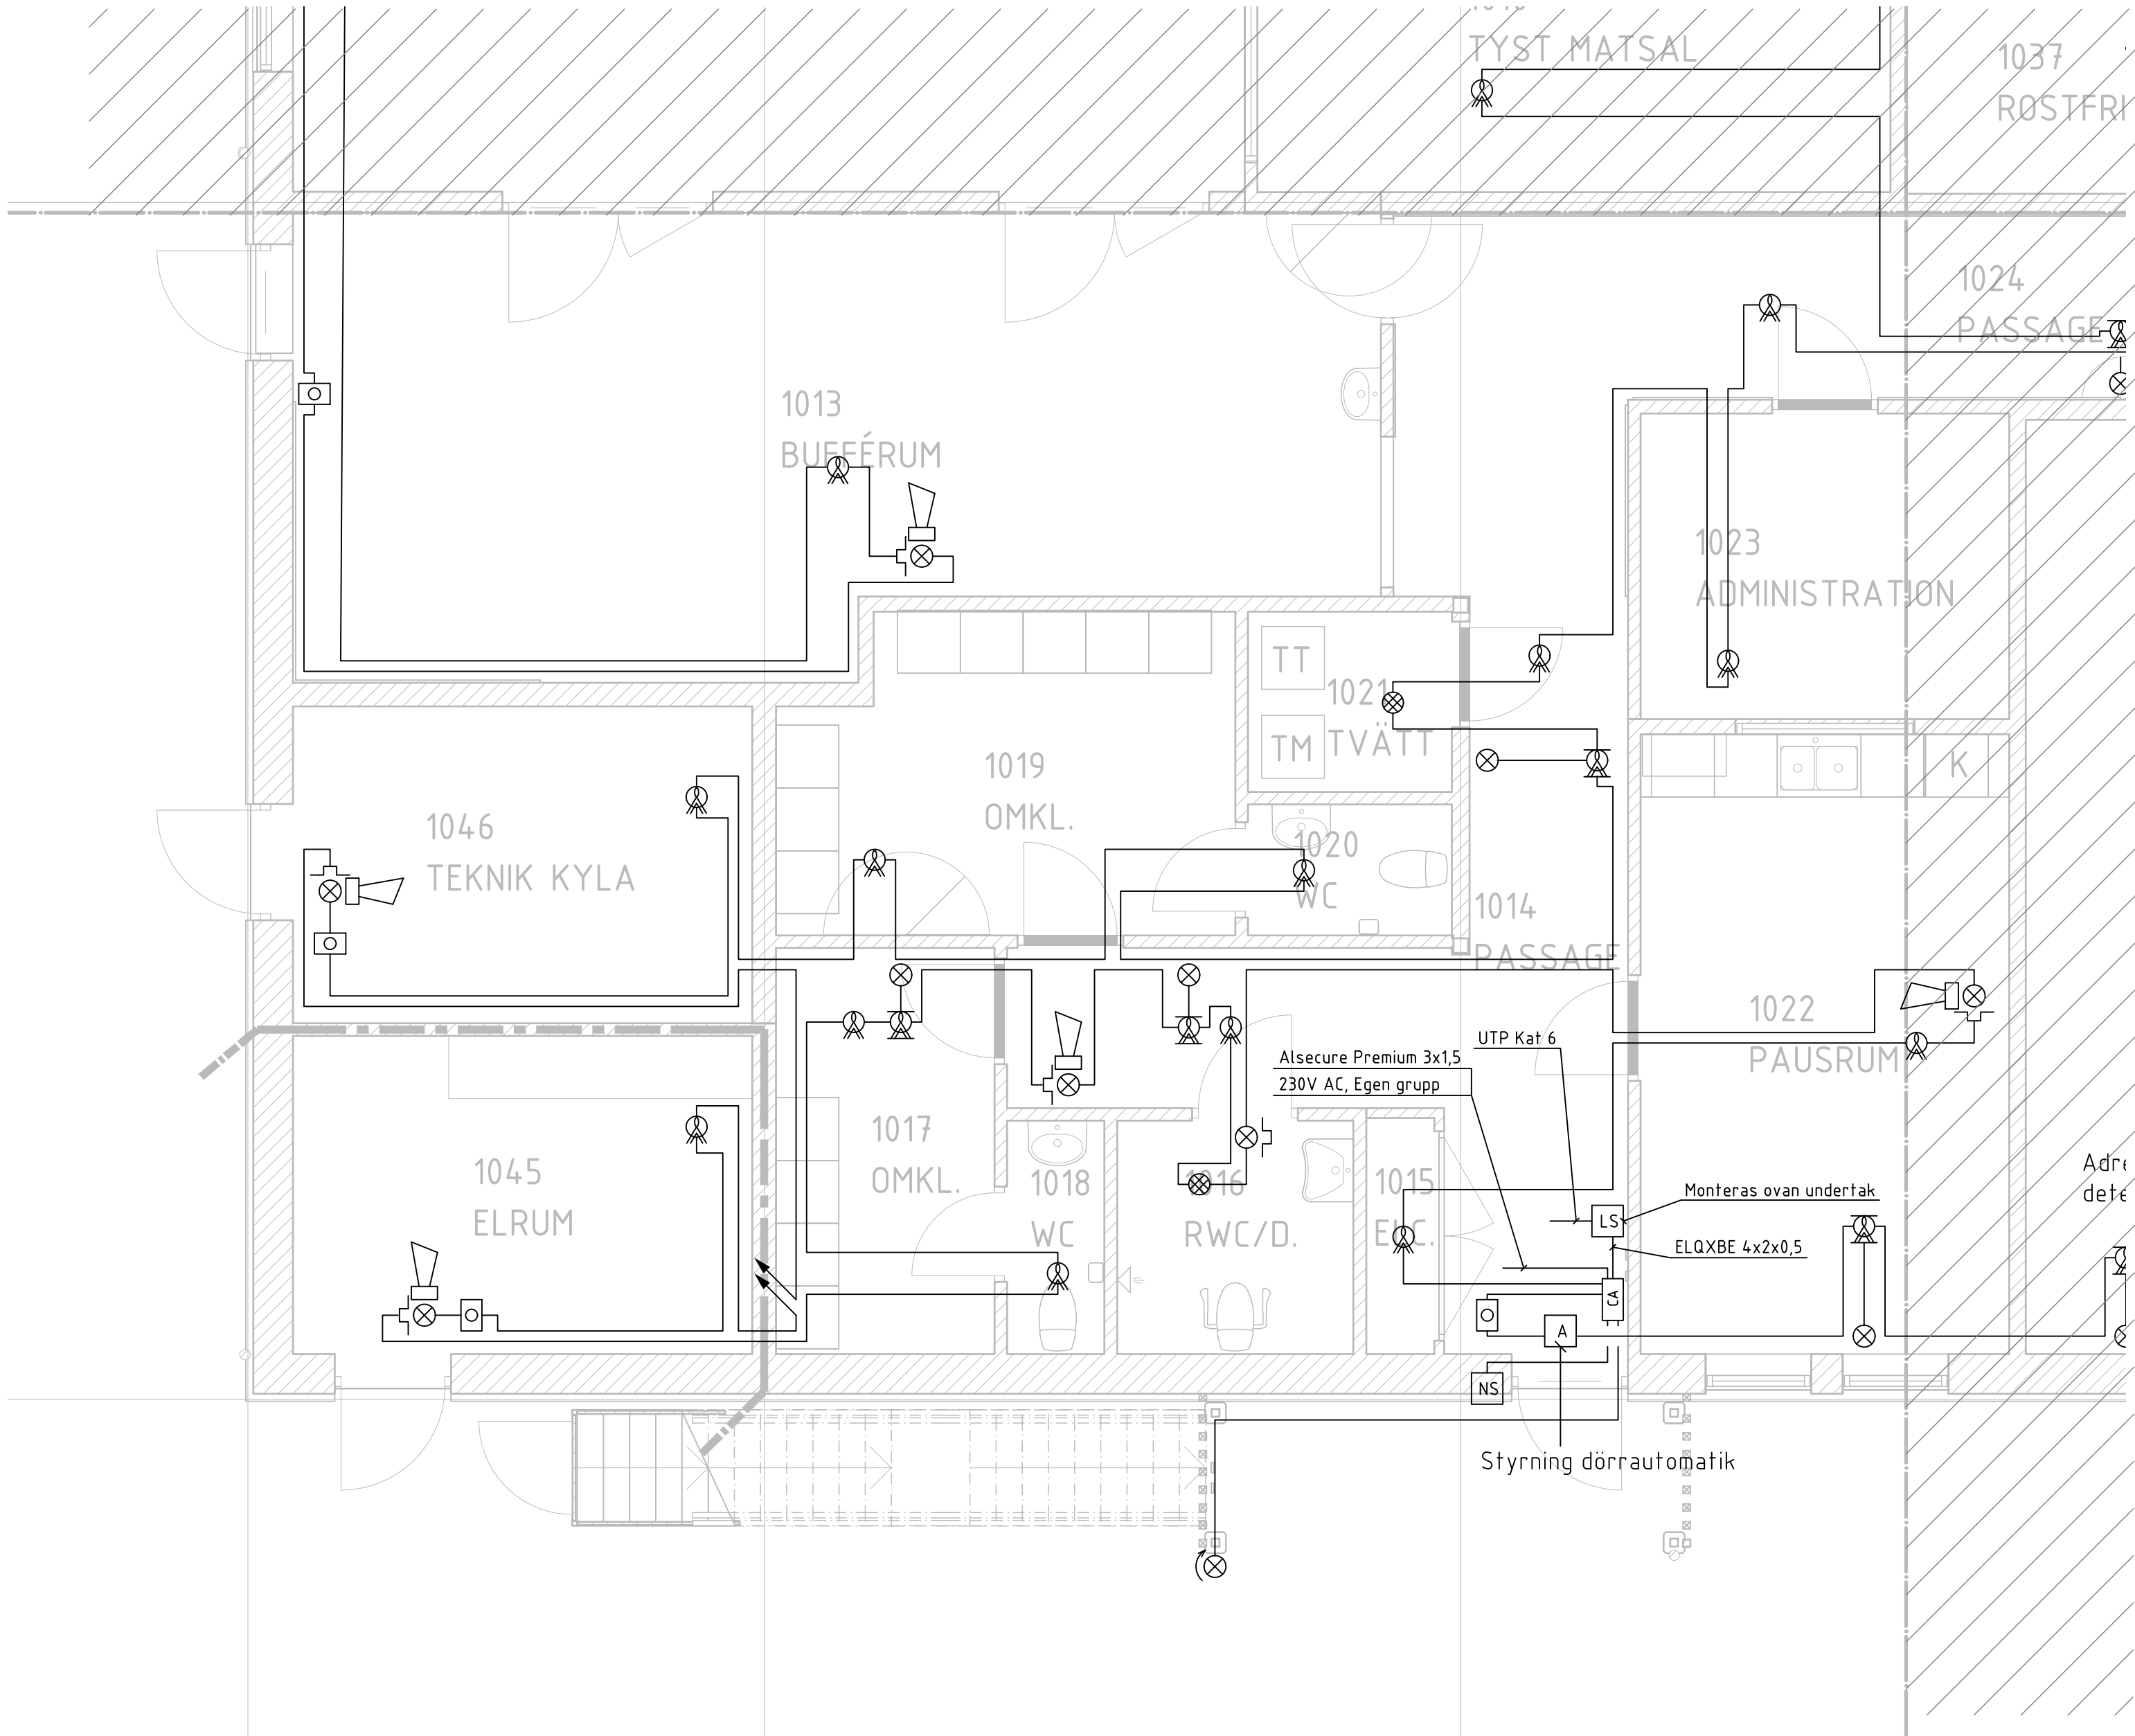



ANVISNINGAR

DETEKTORER MONTERAS DIKT TAK/UNDERTAK DÄR EJ ANNAT ANGES.
EXAKT PLACERING DETEKTORER ANPASSAS EFTER:
MIN 1m - TILLUFTSDÖN
MIN 0,5m - FRÄNLUFTSDÖN, VÄGG, ARMATUR ELLER ANNAT
SOM INTE ÄR INFÄLLT I TAK/UNDERTAK.
ADRESSENHETER MONTERAS OVAN UNDERTAK I EGEN KAPSLING.
INDIKERING "DOLD DETEKTOR" MONTERAS PÅ VÄGG I TAK-VINKEL ALT. I UNDERTAKS RAMVERK I ANSLUTNING TILL DETEKTOR.
SAMTLIGA LARMÖN MONTERAS PÅ VÄGG 100mm NEDAN UNDERTAK DÄR EJ ANNAT ANGES.
KABELSTRÅK GENOM VÄGG BRANDTÄTAS MED SAMMA BRANDKLASSNING SOM VÄGG.

KABEL DÄR EJ ANNAT ANGES: ELQYB 2X1 RÖD

SYMBOLFÖRKLARINGAR

- CA BRANDLARMSCENTRAL / BFT
- LS LARMSÄNDARE
- RÖKDETEKTOR ADRESSERBAR
- DOLD RÖKDETEKTOR ADRESSERBAR
- HISSBAR DETEKTOR
- INDIKERING DOLD DETEKTOR
- RÖKDETEKTOR MED MÅTKAMMARE MONTERAS I VENTILATIONSAGGREGAT
- KAPSLAD VÄRMEDETEKTOR ADRESSERBAR
- KAPSLAD VÄRMEDETEKTOR KONVENTIONELL
- A ADRESSENHET
- BIBRANDSKÄP, MONTERAS +1200mm ÖG
- KOMBILARMÖN BLIXT/SIREN, MONTERAS +2300 ÖG
- ROTORLJUS RÖD, IP65, MONTERAS +3500mm ÖM
- NS NYCKELSKÅP, MONTERAS I VÄGG +1800mm ÖM

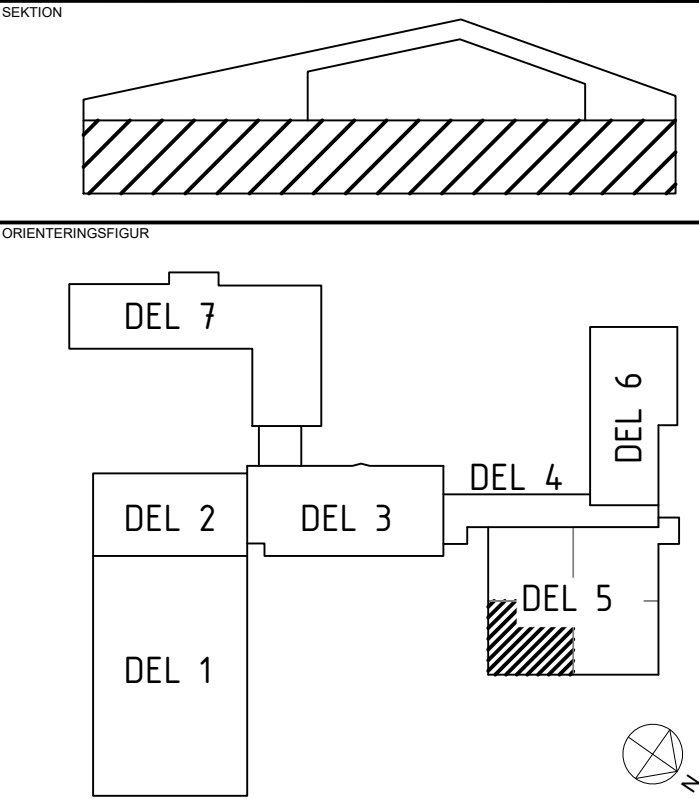

STATUS		
FÖRFRÅGNINGSUNDERLAG		
HANDLING		
BYGGHANDLING		
DATUM	ÖVERSKAD AV	ÄNDRINGS PM
2024-12-20	T. BERGSTRÖM	-
BESTÄLLARE		



PROJEKTNAMN		
CENTRALKÖK		
OMRÅDE		
ROBERTSFORS KOMMUN		
PROJEKTNUMMER	ADRESS	
	YTTRE RINGVÄGEN 4	
DÄRRETNUMMER	FASTIGHET	
	FORDONET 1	
DISCIPLIN	FÖRETAG	
E	NORCONSULT SVERIGE AB	
UPPDRAGSNUMMER	SKAPAD AV	
1088371	OPN	
TELEFON	KONTAKTPERSON	
010 141 80 00	TOMAS BERGSTRÖM	
BYGGNADSVÄRK	FÖLJESKIVOR (PM)	
	+45,54 (FG)	
VÄNINGSPLAN	VÄNINGSDEL	DELOMRÅDE
1		DEL 5.3
SYSTEM		
BRAND- & UTRYMNINGSLARM		
SPECIFIKATION		
PLAN 1		
TEKNIKSPECIFIKATION	SKALA	FORMAT
PLANER	1:50	A1
DOCUMENTNUMMER	ÄNDRING	
E-64CBB-1-513	-	