
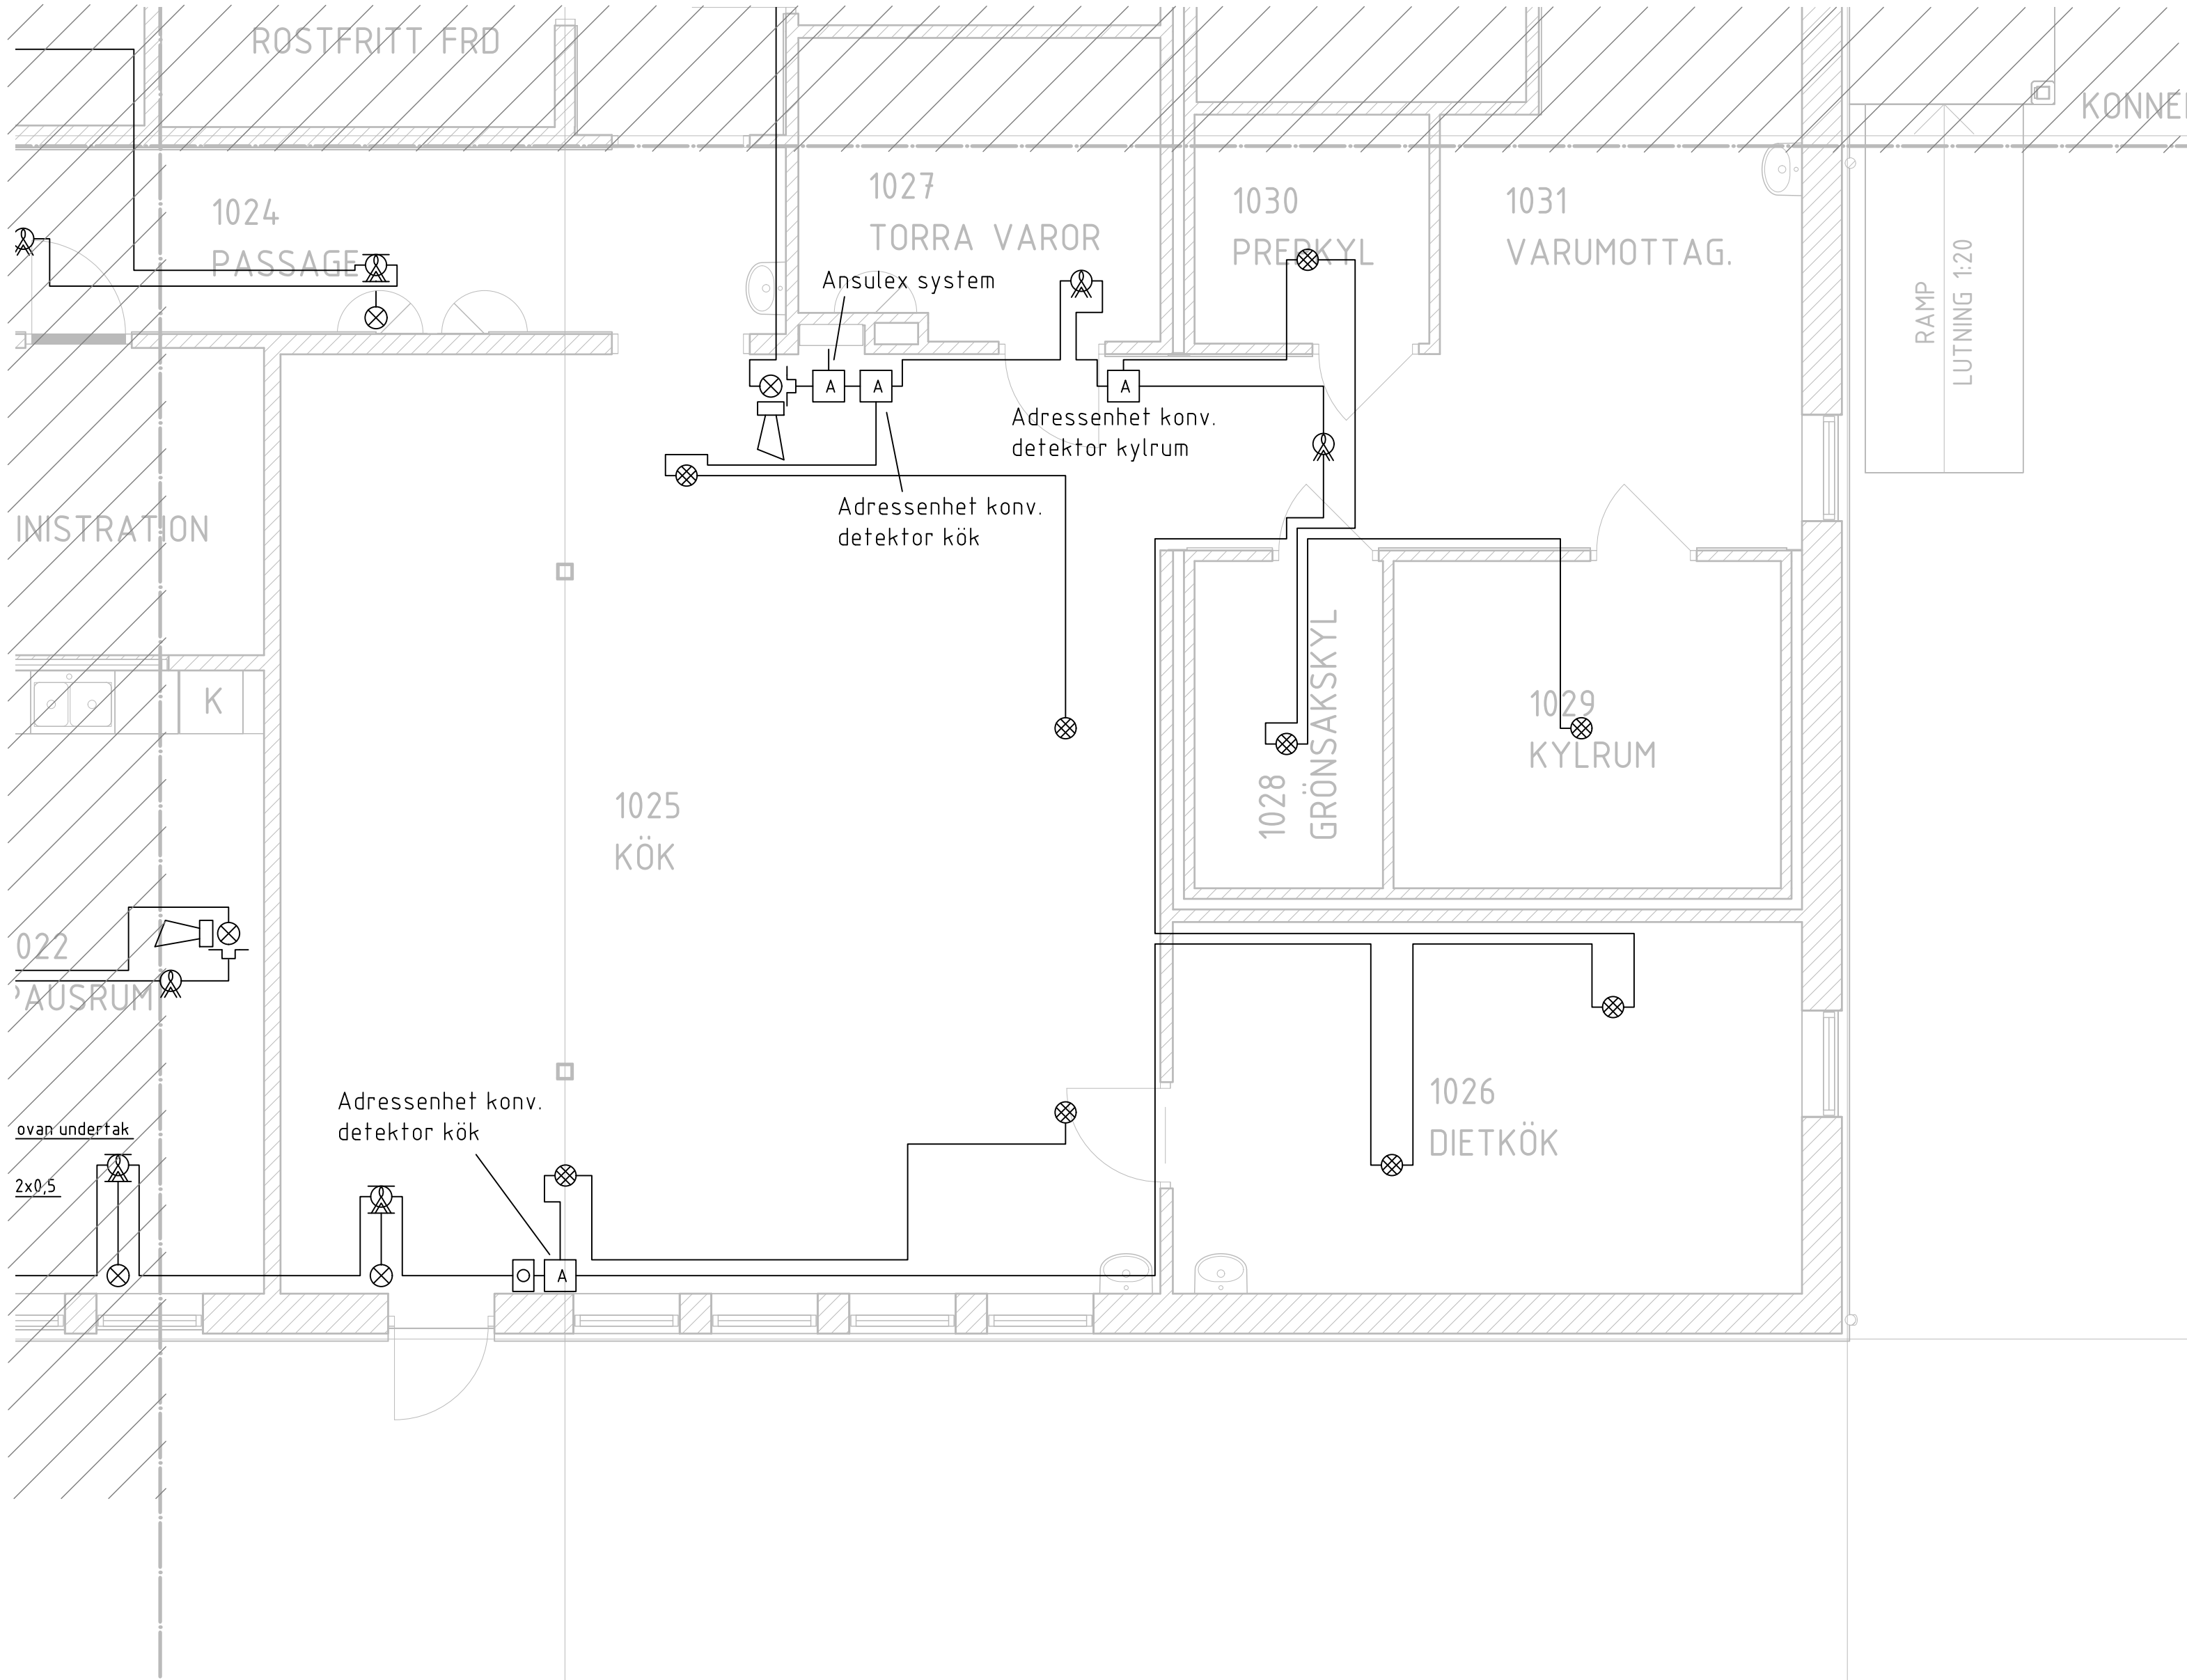


ANVISNINGAR
DETEKTORER MONTERAS DIKT TAK/UNDERTAK DÄR EJ ANNAT ANGES.
EXAKT PLACERING DETEKTORER ANPASSAS EFTER:
MIN 1m - TILLUFTSDON
MIN 0,5m - FRÄNLUFTSDON, VÄGG, ARMATUR ELLER ANNAT
SOM INTE ÄR INFÄLLT I TAK/UNDERTAK.
ADRESSENHETER MONTERAS OVAN UNDERTAK I EGEN KAPSLING.
INDIKERING "DOLD DETEKTOR" MONTERAS PÅ VÄGG I TAK-VINKEL. ALT. I UNDERTAKS RAMVERK I ANSLUTNING TILL DETEKTOR.
SAMTLIGA LARMÖN MONTERAS PÅ VÄGG 100mm NEDAN UNDERTAK DÄR EJ ANNAT ANGES.
KABELSTRÅK GENOM VÄGG BRANDTÄTAS MED SAMMA BRANDKLÄSSNING SOM VÄGG.
KABEL DÄR EJ ANNAT ANGES: ELQYB 2X1 RÖD

- SYMBOLFÖRKLARINGAR**
- CA BRANDALARMSCENTRAL / BFT
 - LS LARMSÄNDARE
 - RÖKDETEKTOR ADRESSERBAR
 - DOLD RÖKDETEKTOR ADRESSERBAR
 - HISSBAR DETEKTOR
 - INDIKERING DOLD DETEKTOR
 - RÖKDETEKTOR MED MÄTKAMMARE. MONTERAS I VENTILATIONSAGGREGAT
 - KAPSLAD VÄRMEDETEKTOR ADRESSERBAR
 - KAPSLAD VÄRMEDETEKTOR KONVENTIONELL
 - A ADRESSENHET
 - BIBRANDSKÄP, MONTERAS +1200mm ÖG
 - KOMBILARMÖN BLIXT/SIREN, MONTERAS +2300 ÖG
 - ROTORLJUS RÖD, IP65. MONTERAS +3500mm ÖM
 - NS NYCKELSKÄP, MONTERAS I VÄGG +1800mm ÖM

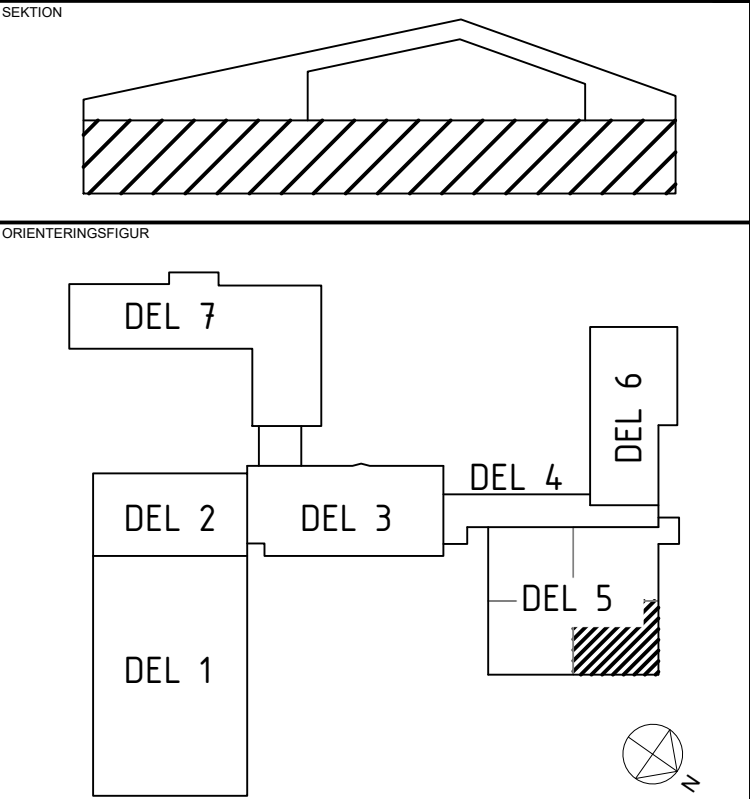

STATUS
FÖRFRÅGNINGSUNDERLAG

HANDLING
BYGGHANDLING

DATUM
2024-12-20

ÖVERSKAD AV
T. BERGSTRÖM

ÄNDRINGS PM
-

BESTÄLLARE
 **ROBERTSFORS KOMMUN**

PROJEKTNAMN
CENTRALEKÖK

OMRÅDE
ROBERTSFORS KOMMUN

PROJEKTNUMMER
ADRESS
YTTRE RINGVÄGEN 4

DÄRRETNAMN
FASTIGHET
FORDONET 1

DISCIPLIN
FÖRETAG
NORCONSULT SVERIGE AB

UPPDRAGSNUMMER
SKAPAD AV
1088371 OPN

TELEFON
KONTAKTPERSON
010 141 80 00 TOMAS BERGSTRÖM

BYGGNADSVÄRK
FÖLJESKEDVÄRK
+45,54 (FG)

VÄNINGSPLAN
VÄNINGSDEL
DELOMRÅDE
1 DEL 5.4

SYSTEM
BRAND- & UTRYMNINGSLARM

SPECIFIKATION
PLAN 1

BYGGNADSVÄRK
SKALA
FORMAT
PLANER 1:50 A1

DOCUMENTNUMMER
ÄNDRING
E-64CBB-1-514 -