

ANVISNINGAR

DETEKTORER MONTERAS DIKT TAK/UNDERTAK DÄR EJ ANNAT ANGES.
EXAKT PLACERING DETEKTORER ANPASSAS EFTER:
MIN 1m - TILLUFTSDÖN
MIN 0,5m - FRÅNLUFTSDÖN, VÄGG, ARMATUR ELLER ANNAT
SOM INTE ÄR INFÄLLT I TAK/UNDERTAK.
ADRESSENHETER MONTERAS OVAN UNDERTAK I EGEN KAPSLING.
INDIKERING "DOLD DETEKTOR" MONTERAS PÅ VÄGG I TAK-VINKEL, ÄLT. I UNDERTAKS RAMVERK I ANSLUTNING TILL DETEKTOR.
SAMTLIGA LARMÖN MONTERAS PÅ VÄGG 100mm NEDAN UNDERTAK DÄR EJ ANNAT ANGES.
KABELSTRÅK GENOM VÄGG BRANDTÄTAS MED SAMMA BRANDKLÄSSNING SOM VÄGG.

KABEL DÄR EJ ANNAT ANGES: ELÖYB 2X1 RÖD

SYMBOLFÖRKLARINGAR



- EA

BRANDLARMSCENTRAL / BFT
- LS

LARMSÄNDARE
- RÖKDETEKTOR ADRESSERBAR
- DOLD RÖKDETEKTOR ADRESSERBAR
- HISSBAR DETEKTOR
- INDIKERING DOLD DETEKTOR
- RÖKDETEKTOR MED MÅTKAMMARE.
MONTERAS I VENTILATIONSAGGREGAT
- KAPSLAD VÄRMEDETEKTOR ADRESSERBAR
- KAPSLAD VÄRMEDETEKTOR KONVENTIONELL
- A

ADRESSENHET
- BIBRANDSKÅP, MONTERAS +1200mm ÖG
- KOMBILARMÖN BLIXT/SIREN,
MONTERAS +2300 ÖG
- ROTORLJUS RÖD, IP65, MONTERAS +3500mm ÖM
- NS

NYCKELSKÅP, MONTERAS I VÄGG +1800mm ÖM

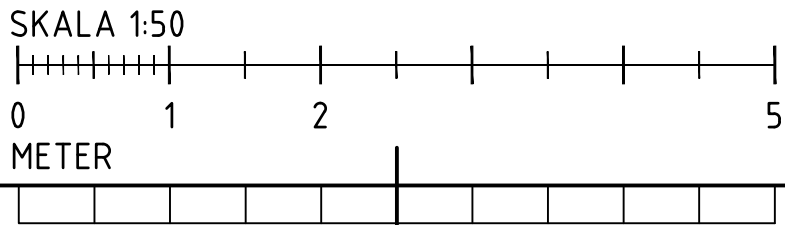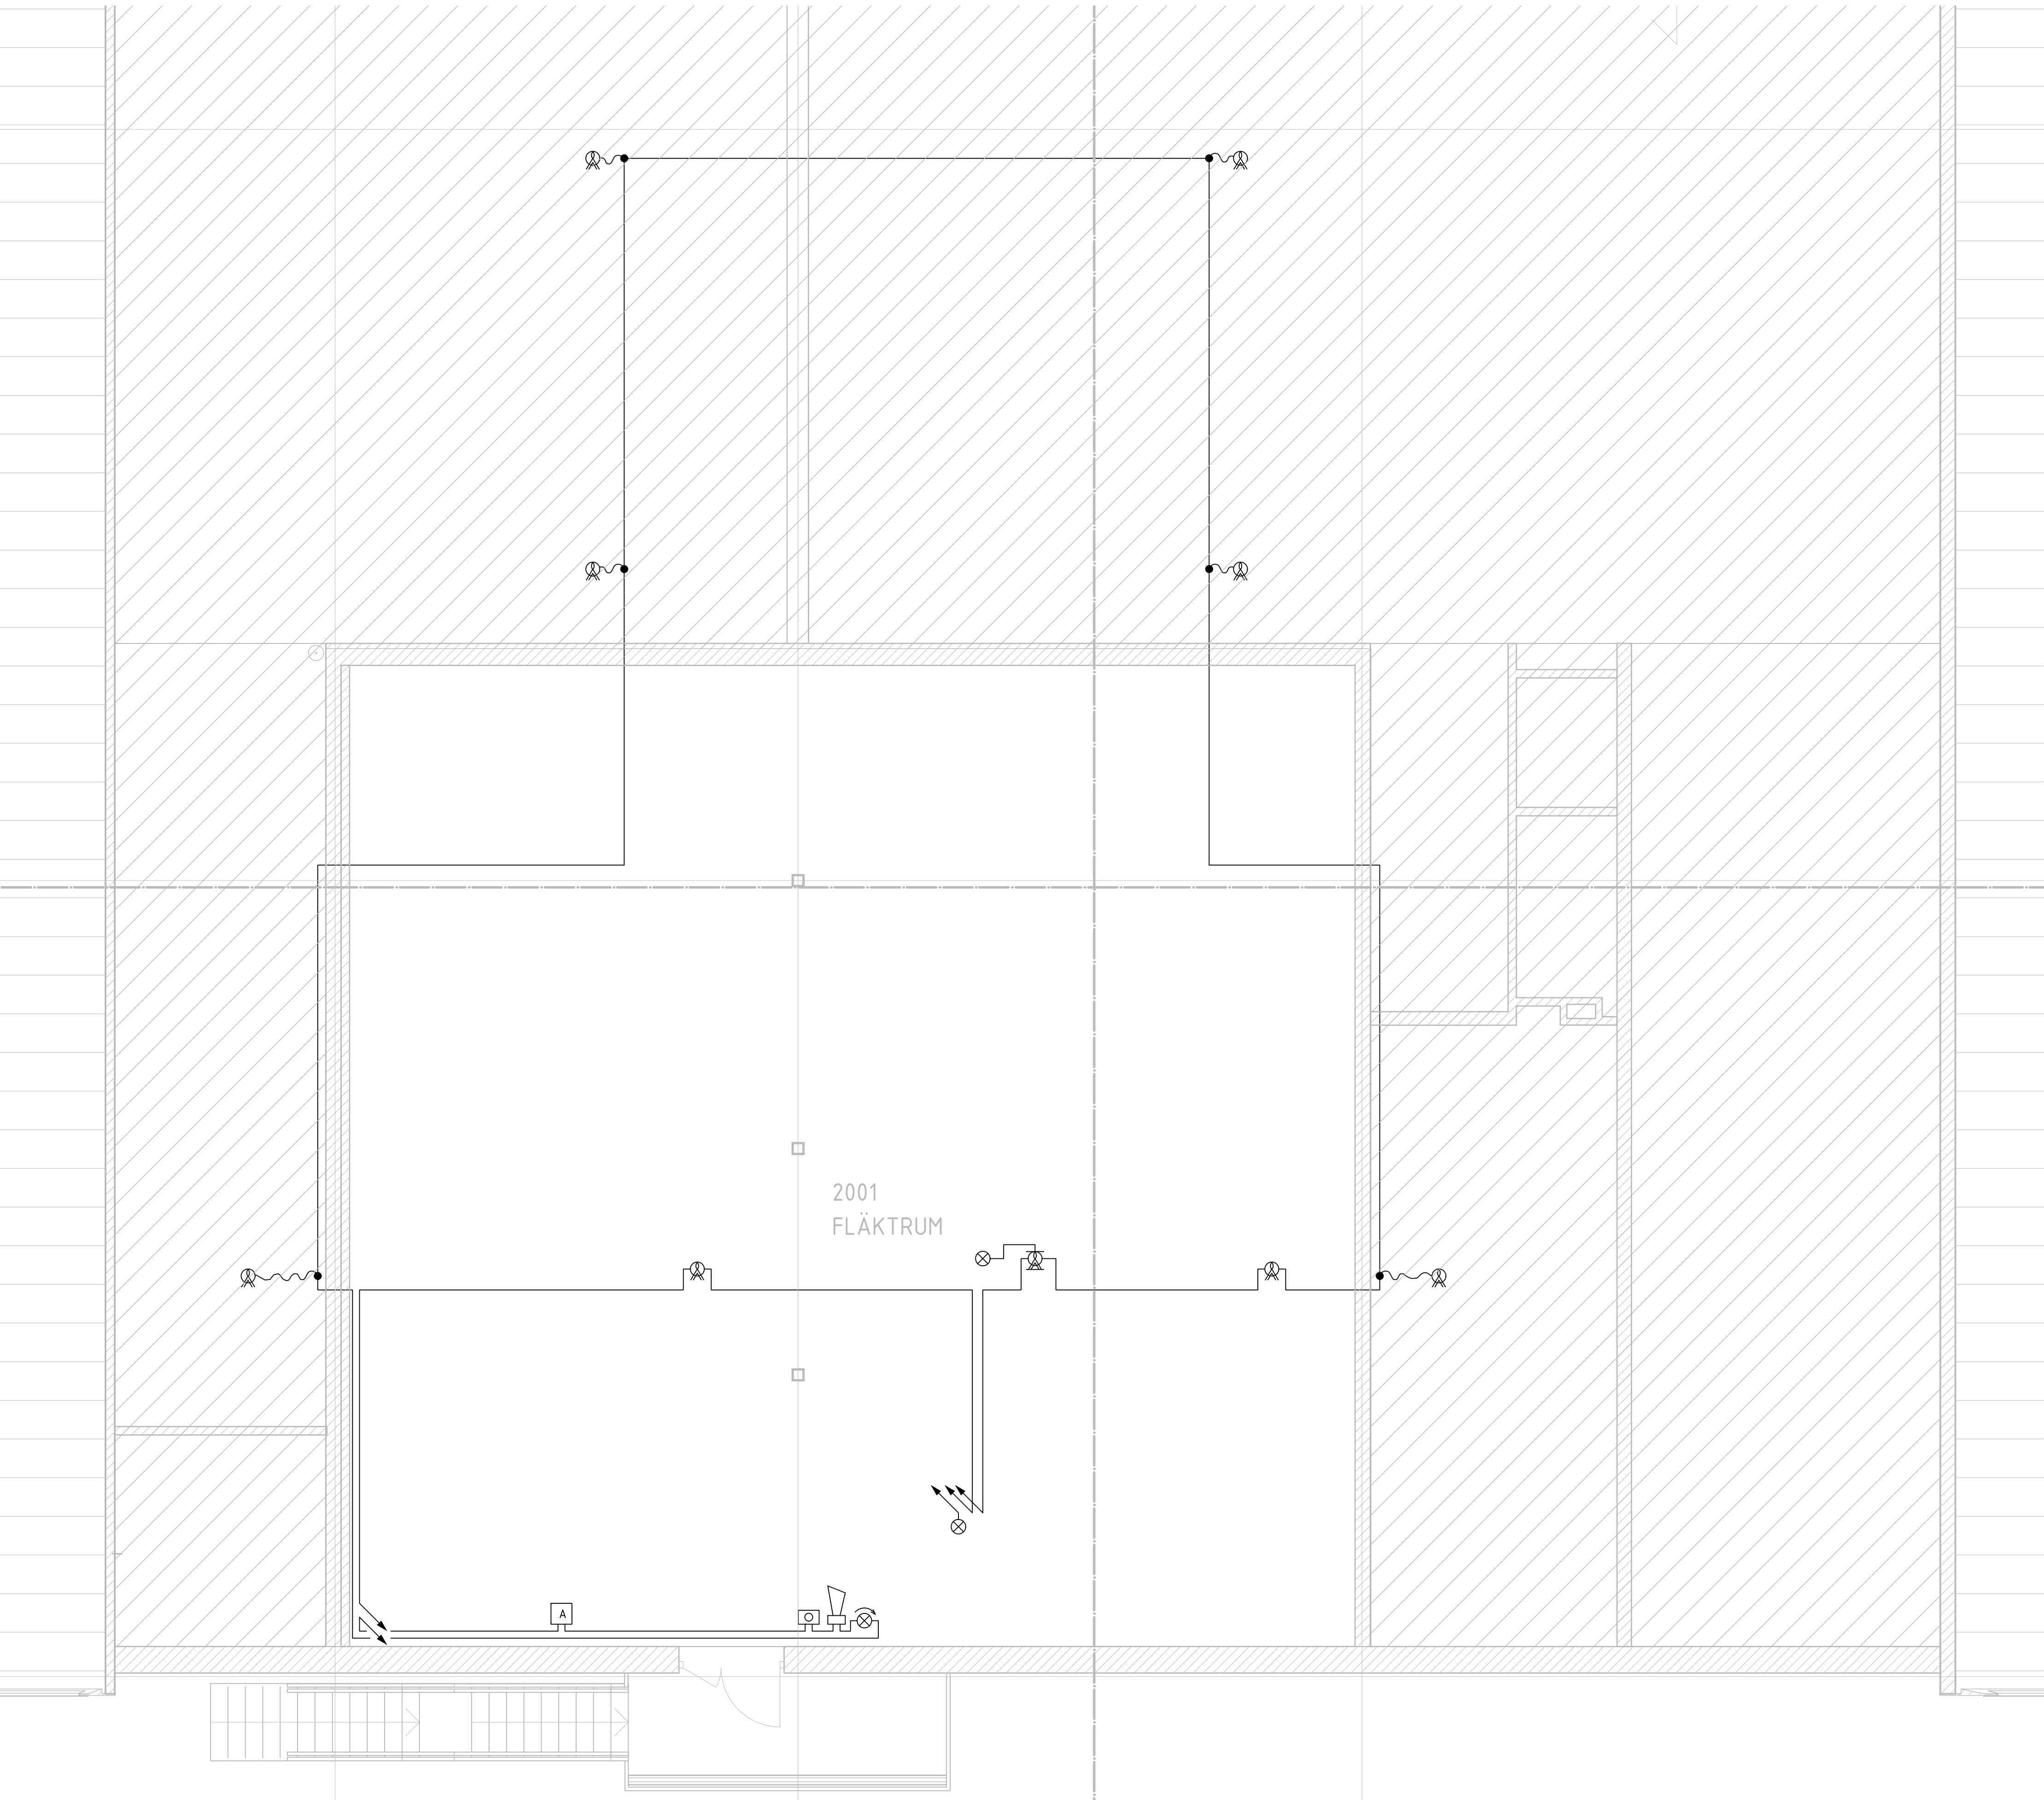

SEKTION

ORIENTERINGSFIGUR

STATUS

HANDLING

DATUM

COORDINAT

ÄNDRINGS PM

BESTÄLLARE

PROJEKTNAMN

OMRÅDE

PROJEKTNUMMER

ADRESS

DIREKTOR

DISCIPLIN

UPPDRAGSNUMMER

TELEFON

BYGGNADSVÄRK

VÄNINGSPLAN

VÄNINGSDEL

DELÖMRÅDE

SYSTEM

SPECIFIKATION

FORMAT

ÄNDRING

ROBERTSFORS
KOMMUN

FÖRFRÅGNINGSUNDERLAG

BYGGHANDLING

2024-12-20

T. BERGSTRÖM

-

CENTRALEKÖK

ROBERTSFORS KOMMUN

YTTRE RINGVÄGEN 4

FORDONET 1

NORCONSULT SVERIGE AB

OPN

TOMAS BERGSTRÖM

+45,54 (FG)

DEL 5

BRAND- & UTRYMNINGSLARM

PLAN 2

SKALA 1:50

FORMAT A1

E-64CBB-1-521

-