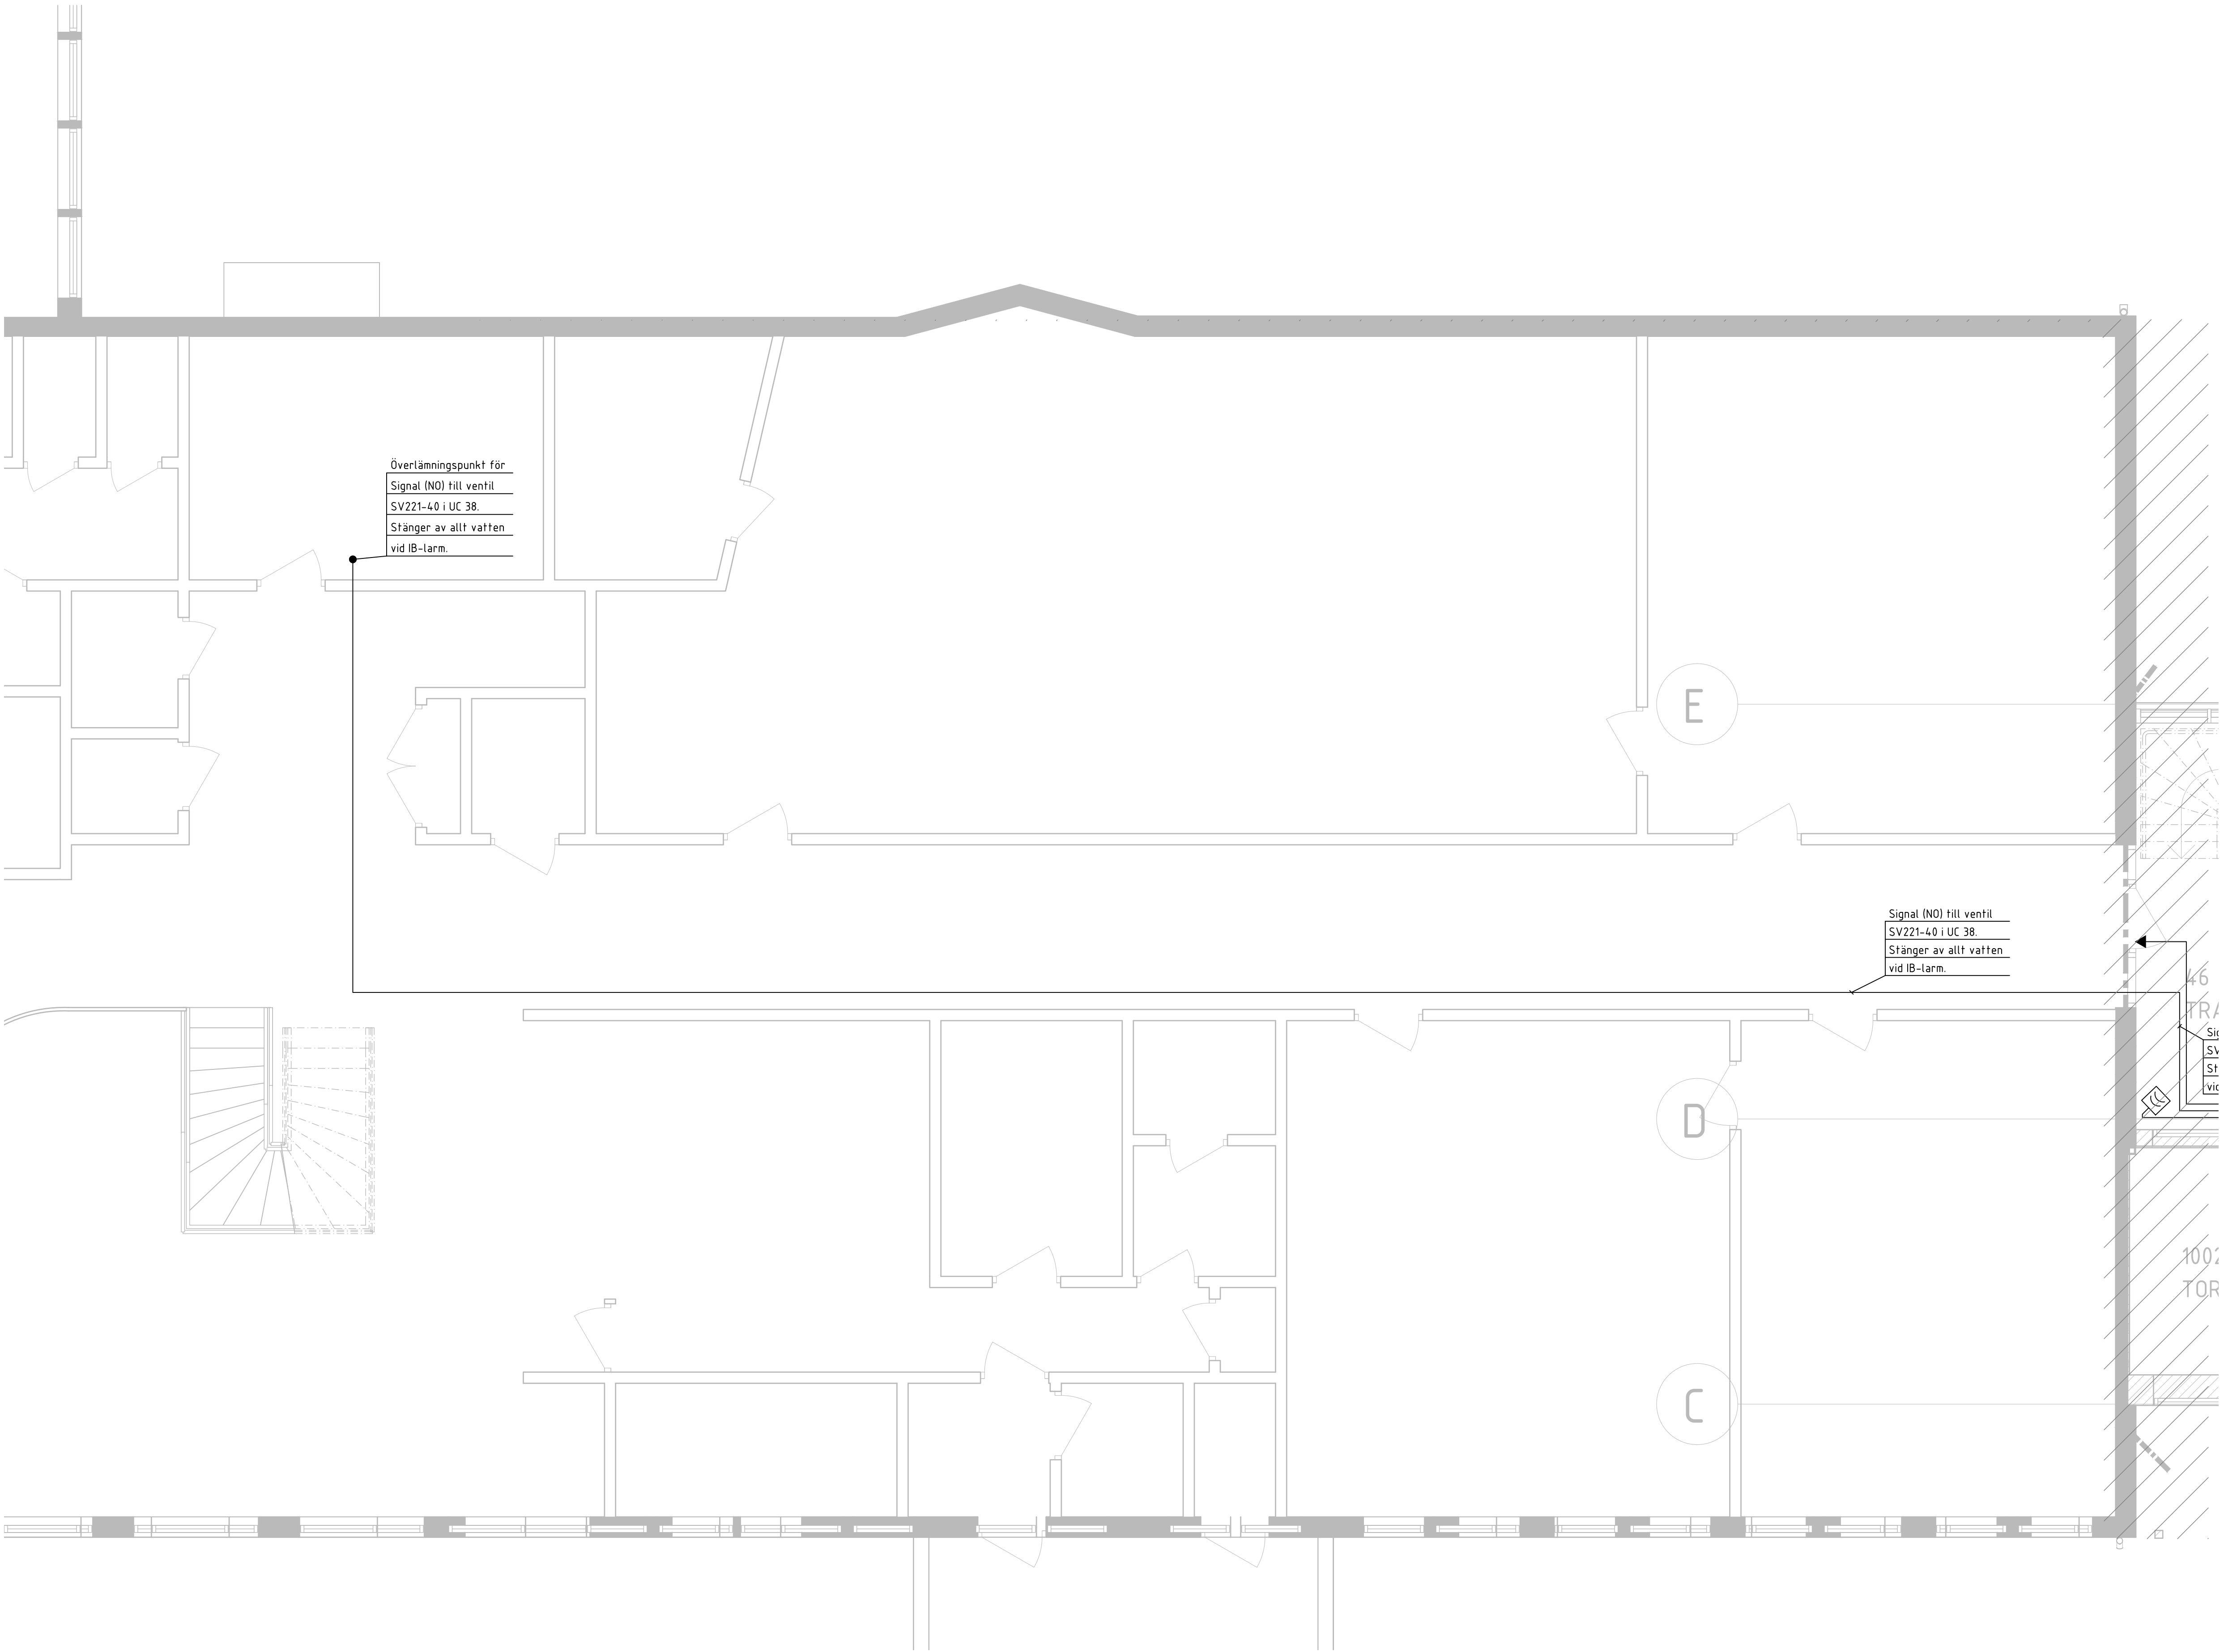


ANVISNINGAR

DOSOR OCH UTTAG SOM PLACERAS PÅ LEDNINGSSTEGE
MONTERAS PÅ STEGPLÅT.
RÖRELSEDETEKTORER OCH LARMODN MONTERAS 50mm
NEDAN TAKVINKEL DÄR EJ ANNAT ANGES.
GLASKROSSDETEKTOR MONTERAS DKT UNDER TAK RIKTADE
MOT FÖNSTERPARTI.

KABEL, DÄR EJ ANNAT ANGES: ELQXB 2X2X0,5


SYMBOLFÖRKLARINGAR

- UC-50 CENTRALAPPARAT INTEGRERAT LARM-/PASSERSYSTEM
- NÄTDEL INKL: BATTERIBACKUP
- M MÄNÖVERPANEL ITEGRERAT SYSTEM, MONTERAS +1600mm ÖG
- MAGNETKONTAKT
- IR DETEKTOR
- IR DETEKTOR 360°
- AKUSTISK GLASKROSSDETEKTOR
- INDIKERINGSLAMPA, MONTERAS OVAN DÖRRKARM
- DÖRR-/LARMODN, MONTERAS OVAN UNDER TAK
- KL KORTLÄSARE, MONTERAS +1200mm ÖM
- ÖPPNAKNAPP, MONTERAS +1200mm ÖG
- KÄRMÖVERFÖRING
- ELSLUTBLECK

-60/-1- FLQ0BR 1X2 + 2X2X0,22

-28/-1- PTS-HF 2X2X0,6

- DETEKTOR FÖRBIKOPPLAS VIA KORTLÄSARE "LASTBRYGGA" TILLS TILLKOPPLING SKER ELLER EFTER MAX 30 MIN
- ENHET TERMINERAS. SE INSTALLATIONS MANUAL AKTUELL ENHET.

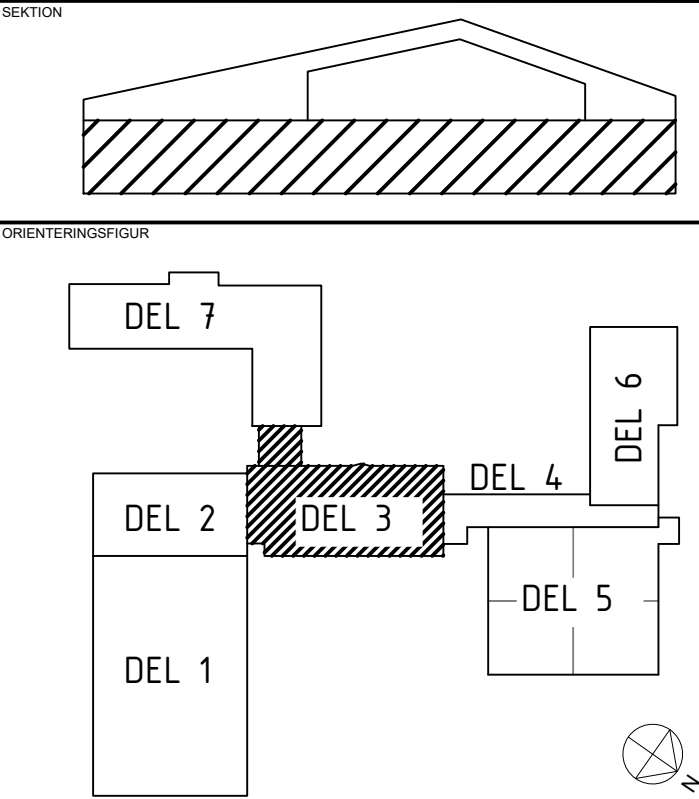

STATUS		
FÖRFRÅGNINGSUNDERLAG		
HANDLING		
BYGGHANDLING		
DATUM	2024-12-20	COORDINATÖR
		T.BERGSTRÖM
RESTALLARE		ÄNDRINGS PM
		-



PROJEKTNAMN		
CENTRALEKÖK		
OBJEKT		
ROBERTSFORS KOMMUN		
PROJEKTNUMMER	YTRE RINGVÄGEN 4	
DIREKTÖR	FASTIGHET	
	FORDONET 1	
DISCIPLIN	FÖRETAG	
	NORCONSULT SVERIGE AB	
UPPDRAGSNUMMER	SKAPAD AV	
1088371	OPN	
TELEFON	KONTAKTPERSON	
010 141 80 00	TOMAS BERGSTRÖM	
BYGGNADSVÄRK	PÅLÖSNINGSVÄRK	
	+45,54 (FG)	
VÄNINGSPLAN	VÄNINGSDEL	DELOMRÅDE
1		DEL 3
SYSTEM		
INBROTT & PASSAGE		
SPECIFIKATION		
PLAN 1		
TYTNINGSKVALITET	SKALA	FORMAT
PLANER	1:50	A1
DOCUMENTNUMMER	ÄNDRING	
E-64CCB-1-311	-	