



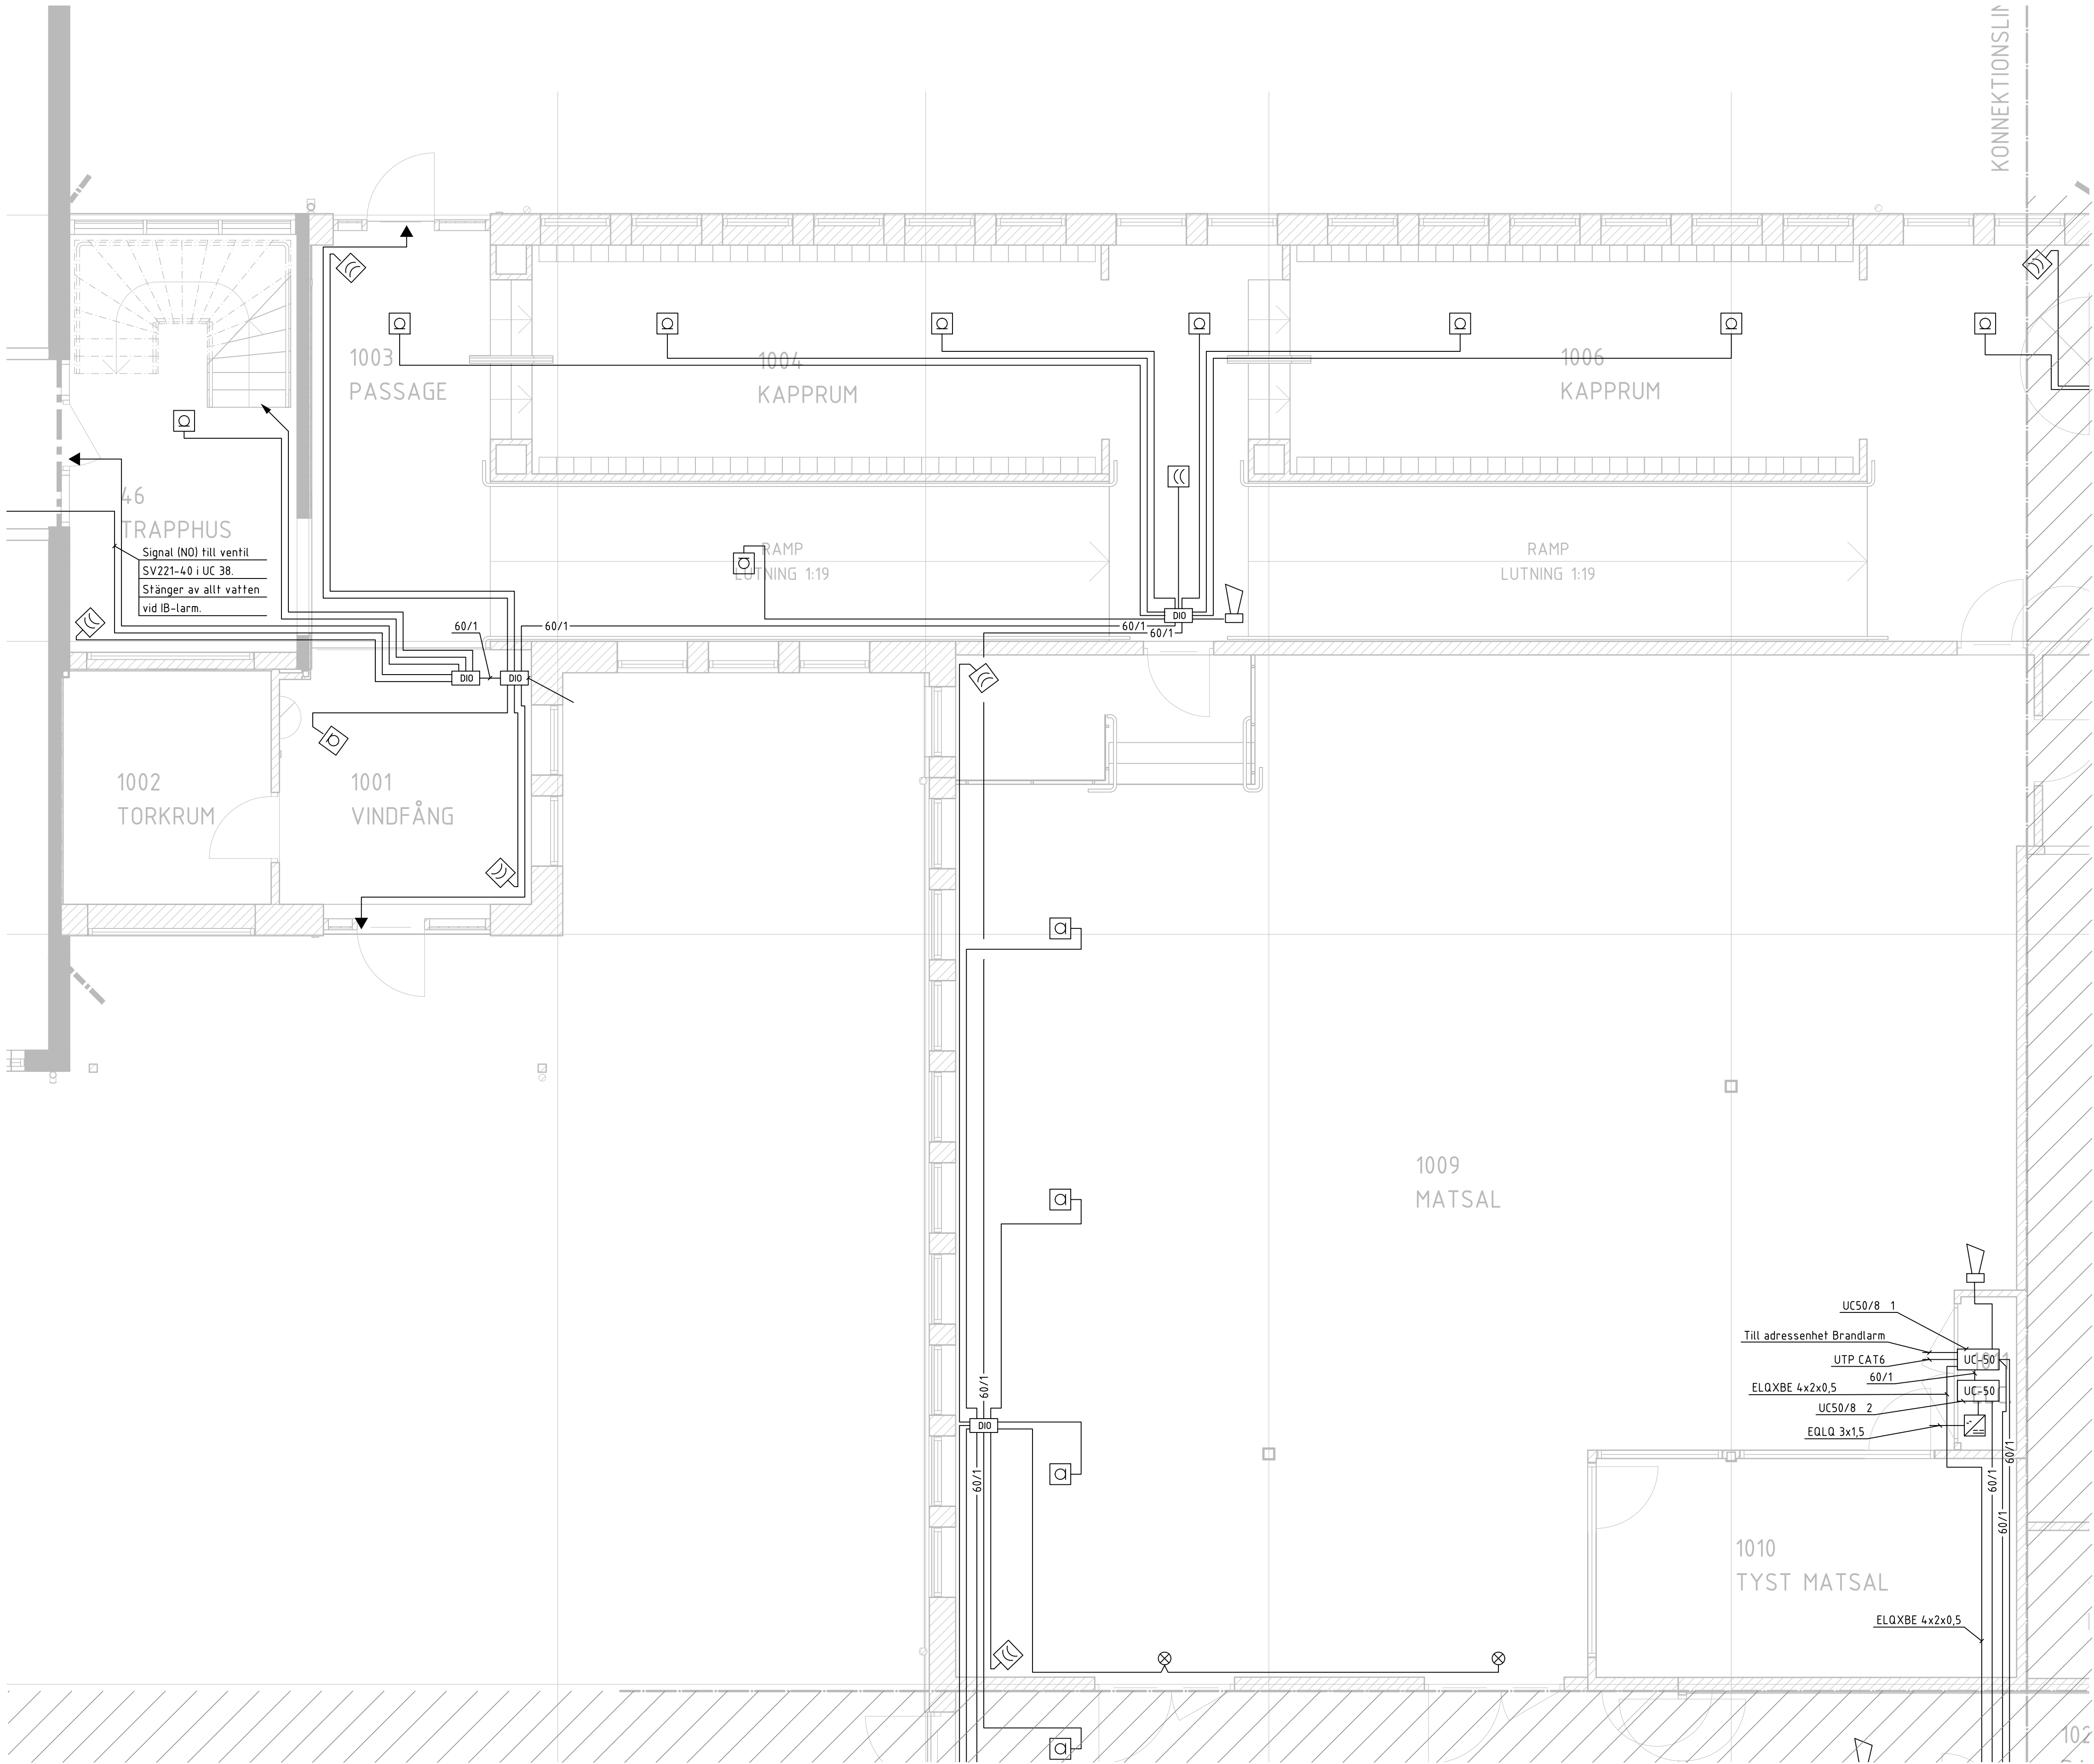

- ANVISNINGAR**
DOSOR OCH UTTAG SOM PLACERAS PÅ LEDNINGSSTEGE
MONTERAS PÅ STEGPLÅT.
RÖRELSEDETEKTORER OCH LARMÖN MONTERAS 50mm
NEDAN TAKVINKEL DÄR EJ ANNAT ANGES.
GLASKROSSDETEKTOR MONTERAS DIKT UNDER TAK RIKTADE
MOT FÖNSTERPARTI.
- KABEL, DÄR EJ ANNAT ANGES: ELOXB 2X2X0,5
- SYMBOLFÖRKLARINGAR**
- UC-50 CENTRALAPPARAT INTEGRERAT LARM-/PASSERSYSTEM
 - NÄTDEL INKL. BATTERIBACKUP
 - M MANÖVERPANEL ITEGRERAT SYSTEM, MONTERAS +1600mm ÖG
 - MAGNETKONTAKT
 - IR DETEKTOR
 - IR DETEKTOR 360°
 - AKUSTISK GLASKROSSDETEKTOR
 - INDIKERINGSLAMP, MONTERAS OVAN DÖRRKARM
 - DÖRR-/LARMÖN, MONTERAS OVAN UNDER TAK
 - KL KORTLÅSARE, MONTERAS +1200mm ÖM
 - ÖPPNAKNAPP, MONTERAS +1200mm ÖG
 - KÄRMÖVERFÖRNING
 - ELSLUTBLECK
 - 60/1- FLOQBR 1X2 + 2X2X0,22
 - 28/1- PTS-HF 2X2X0,6
 - DETEKTOR FÖRBINDOPPLAS VIA KORTLÅSARE "LASTBRYGGA" TILLS TILLOPPNING SKER ELLER EFTER MAX 30 MIN.
 - ENHET TERMINERAS. SE INSTALLATIONS MANUAL AKTUELL ENHET.

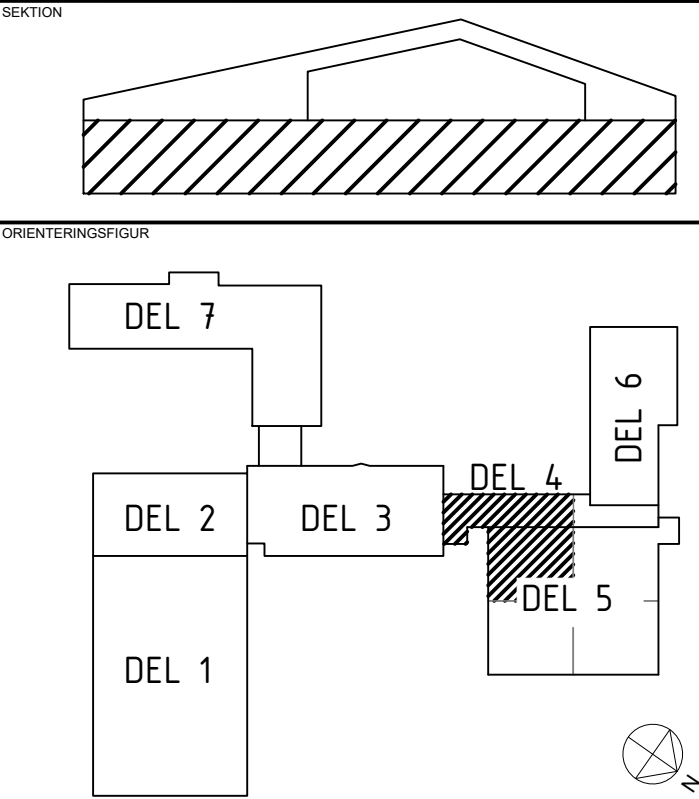

STATUS
FÖRFRÅGNINGSUNDERLAG

HANDLING
BYGGHANDLING

DATUM
2024-12-20

ANSÖKAN AV
T. BERGSTRÖM

ÄNDRING PÅ
-



PROJEKTNAMN
CENTRALEKÖ

OMRÄDE
ROBERTSFORS KOMMUN

PROJEKTNUMMER
FASTIGHET
YTTRE RINGVÄGEN 4

DIREKTOR
FORDONET 1

DISCIPLIN
FÖRETAG
NORCONSULT SVERIGE AB

UPPDRAGSNUMMER
SKAPAD AV
1088371 OPN

TELEFON
KONTAKTPERSON
010 141 80 00 TOMAS BERGSTRÖM

BYGGNADSVÄRDE
FÖLJESKEDVÄRDE
+45,54 (FG)

VÄNINGSPLAN
VÄNINGSDEL
1

DELÖMRÅDE
DEL 4.1, 5.1

SYSTEM
INBROT & PASSAGE

SPECIFIKATION
PLAN 1

PLANER
SKALA
1:50

FORMAT
A1

ANSÖKAN
-

DOCUMENTNUMMER
E-64CCB-1-511