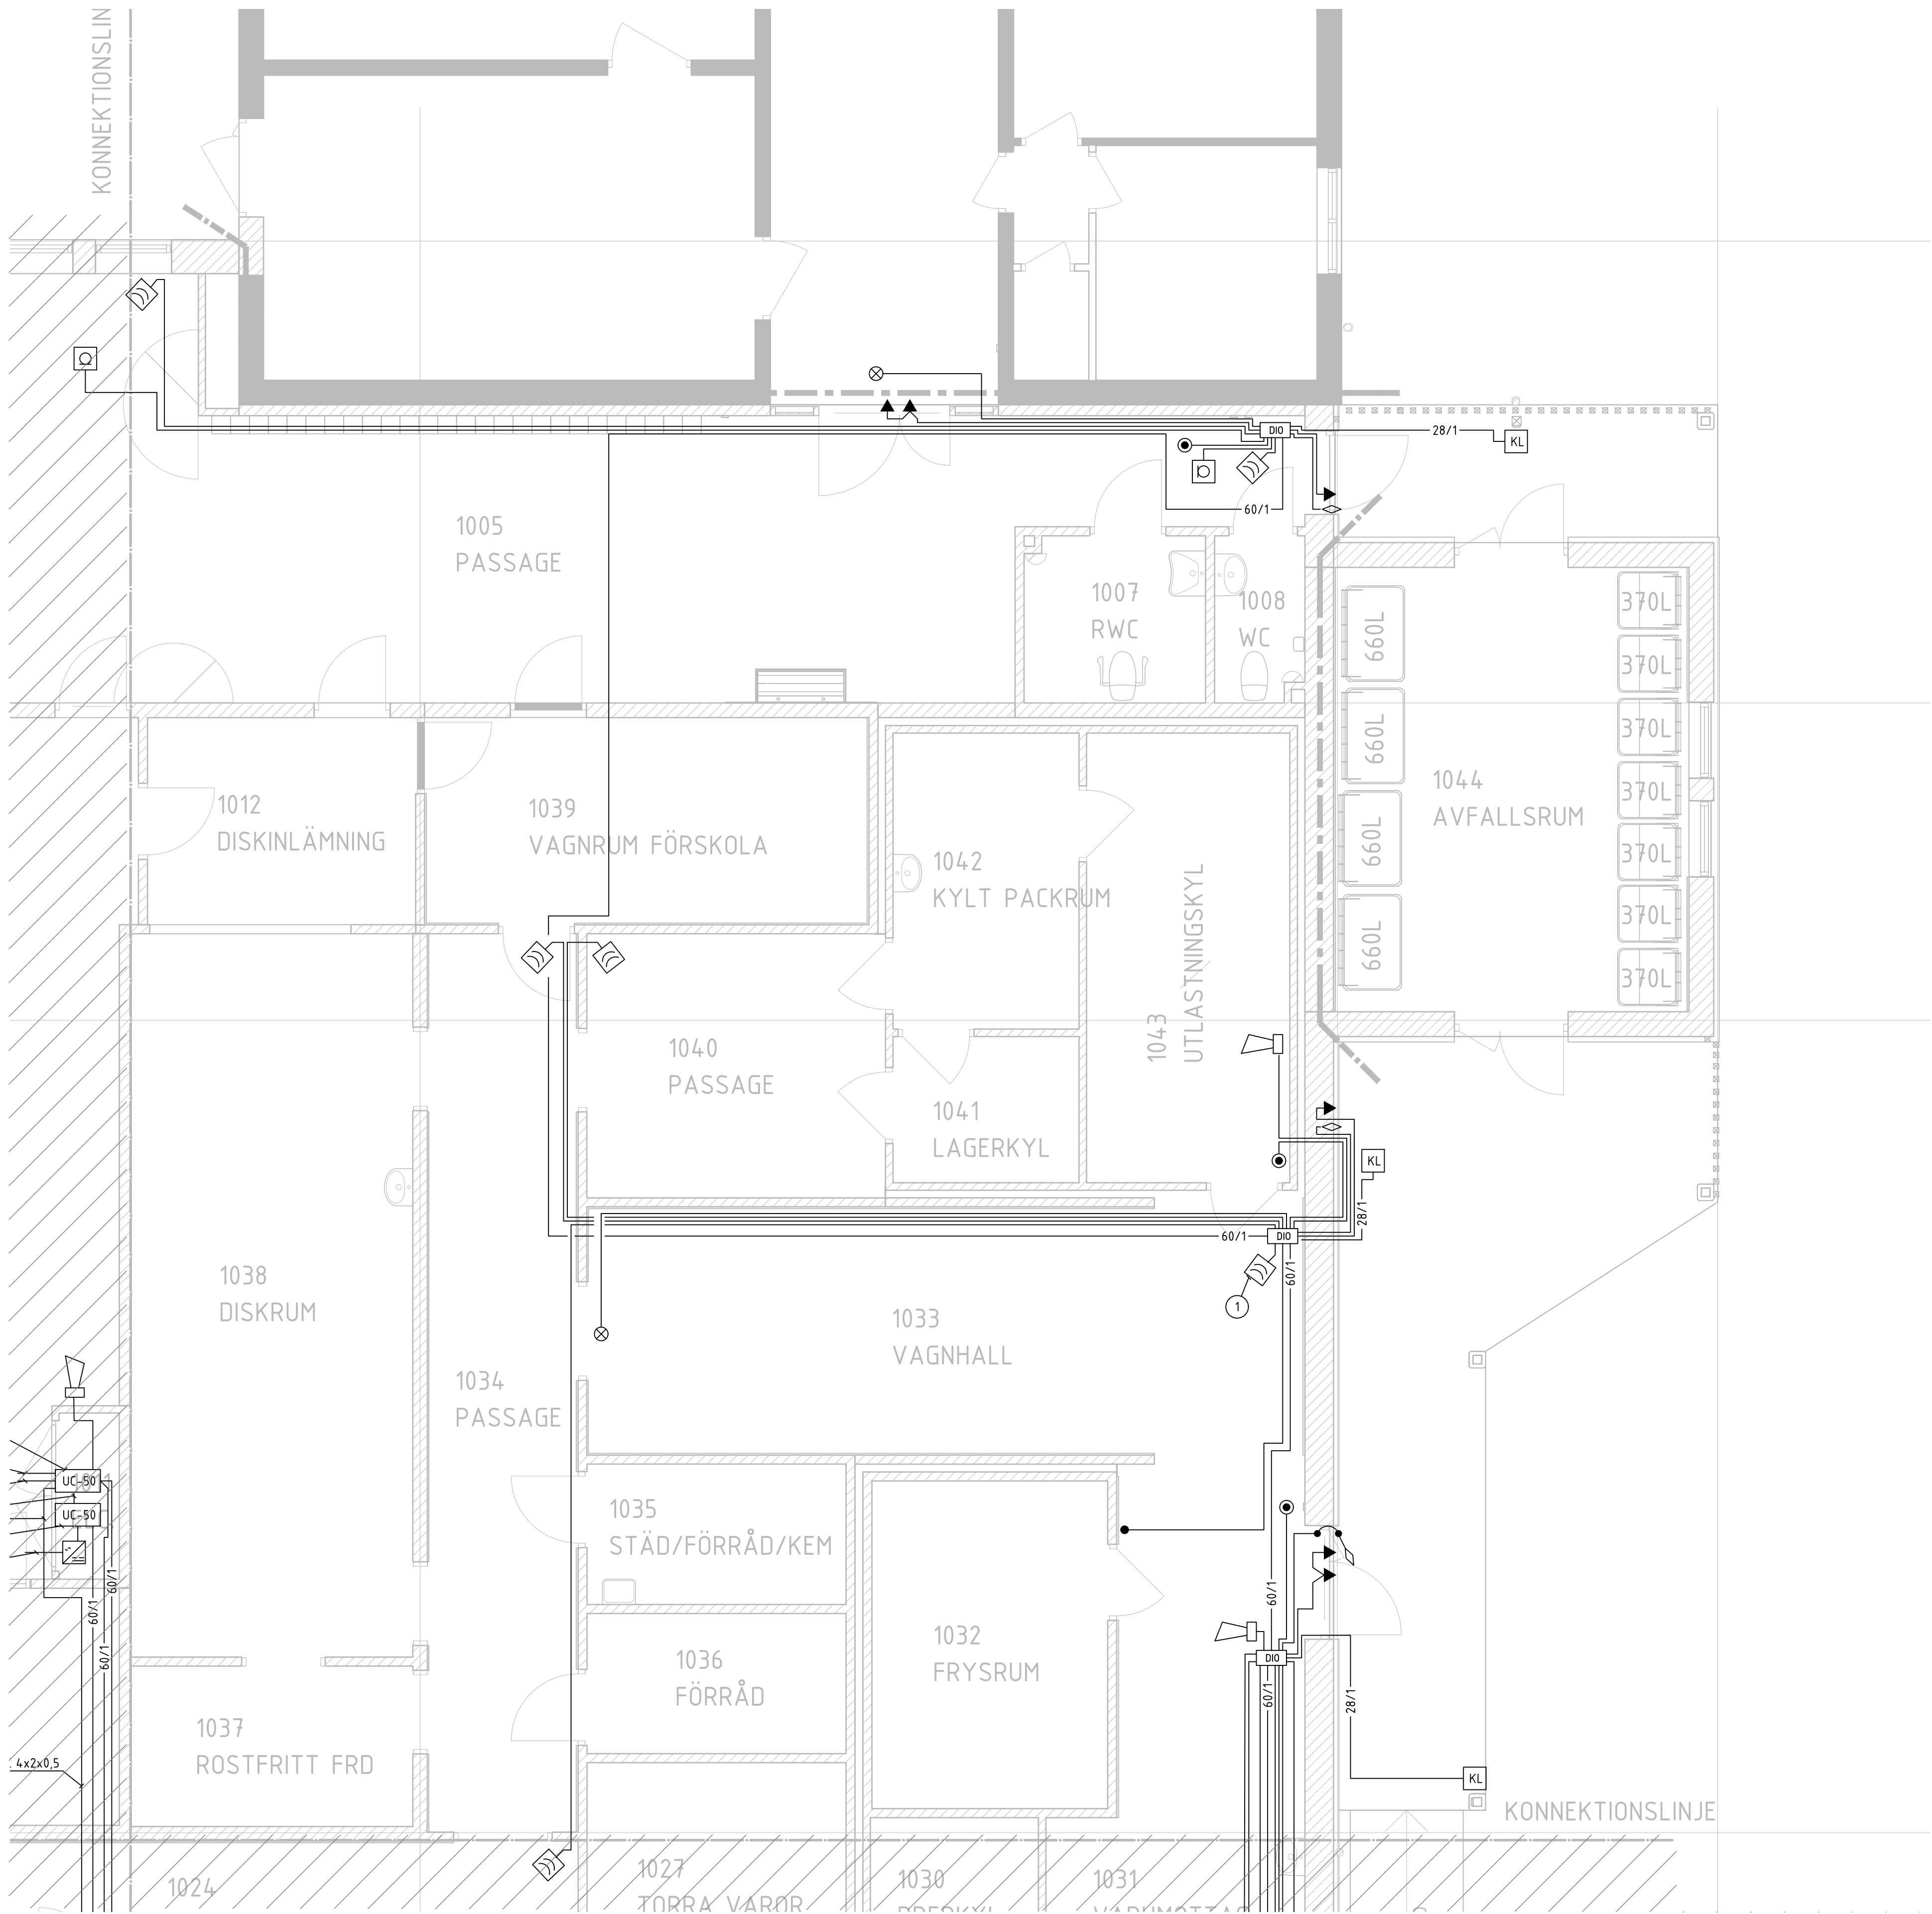


ANVISNINGAR
DOSOR OCH UTTAG SOM PLACERAS PÅ LEDNINGSSTEGE
MONTERAS PÅ STEGPLÅT.
RÖRELSEDETEKTORER OCH LARMÖN MONTERAS 50mm
NEDAN TAKVINKEL DÄR EJ ANNAT ANGES.
GLASKROSSDETEKTOR MONTERAS DIKT UNDER TAK RIKTADE
MOT FÖNSTERPARTI.

KABEL, DÄR EJ ANNAT ANGES: ELQXB 2X2X0,5

SYMBOLFÖRKLARINGAR

- UC-50 CENTRALAPPARAT INTEGRERAT
LARM-/PASSERSYSTEM
- NÄTDEL INKL. BATTERIBACKUP
- M HÄNÖVERPANEL ITEGRERAT SYSTEM,
MONTERAS +1600mm ÖG
- MAGNETKONTAKT
- IR DETEKTOR
- IR DETEKTOR 360°
- AKUSTISK GLASKROSSDETEKTOR
- INDIKERINGSLAMP, MONTERAS OVAN DÖRRKARM
- DÖRR-/LARMÖN, MONTERAS OVAN UNDER TAK
- KL KORTLÄSARE, MONTERAS +1200mm ÖM
- ÖPPNAKNAPP, MONTERAS +1200mm ÖG
- KÄRMÖVERFÖRING
- ELSLUTBLECK

-60/1- FLOQBR 1X2 + 2X2X0,22

-28/1- PTS-HF 2X2X0,6

- DETEKTOR FÖRBIKOPPLAS VIA KORTLÄSARE
"LASTBRYGGA" TILLS TILLOPPNING SKER
ELLER EFTER MAX 30 MIN.
- T ENHET TERMINERAS. SE INSTALLATIONS MANUAL
AKTUELL ENHET.

SEKTION

ORIENTERINGSFIGUR

DEL 7
DEL 2
DEL 3
DEL 4
DEL 5
DEL 6
DEL 1

STATUS

FÖRFRÅGNINGSUNDERLAG

HANDLING

BYGGHANDLING

DATUM 2024-12-20

ANSÖKAN AV T. BERGSTRÖM

ÄNDRING PÅ -

BESTÄLLARE

ROBERTSFORS KOMMUN

PROJEKTNAMN

CENTRALEKÖ

OMRÅDE

ROBERTSFORS KOMMUN

PROJEKTNUMMER

YTTRE RINGVÄGEN 4

DÄRNUMMER

FÄSTIGHET

FORDONET 1

DISCIPLIN

NORCONSULT SVERIGE AB

UPPDRAGSNUMMER

SKAPAD AV

1088371

OPN

TELEFON

KONTAKTPERSON

010 141 80 00

TOMAS BERGSTRÖM

BYGGNADSVÄRDE

PLANSKIVVÄRDE

+45,54 (FG)

VÄNINGSPLAN

VÄNINGSDEL

DELOMRÅDE

1

DEL 4.2, 5.2

SYSTEM

INBROTT & PASSAGE

SPECIFIKATION

PLAN 1

FORMAT

A1

SKALA

1:50

ANSÖKAN

-

DOCUMENTNUMMER

E-64CCB-1-512