
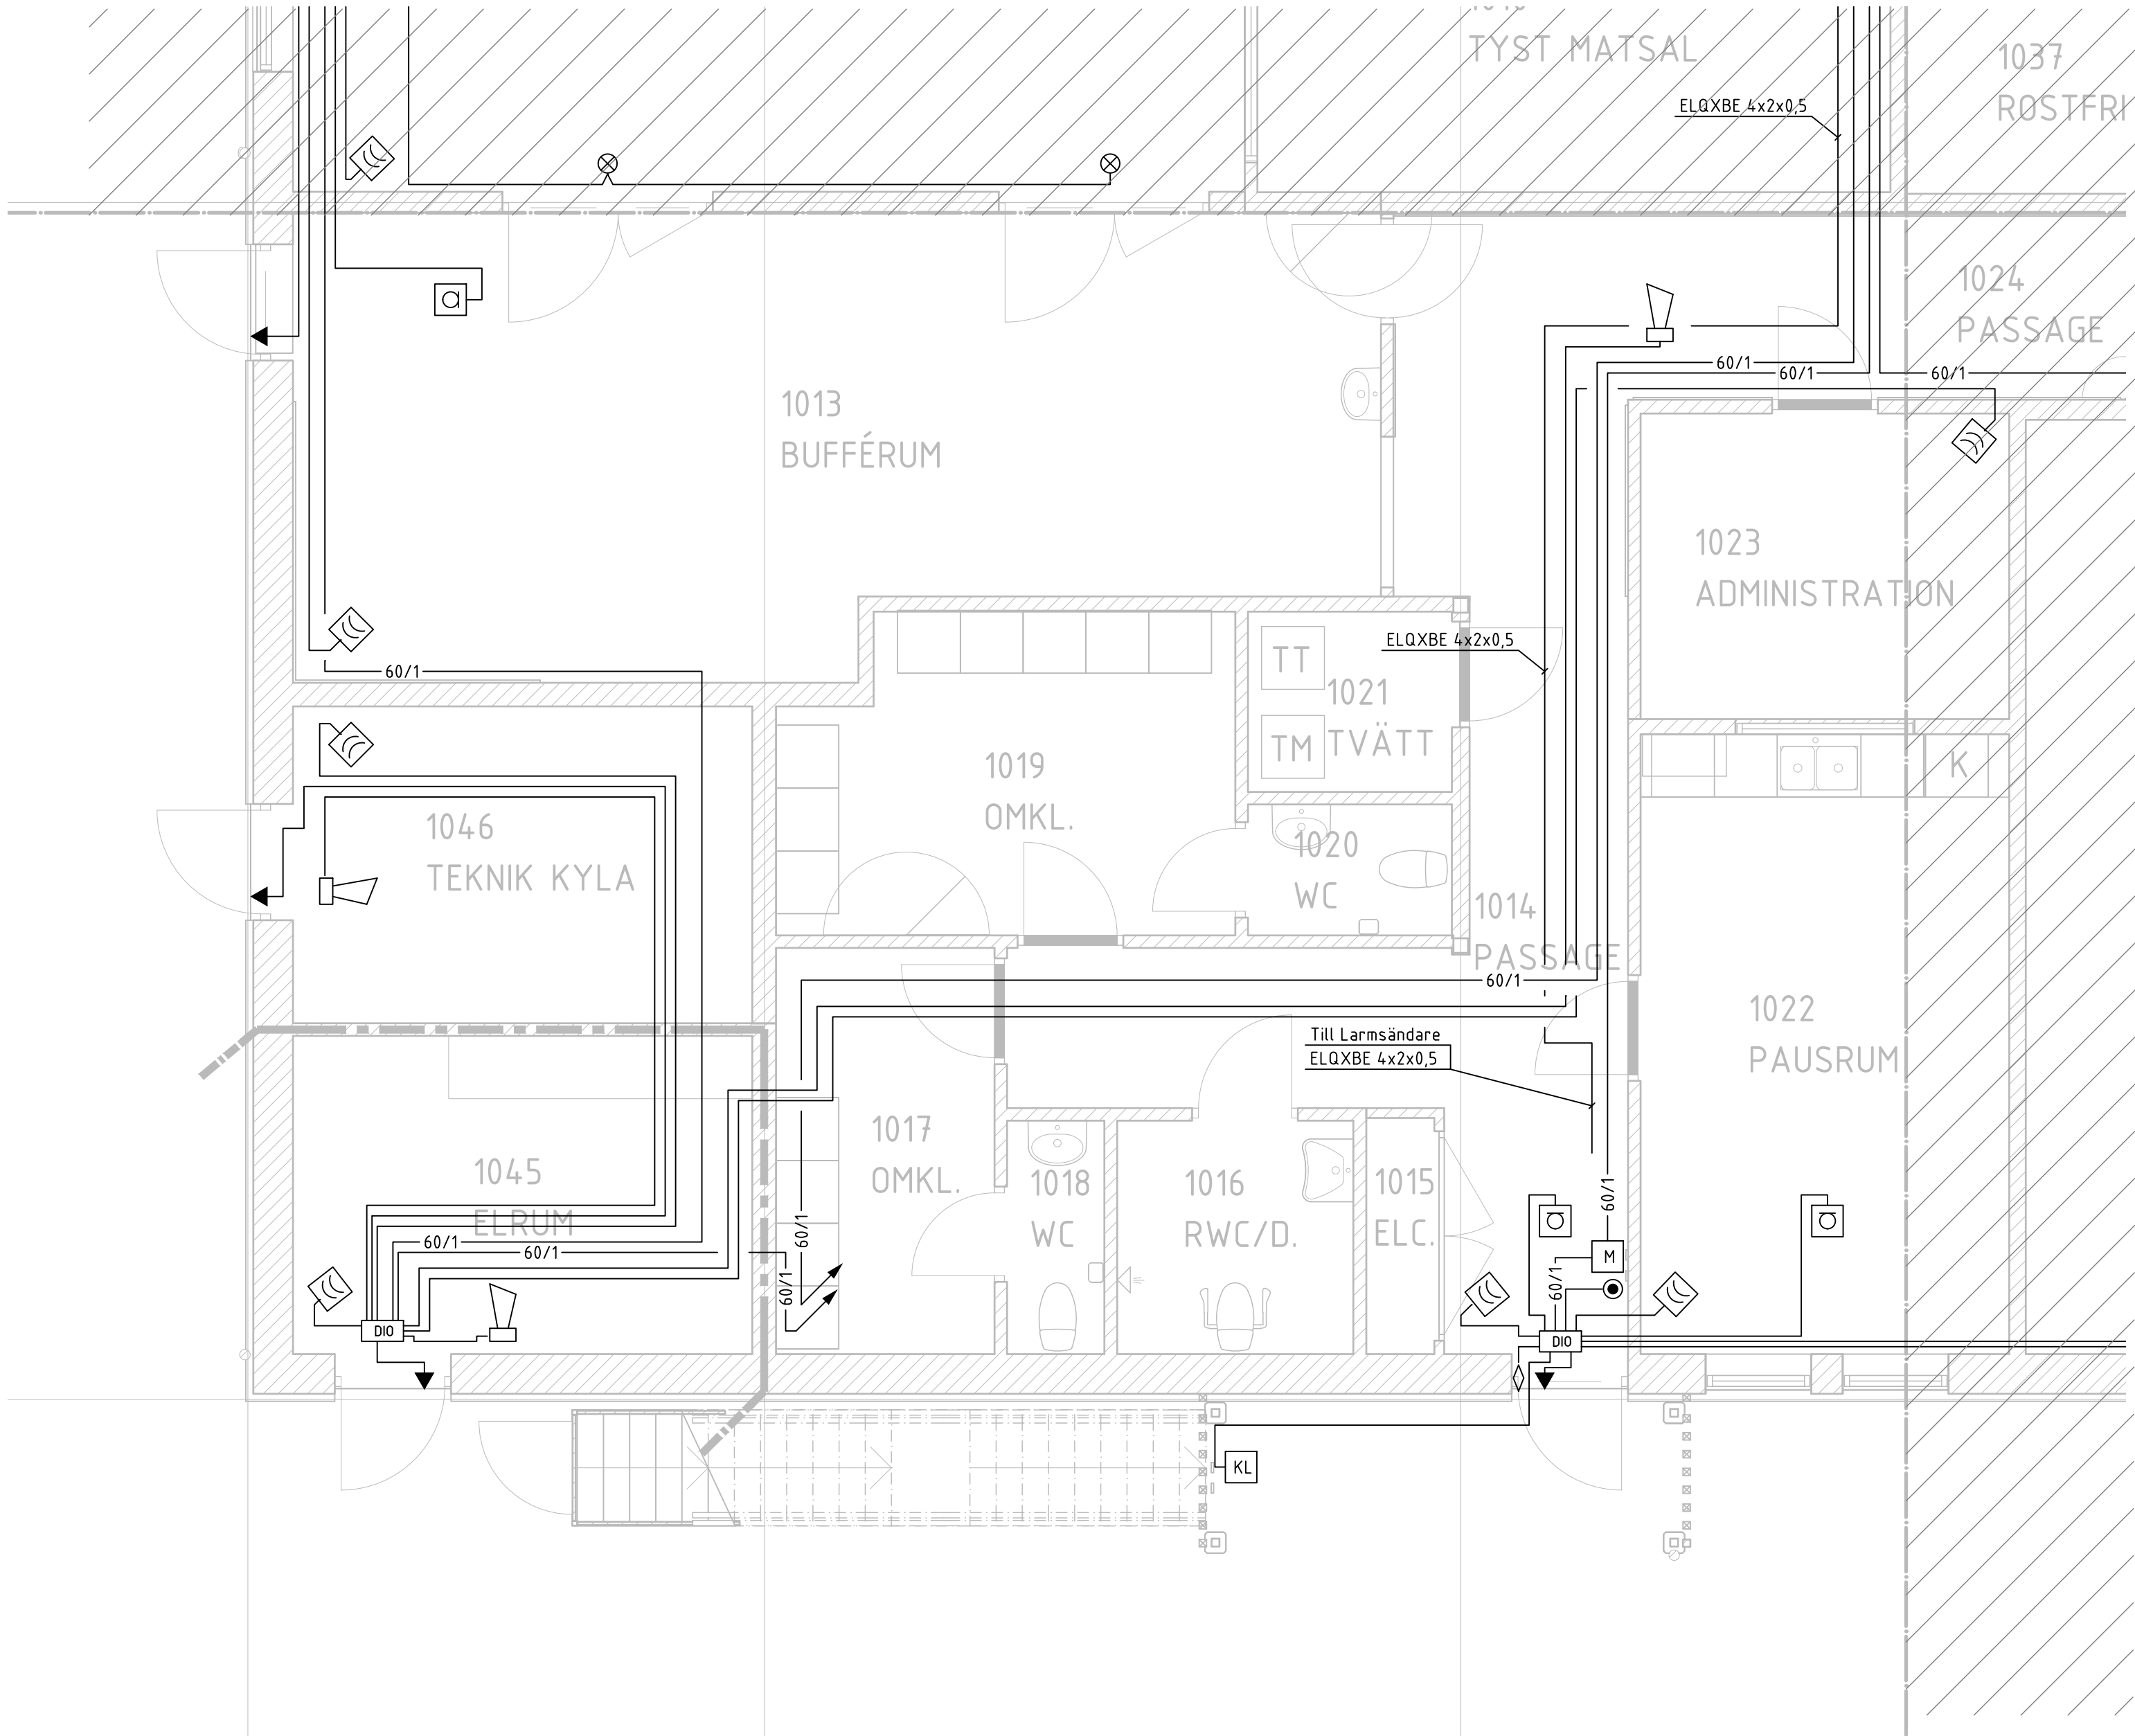


ANVISNINGAR
DOSOR OCH UTTAG SOM PLACERAS PÅ LEDNINGSGE
MONTERAS PÅ STEGPLÅT.
RÖRESEDETEKTORER OCH LARMON MONTERAS 50mm
NEDAN TAKVINKEL DÄR EJ ANNAT ANGES.
GLASKROSSDETEKTOR MONTERAS DIKT UNDER TAK RIKTADE
MOT FÖNSTERPARTI.

KABEL, DÄR EJ ANNAT ANGES: ELQXB 2X2X0,5

SYMBOLFÖRKLARINGAR

- UC-50 CENTRALAPPARAT INTEGRERAT LARM-/PASSERSYSTEM
- NÄTDEL INKL. BATTERIBACKUP
- M MANÖVERPANEL ITEGRERAT SYSTEM, MONTERAS +1600mm ÖG
- MAGNETKONTAKT
- IR DETEKTOR
- IR DETEKTOR 360°
- AKUSTISK GLASKROSSDETEKTOR
- INDIKERINGSLAMP, MONTERAS OVAN DÖRRKARM
- DÖRR-/LARMOD, MONTERAS OVAN UNDER TAK
- KORTLÄSARE, MONTERAS +1200mm ÖM
- ÖPPNAKNAPP, MONTERAS +1200mm ÖG
- KARMOVERFÖRING
- ELSLUTBLECK
- 60/1- FLOQBR 1X2 + 2X2X0,22
- 28/1- PTS-HF 2X2X0,6
- DETEKTOR FÖRBKOPPLAS VIA KORTLÄSARE "LASTBRYGGA" TILLS TILKOPPLING SKER ELLER EFTER MAX 30 MIN.
- ENHET TERMINERAS. SE INSTALLATIONS MANUAL AKTUELL ENHET.

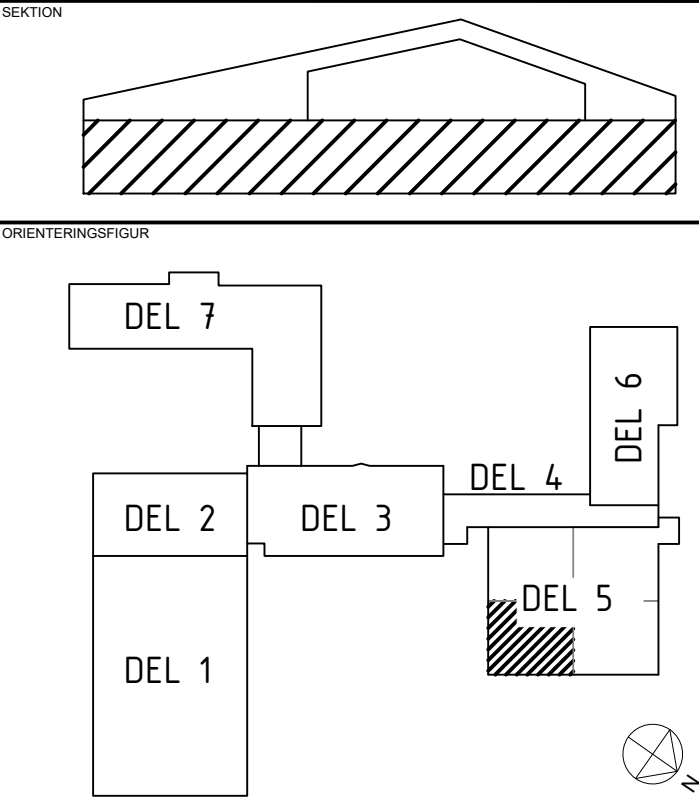

STATUS
FÖRFRÅGNINGSUNDERLAG

HANDLING
BYGGHANDLING

DATUM
2024-12-20

COORDINAT
T. BERGSTRÖM

ÄNDRINGS PM
-



PROJEKTNAMN		
CENTRALKÖK		
OMRÅDE		
ROBERTSFORS KOMMUN		
PROJEKTNUMMER	ADRESS	
	YTTRE RINGVÄGEN 4	
DÄRRETNAMN	FASTIGHET	
	FORDONET 1	
DISCIPLIN	FÖRETAG	
E	NORCONSULT SVERIGE AB	
UPPDRAGSNUMMER	SKAPAD AV	
1088371	OPN	
TELEFON	KONTAKTPERSON	
010 141 80 00	TOMAS BERGSTRÖM	
BYGGNADSVÄR	FÖLJESKEDVÄR	
	+45,54 (FG)	
VÄNINGSPLAN	VÄNINGSDEL	DELOMRÅDE
1		DEL 5.3
SYSTEM		
INBROTT & PASSAGE		
SPECIFIKATION		
PLAN 1		
TYTTERSKATTNING	SKALA	FORMAT
PLANER	1:50	A1
DOCUMENTNUMMER	ÄNDRING	
E-64CCB-1-513	-	