



- ANVISNINGAR**
- DOSOR OCH UTTAG SOM PLACERAS PÅ LEDNINGSSTEGE
MONTERAS PÅ STEGPLÅT.
RÖRELSEDETEKTORER OCH LARMODN MONTERAS 50mm
NEDAN TAKVINKEL DÄR EJ ANNAT ANGES.
GLASKROSSDETEKTOR MONTERAS DIKT UNDER TAK RIKTADE
MOT FÖNSTERPARTI.
- KABEL, DÄR EJ ANNAT ANGES: ELQXB 2X2X0,5
- SYMBOLFÖRKLARINGAR**
- UC-50 CENTRALAPPARAT INTEGRERAT LARM-/PASSERSYSTEM
 - NÄTDEL INKL. BATTERIBACKUP
 - M MANÖVERPANEL ITEGRERAT SYSTEM, MONTERAS +1600mm ÖG
 - MAGNETKONTAKT
 - IR DETEKTOR
 - IR DETEKTOR 360°
 - AKUSTISK GLASKROSSDETEKTOR
 - INDIKERINGSLAMP, MONTERAS OVAN DÖRRKARM
 - DÖRR-/LARMOD, MONTERAS OVAN UNDER TAK
 - KORTLÄSARE, MONTERAS +1200mm ÖM
 - ÖPPNAKNAPP, MONTERAS +1200mm ÖG
 - KARHÖVERFÖRING
 - ELSLUTBLECK
 - FLQGBR 1X2 + 2X2X0,22
 - PTS-HF 2X2X0,6
 - DETEKTOR FÖRBKOPPLAS VIA KORTLÄSARE "LASTBRYGGA" TILLS TILLKOPPLING SÄKER ELLER EFTER MAX 30 MIN.
 - ENHET TERMINERAS. SE INSTALLATIONS MANUAL AKTUELL ENHET.

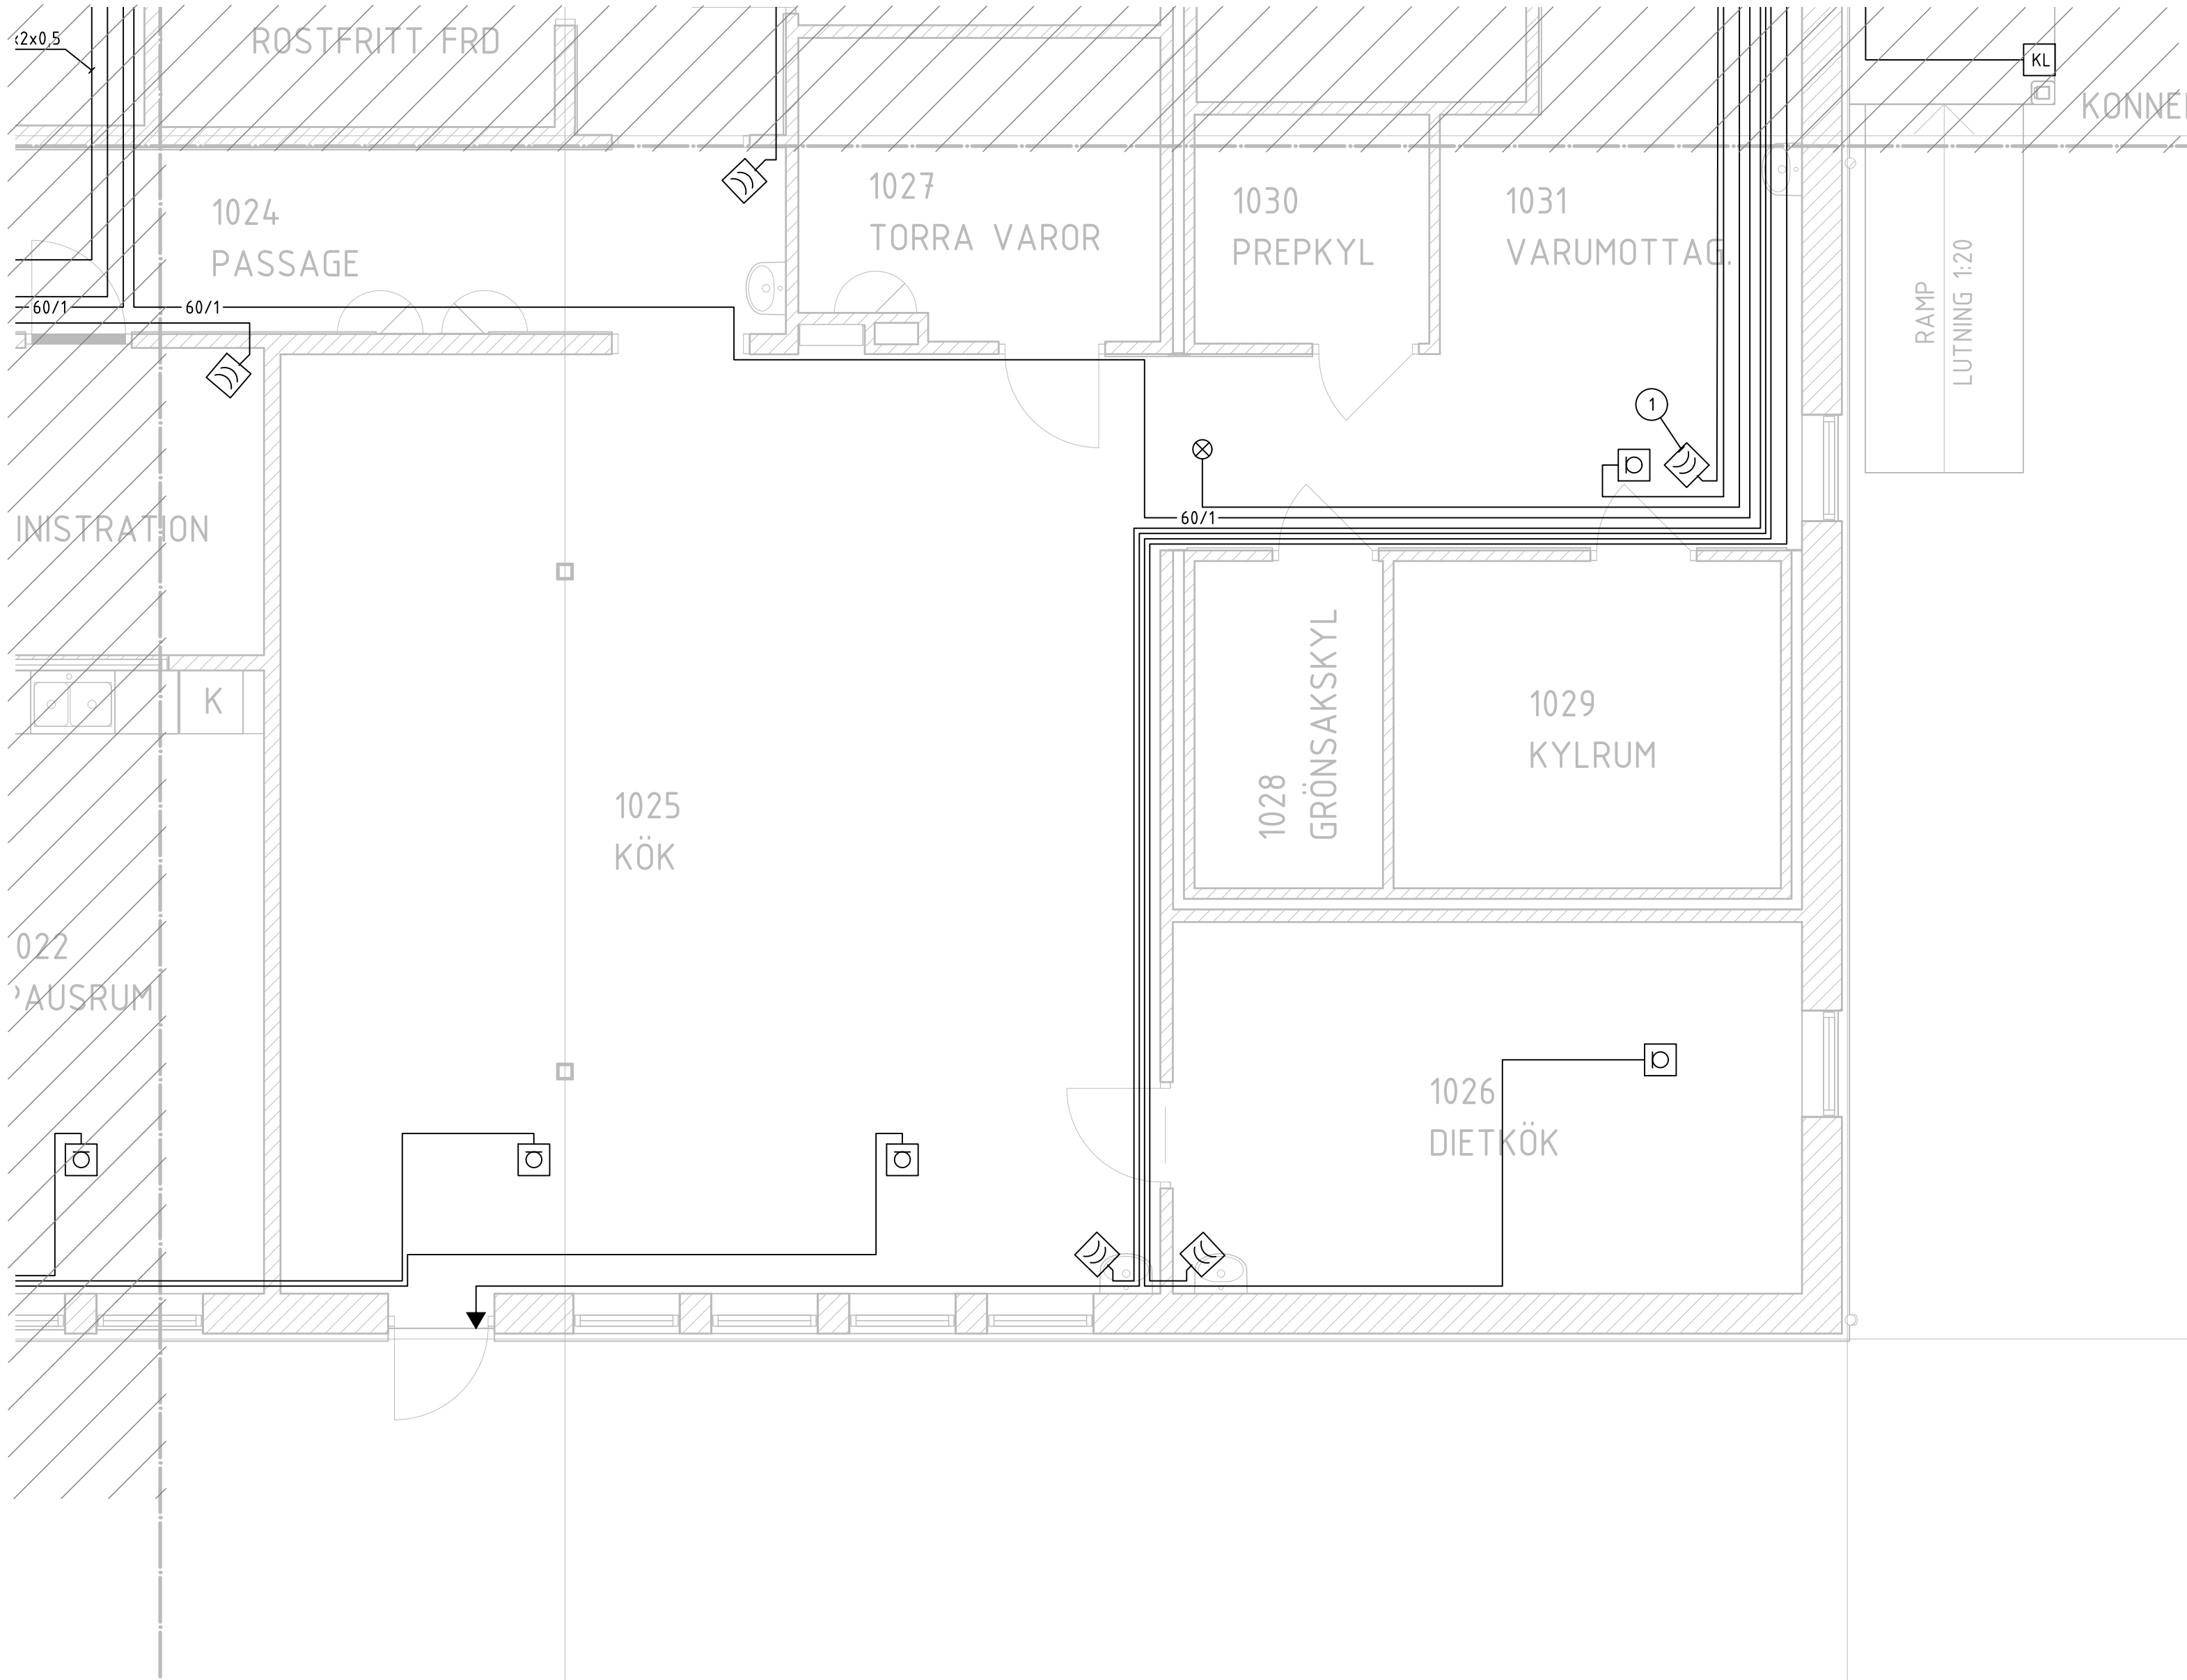

STATUS		
FÖRFRÅGNINGSUNDERLAG		
HANDLING		
BYGGHANDLING		
DATUM	2024-12-20	COORDINATÖR
		T. BERGSTRÖM
ANFÖRARE		

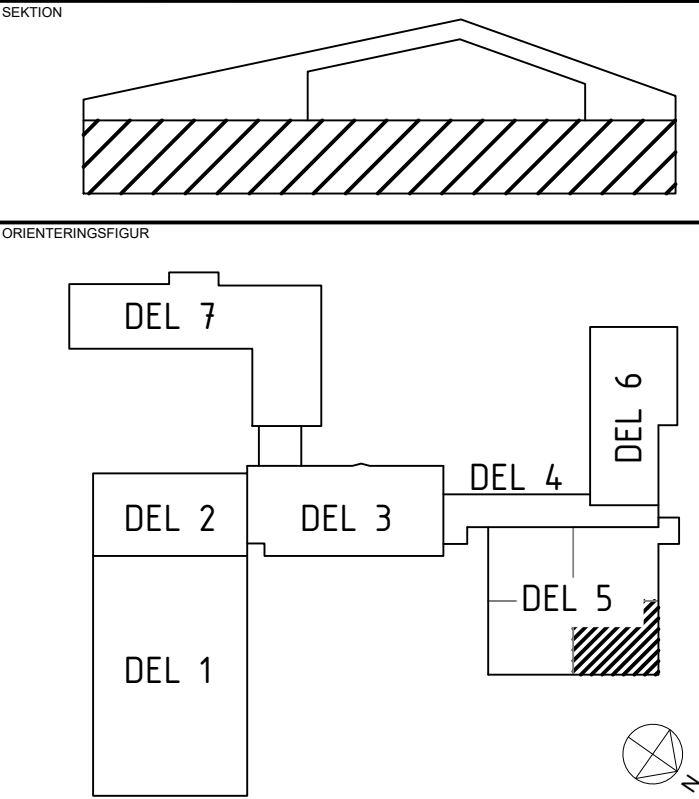

PROJEKTNAMN		
CENTRALKÖK		
OBJEKT		
ROBERTSFORS KOMMUN		
PROJEKTNUMMER	YTTRE RINGVÄGEN 4	
DÄRRETNUMMER	FASTIGHET	
	FORDONET 1	
DISCIPLIN	FÖRETAG	
	NORCONSULT SVERIGE AB	
UPPDRAGSNUMMER	SKAPAD AV	
1088371	OPN	
TELEFON	KONTAKTPERSON	
010 141 80 00	TOMAS BERGSTRÖM	
BYGGNADSVÄR	FÖLJESKIVOR (2024)	
	+45,54 (FG)	
VÄNINGSPLAN	VÄNINGSDEL	DELOMRÅDE
1		DEL 5.3
SYSTEM		
INBROTT & PASSAGE		
SPECIFIKATION		
PLAN 1		
TYTTERSKATTNING	SKALA	FORMAT
PLANER	1:50	A1
DOCUMENTNUMMER	ÄNDRING	
E-64CCB-1-514	-	