


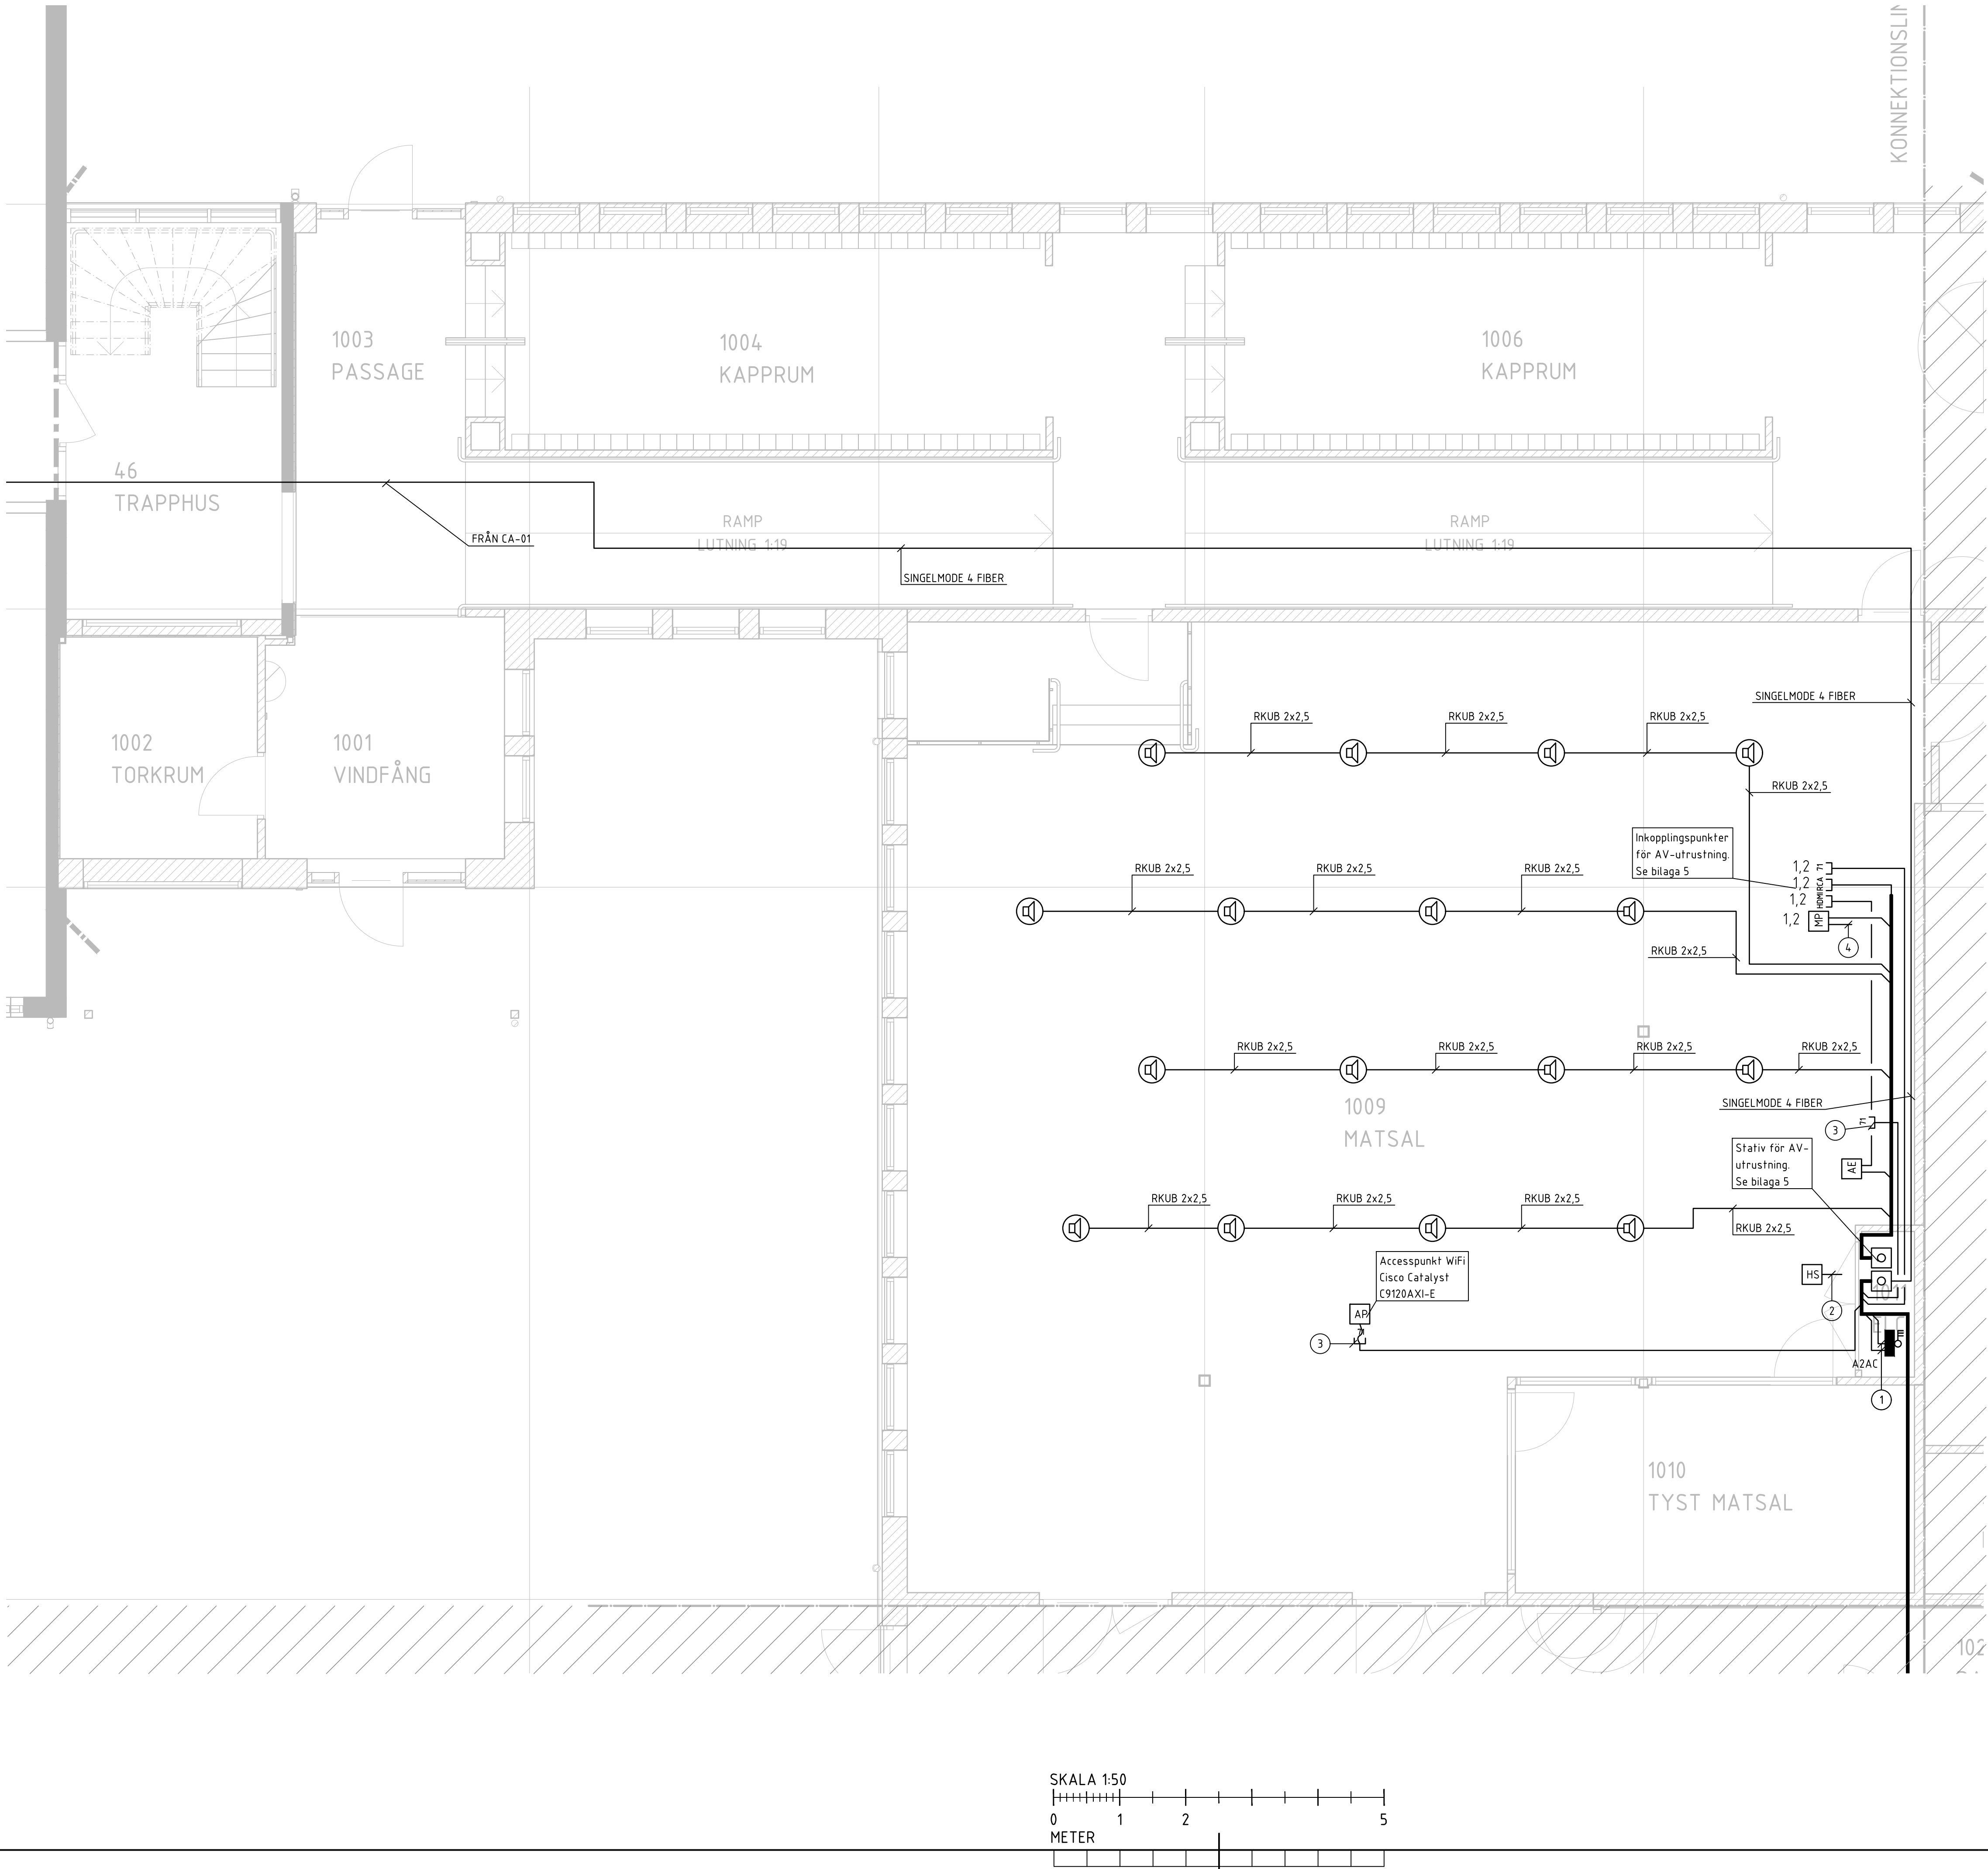

ANVISNINGAR
INFÄLLT MONTAGE.
HALOGENFRITT MATERIAL
FYLLED SYMBOL = INFÄLLD. EJ FYLLED = UTANPÅLIGGANDE.

SYMBOLFÖRKLARINGAR

- MONTERINGSSTATIV 19"
- 2x8 POL RJ45 UTTAG
- 1x8 POL RJ45 UTTAG
- U/UTP CAT 6A KABEL
- ACCESSPUNKT WIFI. LEVERERAS AV BEST.
- AKTIV SKYLT FÖR HÖRSLINGA TYP TRANSISTOR T-SIGN 3000115. MONTERAS 15 MÖG. ANSLUTS TILL VÄGGUTTAG PÅ STEGE. ANSLUTNINGSKABEL FÖR- LÄGGS I VP25 I VÄGG TILL STEGE.
- HDMI AUDIO EXTRACTOR. MONTERAS TELEDOSA.
- HÖGTALARE ENLIGT BESKRIVNING. MONTERAS INFÄLLD I UNDERTAK.
- RWC -SIGNAL:
- MINNESENHET +0.7
- RUMSLAMPA MED SUMMER +2.2
- NÖDSIGNALKNAPP +0.2
- NÖDSIGNALKNAPP MED SIGNALUTTAG +0.55
- NÖDSIGNALSKNAPP MED DRAGKONTAKT +0.55
- NÄTVERSKABEL TYP U/UTP CAT6a 4P TILL DALIROUTRAR HELVAR 905 OCH 910 I CENTRALER.
- ANSLUTS TILL VÄGGUTTAG PÅ KABELSTEGE
- MONTERAS PÅ DOSPLÅT PÅ KABELSTEGE.
- STRÖMFÖRSÖRJNING SE RITNING E63BC.1-512.

SEKTION

ORIENTERINGSFIGUR

STATUS

FÖRFRÅGNINGSUNDERLAG

HANDLING

BYGGHANDLING

DATUM

2024-12-20

TEGNADE AV

GIN

ÄNDRINGS PM

-

BESTÄLLARE

ROBERTSFORS KOMMUN

PROJEKTNAMN

CENTRAKKÖK

OMRÅDE

ROBERTSFORS KOMMUN

PROJEKTNUMMER

YTTRE RINGVÄGEN 4

DÄRRETNUMMER

FASTIGHET

FORDONET 1

DISCIPLIN

FORETAG

NORCONSULT SVERIGE AB

UPPDRAGSNUMMER

1088371

SKAPAD AV

GIN

TELEFON

010 141 80 00

KONTAKTPERSON

TOMAS BERGSTRÖM

BYGGNADSVÄRK

PLÅNSHUVUDPRIS

+45,54 (FG)

VÄNINGSPLAN

1

VÄNINGSDEL

DELOMRÅDE

DEL 4.1, 5.1

SYSTEM

KOMMUNIKATION

SPECIFIKATION

PLAN 1

SKALA

1:50

FORMAT

A1

ANORDNING

-

DOCUMENTNUMMER

E-64ED-1-511