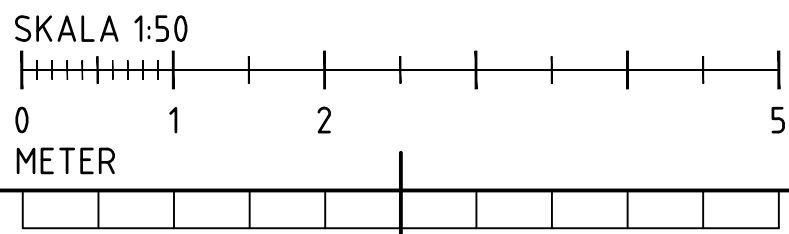
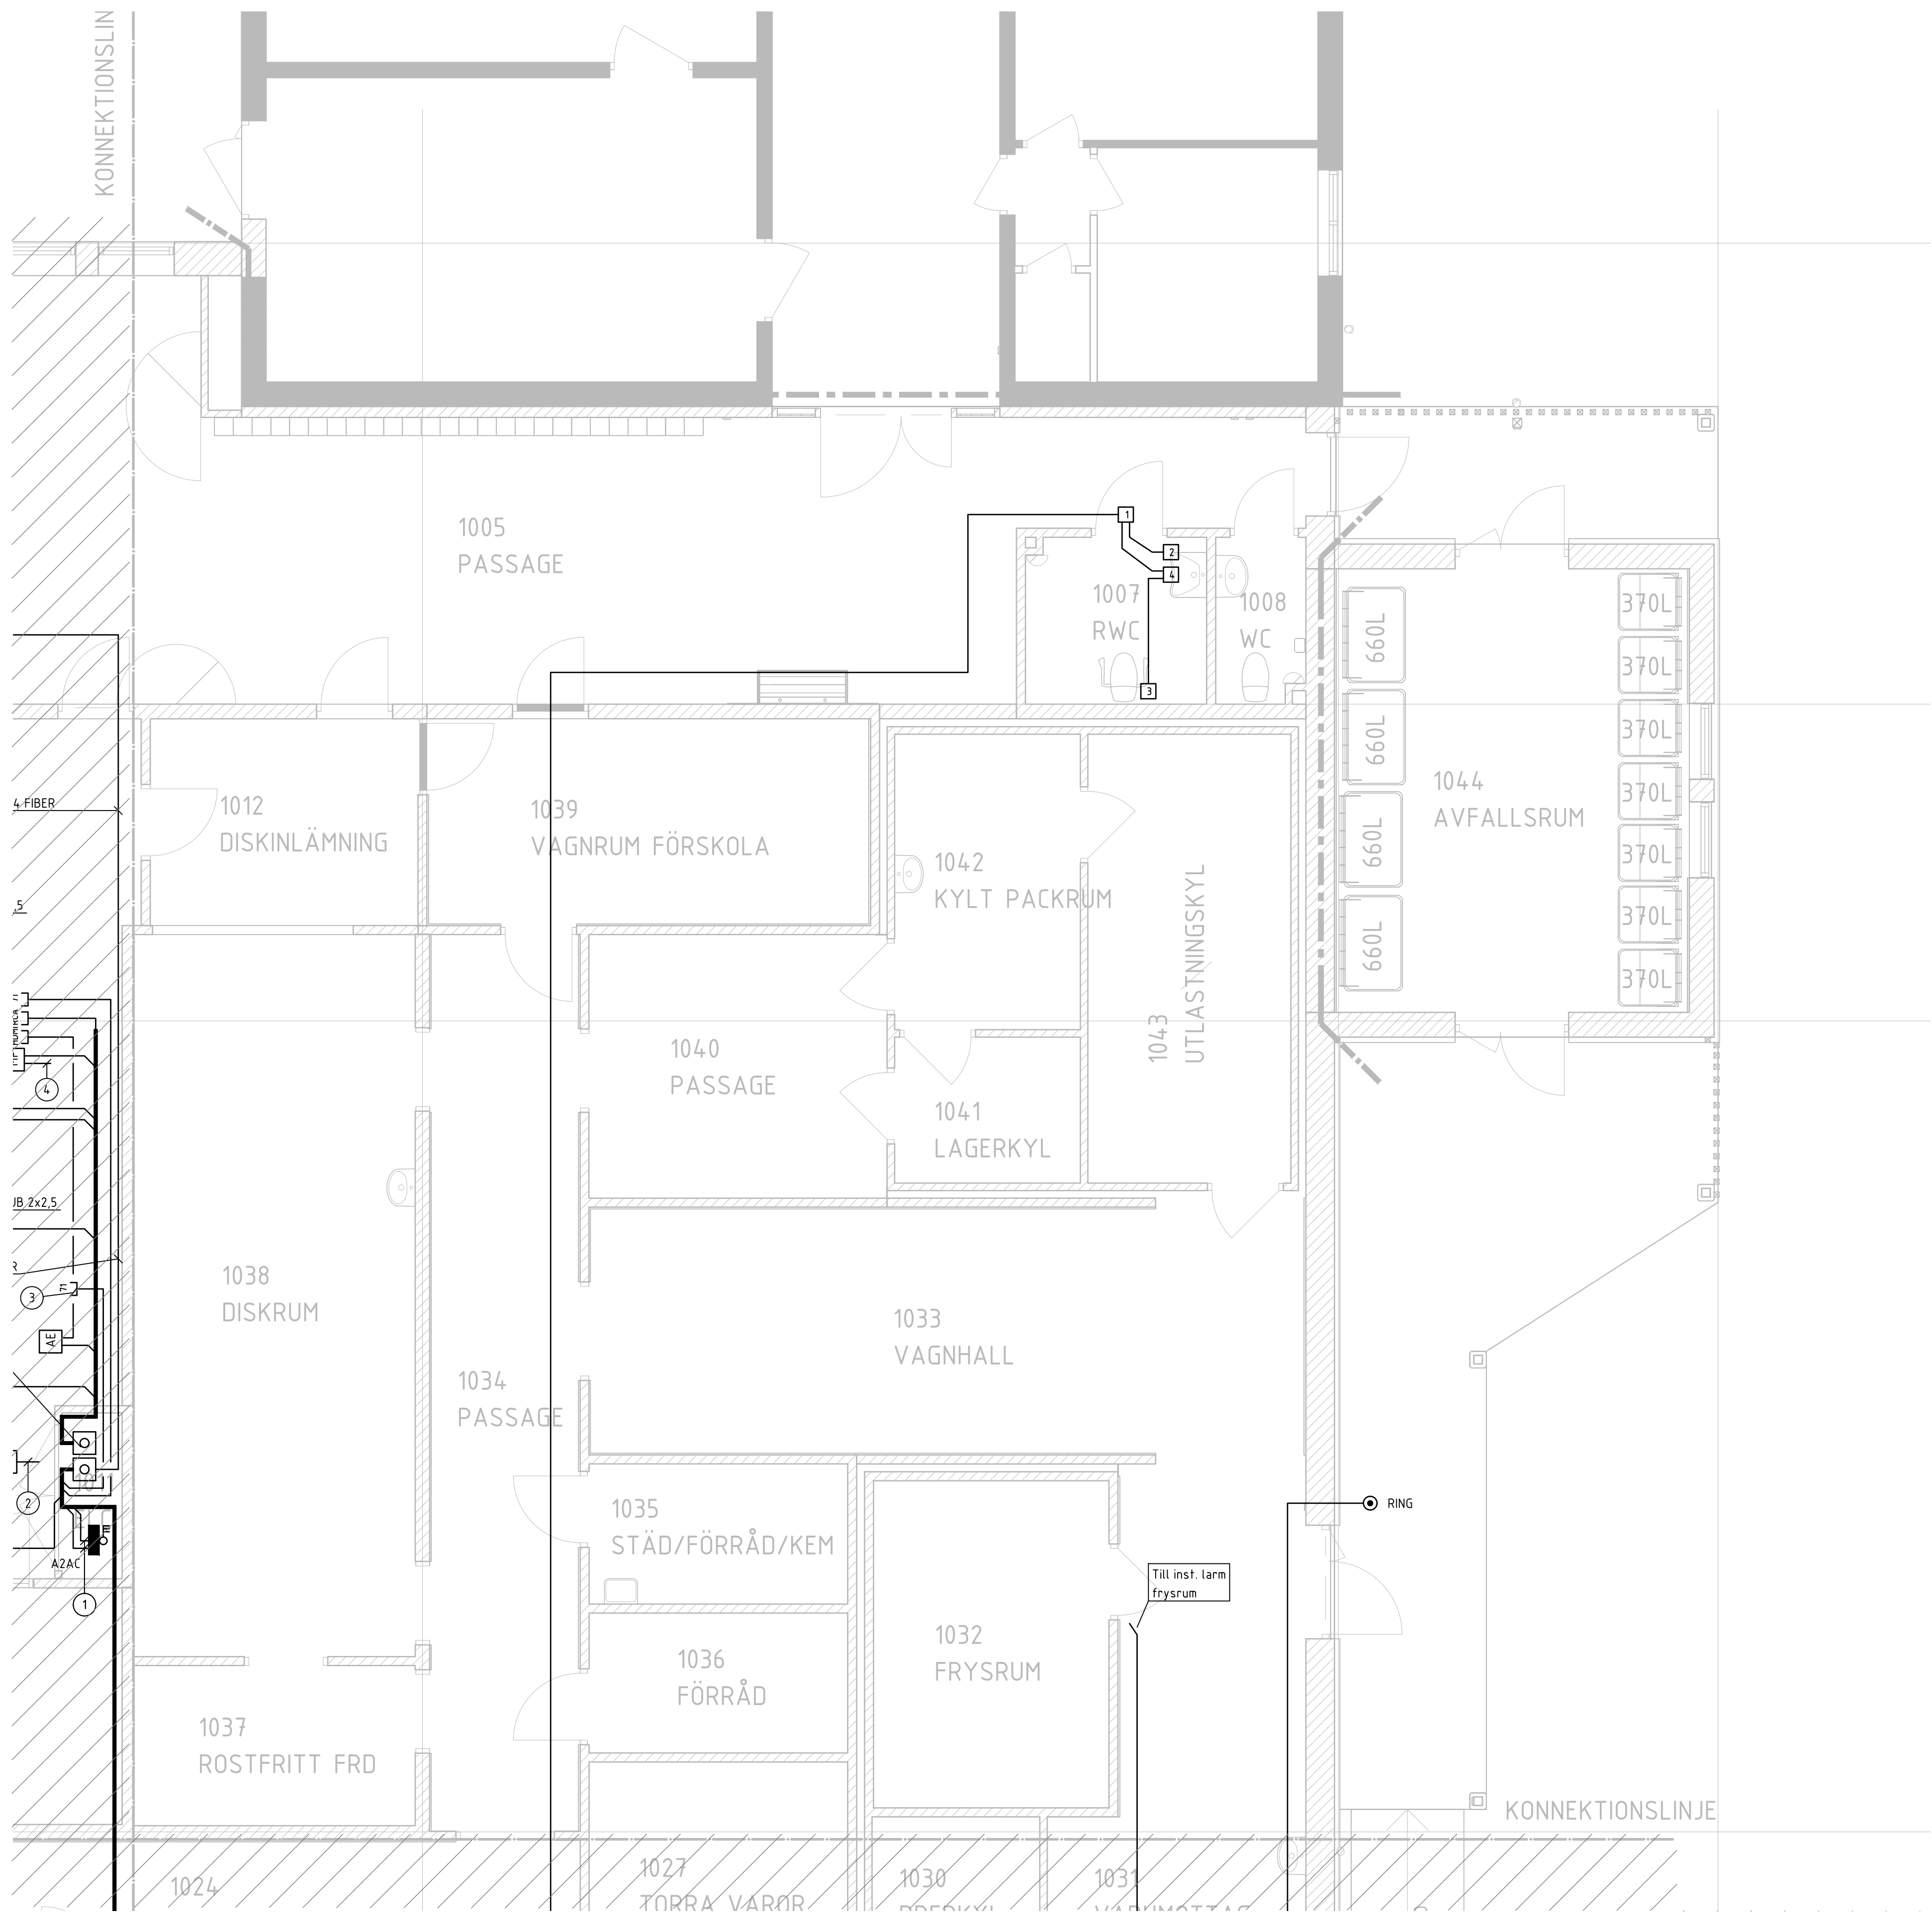


SYMBOLFÖRKLARINGAR

- ☐ MONTERINGSSTATIV 19"
 - ⌚ 2x8 PDL RJ45 UTTAG
 - ⌚ 1x8 PDL RJ45 UTTAG
 - U/UTP CAT 6A KABEL
 - AP ACCESSPUNKT WIFI. LÖSLÄS AV BEST.
 - HS AKTIV SKYLT FÖR HÖRLÅDA TYP TRANSISTOR
T-SIGN 300015, MONTERAS 15 MÖG. ANSLUTS TILL
VÄGGUTTAG PÅ STEGE. ANSLUTNINGSKABEL FÖR
LÄGGS I VP25 I VÄGG TILL STEGE.
 - AE HDMI AUDIO EXTRACTOR. MONTERAS TELEDOSA.
 - Ⓜ HÖGTALARE ENLIGT BESKRIVNING. MONTERAS
INFÄLLD I UNDERBALK.
 - RWC - SIGNAL:
 - 1 MINNESNETHET +0.7
 - 2 RUMSLAMPA MED SUMMER +2.2
 - 3 NÖDSIGNALKNAPP +0.2
 - 4 NÖDSIGNALKNAPP MED SIGNALUTTAG +0.55
 - 5 NÖDSIGNALKNAPP MED DRAGKONTAKT +0.55
 - 1 NÄTVERKSKABEL TYP U/UTP CAT6a 4P TILL
DALIROUTTRAR HELVÄR 905 OCH 910 I CENTRALER.
 - 2 ANSLUTS TILL VÄGGUTTAG PÅ KABELSTEGE
 - 3 MONTERAS PÅ DOSPLÅT PÅ KABELSTEGE.
 - 4 STRÖMFÖRÖRJNING SE RITNING E63BC 1-512.

[illegible]