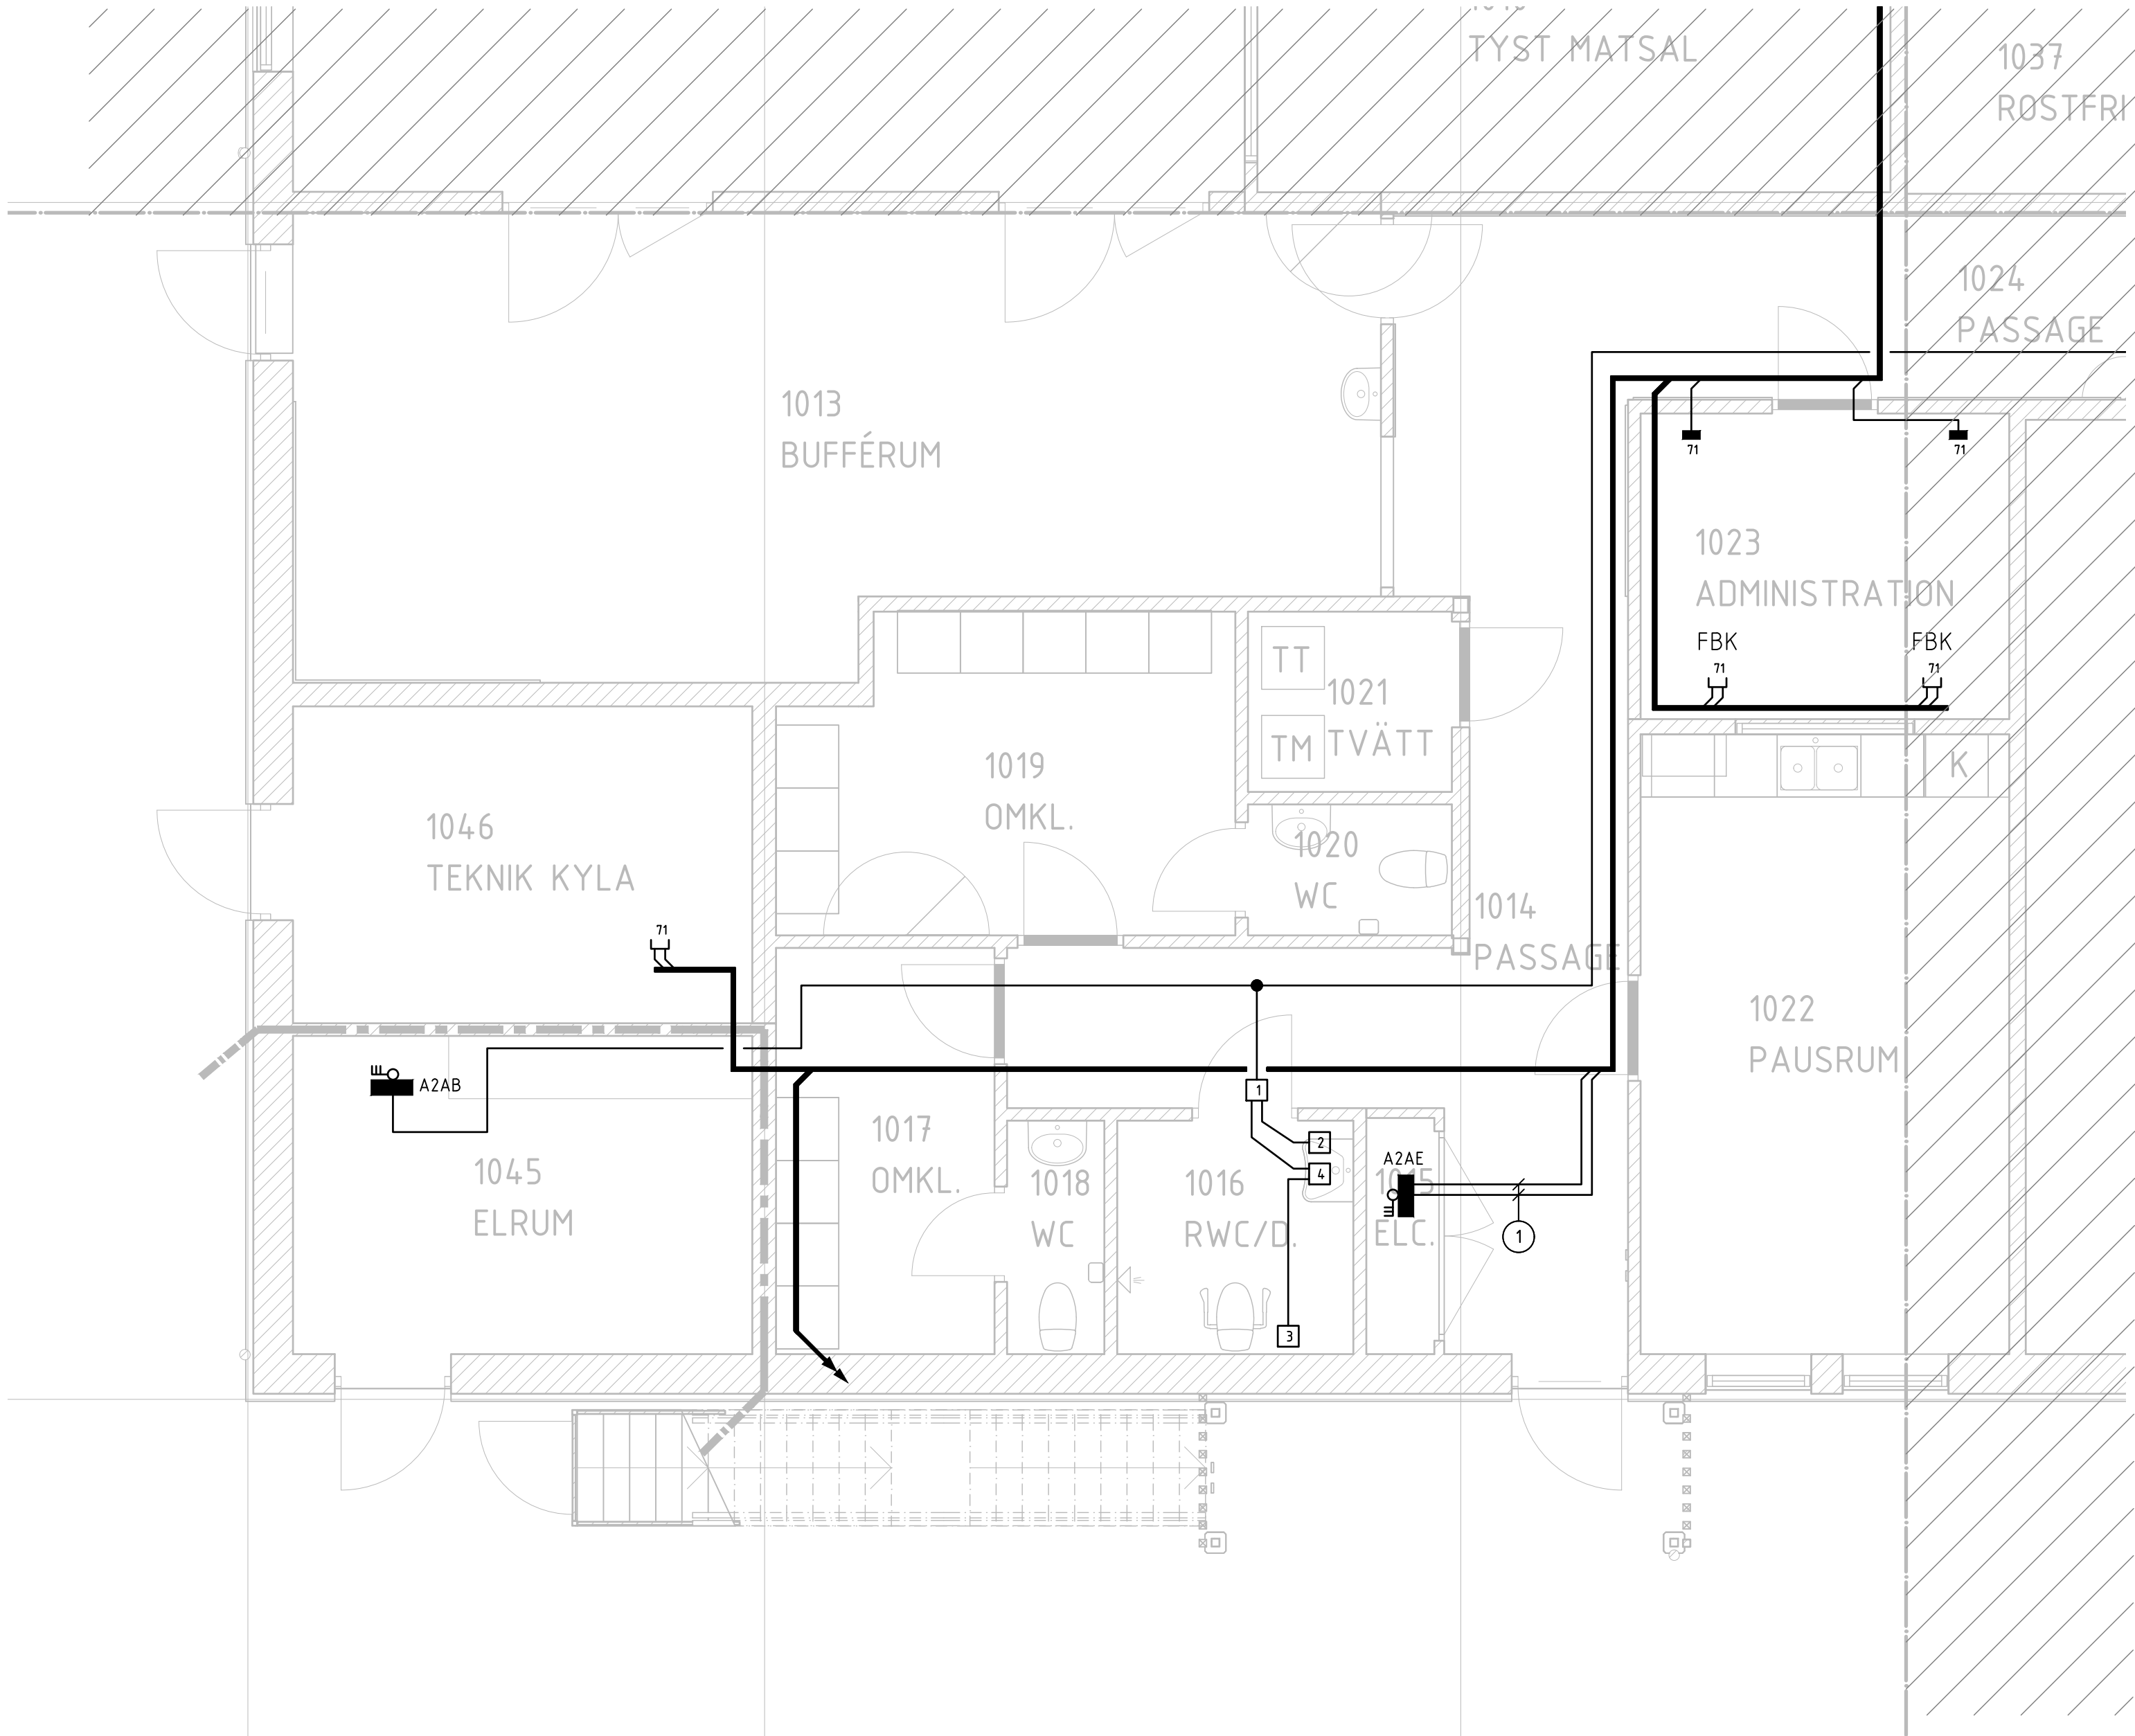


ANVISNINGAR
INFÄLLT MONTAGE.
HALOGENFRITT MATERIAL
FYLLD SYMBOL = INFÄLLD. EJ FYLLD = UTANPÅLIGGANDE.

SYMBOLFÖRKLARINGAR

MONTERINGSSTATIV 19"

2x8 POL RJ45 UTTAG

1x8 POL RJ45 UTTAG

U/UTP CAT 6A KABEL

ACCESSPUNKT WIFI. LEVERERAS AV BEST.

AKTIV SKYLT FÖR HÖRSLINGA TYP TRANSISTOR
T-SIGN 3000115. MONTERAS 15 MÖG. ANSLUTS TILL
VÄGGUTTAG PÅ STEGE. ANSLUTNINGSKABEL FÖR-
LÄGGS I VP25 I VÄGG TILL STEGE.

HDMI AUDIO EXTRACTOR. MONTERAS TELEDOSA.

HÖGTALARE ENLIGT BESKRIVNING. MONTERAS
INFÄLLD I UNDERTAK.

RWC -SIGNAL:

MINNESENHET +0.7

RUMSLAMPA MED SUMMER +2.2

NÖDSIGNALKNAPP +0.2

NÖDSIGNALKNAPP MED SIGNALUTTAG +0.55



NÖDSIGNALKNAPP MED DRAGKONTAKT +0.55

NÄTVERKS KABEL TYP U/UTP CAT6a 4P TILL
DALIROUTRAR HELVAR 905 OCH 910 I CENTRALER.

ANSLUTS TILL VÄGGUTTAG PÅ KABELSTEGE

MONTERAS PÅ DOSPLÅT PÅ KABELSTEGE.

STRÖMFÖRSÖRJNING SE RITNING E63BC.1-512.

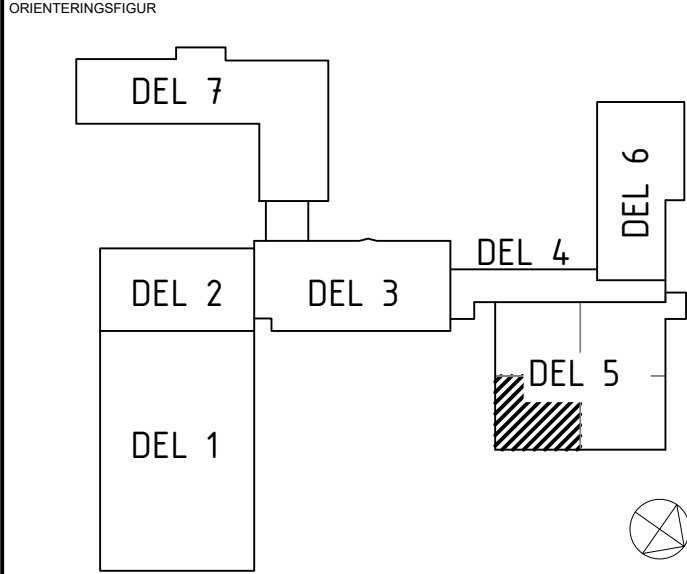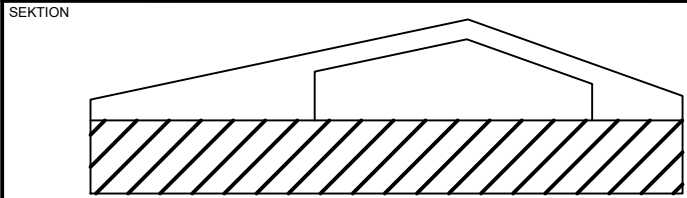

STATUS
FÖRFRÅGNINGSUNDERLAG
HANDLING
BYGGHANDLING
DATUM
2024-12-20
DOKUMENTAV
GIN
ÄNDRINGS PM
-



PROJEKTNAMN
CENTRALEKÖK
OMRÅDE
ROBERTSFORS KOMMUN
PROJEKTNUMMER
ADRESS
YTTRE RINGVÄGEN 4
DÄRRETNUMMER
FASTIGHET
FORDONET 1
DISCIPLIN
FÖRETAG
NORCONSULT SVERIGE AB
UPPDRAGSNUMMER
SKAPAD AV
1088371
GIN
TELEFON
KONTAKTPERSON
010 141 80 00
TOMAS BERGSTRÖM
BYGGNADSVÄRK
PÅLÖSNINGSVÄRK
+45,54 (FG)
VÄNINGSPLAN
VÄNINGSDEL
DELOMRÅDE
1
DEL 5.3
SYSTEM
KOMMUNIKATION
SPECIFIKATION
PLAN 1
TITEL
PLANER
SKALA
1:50
FORMAT
A1
DOKUMENTNUMMER
E-64ED-1-513
ÄNDRING
-