
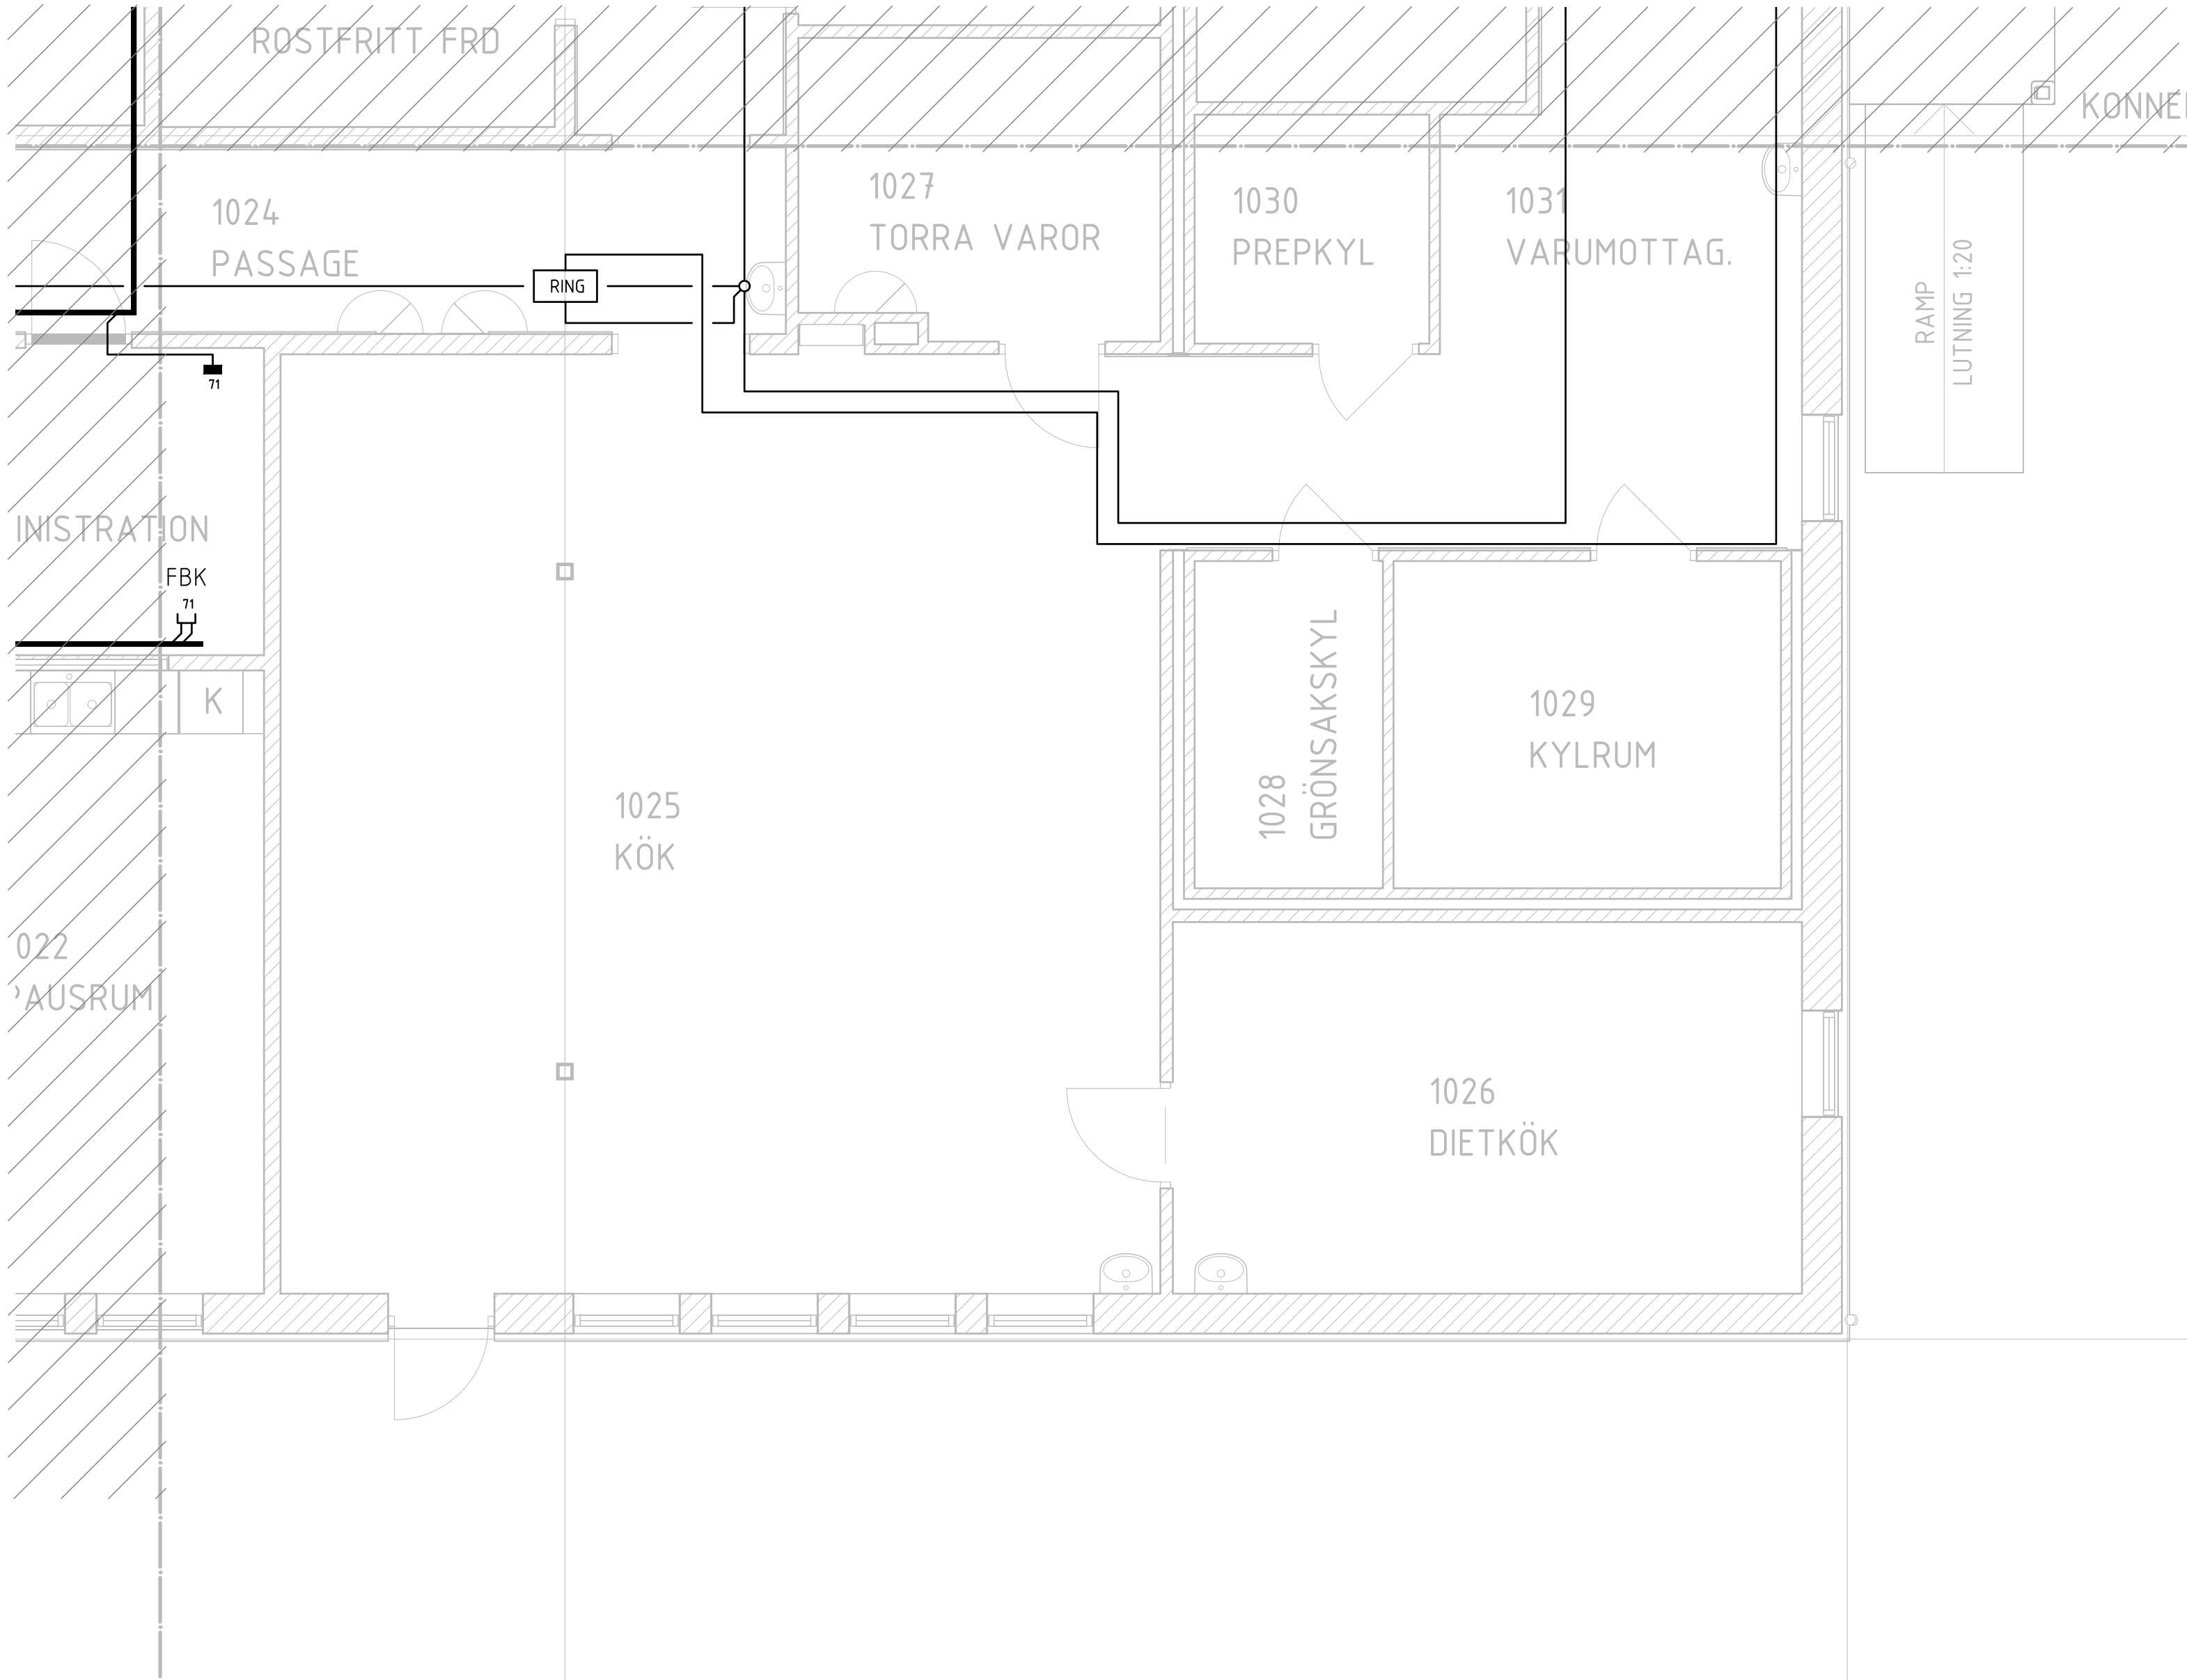


ANVISNINGAR
INFÄLLT MONTAGE.
HALOGENFRITT MATERIAL
FYLLED SYMBOL = INFÄLLD. E.J. FYLLED = UTANPÅLIGGANDE.

SYMBOLFÖRKLARINGAR

- MONTERINGSSTATIV 19"
- 2x8 POL RJ45 UTTAG
- 1x8 POL RJ45 UTTAG
- U/UTP CAT 6A KABEL
- ACCESSPUNKT WIFI. LEVERERAS AV BEST.
- AKTIV SKYLT FÖR HÖRSLINGA TYP TRANSISTOR T-SIGN 3000115. MONTERAS 15 MÖG. ANSLUTS TILL VÄGGUTTAG PÅ STEGE. ANSLUTNINGSKABEL FÖR- LÄGGS I VP25 I VÄGG TILL STEGE.
- HDMI AUDIO EXTRACTOR. MONTERAS TELEDOSA.
- HÖGTALARE ENLIGT BESKRIVNING. MONTERAS INFÄLLD I UNDERTAK.
- RWC -SIGNAL:
- MINNESENHET +0.7
- RUMSLAMPA MED SUMMER +2.2
- NÖDSIGNALKNAPP +0.2
- NÖDSIGNALKNAPP MED SIGNALUTTAG +0.55
- NÖDSIGNALKNAPP MED DRAGKONTAKT +0.55
- NÄTVERKS KABEL TYP U/UTP CAT6a 4P TILL DALIROUTRAR HELVAR 905 OCH 910 I CENTRALER.
- ANSLUTS TILL VÄGGUTTAG PÅ KABELSTEGE
- MONTERAS PÅ DOSPLÅT PÅ KABELSTEGE.
- STRÖMFÖRSÖRJNING SE RITNING E63BC.1-512.

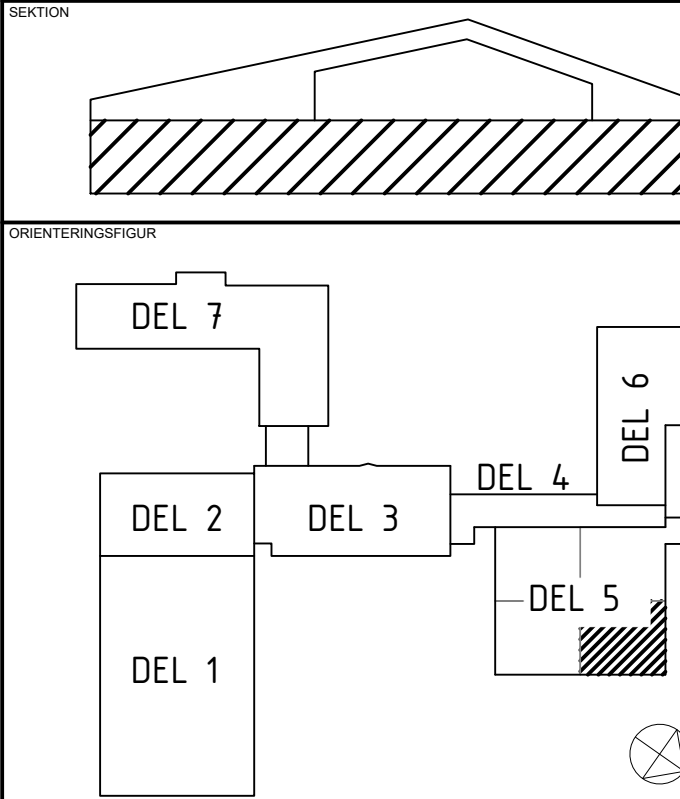

STATUS			
FÖRFRÅGNINGSUNDERLAG			
HANDLING			
BYGGHANDLING			
DATUM		2024-12-20	
TIOGÅRD AV		GIN	
ÄNDRINGS PM		-	
BESTÄLLARE			
 ROBERTSFORS KOMMUN			
PROJEKTNAMN			
CENTRALEKÖK			
OMRÅDE			
ROBERTSFORS KOMMUN			
PROJEKTNUMMER		ADRESS	
YTTRE RINGVÄGEN 4		FASTIGHET	
FORDONET 1		FÖRETAG	
NORCONSULT SVERIGE AB		UPPDRAGSNUMMER	
1088371		SKAPAD AV	
GIN		TELEFON	
010 141 80 00		KONTAKTPERSON	
TOMAS BERGSTRÖM		BYGGNADSVÄRDE	
+45,54 (FG)		VÄNINGSPLAN	
1		VÄNINGSDEL	
DEL 5.4		SYSTEM	
KOMMUNIKATION		SPECIFIKATION	
PLAN 1		TITEL	
PLANER		SKALA	
1:50		FORMAT	
A1		ÄNDRING	
-		DOCUMENTNUMMER	
E-64ED-1-514		-	