


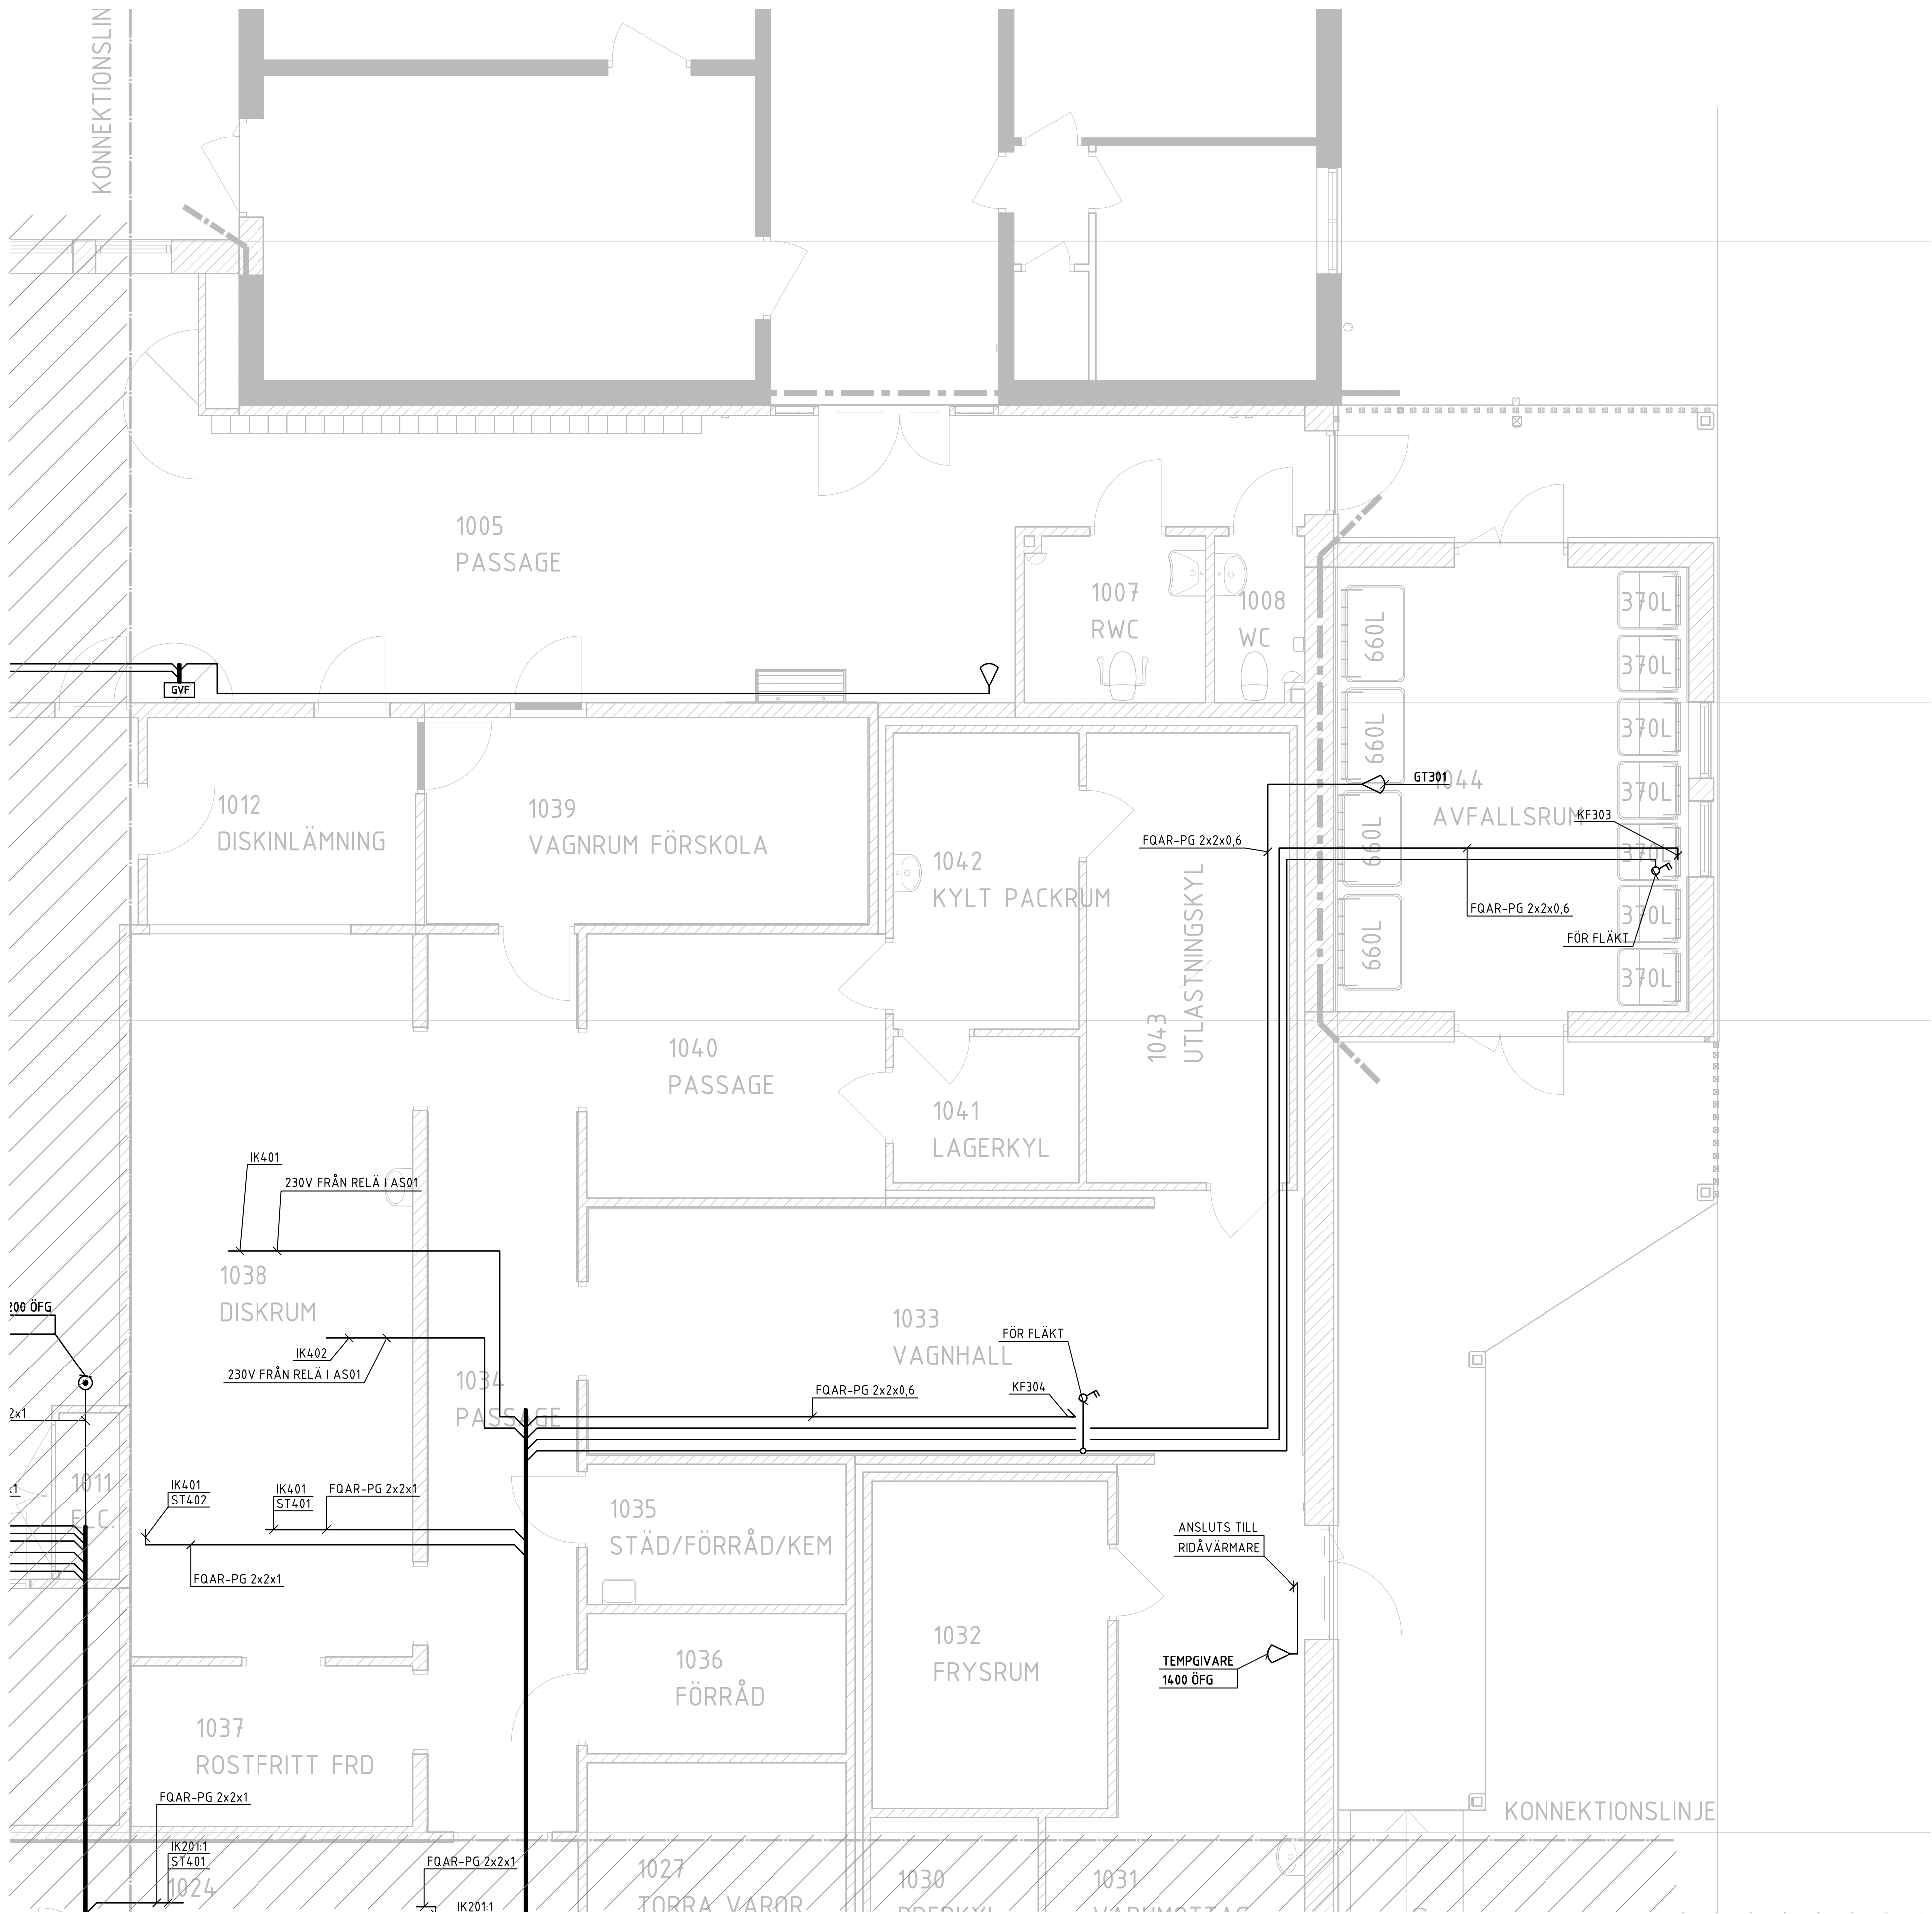

ANVISNINGAR
DÄR INGET ANNAT ANGES GÄLLER:
INFÄLLT MONTAGE PRIORITERAS DÄR BYGGNADES
KONSTRUKTIONEN TILLÅTER. VID UPL. MONTAGE FÖRLÄGGS
KABLAGE I EL-LIST
BRANDTÄTNING I SAMMA KLASS SOM VÄGGENS
BRANDKLASS.
HÖJD ANGES METER ÖFG.
HALOGENFRITT MATERIAL
KABEL 3G1,5

SYMBOLFÖRKLARINGAR

- ⊗ BLIXTLJUS
- ▷ TEMPGIVARE GOLVVÄRME, HÖJD +1,5 ÖFG
- UV UV KONTROLLER
- ⚡ 2POLIG SÄKERHETSBRYTARE
- APPARATSKÅP

HÄNVISNINGAR

- SE ÄVEN:
- STYR-UNDERLAG

SEKTION

ORIENTERINGSFIGUR

STATUS

HANDLING

DATUM

LODPAAD AV

ÄNDRINGS PM

BESTÄLLARE

PROJEKTNAMN

OMRÅDE

PROJEKTNUMMER

DÄRRETNAMN

DISCIPLIN

UPPDRAGSNUMMER

TELEFON

BYGGNADSVÄR

VÄNINGSPLAN

VÄNINGSDEL

DELOMRÅDE

SYSTEM

SPECIFICATION

PLAN 1

PLANER

DOCUMENTNUMMER

SKALA

FORMAT

ÄNDRING

DEL 7

DEL 6

DEL 4

DEL 5

DEL 3

DEL 2

DEL 1

FÖRFRÅGNINGSUNDERLAG

BYGGHANDLING

2024-12-20

GIN

-

ROBERTSFORS

KOMMUN

CENTRALEKÖK

ROBERTSFORS KOMMUN

YTTRE RINGVÄGEN 4

FORDONET 1

NORCONSULT SVERIGE AB

GIN

TOMAS BERGSTRÖM

+45.54 (FG)

DEL 4.2, 5.2

EL I STYR

PLAN 1

SKALA

1:50

FORMAT

A1

ÄNDRING

-

SKALA 1:50

0

1

2

3

4

5

METER