

ANVISNINGAR




DÄR INGET ANNAT ANGES GÄLLER:
INFÄLLT MONTAGE PRIORITERAS DÄR BYGGNADES
KONSTRUKTIONEN TILLÅTER. VID UPL. MONTAGE FÖRLÄGGS
KABLAGE I EL-LIST
BRANDTÄTNING I SAMMA KLASS SOM VÄGGENS
BRANDKLASS.
HÖJD ANGES METER ÖFG.
HALOGENFRITT MATERIAL
KABEL 3G2,5

SYMBOLFÖRKLARINGAR

- ⊗ BLIXTLJUS
- ▷ TEMPORÄRE GOLVVÄRME, HÖJD +1,5 ÖFG
- UV UV KONTROLLER
- 2PÖLIG SÄKERHETSÖRYTARE
- APPARATSKÄP

HÄNVISNINGAR

SE ÄVEN:
- STYR-UNDERLAG

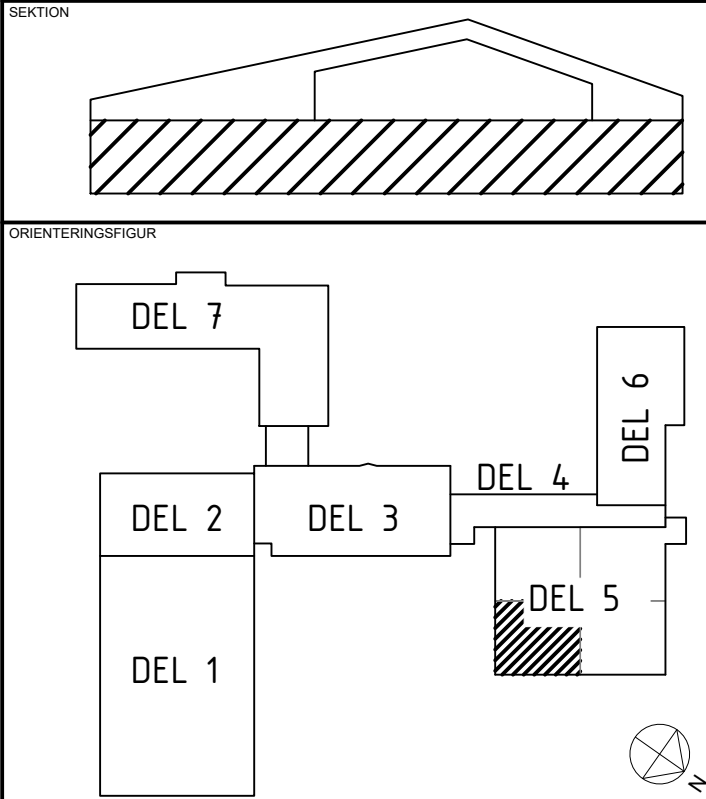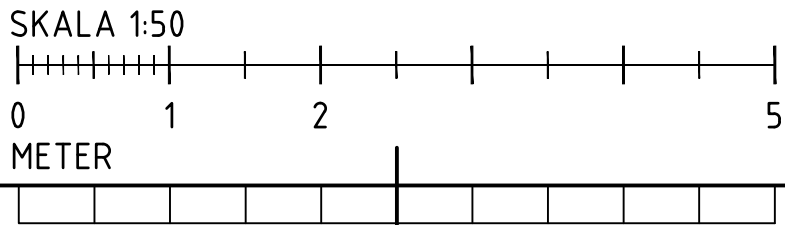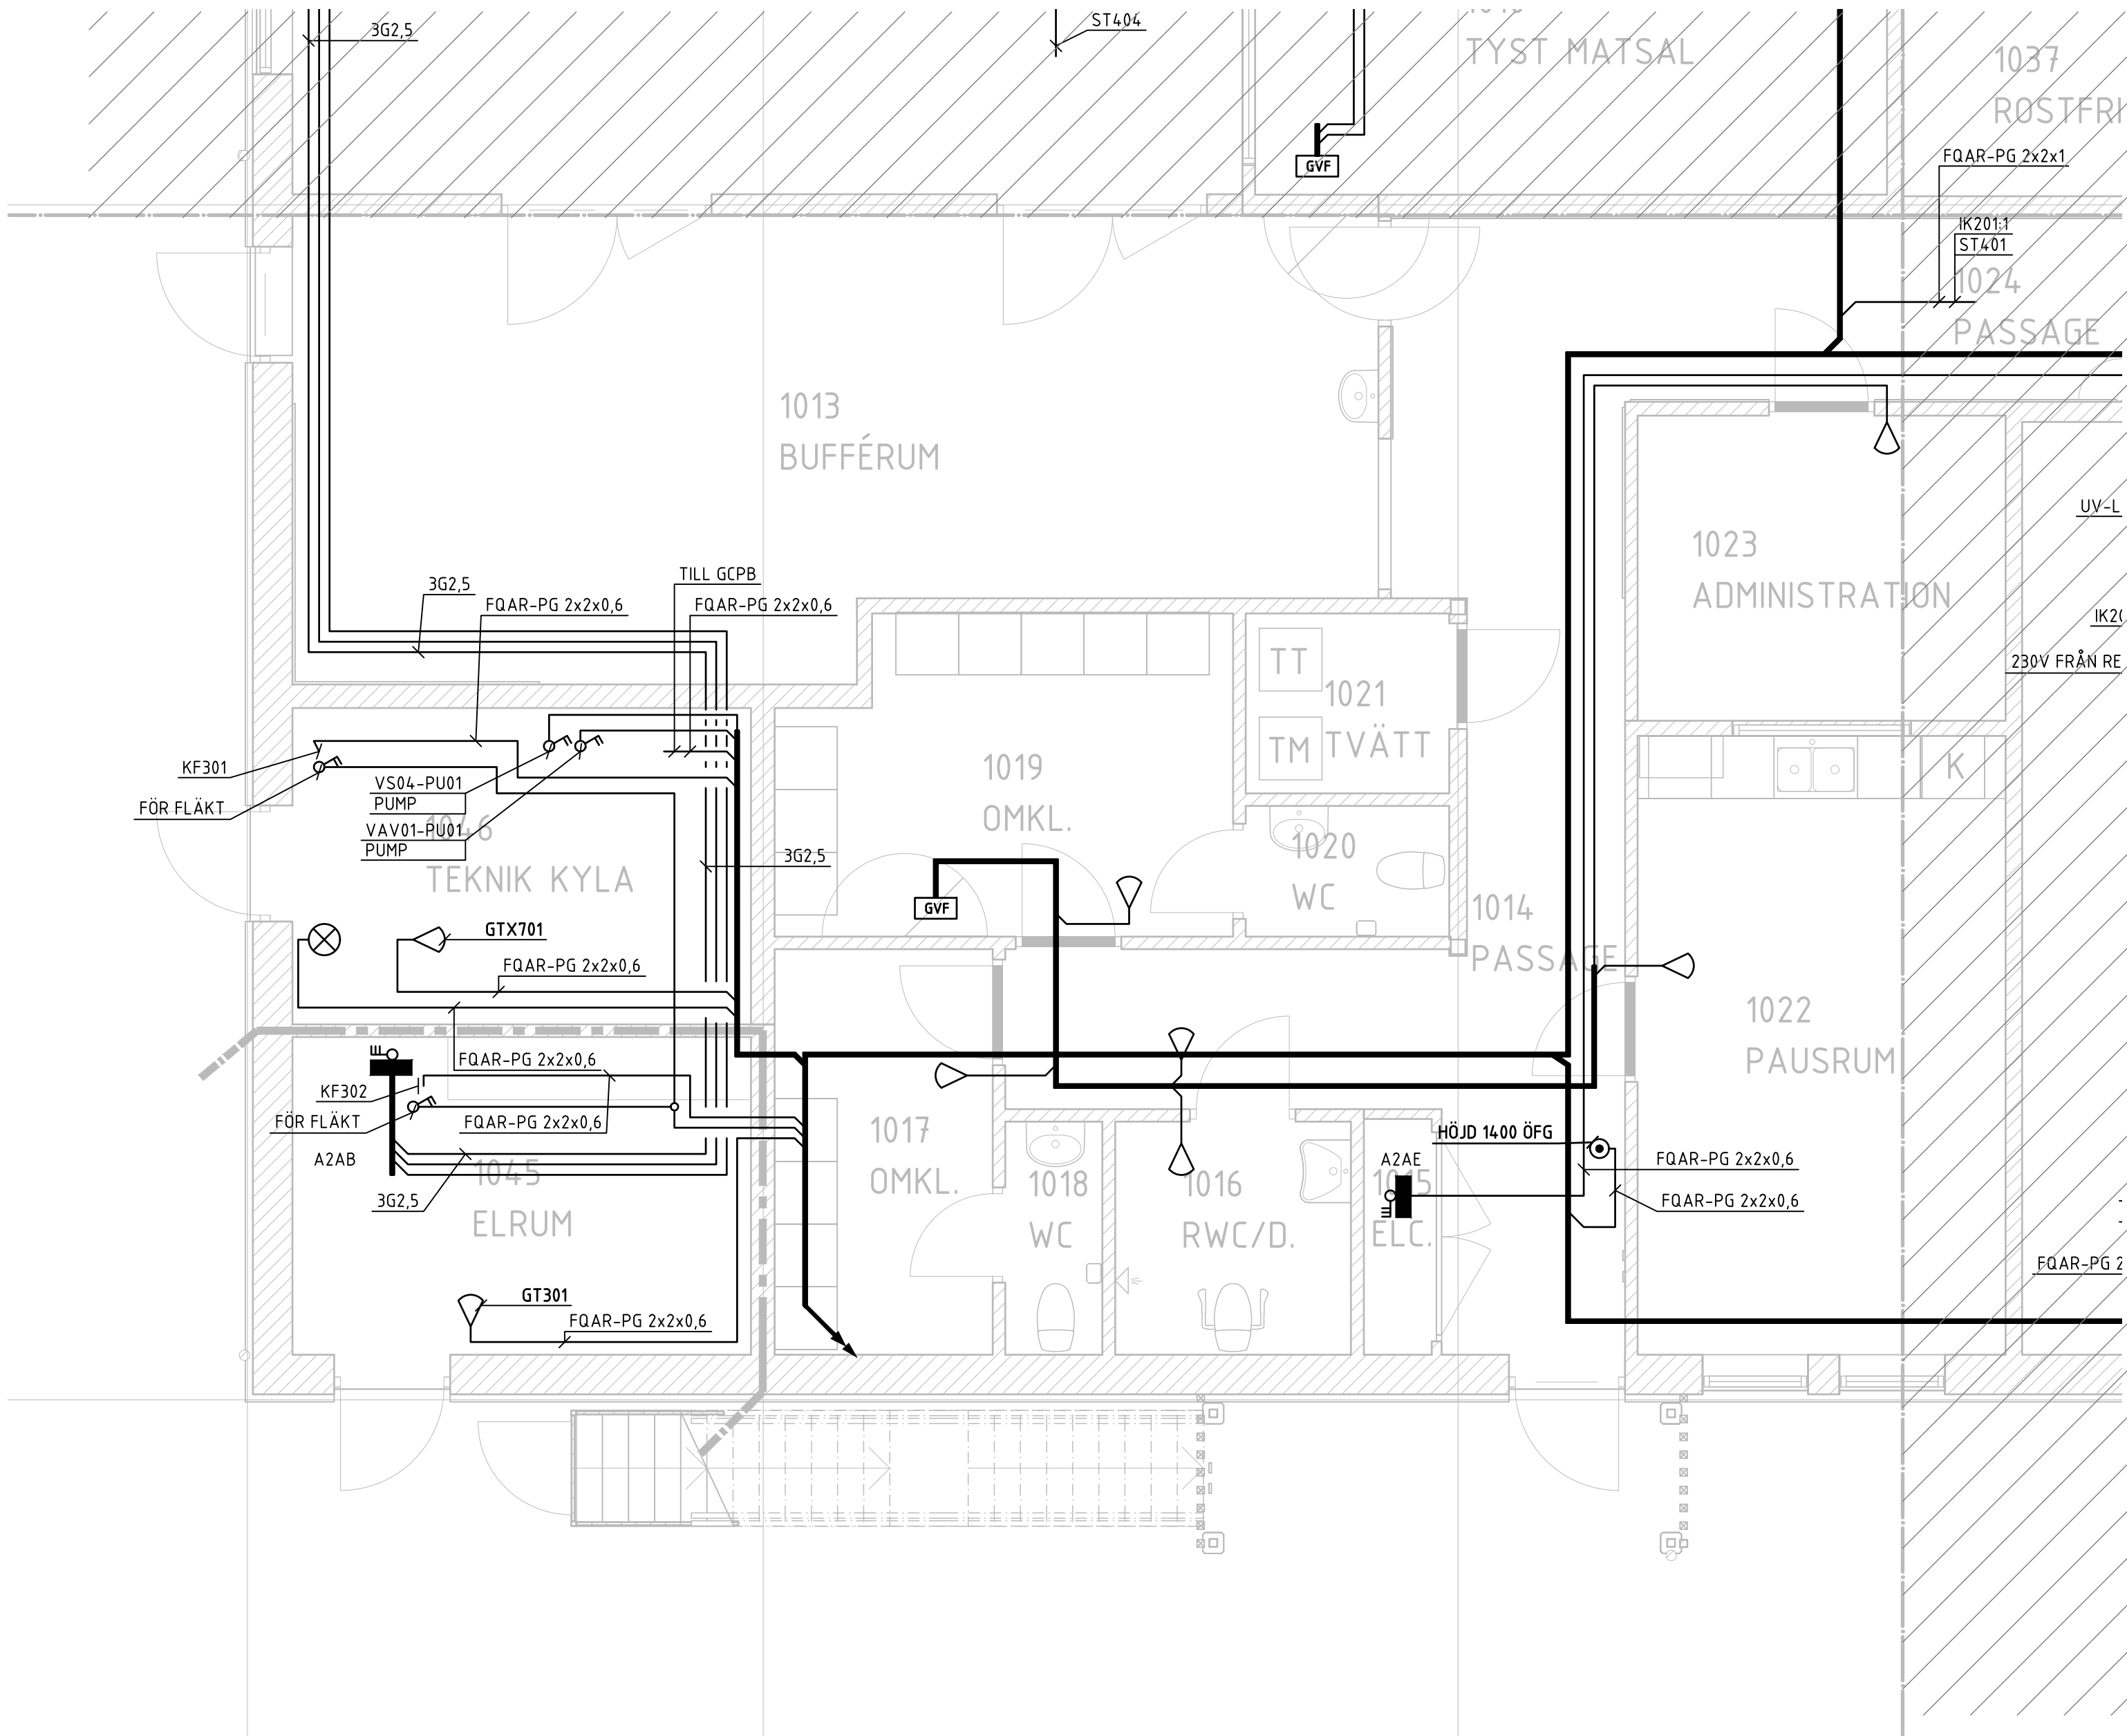

STATUS
FÖRFRÅGNINGSUNDERLAG

HANDLING
BYGGHANDLING

DATUM
2024-12-20

ÖVERSEER AV
GIN

ÄNDRINGS PM
-



PROJEKTNAMN		
CENTRALKÖK		
OBJEKT		
ROBERTSFORS KOMMUN		
PROJEKTNUMMER	ADRESS	
	YTTRE RINGVÄGEN 4	
DÄRRETNAMN	FASTIGHET	
	FORDONET 1	
DISCIPLIN	FÖRETAG	
E	NORCONSULT SVERIGE AB	
UPPDRAGSNUMMER	SKAPAD AV	
1088371	GIN	
TELEFON	KONTAKTPERSON	
010 141 80 00	TOMAS BERGSTRÖM	
BYGGNADSVÄRDE	BYGGNADSVÄRDE	
	+45,54 (FG)	
VÄNINGSPLAN	VÄNINGSDEL	DELOMRÅDE
1		DEL 5.3
SYSTEM		
EL I STYR		
SPECIFIKATION		
PLAN 1		
TEKNIKSÖSKATNING	SKALA	FORMAT
PLANER	1:50	A1
DOCUMENTNUMMER	ÄNDRING	
E-81-1-513	-	